



修改 日期	

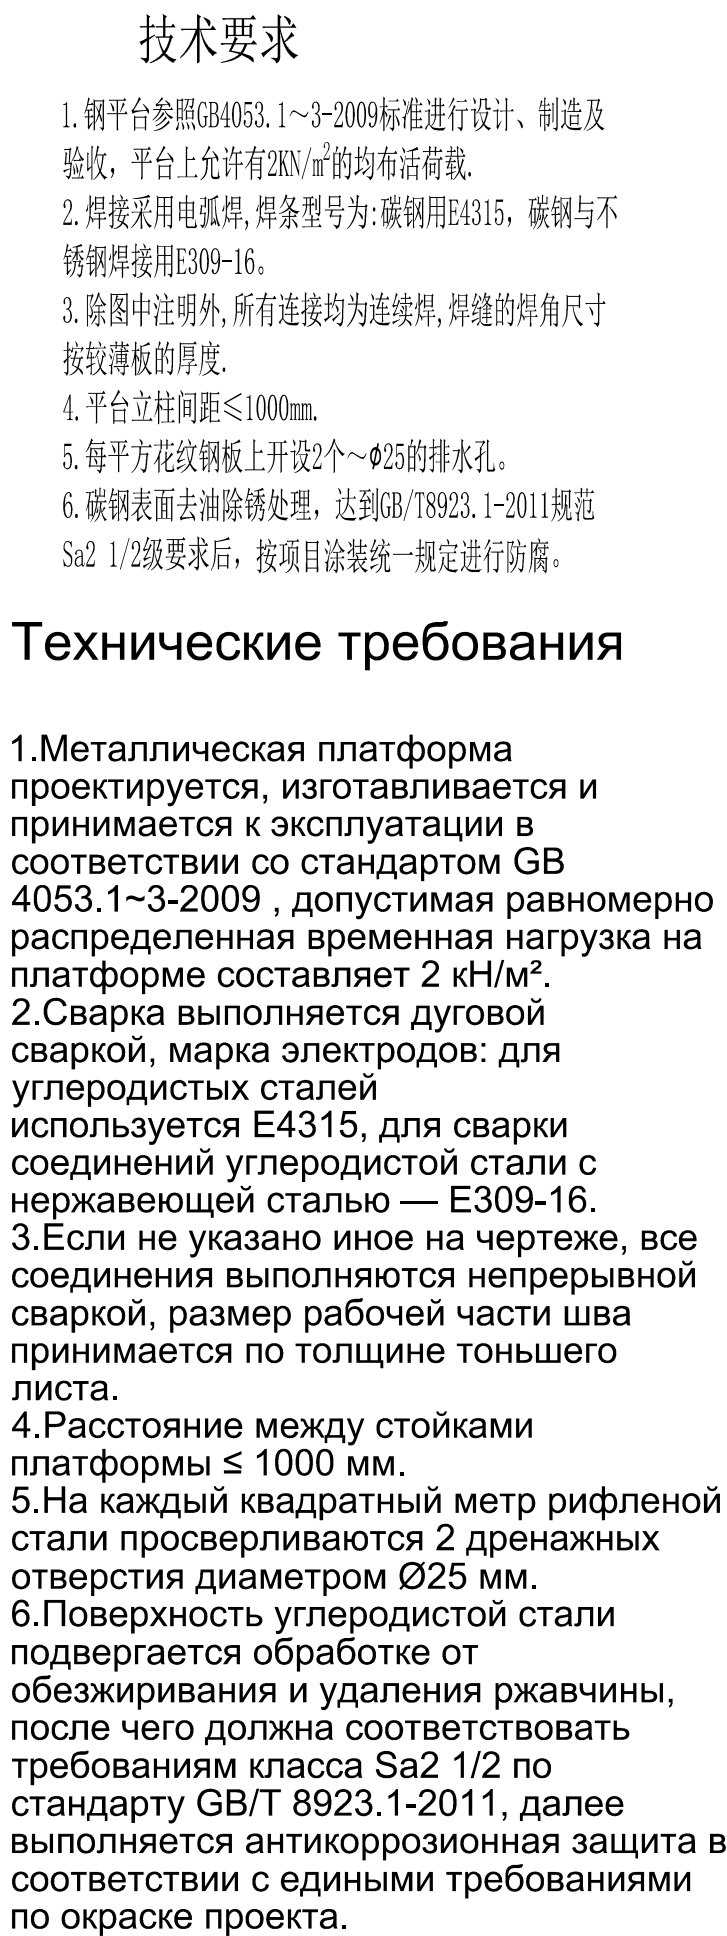

版次 Версия		说明 Примечания				日期 Дата			
 云南化工设计院有限公司 YUNNAN CHEMICAL INSTITUTE OF CHEMICAL ENGINEERING CO., LTD.				 中信建设有限责任公司 CITIC Construction Co., Ltd.					
工程名称 НАЗВАНИЕ ПРОЕКТА		乌兹别克斯坦年产50万吨硫酸钾酸项目 Uzbekistan UTMK Chemical LLC Проект завода по производству серной кислоты						工程代号 Код объекта	
								3147	
审定 Утверждение	姓名 Фамилия и и.	签名 Подпись	日期 Дата	检修平台 (一) Ремонтная площадка			设计项目 Проектируемый объект		
	审核 Разраб.	徐程	1.16				设计阶段 Стадия проектирования		施工图
设计 Проектирование	校核 Проверка	曹元刚	1.16	专业 Специальность	设备 Оборудование	比例 Масштаб	图号 № чертежа	3147-5H113-07-01	
	设计 Проектирование	张春桃	1.16	日期 Дата	2026.1.16	版次 Версия	Rev. 0	共 1 张 Лист 1	
									

会签	姓名	签名
工艺	姓名	签名
设备	姓名	签名
管道	姓名	签名
电气	姓名	签名
暖通	姓名	签名
给排水	姓名	签名
自控	姓名	签名
消防	姓名	签名
结构	姓名	签名
其他	姓名	签名
设计	姓名	签名
审核	姓名	签名
批准	姓名	签名

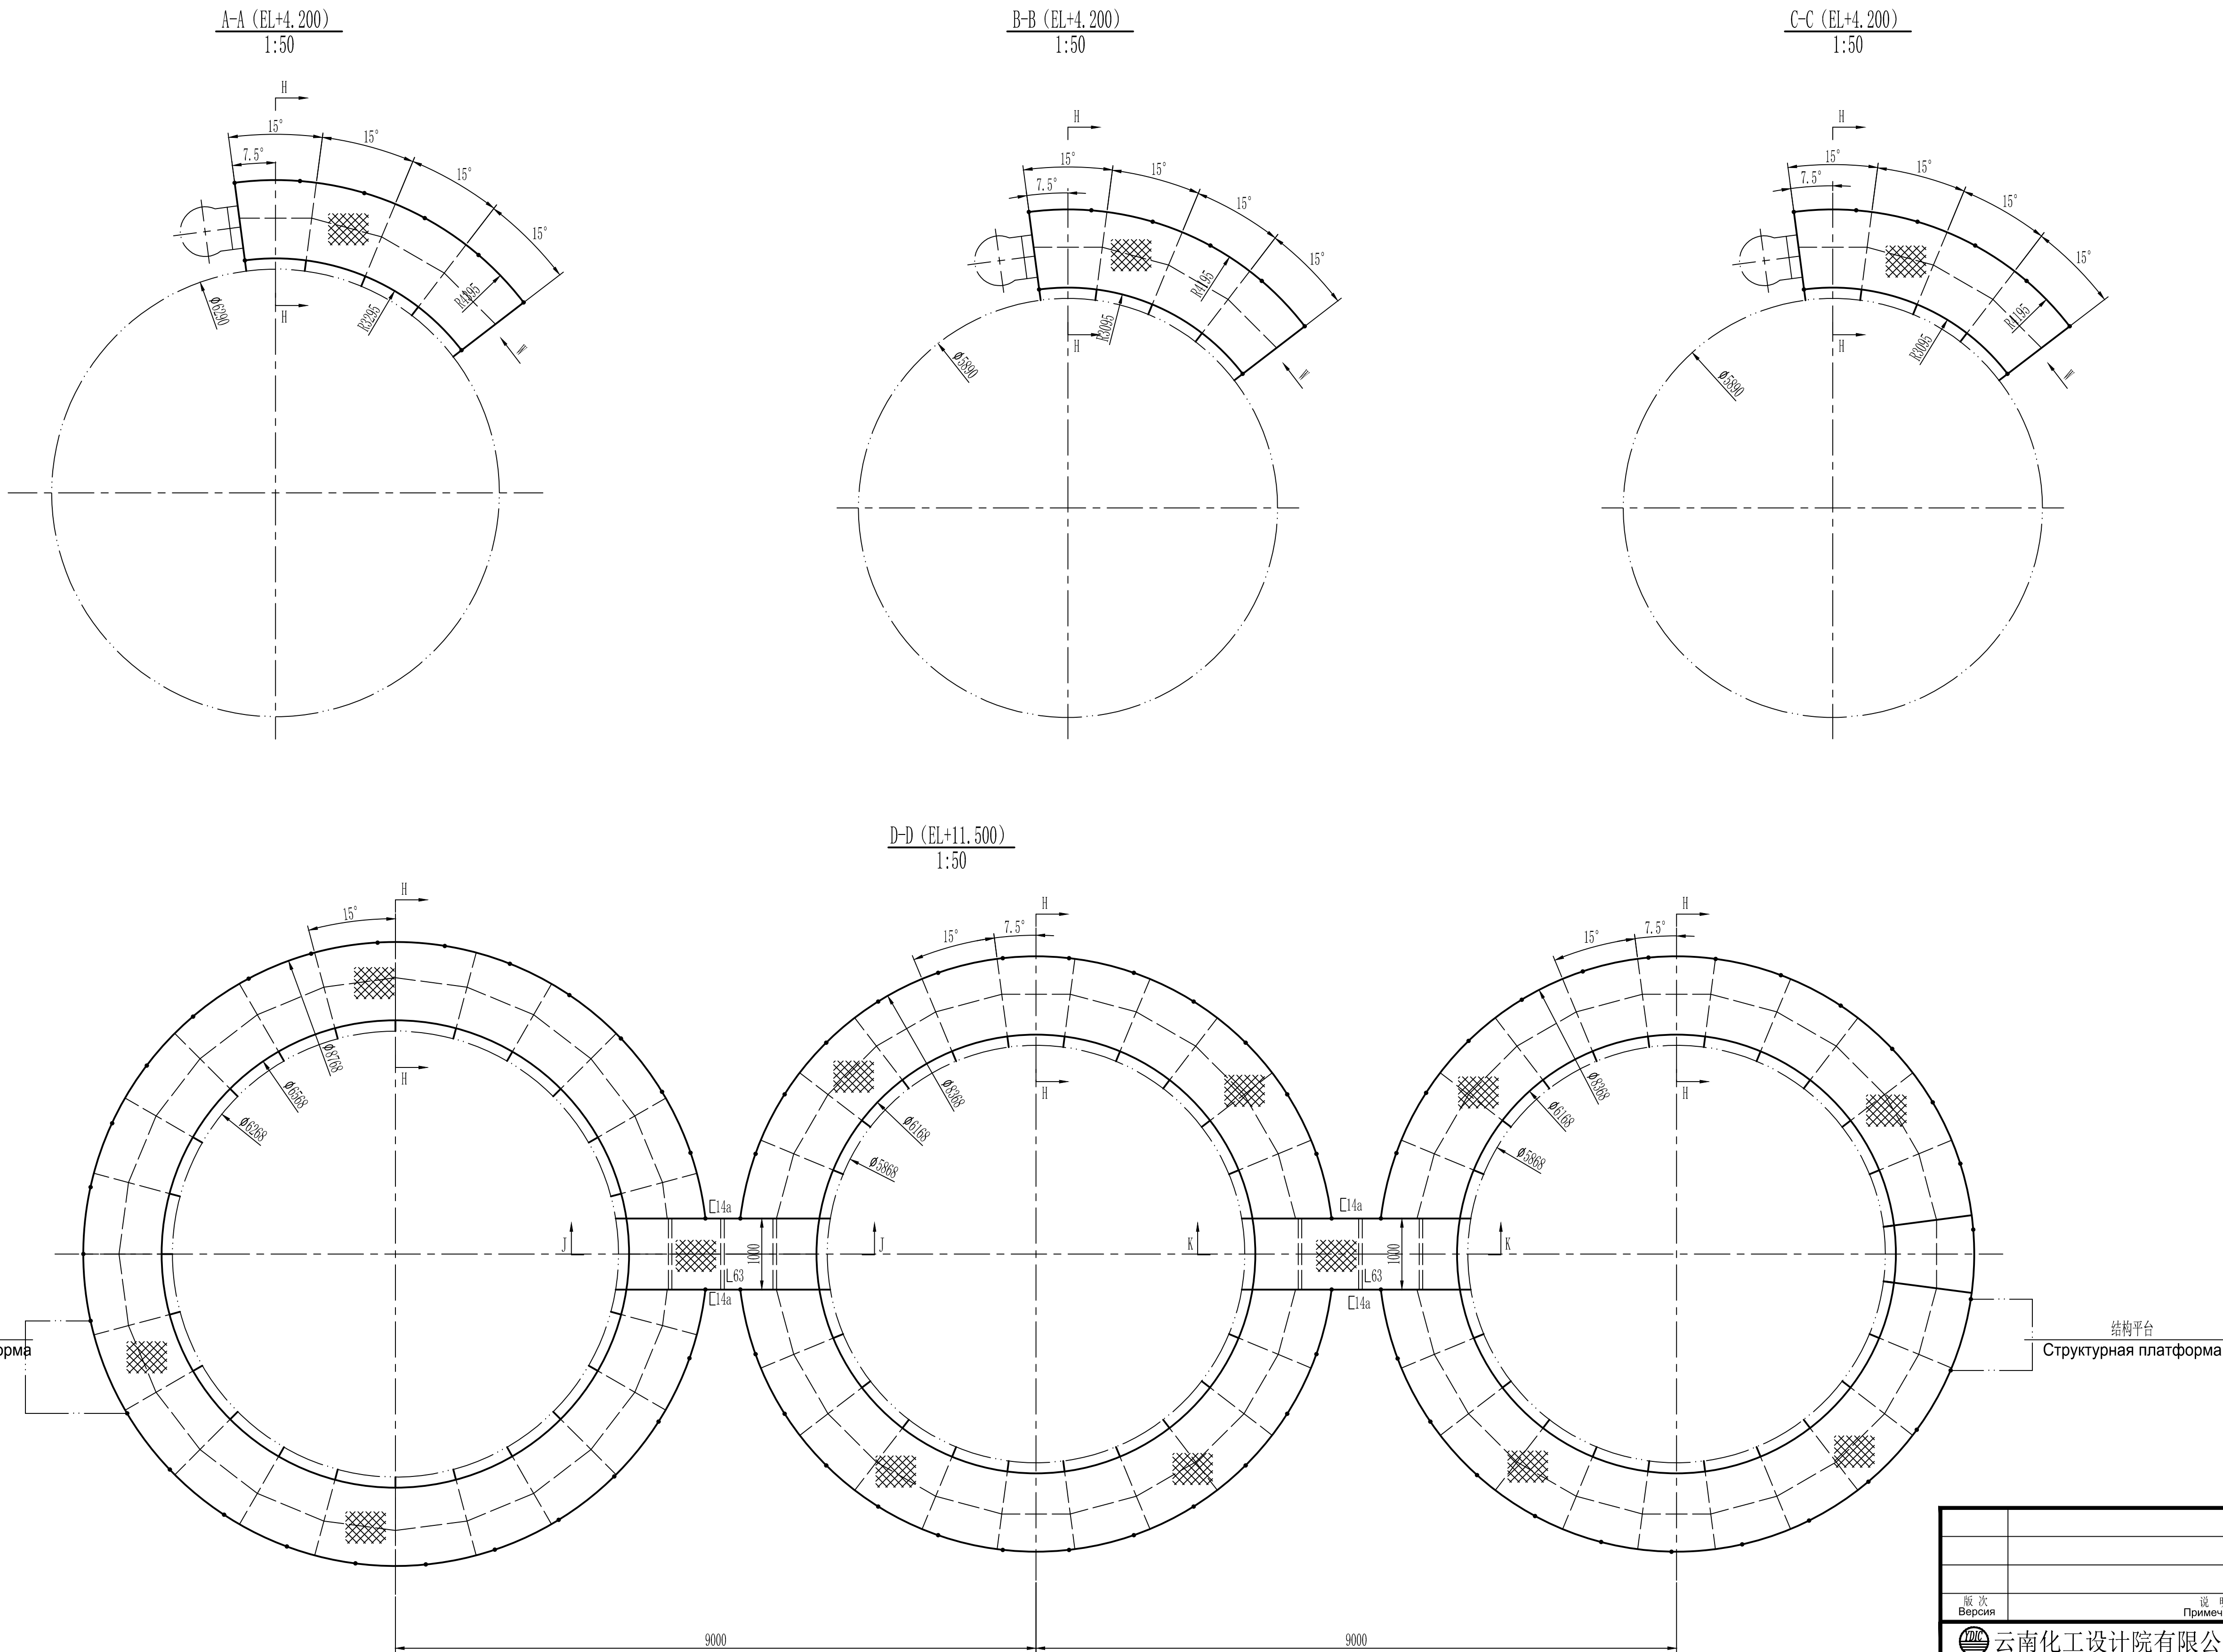

云南省工程勘察设计文件《出图》专用章

单位名称：云南化工设计院有限公司

证书编号：5300790

有效期至：2030年02月14日

说明：化工石化医药行业甲级；建筑行业《建筑工程》甲级；环境工程（水污染防治工程、大气污染防治工程、固体废物处理工程）甲级；轻工行业《石化及塑料工程、食品及发酵工程》乙级；市政行业《给水工程、排水工程、城市燃气工程、环境卫生工程》乙级。

云南省住房和城乡建设厅2025年08月15日颁发

项目出图章编号：4302519044894 项目名称：乌兹别克斯坦年产50万吨硫磺制酸项目

用途：施工图



工程名称		乌兹别克斯坦年产50万吨硫磺制酸项目		工程代号
Uzbekistan UTMK Chemical LLC Проект завода по производству серной кислоты				3147
审定	姓名	签名	日期	设计项目
审核	姓名	签名	日期	设计阶段
校对	姓名	签名	日期	设计阶段
检查	姓名	签名	日期	设计阶段
设计	姓名	签名	日期	设计阶段
专业	姓名	签名	日期	设计阶段
设备	姓名	签名	日期	设计阶段
比例	姓名	签名	日期	设计阶段
版次	姓名	签名	日期	设计阶段
Rev.0	姓名	签名	日期	设计阶段
第1章	姓名	签名	日期	设计阶段
共1张	姓名	签名	日期	设计阶段
第1页	姓名	签名	日期	设计阶段

版权归云南化工设计院有限责任公司所有，未经本公司许可不得转让、复制、泄露给第三方或用于其他目的。 ВСЕ ПРАВА ЗАЩИЩЕНЫ ЮИС. ДАННЫЙ ЧЕРТЕЖ НЕ МОЖЕТ БЫТЬ ПЕРЕУПУЩЕН, ПЕРЕДАН, СКОПИРОВАН, РАСПРЯТ ТРЕТЬИМ ЛИЦАМ, А ТАКЖЕ ИСПОЛЬЗОВАН ДЛЯ ДРУГИХ ЦЕЛЕЙ БЕЗ РАЗРЕШЕНИЯ ЮИС.

修改 Rev.	
------------	--

ВСЕ ПРАВА ЗАЩИЩЕНЫ YDİC. ДАННЫЙ ЧЕРТЕЖ НЕ МОЖЕТ БЫТЬ ПЕРЕУСТУПЛЕН, ПЕРЕДАН, СКОПИРОВАН, РАСКРЫТ ТРЕТЬИМ ЛИЦАМ, А ТАКЖЕ ИСПОЛЬЗОВАН ДЛЯ ДРУГИХ ЦЕЛЕЙ БЕЗ РАЗРЕШЕНИЯ YDİC.