

[illegible]

管口材料表									
Таблица материалов патрубков									
序号 Номер детали	图号或标准号 Номер чертежа или номер стандарта	名称 Название	数量 Количество	材料 Материал	单重 Единица	重量 Масса	备注 Примечания		
20		垫板130x4 L=22.2m Полоса 130x4, длина=22,2 м	1	S30408		92.4			
19		钢板 306x12 Стальная пластина 306x12	1	S31603		107			
18		旋转座 Подставка для тарелки	1	S30408		1.56			
17		槽钢 [20a L=3348 Швеллер [20a L=3348	2	Q235B	55.79	151.6			
16		接地板 100x50x10 Плата заземления 100x50x10	2	S30408	0.21	0.48			
15	3147-5H123-02-04	连接板130 Втулка 130x16	1	组合件 Сборочная узел		18.92			
14	3147-5H123-02-04	硫酸入口DN6, 连接口DN8 Вход серной кислоты DN6, втулка DN8	2	组合件 Сборочная узел	40.87	81.74			
13	3147-5H123-02-04	回流口DN5 Отвод DN5	1	组合件 Сборочная узел		31.95			
12	3147-5H123-02-03	空架板 Профиль из нержавеющей стали	2	Q235B	37.58	115.1			
11		槽钢 [32a Швеллер [32a	20.38	Q235B		885			
10	3147-5H123-02-04	开车按钮进口DN7 Кнопка запуска кислоты импорт DN7	1	组合件 Сборочная узел		118.7			
9	3147-5H123-02-04	硫酸入口DN2 Вход серной кислоты импорт DN2	1	组合件 Сборочная узел		98.2			
8		盲板 Φ120 S=6 Крышка Φ120 S=6	1	S31603		640			
7		角钢腿125x75x8 Крышка из углового стального 125x75x8	1	Q235B		114.2			
6	3147-5H123-02-03	防腐罩 Полупрозрачный	1	Q235B		322.1			
5		NPT耐酸胶泥 Кислотоустойчивый цемент	1	/		1632			

ВСТЕП. 1.01. 1.02. 1.03. 7.81. 7.

7 806513 286107



云南化工设计院有限公司

YUNNAN DESIGN INSTITUTE OF CHEMICAL ENGINEERING CO., LTD.

工程名称 乌兹别克斯坦年产50万吨硫磺制酸项目
Наименование объекта Проект завода по производству серной кислоты

设计项目 产品硫酸罐区
Объект проектирования Зона резервуара для серной кислоты с продуктом

设计阶段 施工图
Стадия проектирования Рабочий чертёж

硫酸地下槽 (VE-12302)
Подземный резервуар для серной кислоты
管口方位图

Схема расположения штуцеров

版权所有, 未经本公司许可不得转让、复制、
泄露给第三方或用于其它目的。
Все права защищены. Запрещается передача, копирование,
разглашение третьим сторонам или использование в иных
целях без разрешения нашей компании.

工程代号
Код объекта

3147

图号
Номер чертежа


3147-5G123-08

日期
Дата

2026. 4. 1

第1张
Лист

共1张
Листы

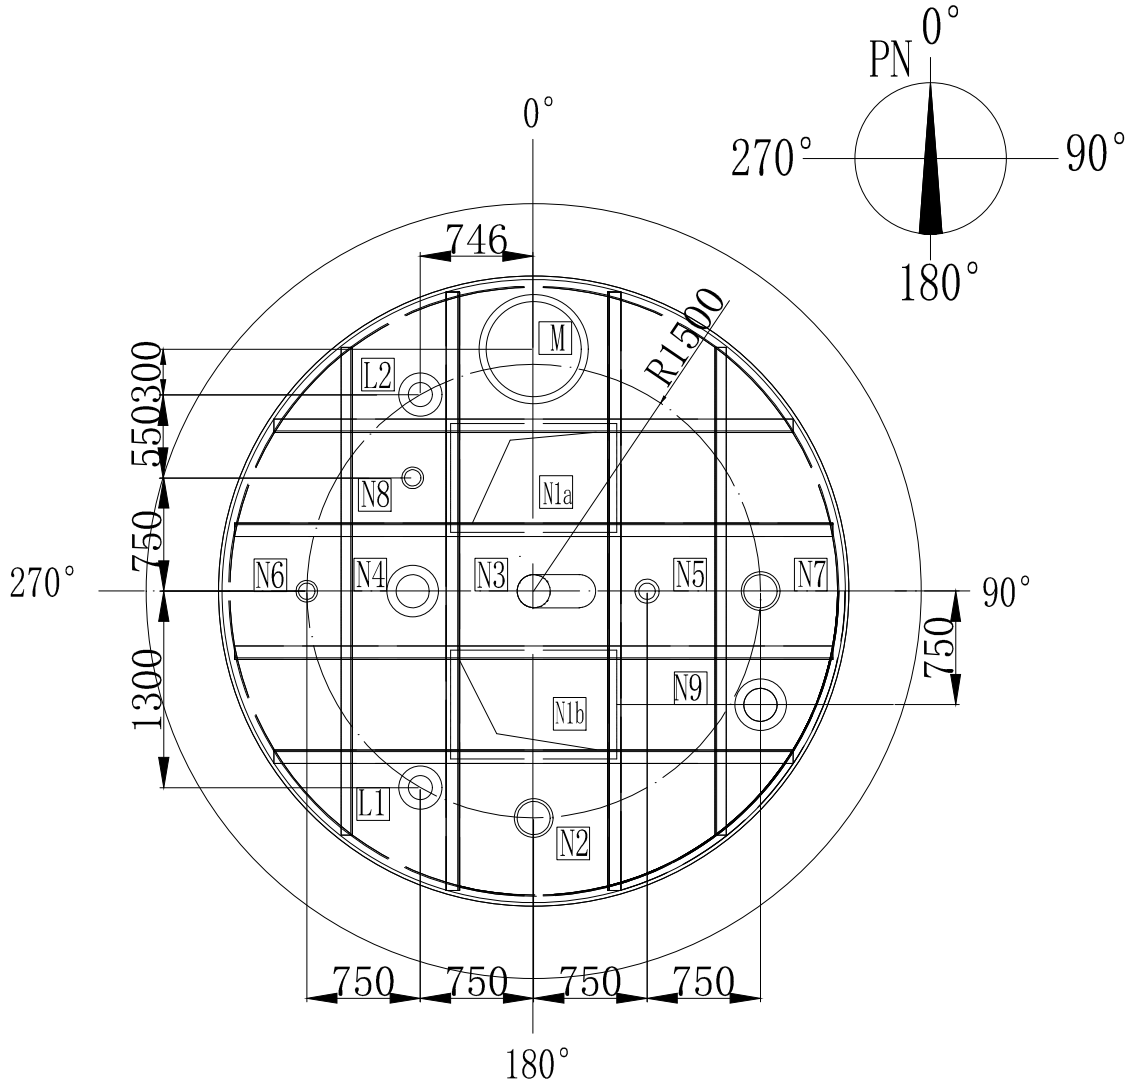

设备装配图号: 3147-5H123-02

审定 Утверждение		M	600	HG/T21516-2014 PL600-6 RF	人孔 Люк	N9	50/100	HG/T20592-2009 S050(B)-16/PL100-10 RF	排酸口 (套管) Отвод кислоты
签名 Подпись		N5	100/150	HG/T20592-2009 S0100(B)-16/PL150-10 RF	回流口 (套管) Патрубок рециркуляции (со втулкой)	L2	150	HG/T20592-2009 S0150(B)-16 RF	现场液位计接口 Стык местного уровнемера
审核 Рассм.	李海昆	N4	200	HG/T20592-2009 S0200(B)-16 RF	备用口 (配法兰盖) Резервный патрубок (с фланцевой заглушкой)	L1	150	HG/T20592-2009 S0150(B)-16 RF	远传液位计接口 Штуцер дистанционного уровнемера
签名 Подпись	李海昆	N3	200		排气口 Высасывное отверстие	N8	100/150	HG/T20592-2009 S0100(B)-16/PL150-10 RF	进酸口 (套管) Вход кислоты (со втулкой)
校核 Пров.	郑斌斌	N2	200/250	HG/T20592-2009 S0200(B)-16/PL250-10 RF	硫酸入口 (套管) Вход серной кислоты (со втулкой)	N7	200/250	HG/T20592-2009 S0200(B)-16/PL250-10 RF	开车母酸进口 (配法兰盖) Вход стартовой маточной кислоты (с фланцевой заглушкой)
签名 Подпись	郑斌斌	N1a/b			卸酸泵安装口 Монтажный патрубок насоса для слива кислоты	N6	100/150	HG/T20592-2009 S0100(B)-16/PL150-10 RF	硫酸入口 (套管) Вход серной кислоты (со втулкой)
设计 Проектирование	甘丽平	管口 符号	公称 口径	连接形式及标准 Форма и стандарт соединения	用途或名称 Назначение или название	管口 符号	公称 口径	连接形式及标准 Форма и стандарт соединения	用途或名称 Назначение или название
签名 Подпись	甘丽平	Символ штуцера	Условный проход			Символ штуцера	Условный проход		