




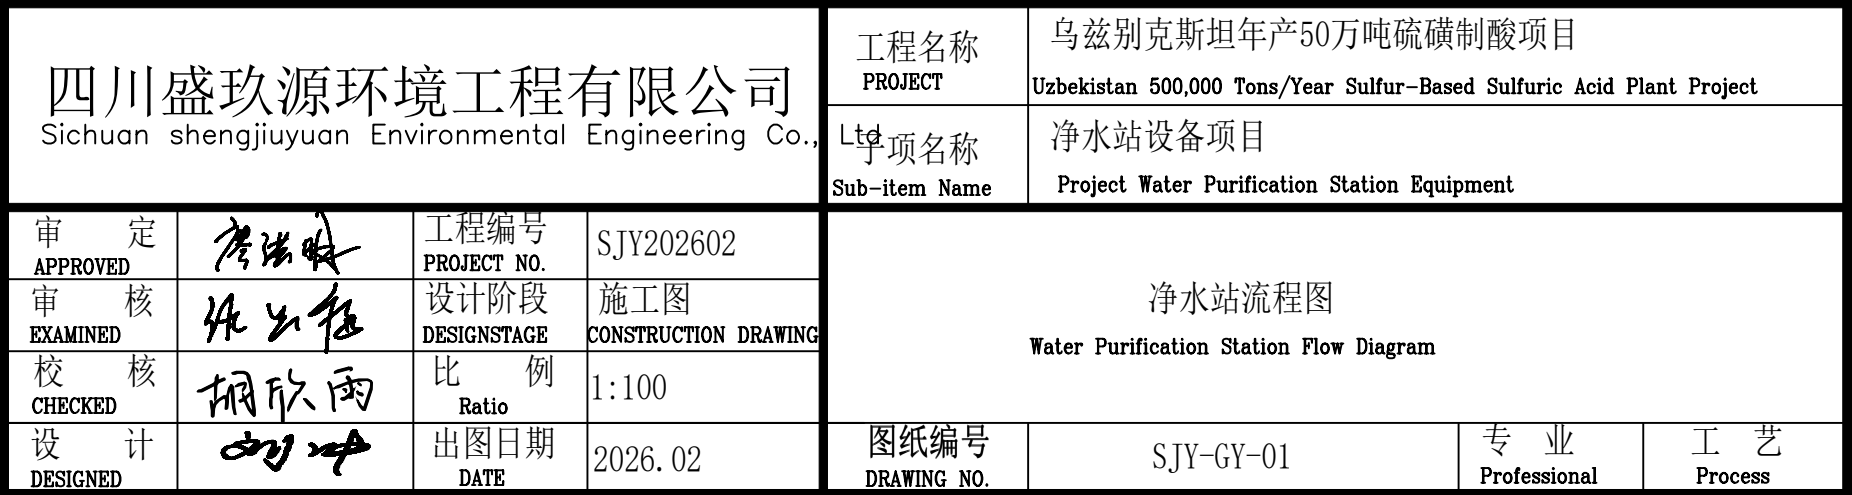

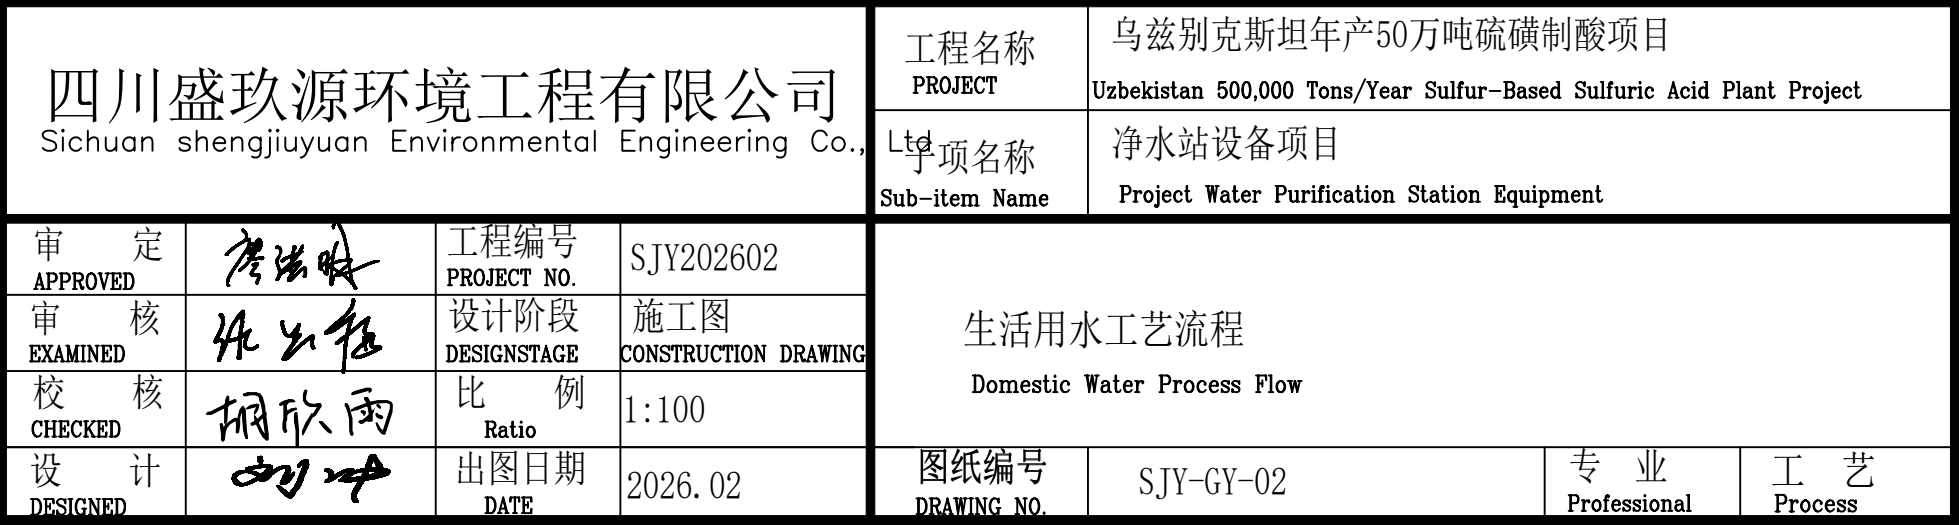

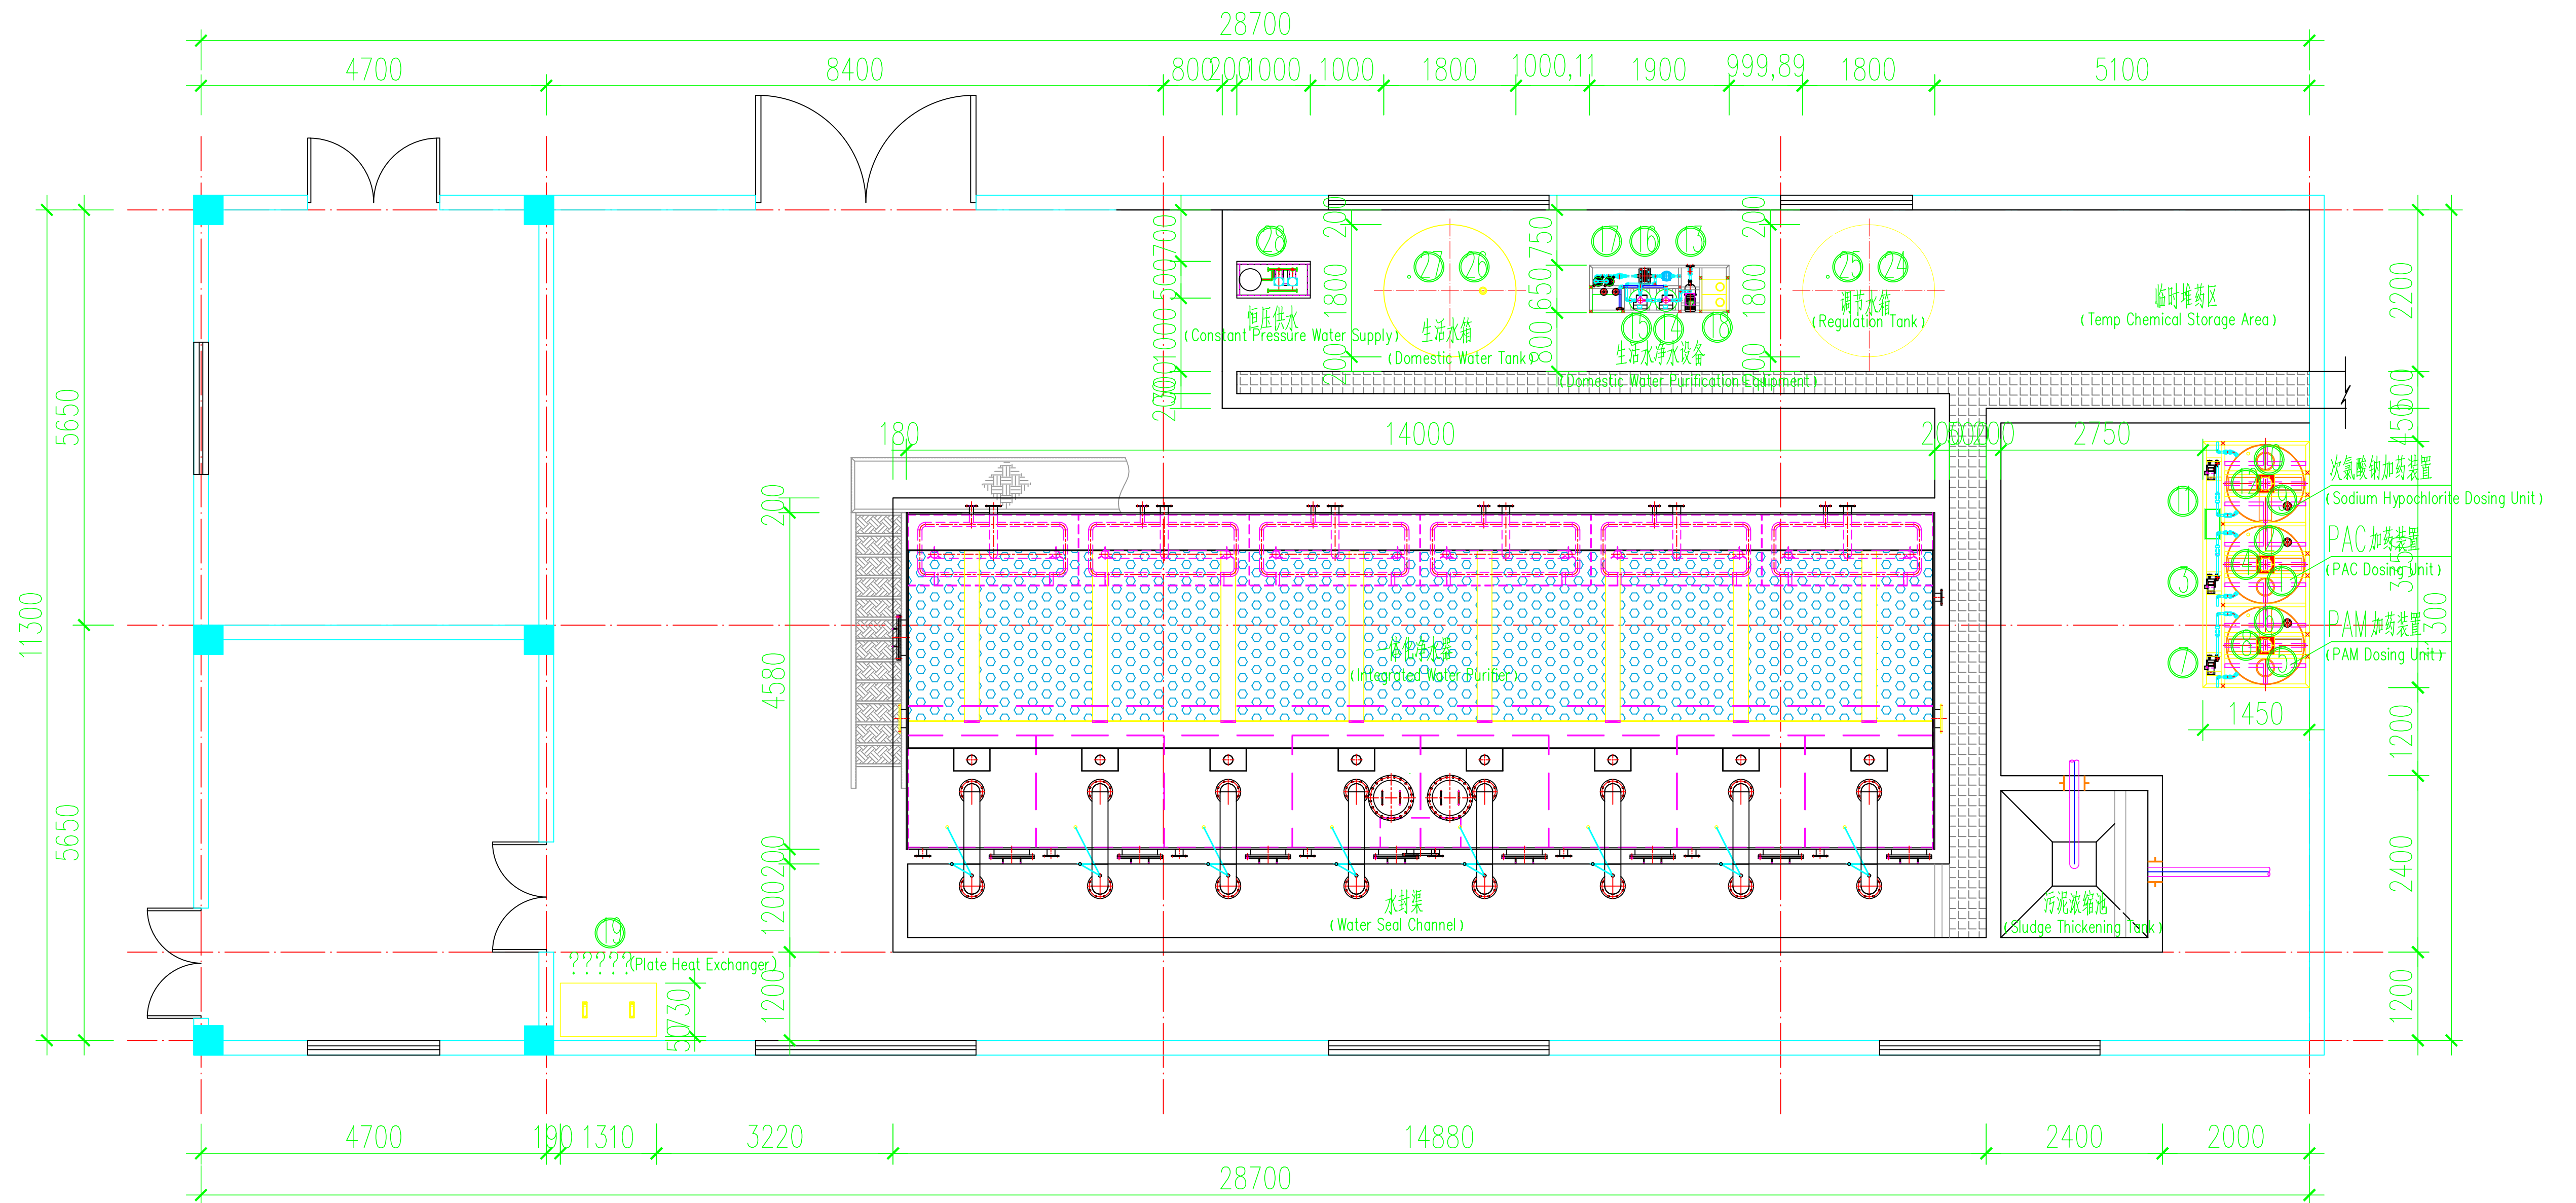


????????????  
(Water Purification Station Equipment Layout Plan)

|                                                                           |     |                      |                             |                                                                 |                                                                                             |                     |                |  |
|---------------------------------------------------------------------------|-----|----------------------|-----------------------------|-----------------------------------------------------------------|---------------------------------------------------------------------------------------------|---------------------|----------------|--|
| 四川盛玖源环境工程有限公司<br>Sichuan shengjiuyuan Environmental Engineering Co., Ltd. |     |                      |                             | 工程名称<br>PROJECT                                                 | 乌兹别克斯坦年产50万吨硫磺制酸项目<br>Uzbekistan 500,000 Tons/Year Sulfur-Based Sulfuric Acid Plant Project |                     |                |  |
|                                                                           |     |                      |                             | 子项名称<br>Sub-item Name                                           | 净水站设备项目<br>Project Water Purification Station Equipment                                     |                     |                |  |
| 审 定<br>APPROVED                                                           | 廖瑞林 | 工程编号<br>PROJECT NO.  | SJY202602                   | 净水站设备定位平面布置<br>Water Purification Station Equipment Layout Plan |                                                                                             |                     |                |  |
| 审 核<br>EXAMINED                                                           | 张永强 | 设计阶段<br>DESIGN STAGE | 施工图<br>CONSTRUCTION DRAWING |                                                                 |                                                                                             |                     |                |  |
| 校 核<br>CHECKED                                                            | 胡欣雨 | 比 例<br>Ratio         | 1:100                       |                                                                 |                                                                                             |                     |                |  |
| 设 计<br>DESIGNED                                                           | 刘 明 | 出图日期<br>DATE         | 2026. 02                    |                                                                 |                                                                                             |                     |                |  |
|                                                                           |     |                      |                             | 图纸编号<br>DRAWING NO.                                             | SJY-GY-04                                                                                   | 专 业<br>Professional | 工 艺<br>Process |  |


???

- 溢流管 (Overflow Pipe)
- 原水管 (Raw Water Pipe)
- 产水管 (Product Water Pipe)
- 污泥管 (Sludge Pipe)
- 蒸汽管 (Steam Pipe)
- 药剂管 (Chemical Pipe)
- 反洗管 (Backwash Pipe)

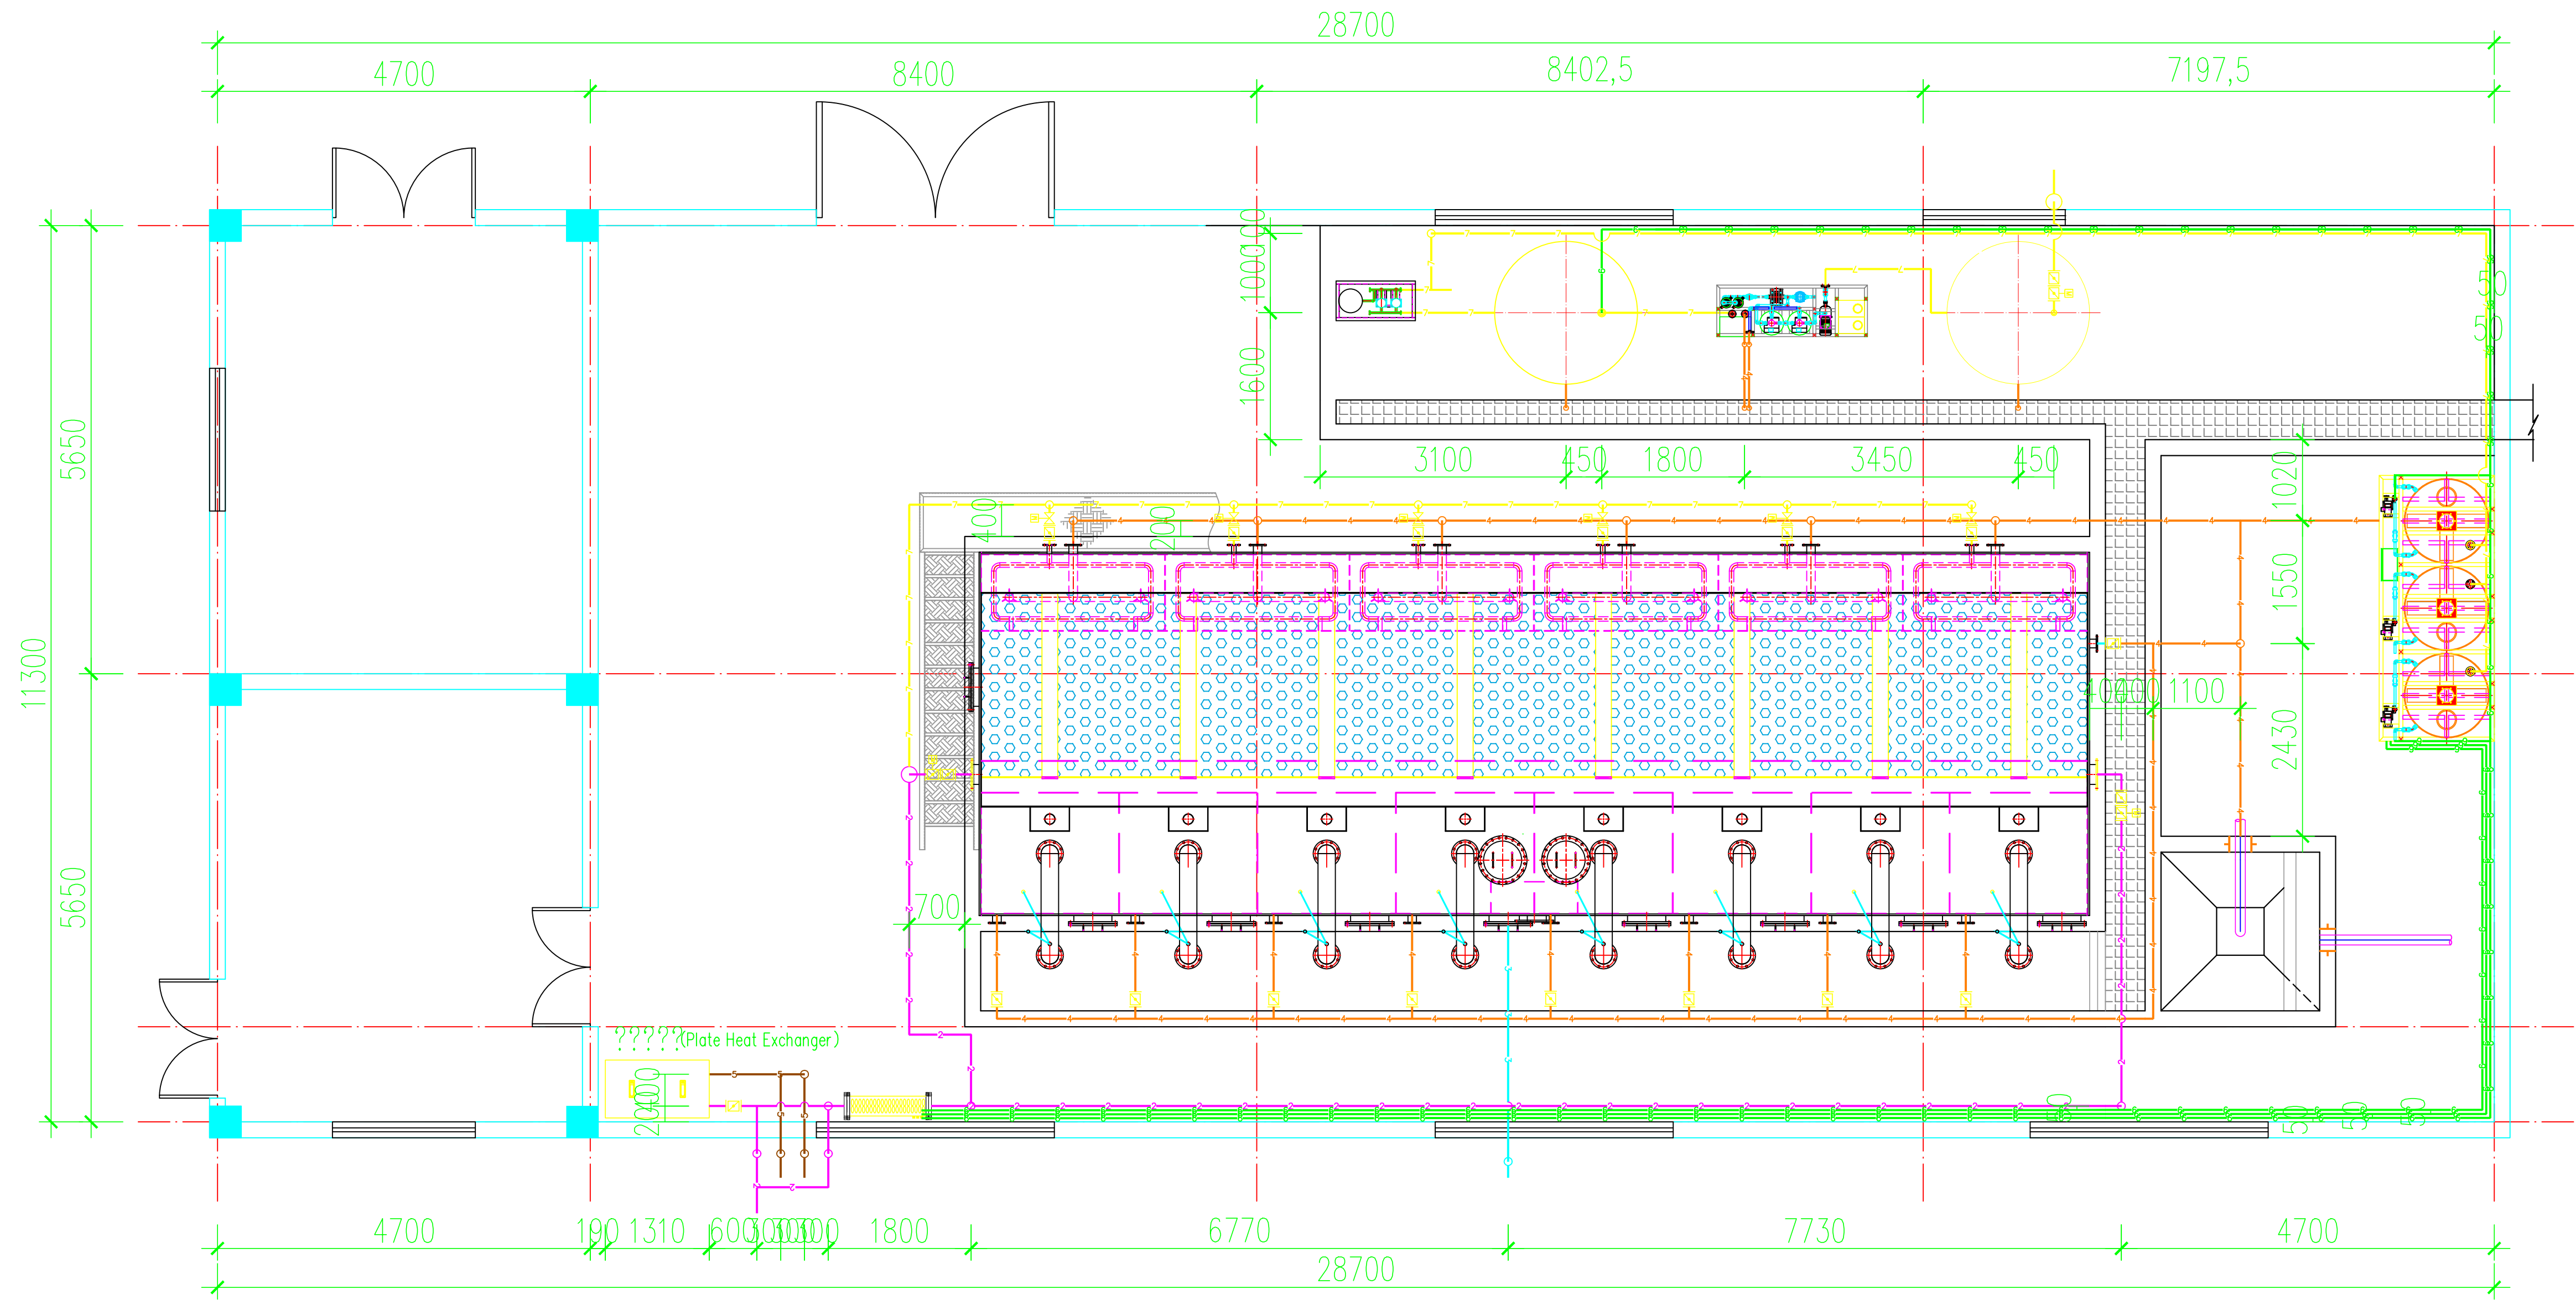


????????  
(Water Purification Station Pipeline Layout Plan)


|                                                                      |  |     |  |                       |  |                                                                                             |  |
|----------------------------------------------------------------------|--|-----|--|-----------------------|--|---------------------------------------------------------------------------------------------|--|
| 四川盛玖源环境工程有限公司<br>Sichuan shengjiuyuan Environmental Engineering Co., |  |     |  | 工程名称<br>PROJECT       |  | 乌兹别克斯坦年产50万吨硫磺制酸项目<br>Uzbekistan 500,000 Tons/Year Sulfur-Based Sulfuric Acid Plant Project |  |
|                                                                      |  |     |  | 子项名称<br>Sub-Item Name |  | 净水站设备项目<br>Project Water Purification Station Equipment                                     |  |
| 审 定<br>APPROVED                                                      |  | 张洪明 |  | 工程编号<br>PROJECT NO.   |  | SJY202602                                                                                   |  |
| 审 核<br>EXAMINED                                                      |  | 张洪明 |  | 设计阶段<br>DESIGNSTAGE   |  | 施工图<br>CONSTRUCTION DRAWING                                                                 |  |
| 校 核<br>CHECKED                                                       |  | 胡欣雨 |  | 比 例<br>Ratio          |  | 1:100                                                                                       |  |
| 设 计<br>DESIGNED                                                      |  | 胡欣雨 |  | 出图日期<br>DATE          |  | 2026. 02                                                                                    |  |
|                                                                      |  |     |  | 图纸编号<br>DRAWING NO.   |  | SJY-GY-06                                                                                   |  |
|                                                                      |  |     |  |                       |  | 专 业<br>Professional                                                                         |  |
|                                                                      |  |     |  |                       |  | 工 艺<br>Process                                                                              |  |

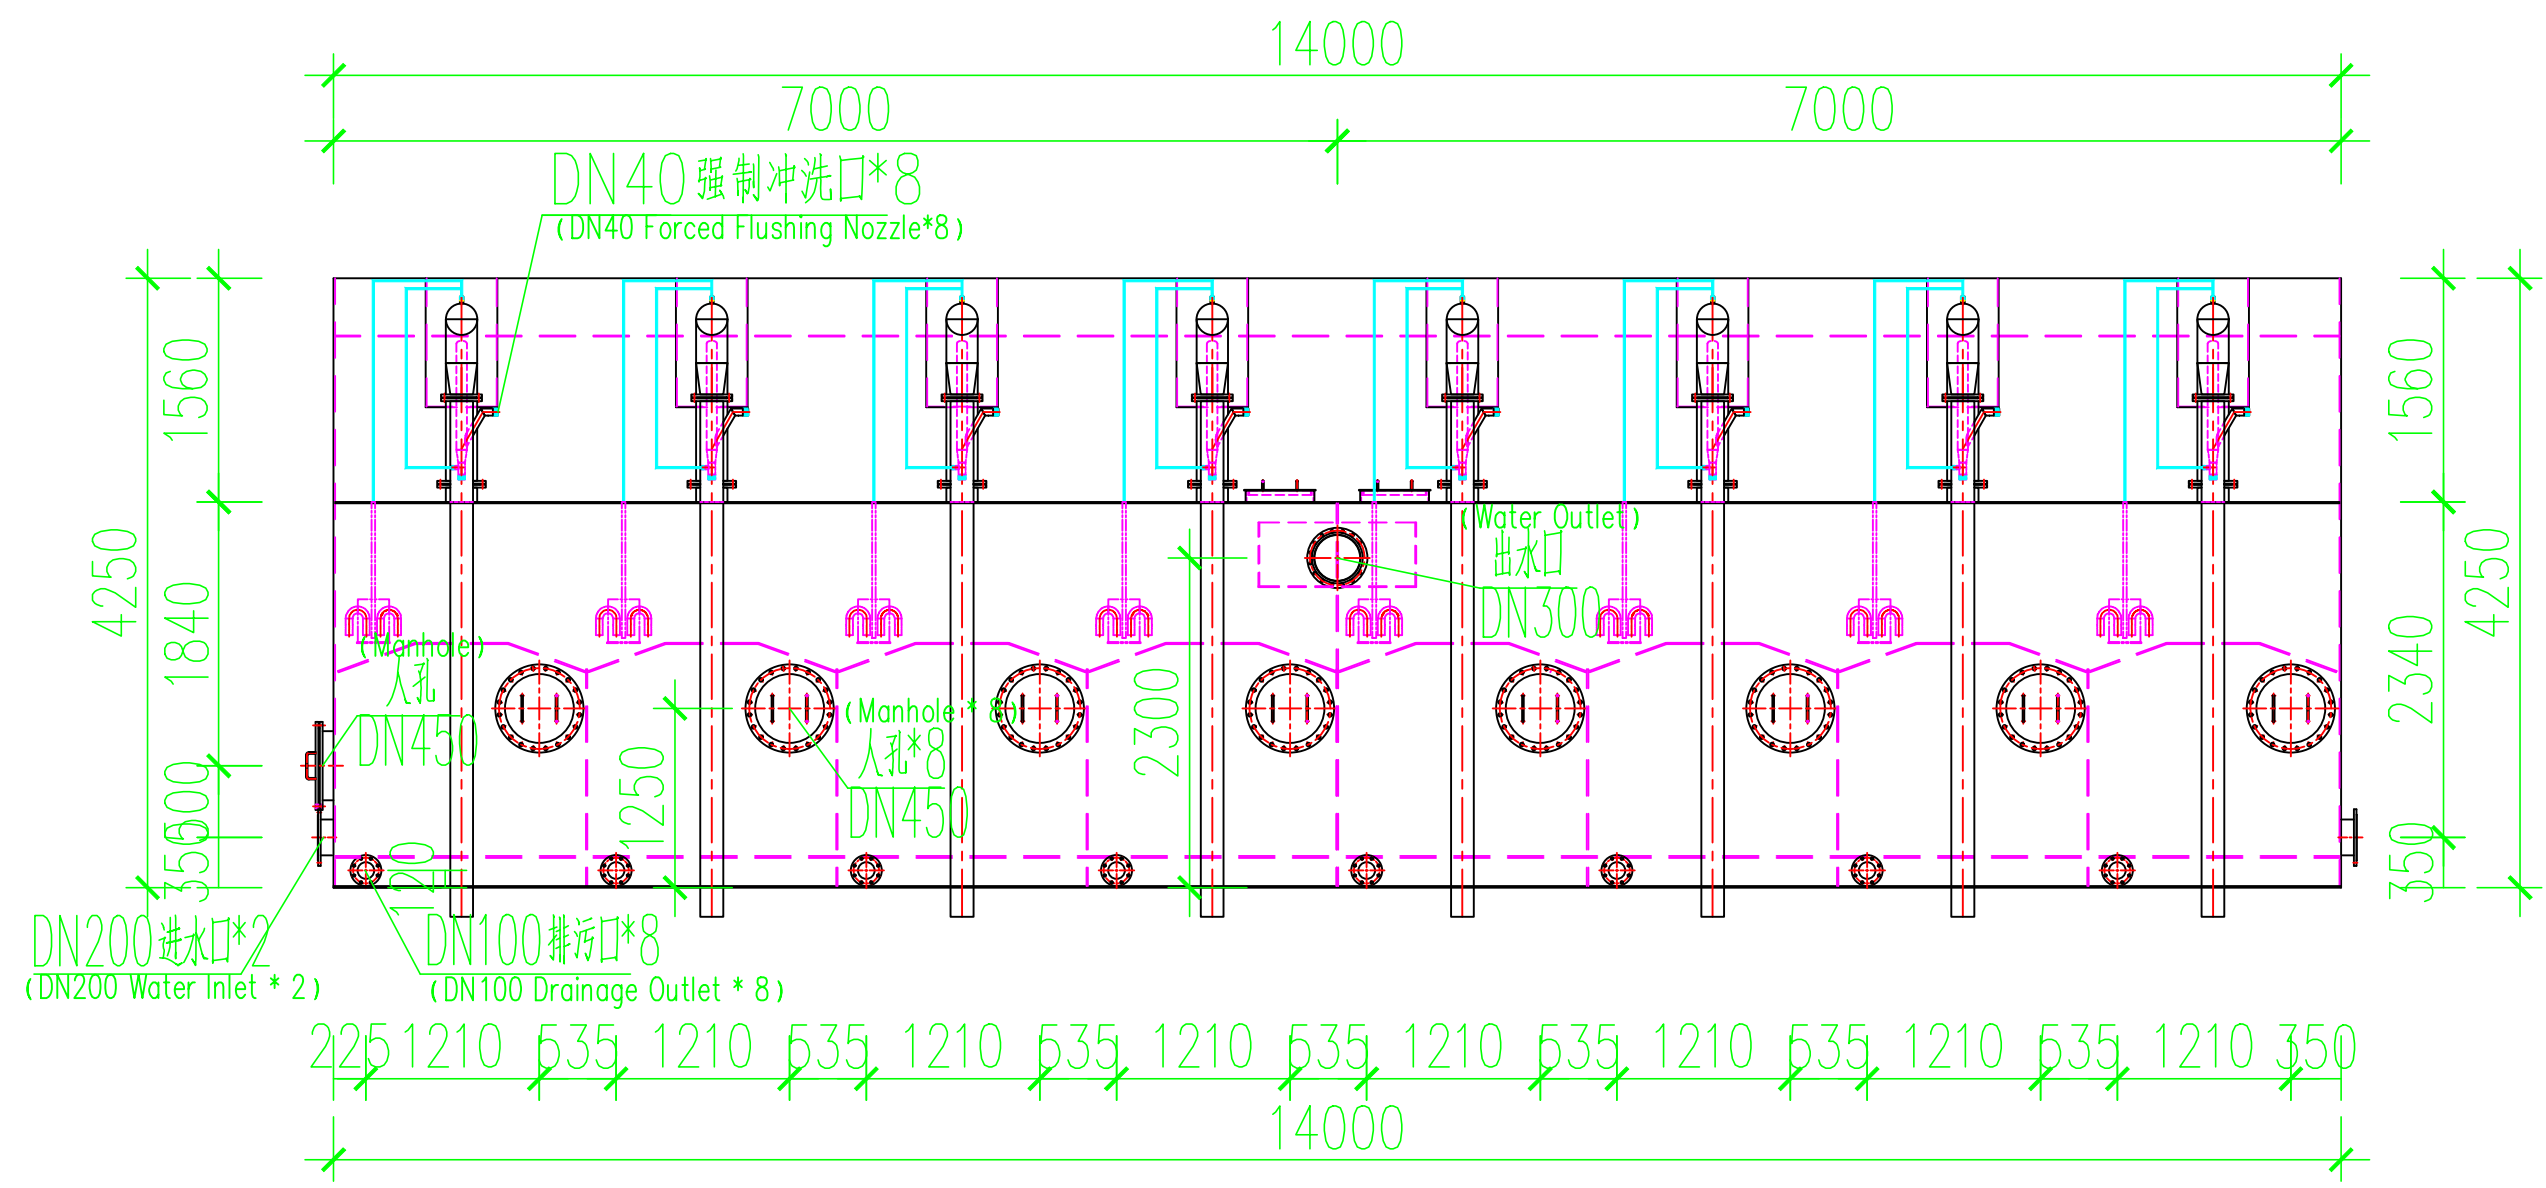

正视图  
(Front View)

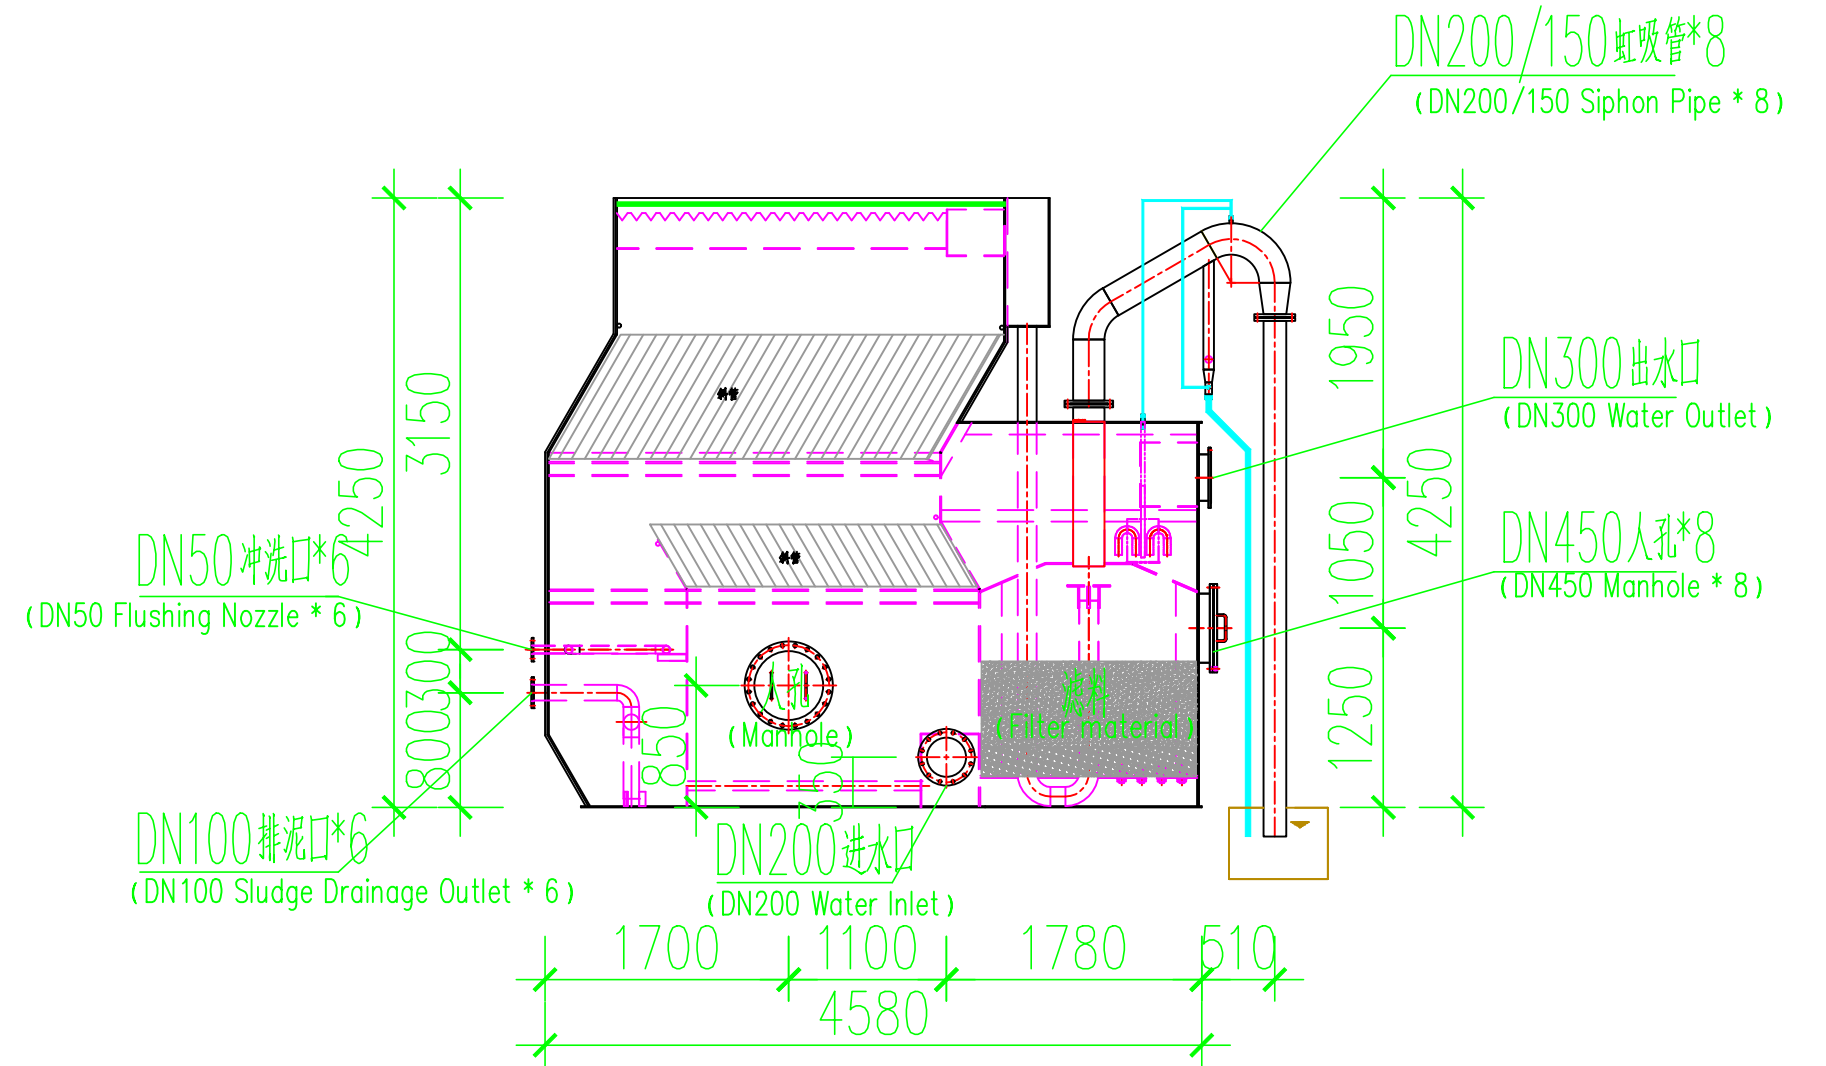

左视图  
(Left View)

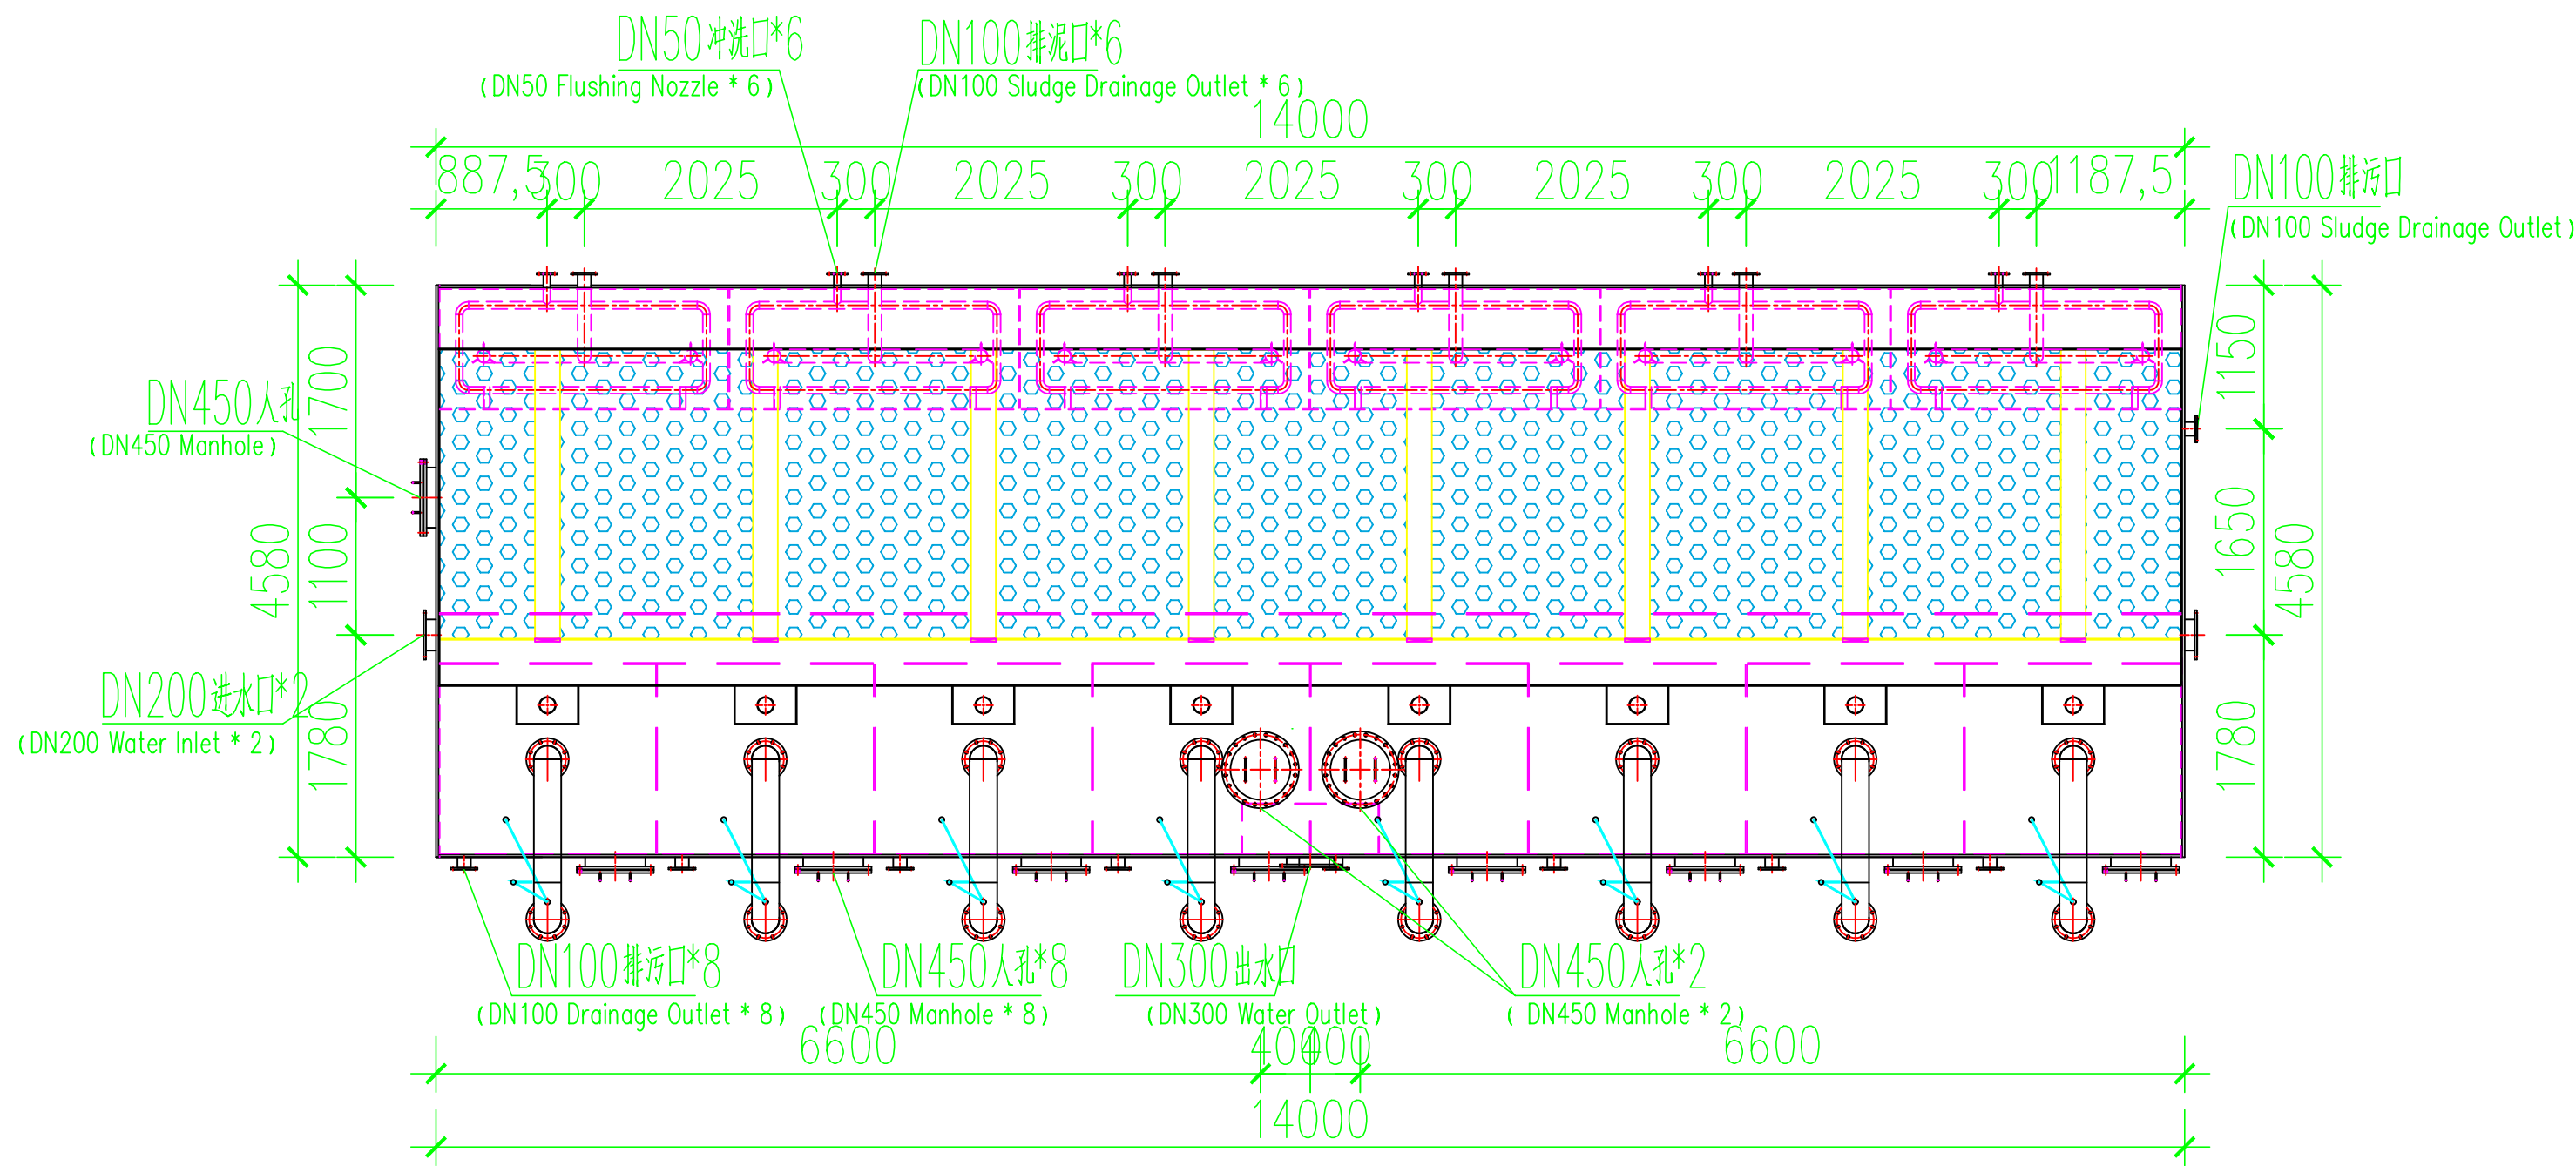

俯视图  
(Top View)


说明:

- 1、本设计尺寸单位: 标高以米计, 其余以毫米计。
- 2、本工程设计一套一体化净水器, 一套生活水净水系统。
- 3、一体化净水器设计处理水量200m<sup>3</sup>/h。
- 4、一体化净水器制作成半成品, 到项目现场进行二次组装。
- 5、设备运行重量约320吨, 虹吸装置可根据现场虹吸渠调整。
- 6、室内排水沟需加盖板, 以便操作人员通行。


Notes:

- 1.Units of measurement in this design: Elevations are in meters, all other dimensions are in millimeters.
- 2.This project includes one integrated water purifier and one domestic water purification system.
- 3.Design flow rate of the integrated water purifier is 200m<sup>3</sup>/h.
- 4.The integrated water purifier is manufactured as semi-finished products and assembled on-site at the project location.
- 5.The operating weight of the equipment is approximately 320 tons. The siphon device can be adjusted according to the on-site siphon channel.
- 6.Indoor drainage ditches shall be covered with plates for operator access.


|                                                                           |     |                     |                             |                       |                                                                                             |                     |                |
|---------------------------------------------------------------------------|-----|---------------------|-----------------------------|-----------------------|---------------------------------------------------------------------------------------------|---------------------|----------------|
| 四川盛玖源环境工程有限公司<br>Sichuan shengjiuyuan Environmental Engineering Co., Ltd. |     |                     |                             | 工程名称<br>PROJECT       | 乌兹别克斯坦年产50万吨硫磺制酸项目<br>Uzbekistan 500,000 Tons/Year Sulfur-Based Sulfuric Acid Plant Project |                     |                |
|                                                                           |     |                     |                             | 子项名称<br>Sub-Item Name | 净水站设备项目<br>Project Water Purification Station Equipment                                     |                     |                |
| 审 定<br>APPROVED                                                           | 张洪明 | 工程编号<br>PROJECT NO. | SJY202602                   |                       | 净水器外形尺寸图<br>External Dimension Drawing of Water Purifier                                    |                     |                |
| 审 核<br>EXAMINED                                                           | 张公强 | 设计阶段<br>DESIGNSTAGE | 施工图<br>CONSTRUCTION DRAWING |                       |                                                                                             |                     |                |
| 校 核<br>CHECKED                                                            | 胡欣雨 | 比 例<br>Ratio        | 1:100                       |                       |                                                                                             |                     |                |
| 设 计<br>DESIGNED                                                           | 刘冲  | 出图日期<br>DATE        | 2026. 02                    |                       |                                                                                             |                     |                |
|                                                                           |     |                     |                             | 图纸编号<br>DRAWING NO.   | SJY-GY-08                                                                                   | 专 业<br>Professional | 工 艺<br>Process |

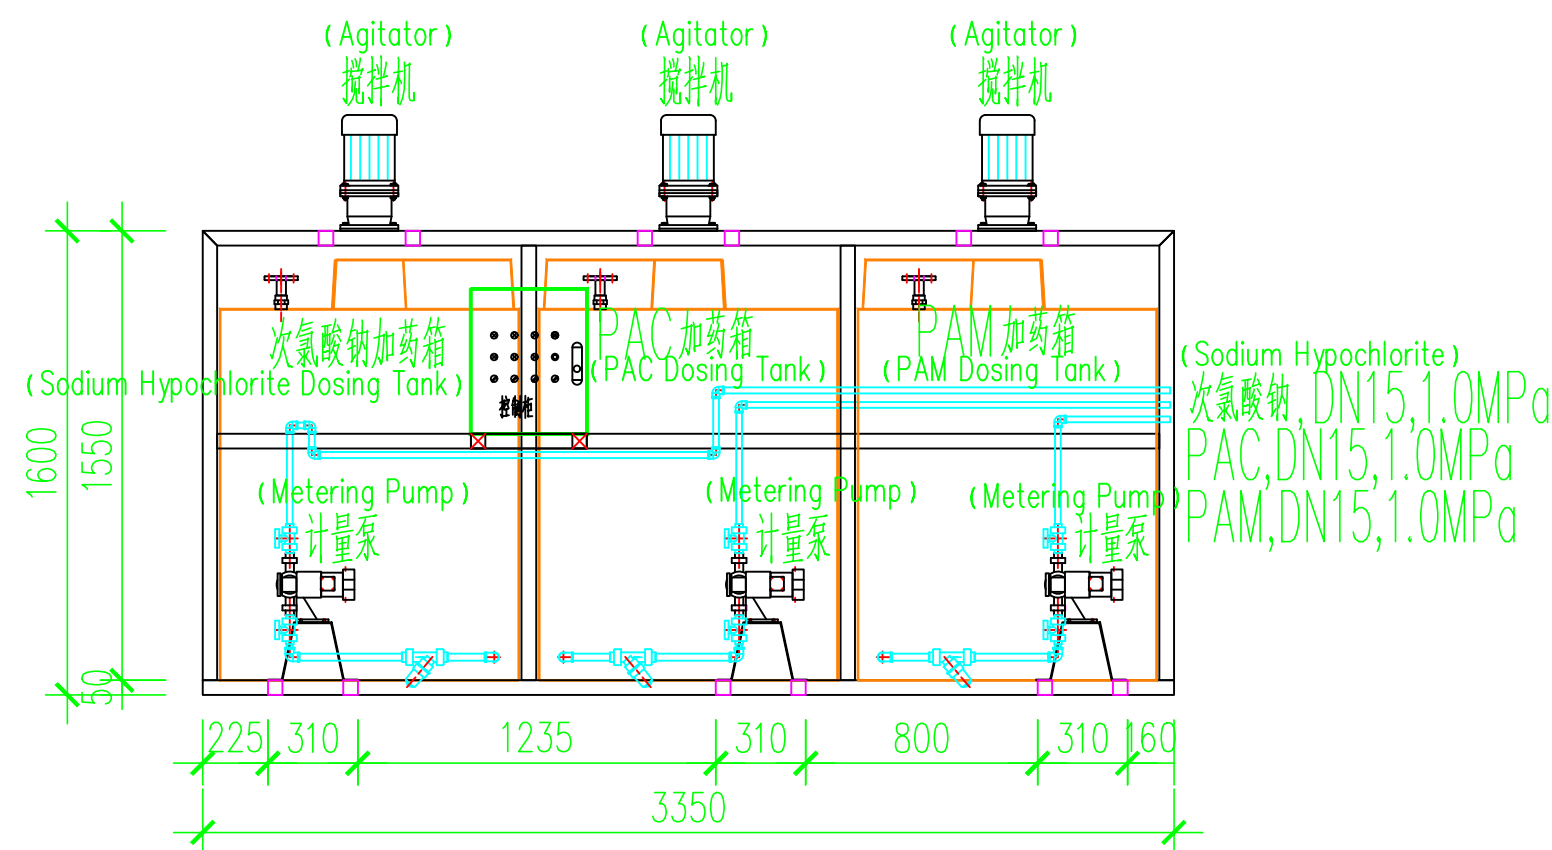

正视图  
(Front View)

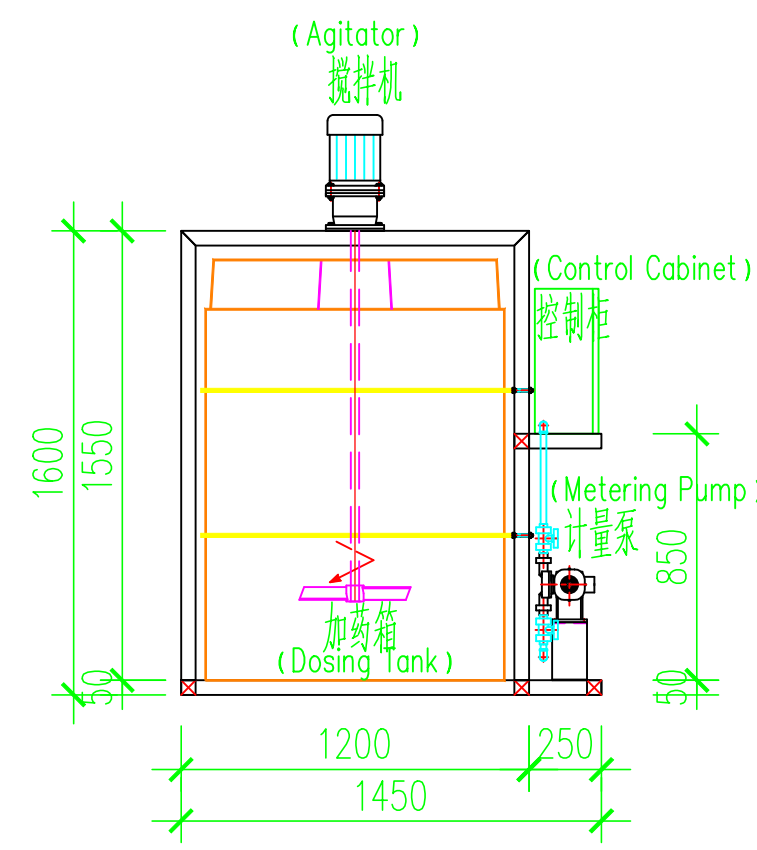

左视图  
(Left View)

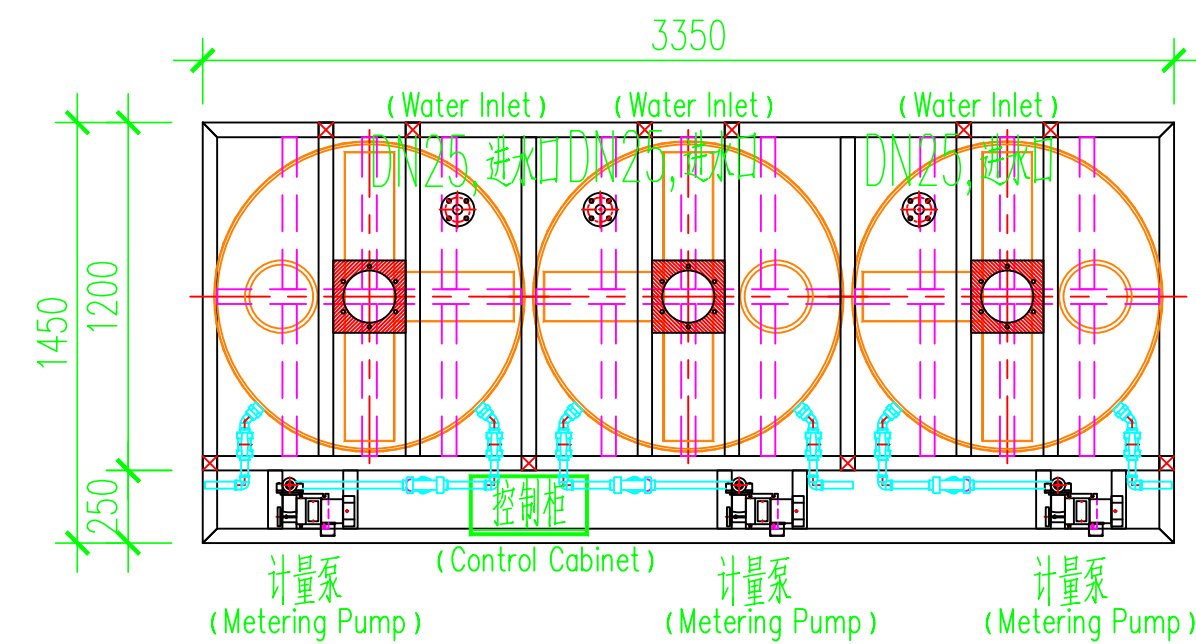

俯视图  
(Top View)

说明:


- 1、本设计尺寸单位: 标高以米计, 其余以毫米计。
- 2、加药设备集成于一个机架上, 配套集成管阀件和就地控制箱。

Notes:


- 1.Units of measurement in this design: Elevations are in meters, all other dimensions are in millimeters.
- 2.The chemical dosing equipment is integrated on one frame, with integrated pipe fittings and local control cabinet.

| 加药装置设备清单 Chemical Dosing Unit List |                                               |                                                   |         |         |                             |            |
|------------------------------------|-----------------------------------------------|---------------------------------------------------|---------|---------|-----------------------------|------------|
| 序号No.                              | 名称 Name                                       | 规格型号 Model & Spec                                 | 单位 Unit | 数量 Qty. | 材质 Material                 | 备注 Remarks |
| 1                                  | PAC加药箱<br>PAC Dosing Tank                     | 1000L/ $\varphi$ 1180×1300                        | 台 /unit | 1       | PE                          |            |
| 2                                  | 液位计<br>Level Gauge                            | MD-UK221/0-5m                                     | 套 /set  | 1       | 工程塑料<br>Engineering Plastic | 24V        |
| 3                                  | 计量泵<br>Metering Pump                          | Q=60L/h, 压力P=1.0MPa<br>Q=60L/h, Pressure P=1.0MPa | 台 /unit | 1       | PVC泵头<br>PVC Pump Head      | 380V,50Hz  |
| 4                                  | 搅拌电机<br>Agitator Motor                        | 0.55KW, 70-100r/min                               | 台 /unit | 1       | 304叶轮<br>304 Impeller       | 380V,50Hz  |
| 5                                  | PAM加药箱<br>PAM Dosing Tank                     | 1000L/ $\varphi$ 1180×1300                        | 台 /unit | 1       | PE                          |            |
| 6                                  | 液位计<br>Level Gauge                            | MD-UK221/0-5m                                     | 套 /set  | 1       | 工程塑料<br>Engineering Plastic | 24V        |
| 7                                  | 计量泵<br>Metering Pump                          | Q=60L/h, 压力P=1.0MPa<br>Q=60L/h, Pressure P=1.0MPa | 台 /unit | 1       | PVC泵头<br>PVC Pump Head      | 380V,50Hz  |
| 8                                  | 搅拌电机<br>Agitator Motor                        | 0.55KW, 70-100r/min                               | 台 /unit | 1       | 304叶轮<br>304 Impeller       | 380V,50Hz  |
| 9                                  | 次氯酸钠加药箱<br>Sodium Hypochlorite<br>Dosing Tank | 1000L/ $\varphi$ 1180×1300                        | 台 /unit | 1       | PE                          |            |
| 10                                 | 液位计<br>Level Gauge                            | MD-UK221/0-5m                                     | 套 /set  | 1       | 工程塑料<br>Engineering Plastic | 24V        |
| 11                                 | 计量泵<br>Metering Pump                          | Q=15L/h, 压力P=1.0MPa<br>Q=60L/h, Pressure P=1.0MPa | 台 /unit | 1       | PVC泵头<br>PVC Pump Head      | 380V,50Hz  |
| 12                                 | 搅拌电机<br>Agitator Motor                        | 0.55KW, 70-100r/min                               | 台 /unit | 1       | 304叶轮<br>304 Impeller       | 380V,50Hz  |


|                                                                           |     |                       |                                                                                             |                     |                |
|---------------------------------------------------------------------------|-----|-----------------------|---------------------------------------------------------------------------------------------|---------------------|----------------|
| 四川盛玖源环境工程有限公司<br>Sichuan shengjiuyuan Environmental Engineering Co., Ltd. |     | 工程名称<br>PROJECT       | 乌兹别克斯坦年产50万吨硫磺制酸项目<br>Uzbekistan 500,000 Tons/Year Sulfur-Based Sulfuric Acid Plant Project |                     |                |
|                                                                           |     | 子项名称<br>Sub-item Name | 净水站设备项目<br>Project Water Purification Station Equipment                                     |                     |                |
| 审 定<br>APPROVED                                                           | 廖强林 | 工程编号<br>PROJECT NO.   | SJY202602                                                                                   |                     |                |
| 审 核<br>EXAMINED                                                           | 张永强 | 设计阶段<br>DESIGNSTAGE   | 施工图<br>CONSTRUCTION DRAWING                                                                 |                     |                |
| 校 核<br>CHECKED                                                            | 胡欣雨 | 比 例<br>Ratio          | 1:100                                                                                       |                     |                |
| 设 计<br>DESIGNED                                                           | 刘 明 | 出图日期<br>DATE          | 2026. 02                                                                                    |                     |                |
|                                                                           |     | 图纸编号<br>DRAWING NO.   | SJY-GY-09                                                                                   | 专 业<br>Professional | 工 艺<br>Process |

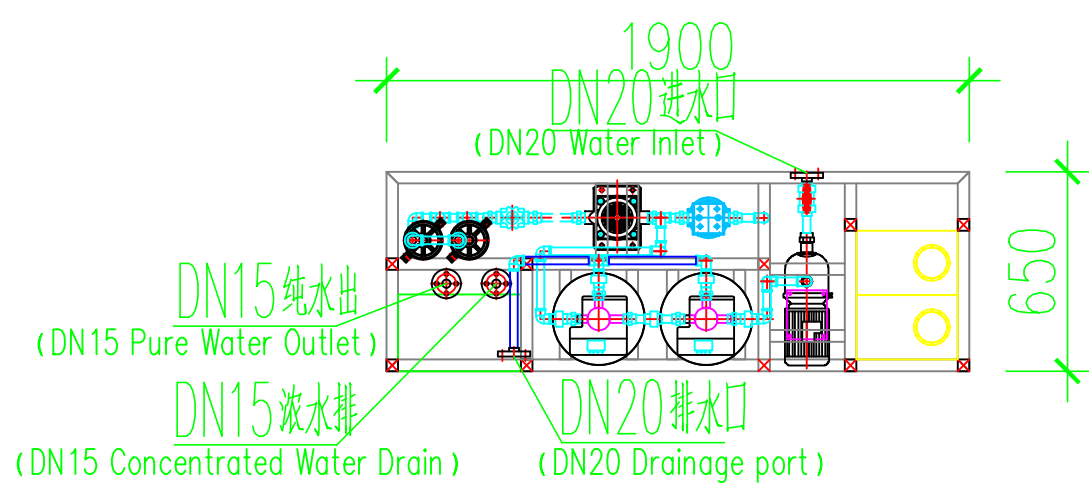


俯视图  
(Top View)

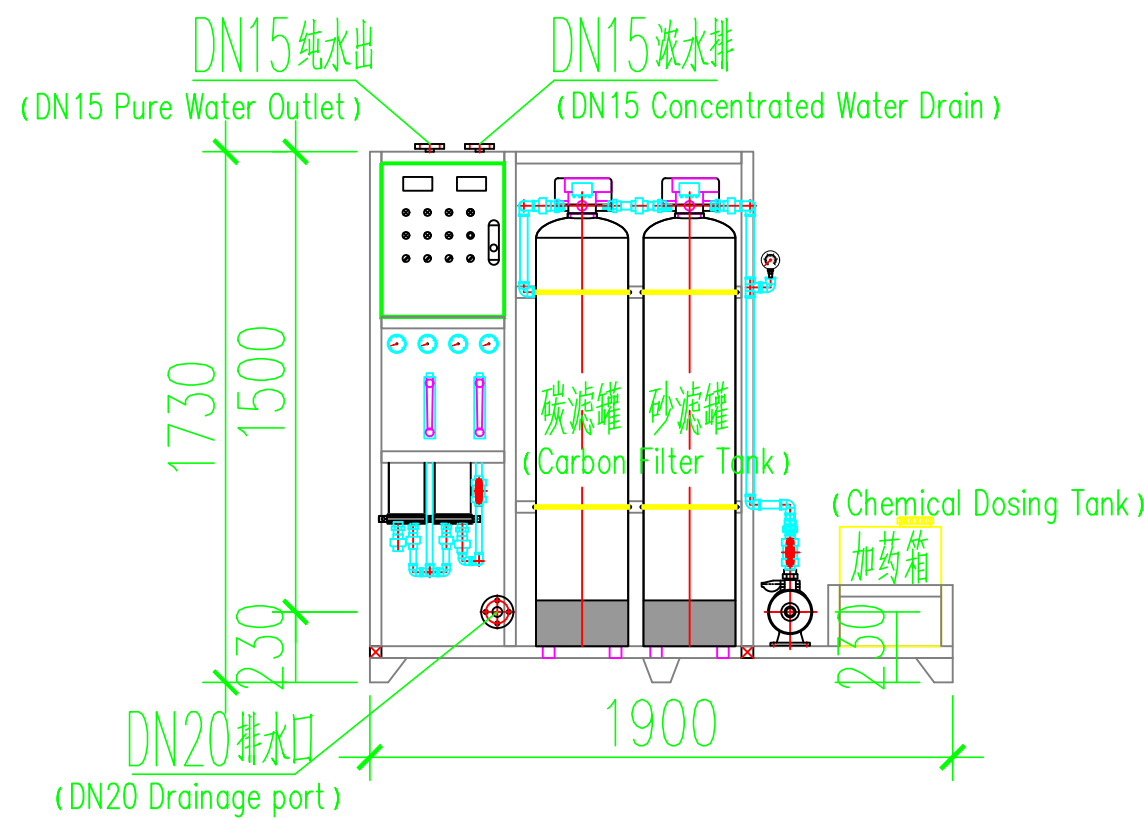


主视图  
(Front View)

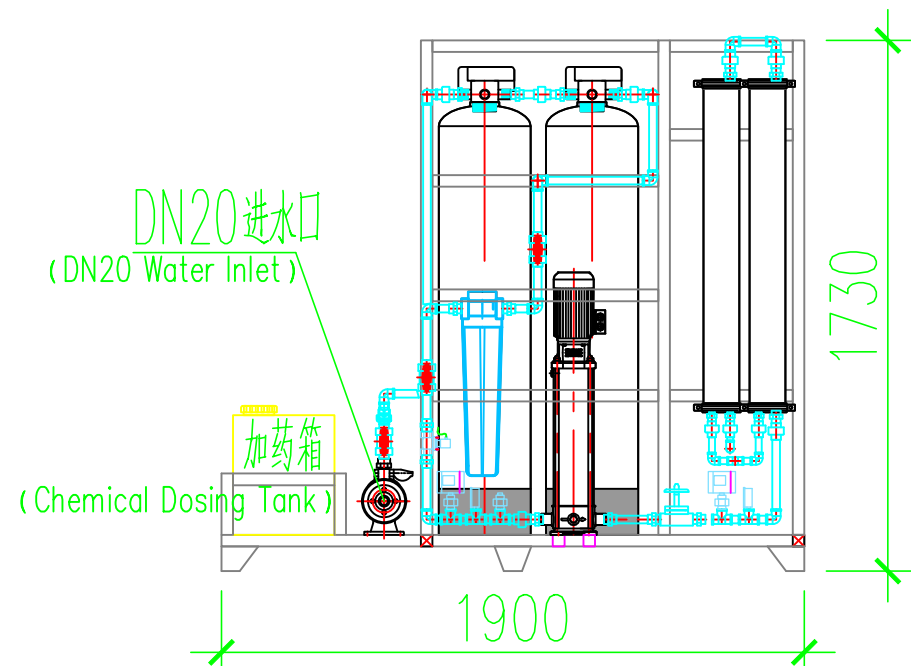

后视图  
(Rear View)

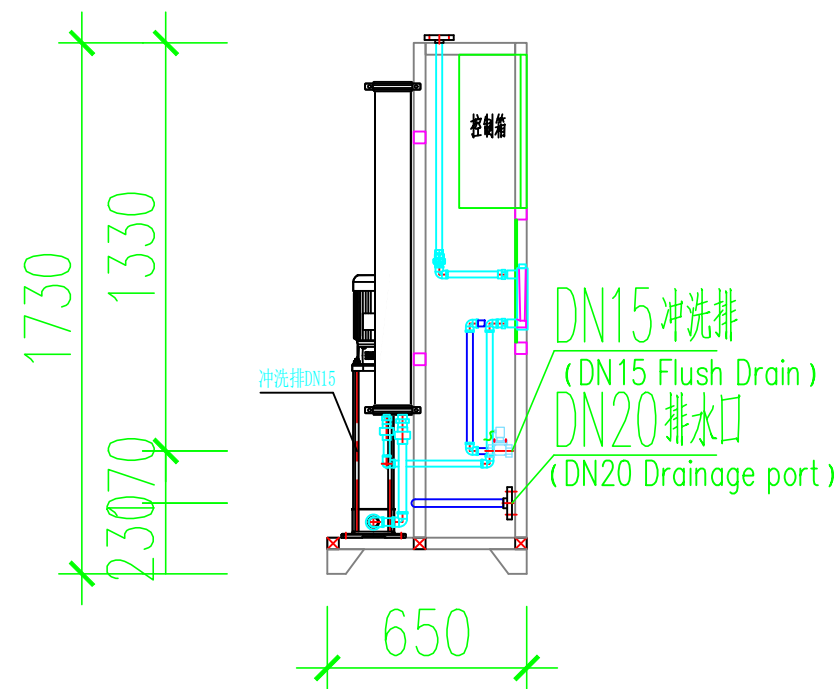

左视图  
(Left View)

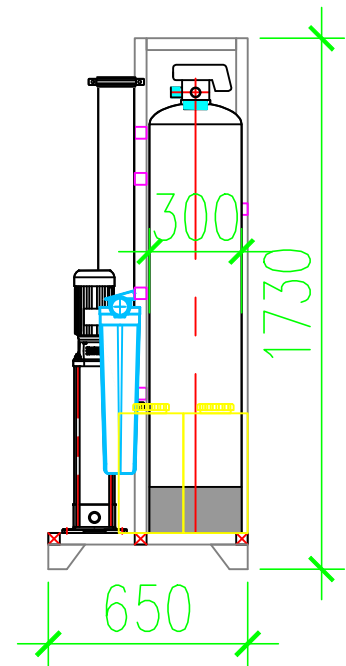

右视图  
(Right View)


说明:

- 1、本设计尺寸单位: 标高以米计, 其余以毫米计。
- 2、生活水净水设备集成于一个机架上, 配套集成管阀件和就地控制箱。


Notes:

- 1.Units of measurement in this design: Elevations are in meters, all other dimensions are in millimeters.
- 2.The domestic water purification equipment is integrated on one frame, with integrated pipe fittings and local control cabinet.

| 生活水净水设备清单 Domestic Water Purification Equipment List |                                   |   |         |         |             |            |
|------------------------------------------------------|-----------------------------------|---|---------|---------|-------------|------------|
| 序号No.                                                | 名称 Name                           | 规格型号 Model & Spec                                                                                               | 单位 Unit | 数量 Qty. | 材质 Material | 备注 Remarks |
| 13                                                   | 增压泵1<br>Booster Pump 1            | 生活水净水设备配套, 提升能力≥5m3/d, N=0.55kW<br>For domestic water purification system,<br>lifting capacity ≥5m3/d, N=0.55kW | 台 /unit | 1       |             | 380V,50Hz  |
| 14                                                   | 多介质过滤器<br>Multi-media Filter      | 处理能力: Q≥5m3/d<br>Capacity: Q≥5m3/d                                                                              | 套 /set  | 1       |             |            |
| 15                                                   | 活性炭过滤器<br>Activated Carbon Filter | 处理能力: Q≥5m3/d<br>Capacity: Q≥5m3/d                                                                              | 套 /set  | 1       |             |            |
| 16                                                   | 增压泵2<br>Booster Pump 2            | 生活水净水设备配套, 提升能力≥5m3/d, N=1.1kW<br>For domestic water purification system,<br>lifting capacity ≥5m3/d, N=1.1kW   | 台 /unit | 1       |             | 380V,50Hz  |
| 17                                                   | RO机组<br>RO Unit                   | 处理能力: Q≥5m3/d, 配套膜/仪表、连接管道 / Pipe/管件/阀门等<br>membrane/instruments, connecting pipes<br>/fittings/valves, etc.    | 台 /unit | 1       |             |            |
| 18                                                   | 清洗系统<br>Cleaning System           | 生活水净水设备配套, 加药泵N=12W<br>For domestic water purification system,<br>dosing pump N=12W                             | 套 /set  | 2       |             | 380V,50Hz  |

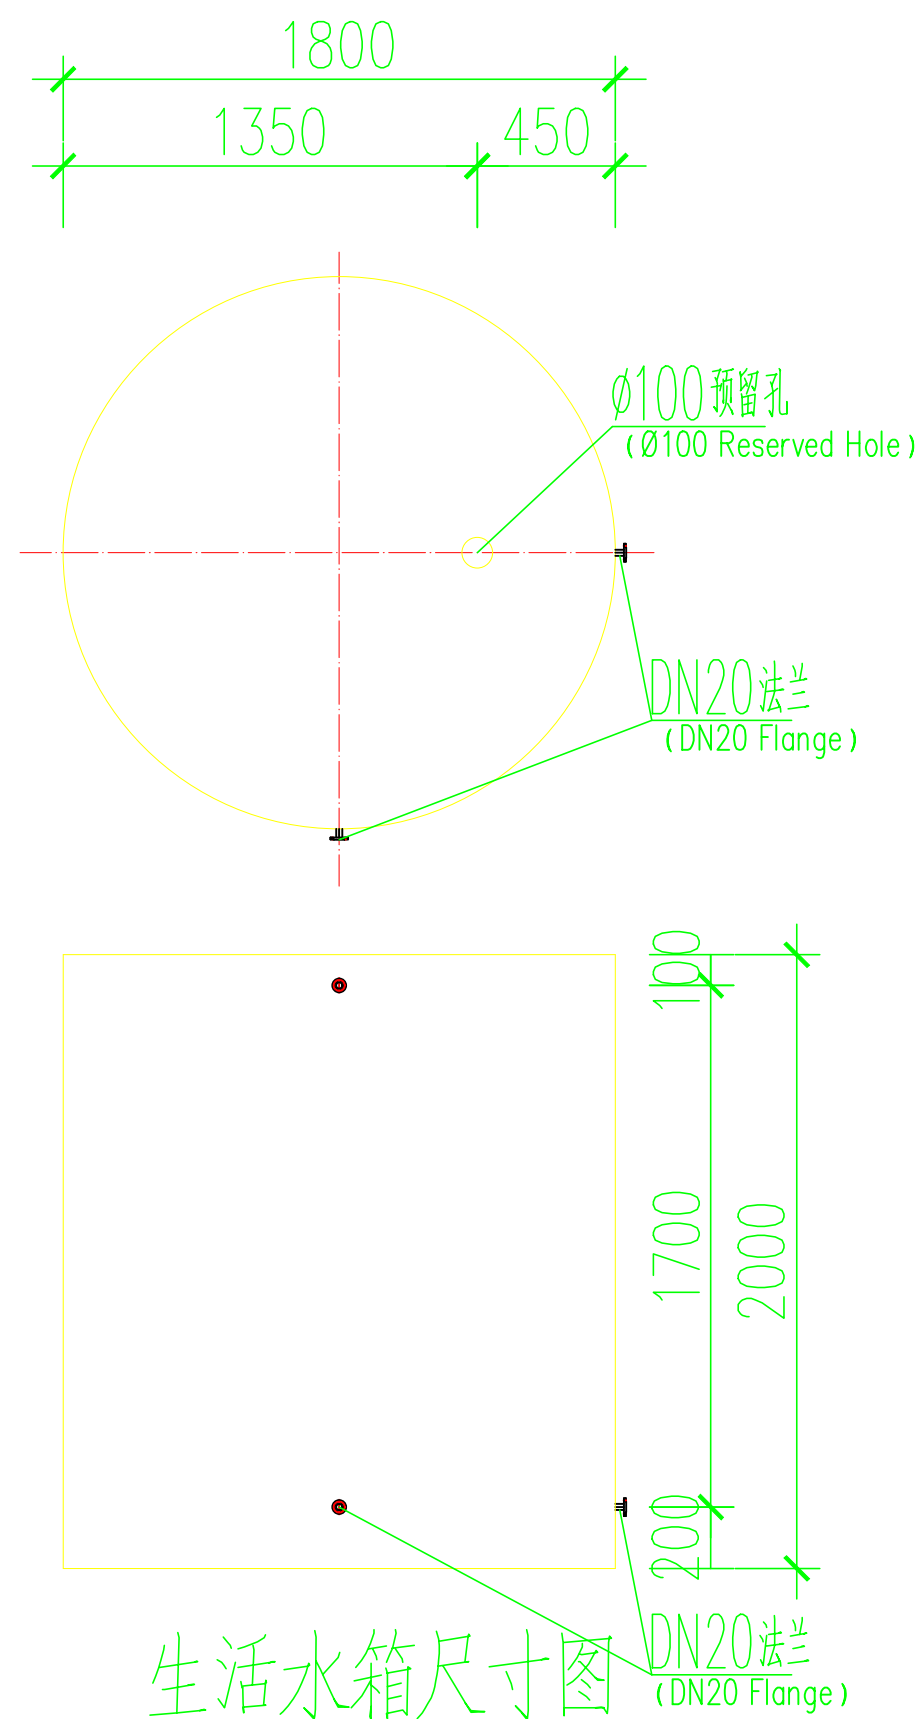

生活水箱尺寸图  
(Domestic Water Tank Dimension Drawing)

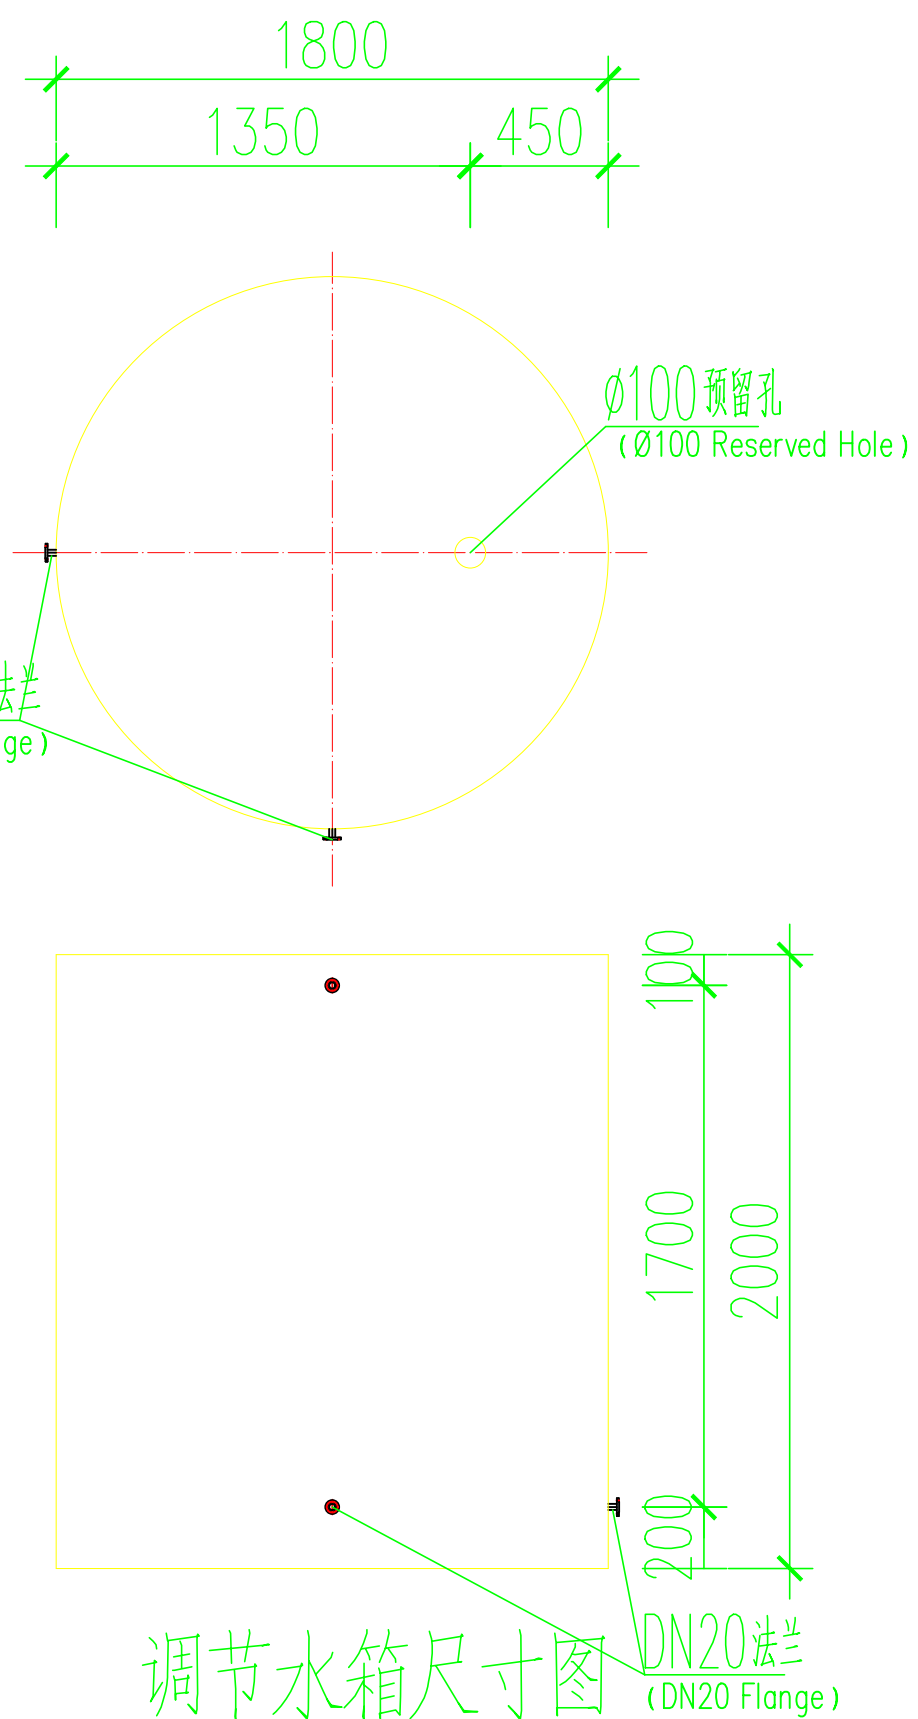


调节水箱尺寸图  
(Regulating Water Tank Dimension Drawing)

|                                                                      |     |                     |                             |                                                                               |                                                                                             |                     |                |
|----------------------------------------------------------------------|-----|---------------------|-----------------------------|-------------------------------------------------------------------------------|---------------------------------------------------------------------------------------------|---------------------|----------------|
| 四川盛玖源环境工程有限公司<br>Sichuan shengjiuyuan Environmental Engineering Co., |     |                     |                             | 工程名称<br>PROJECT                                                               | 乌兹别克斯坦年产50万吨硫磺制酸项目<br>Uzbekistan 500,000 Tons/Year Sulfur-Based Sulfuric Acid Plant Project |                     |                |
|                                                                      |     |                     |                             | 子项名称<br>Sub-Item Name                                                         | 净水站设备项目<br>Project Water Purification Station Equipment                                     |                     |                |
| 审 定<br>APPROVED                                                      | 张洪明 | 工程编号<br>PROJECT NO. | SJY202602                   | 生活水系统设备外形尺寸图<br>External Dimension Drawing of Domestic Water System Equipment |                                                                                             |                     |                |
| 审 核<br>EXAMINED                                                      | 张公征 | 设计阶段<br>DESIGNSTAGE | 施工图<br>CONSTRUCTION DRAWING |                                                                               |                                                                                             |                     |                |
| 校 核<br>CHECKED                                                       | 胡欣雨 | 比 例<br>Ratio        | 1:100                       |                                                                               |                                                                                             |                     |                |
| 设 计<br>DESIGNED                                                      | 刘冲  | 出图日期<br>DATE        | 2026. 02                    |                                                                               |                                                                                             |                     |                |
|                                                                      |     |                     |                             | 图纸编号<br>DRAWING NO.                                                           | SJY-GY-10                                                                                   | 专 业<br>Professional | 工 艺<br>Process |

???

- 溢流管 (Overflow Pipe)
- 原水管 (Raw Water Pipe)
- 产水管 (Product Water Pipe)
- 污泥管 (Sludge Pipe)
- 蒸汽管 (Steam Pipe)
- 药剂管 (Chemical Pipe)
- F 反洗管 (Backwash Pipe)

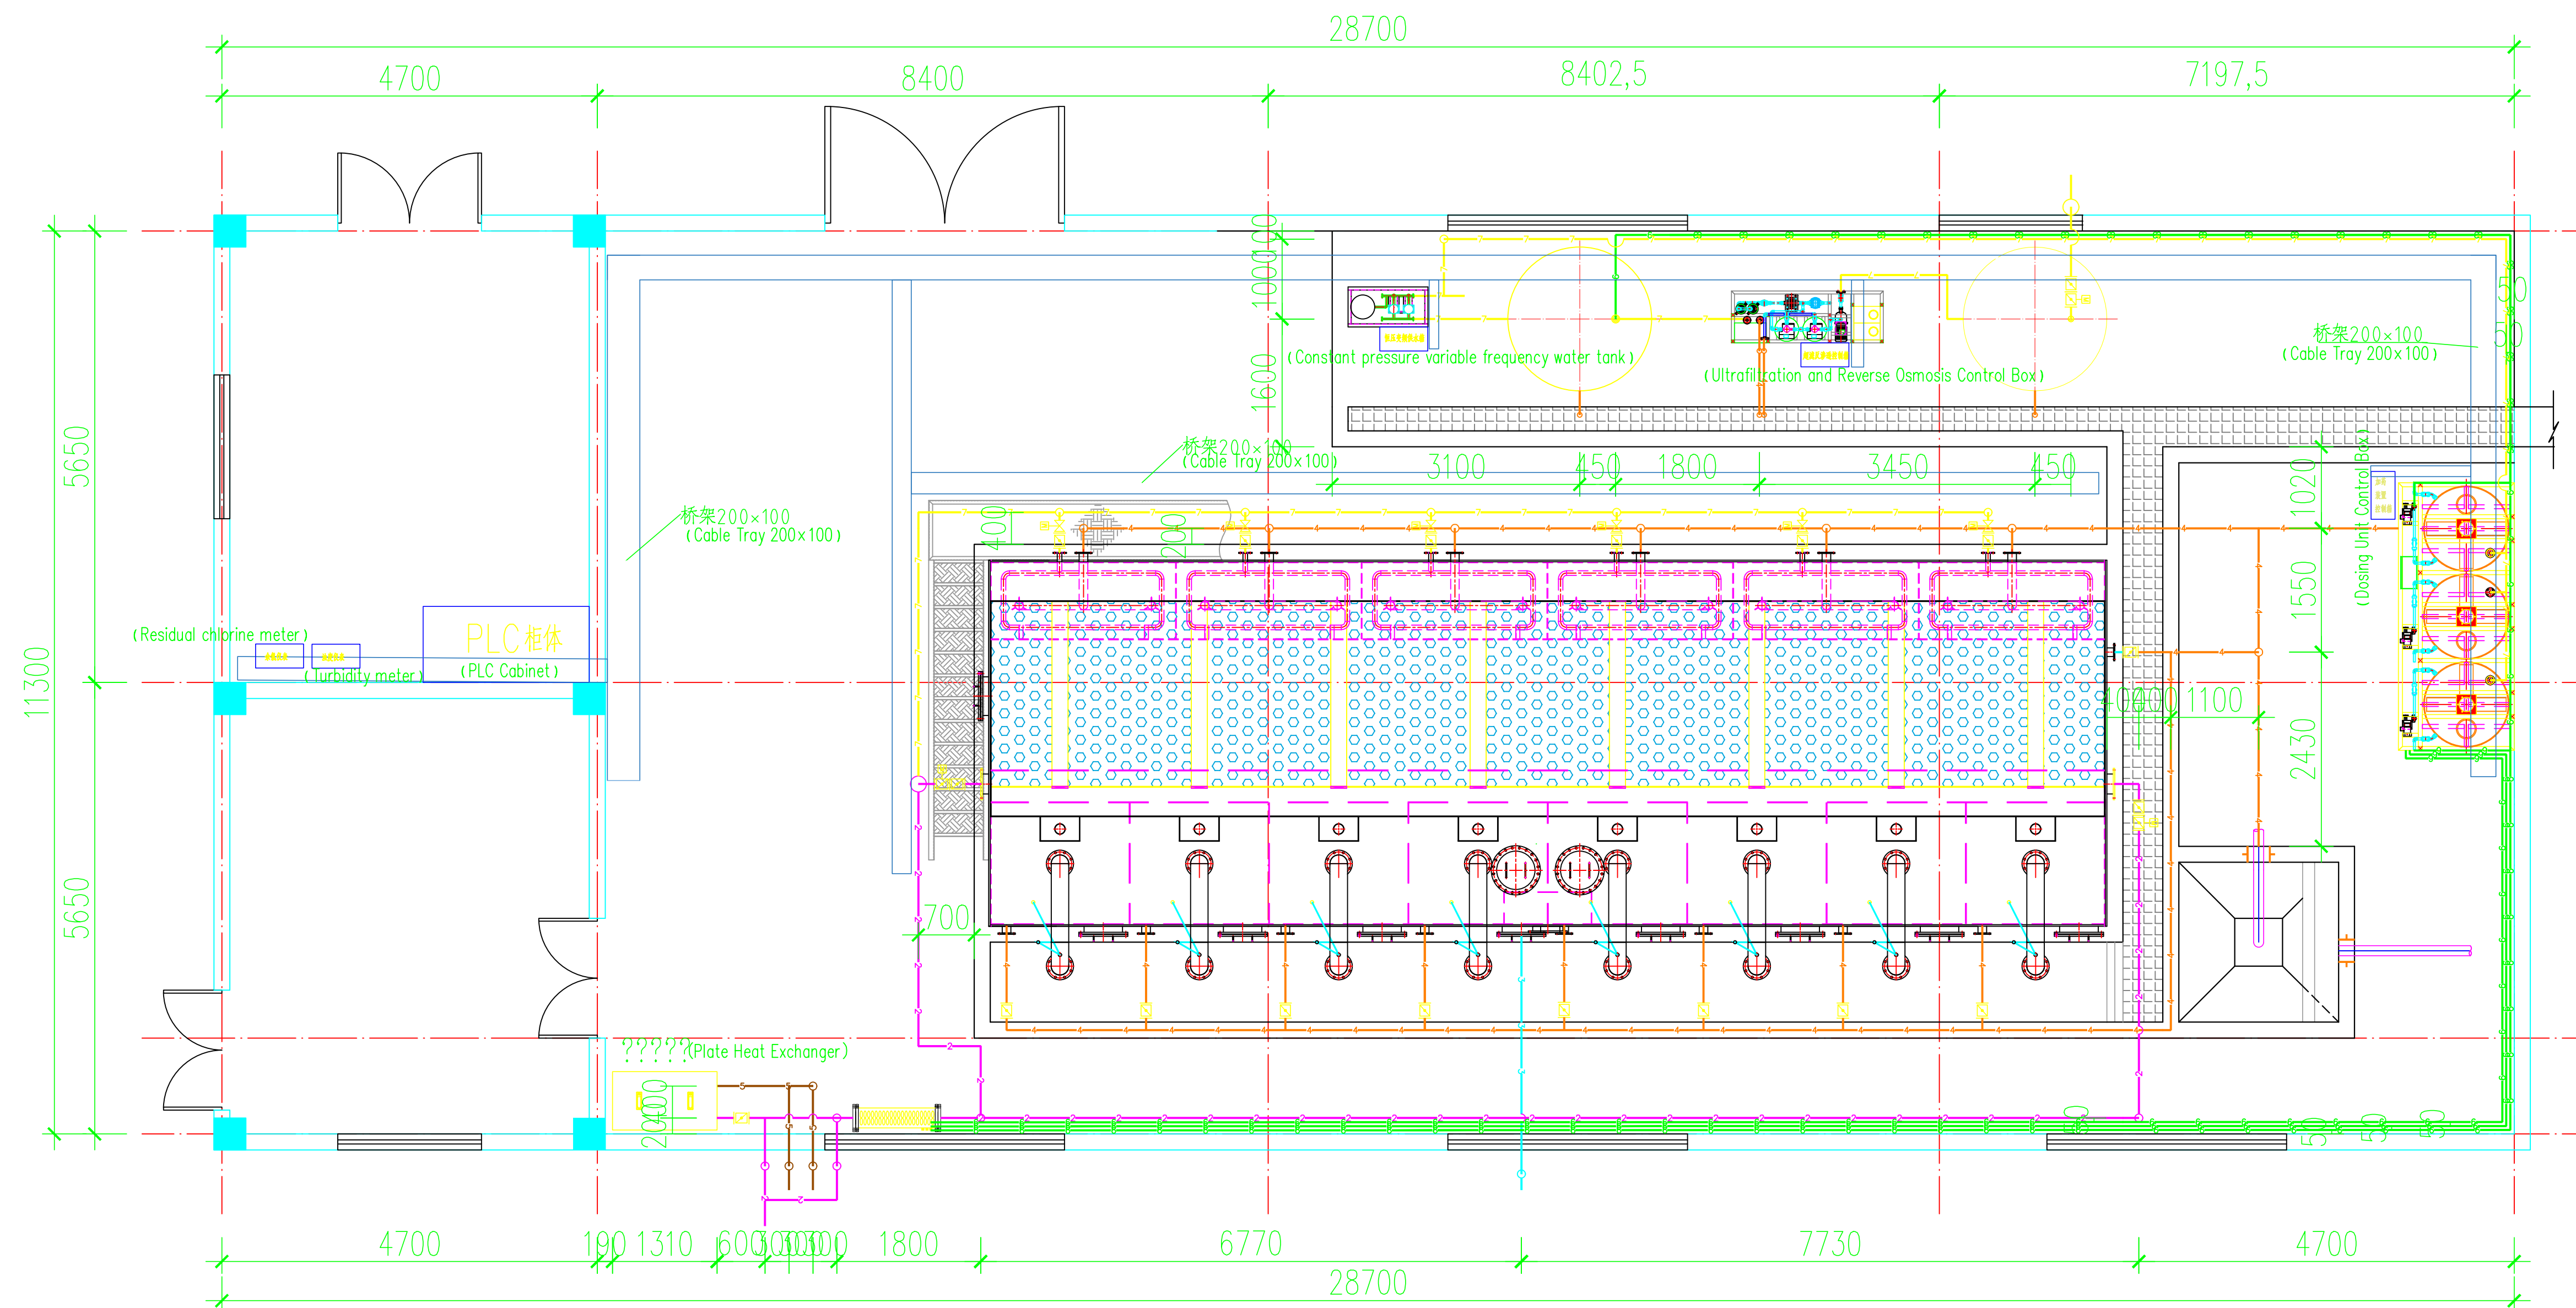

????????????

(Cable Tray & Cabinet Layout Plan of Water Purification Station)

|                                                                                 |     |                       |                                                                                             |                |
|---------------------------------------------------------------------------------|-----|-----------------------|---------------------------------------------------------------------------------------------|----------------|
| 四川盛玖源环境工程有限公司<br>Sichuan shengjiuyuan Environmental Engineering Co., Ltd.       |     | 工程名称<br>PROJECT       | 乌兹别克斯坦年产50万吨硫磺制酸项目<br>Uzbekistan 500,000 Tons/Year Sulfur-Based Sulfuric Acid Plant Project |                |
|                                                                                 |     | 子项名称<br>Sub-item Name | 净水站设备项目<br>Project Water Purification Station Equipment                                     |                |
| 审 定<br>APPROVED                                                                 | 廖洪林 | 工程编号<br>PROJECT NO.   | SJY202602                                                                                   |                |
| 审 核<br>EXAMINED                                                                 | 张山松 | 设计阶段<br>DESIGN STAGE  | 施工图<br>CONSTRUCTION DRAWING                                                                 |                |
| 校 核<br>CHECKED                                                                  | 胡欣雨 | 比 例<br>Ratio          | 1:100                                                                                       |                |
| 设 计<br>DESIGNED                                                                 | 刘 明 | 出图日期<br>DATE          | 2026. 02                                                                                    |                |
| 净水站桥架柜体定位平面布置<br>Cable Tray & Cabinet Layout Plan of Water Purification Station |     |                       | 图纸编号<br>DRAWING NO.                                                                         | SJY-GY-14      |
|                                                                                 |     |                       | 专 业<br>Professional                                                                         | 工 艺<br>Process |