


方案	姓名	签名
工艺		
设备		
电气		
暖通		
给排水		
自控		
建筑		
结构		
总图		
设计		
审核		
批准		

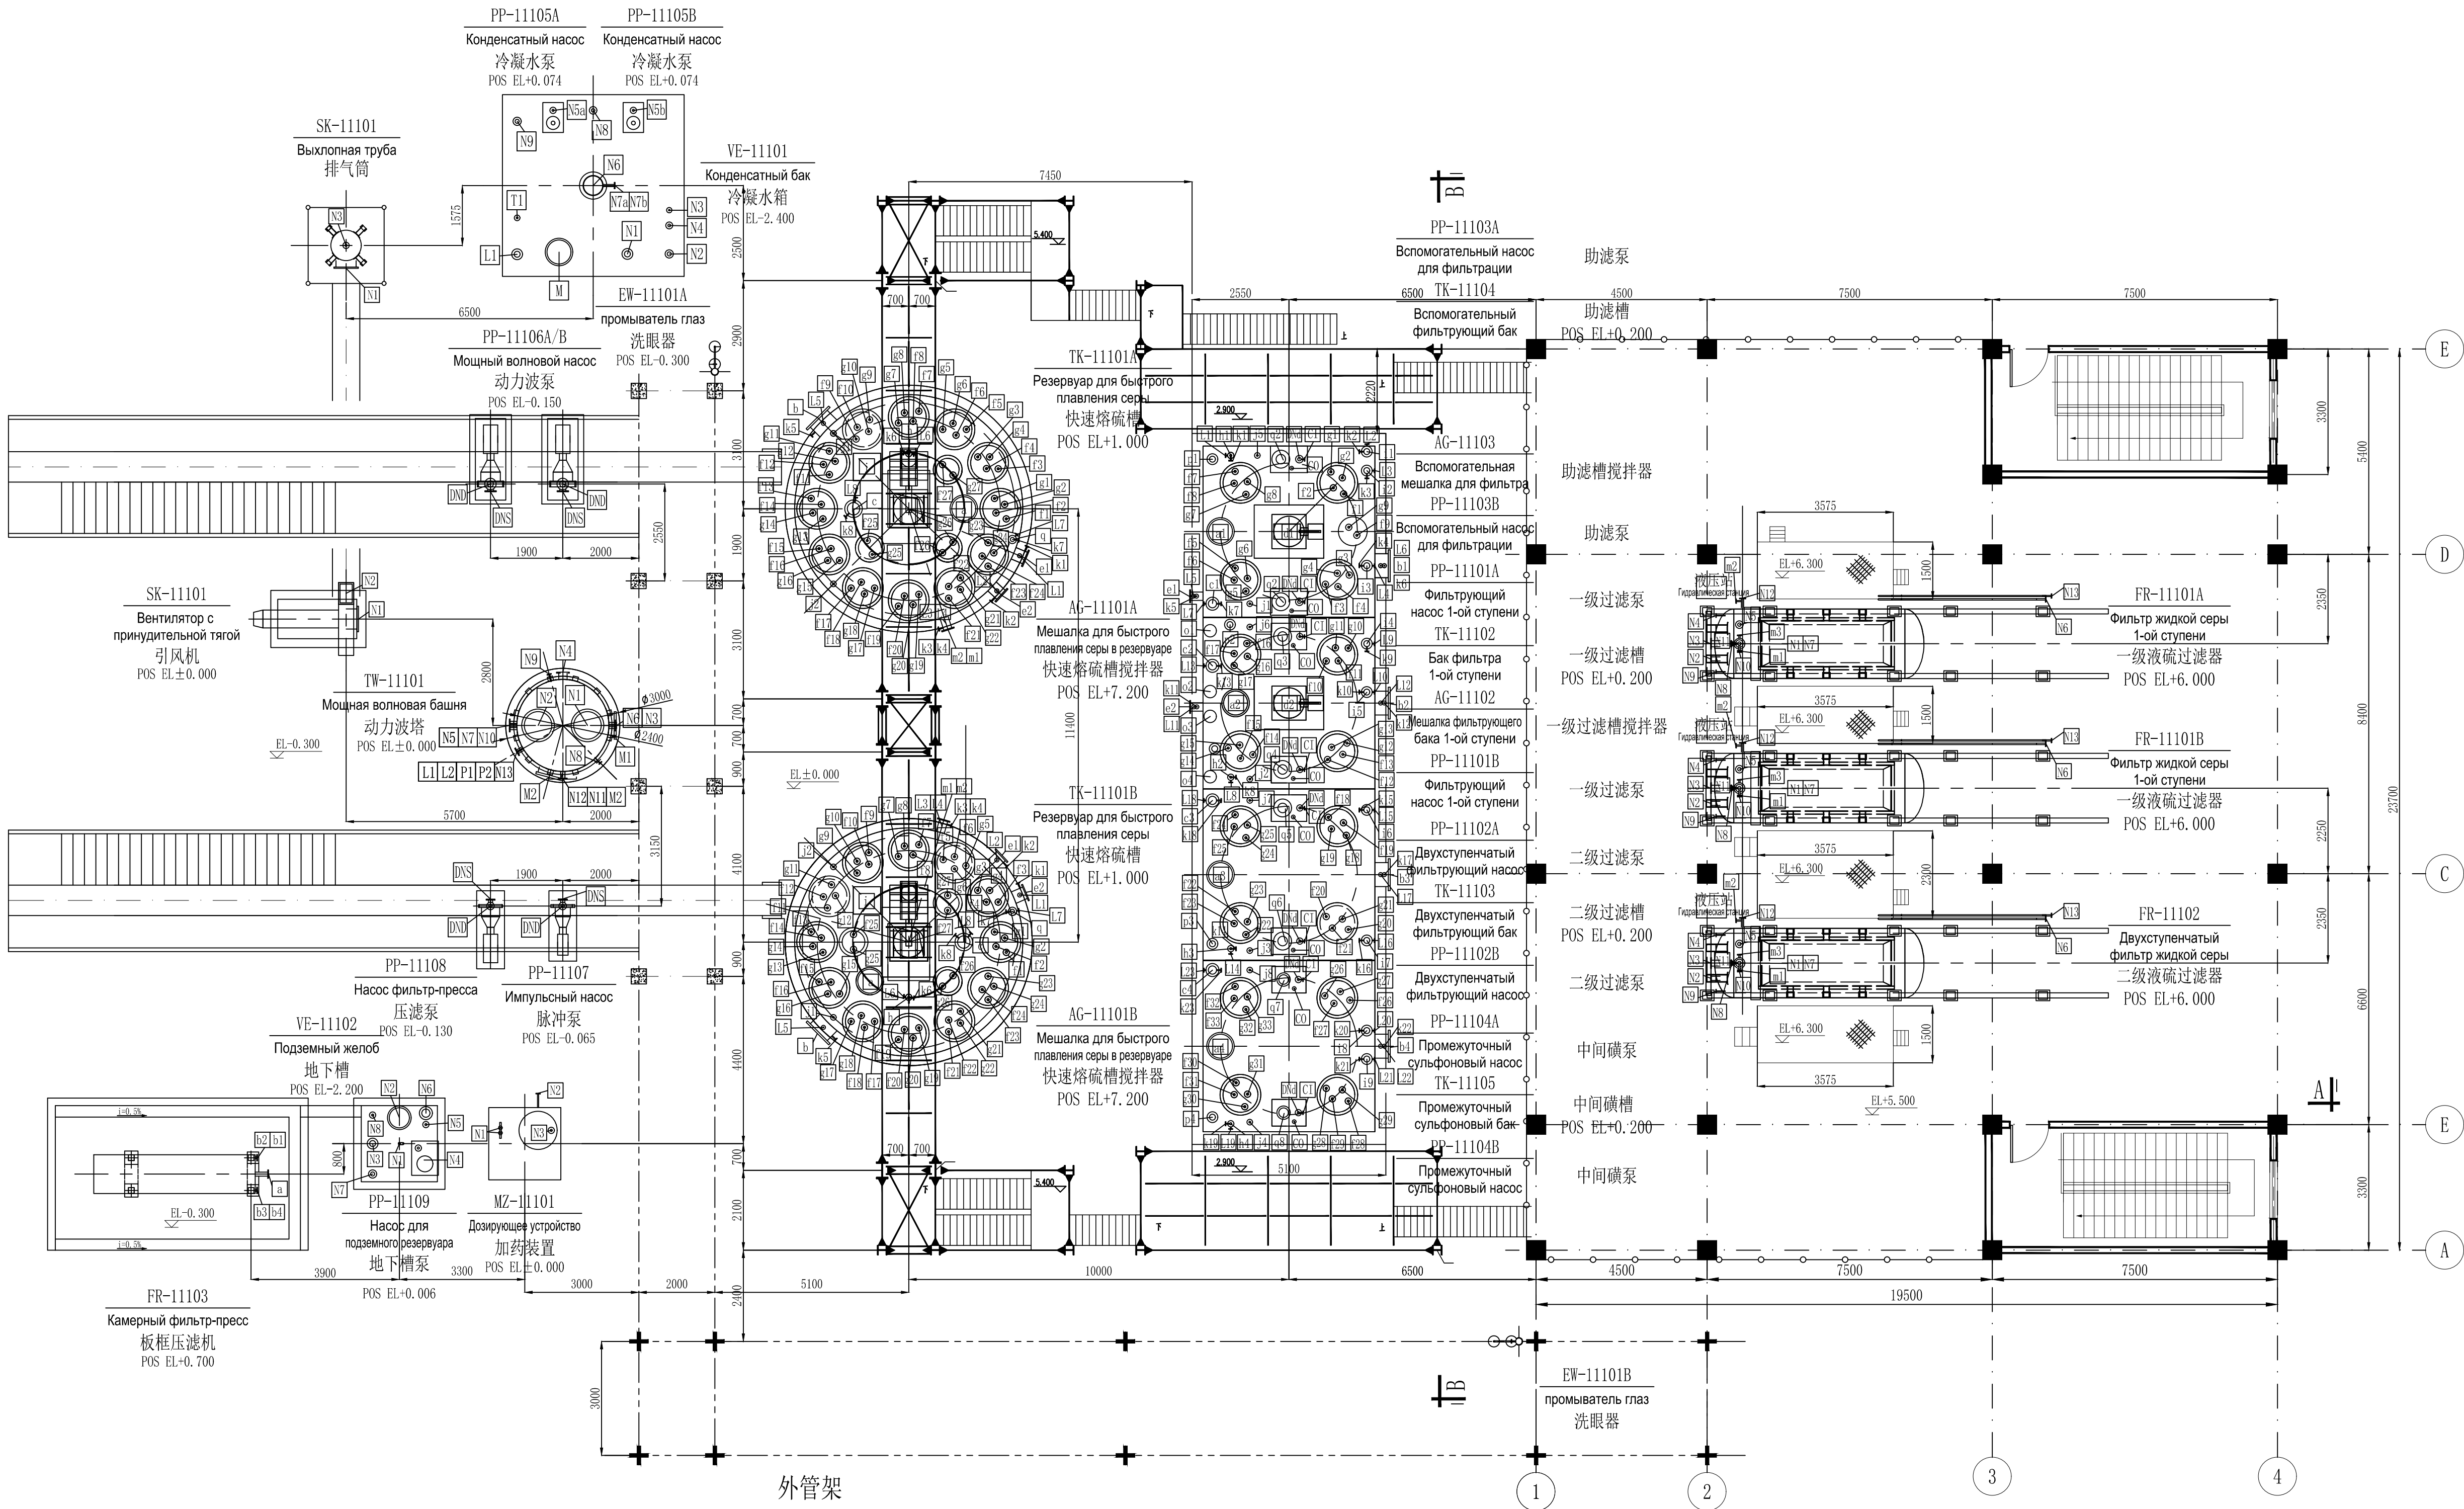

Площадь с
отметкой EL±5.500

EL±5.500平面

版本 Версия		说明 Примечания		日期 Дата
云南化工设计院有限公司 YUNNAN DESIGN INSTITUTE OF CHEMICAL ENGINEERING CO., LTD.		中信建设有限责任公司 CITIC Construction Co., Ltd.		
工程名称 Название проекта		乌兹别克斯坦年产50万吨硫酸项目 Uzbekistan UTMK Chemical LLC Проект завода по производству серной кислоты		工程代号 Код объекта 3147
审定 Утверждение	姓名 Фамилия и имя	签名 Подпись	日期 Дата	设计项目 Проектируемый объект EL±5.500平面 Схема размещения оборудования Площадь с отметкой EL±5.500
审核 Риском.	李海昆	李海昆		设计阶段 Стадия проектирования 施工图 3147-56111-08
校核 Проверка	张斌斌	张斌斌		第 1 页 Лист
设计 Проектирование	董俊	董俊		共 1 页 Листы
专业 Специальность		工艺 Технология	比例 Масштаб	日期 Дата
日期 Дата		2026.05	版次 Версия	