


方案	姓名	签名
工艺	姓名	签名
设备	姓名	签名
暖通	姓名	签名
电气	姓名	签名
给排水	姓名	签名
自控	姓名	签名
消防	姓名	签名
结构	姓名	签名
总图	姓名	签名
设计	姓名	签名
审核	姓名	签名
批准	姓名	签名

修改	
100	


会签	姓名	签名
工艺		
设备		
管道		
自控		
给排水		
电		
暖通		
建筑		
结构		
总图		
设计		
经理		

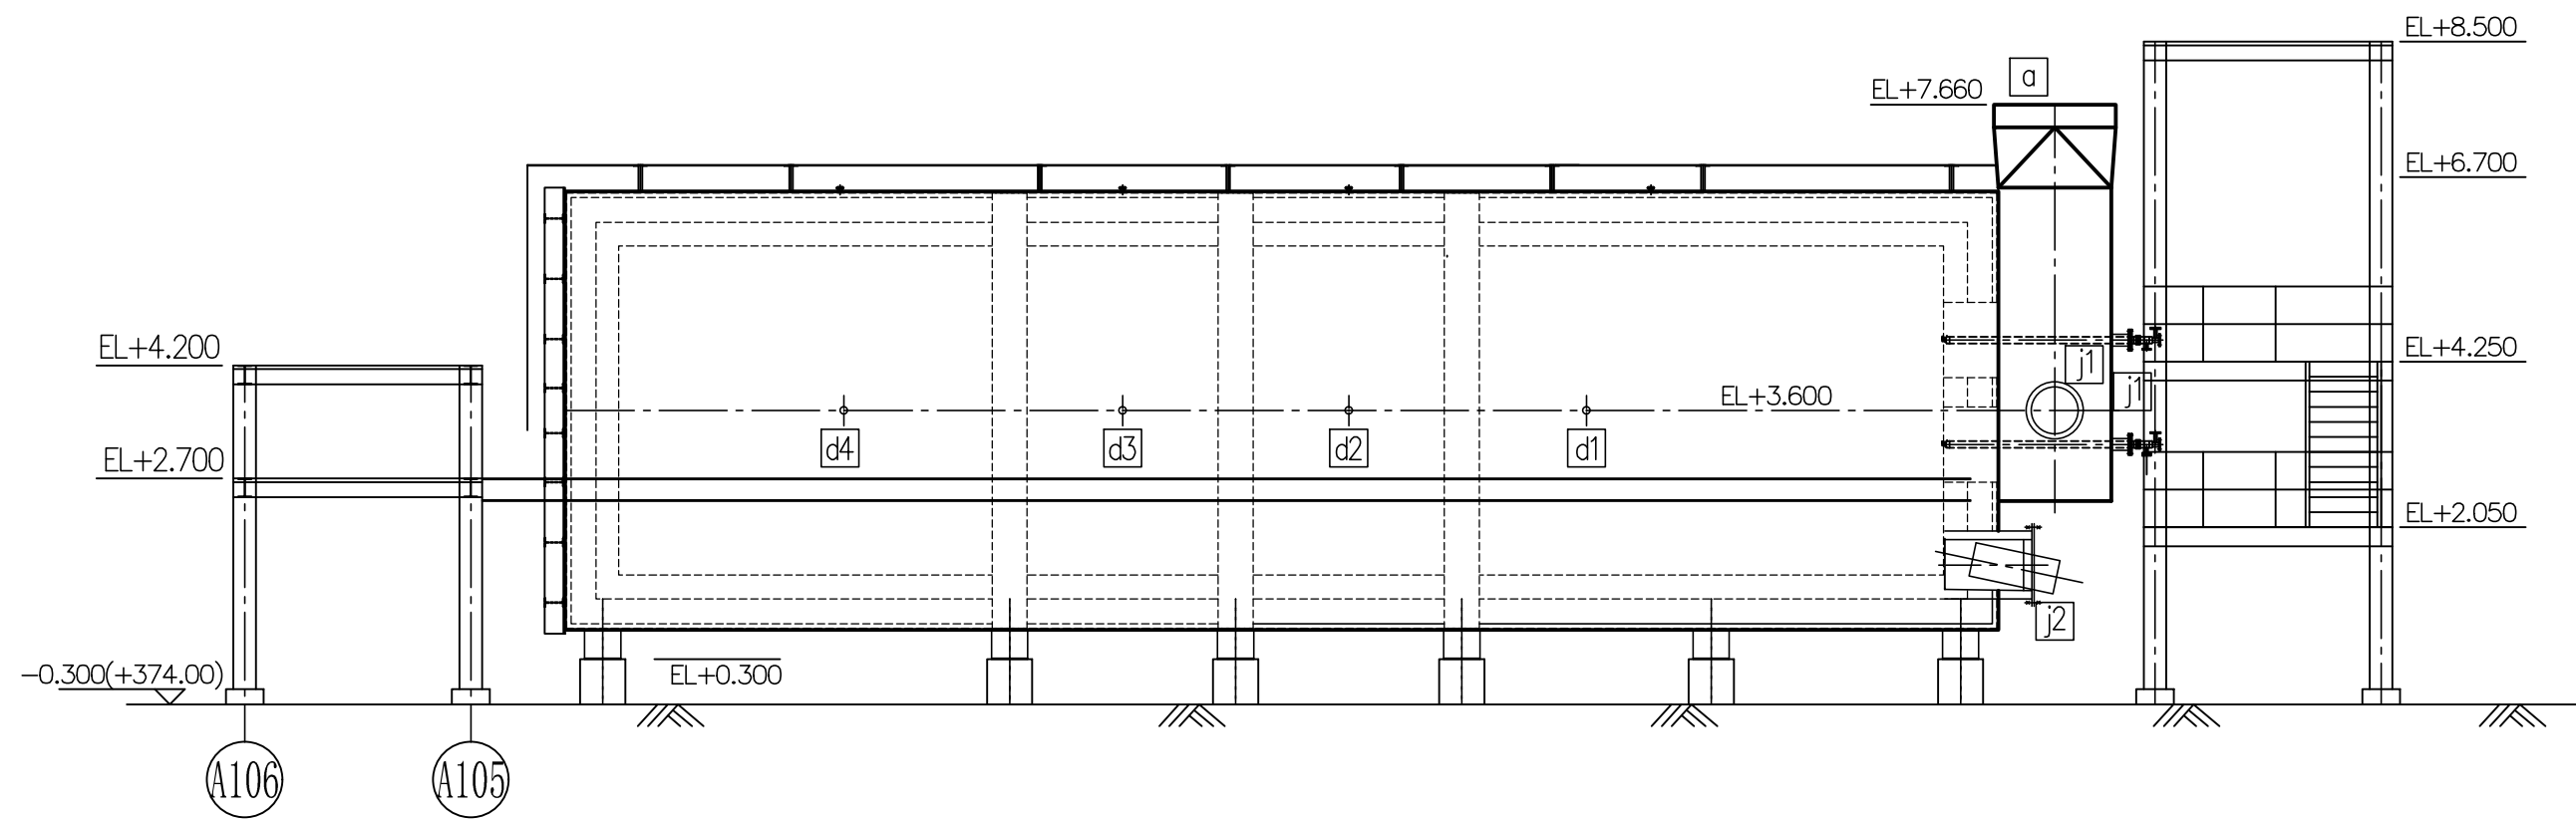

FU-11201
焚硫炉
Печь для сжигания серы

A-A 剖视


Вид в разрезе A-A

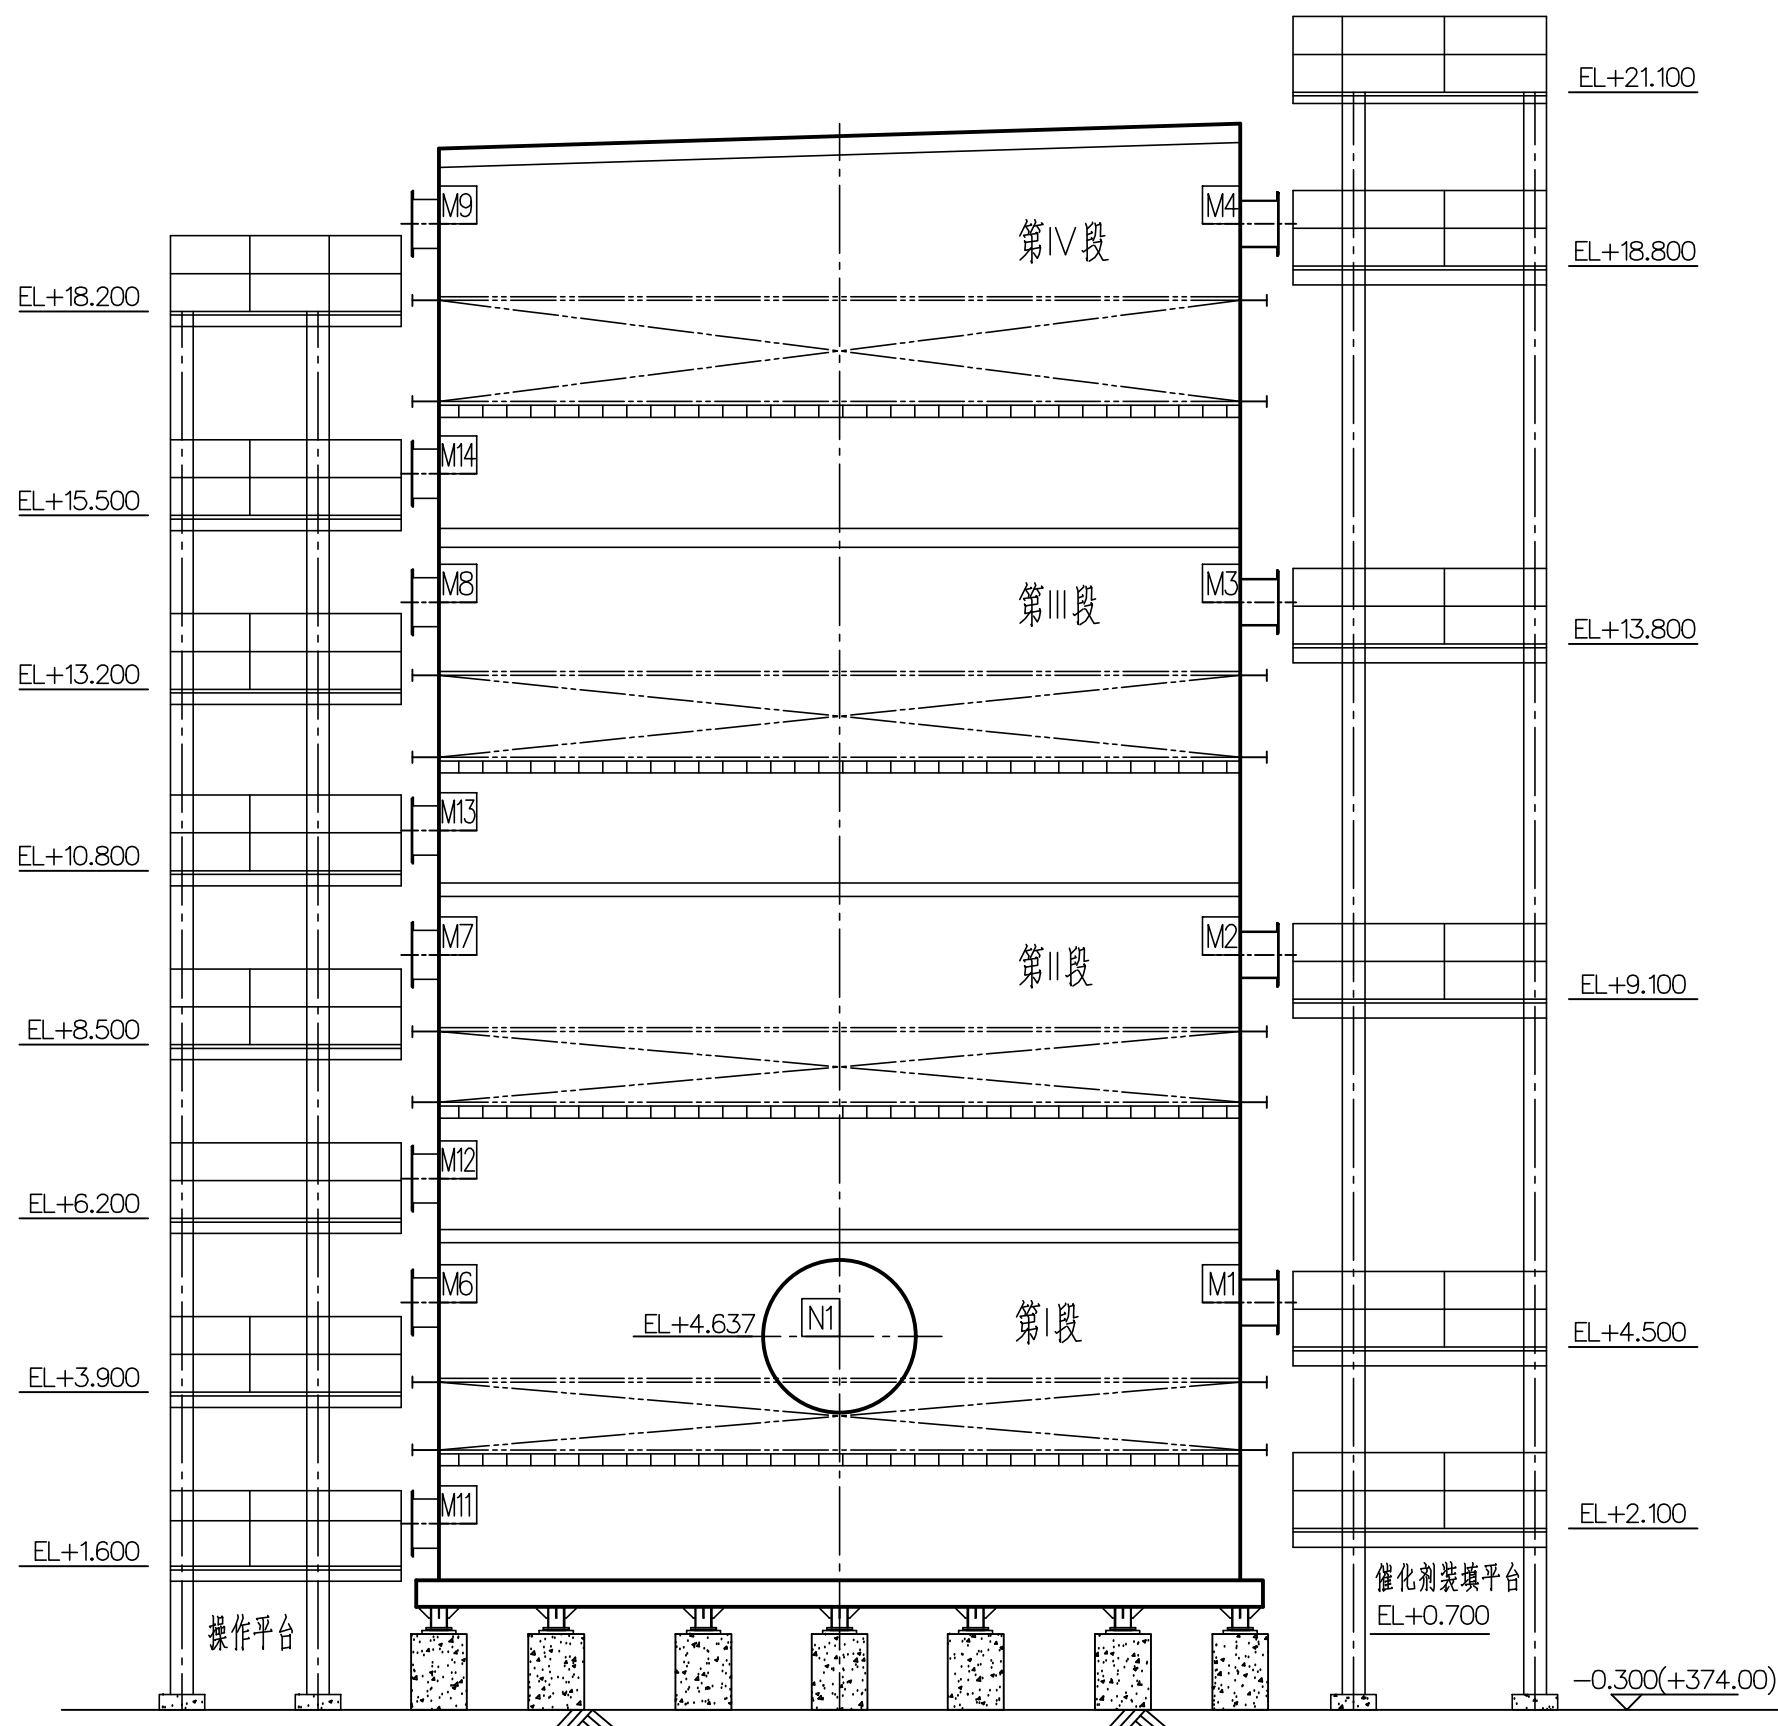

RE-11201
转化器
Конвертер

D-D 剖视


Вид в разрезе D-D

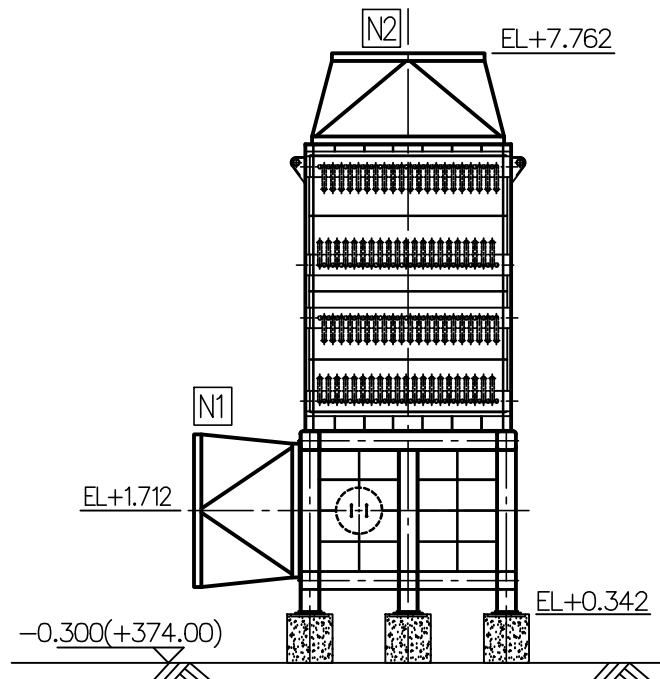

EX-11202
过热蒸汽
Пароперегреватель 1B

E-E 剖视


Вид в разрезе E-E

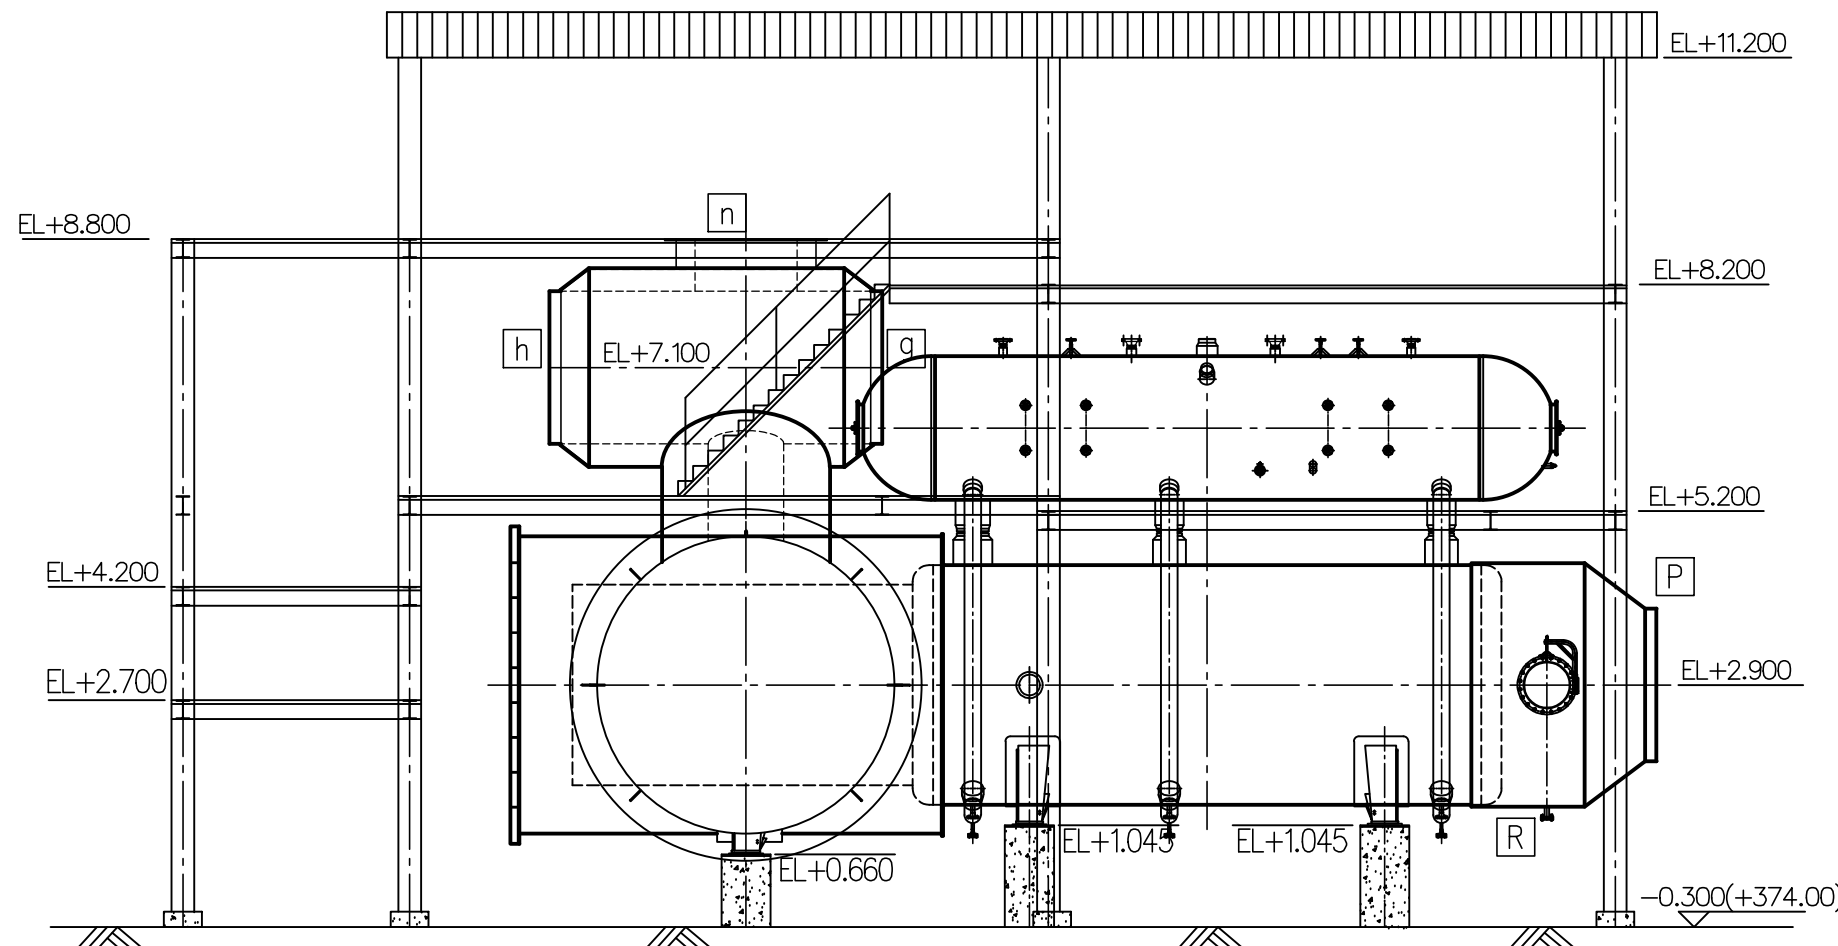

EX-11201
废热锅炉
Утилизационный котёл

B-B 剖视


Вид в разрезе B-B

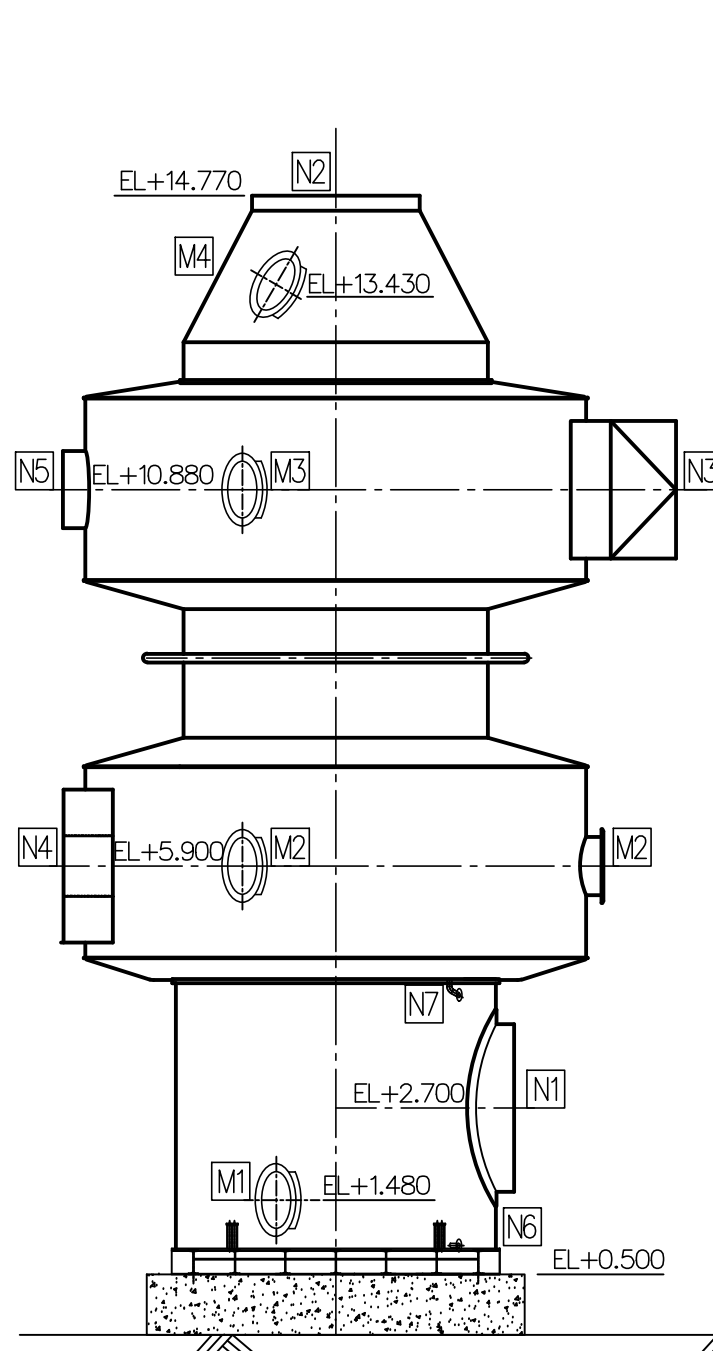


EX-11303
热交换器
Теплообменник
холодных и горячих сред

F-F 剖视

Вид в разрезе F-F

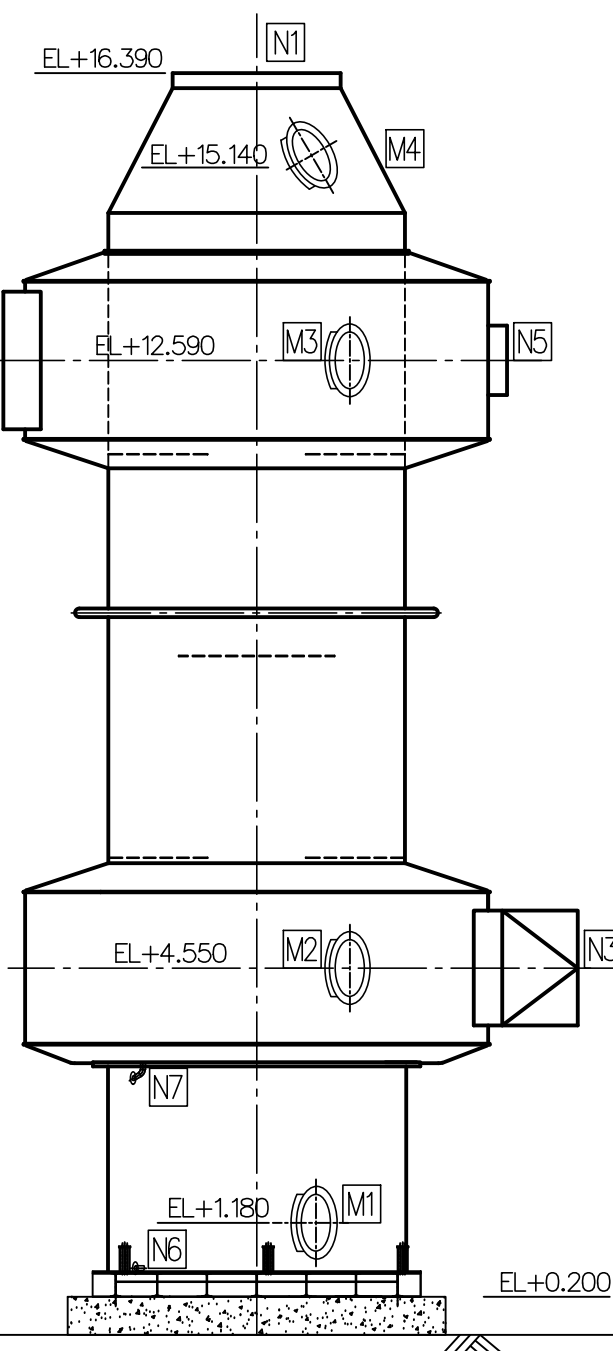


EX-11304
冷热交换器
Теплообменник
холодных и горячих сред

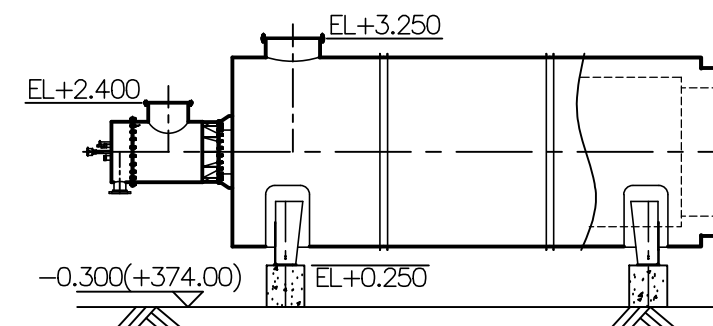

EX-11208
空气预热器
Воздухоподогреватель

C-C 剖视


Вид в разрезе C-C

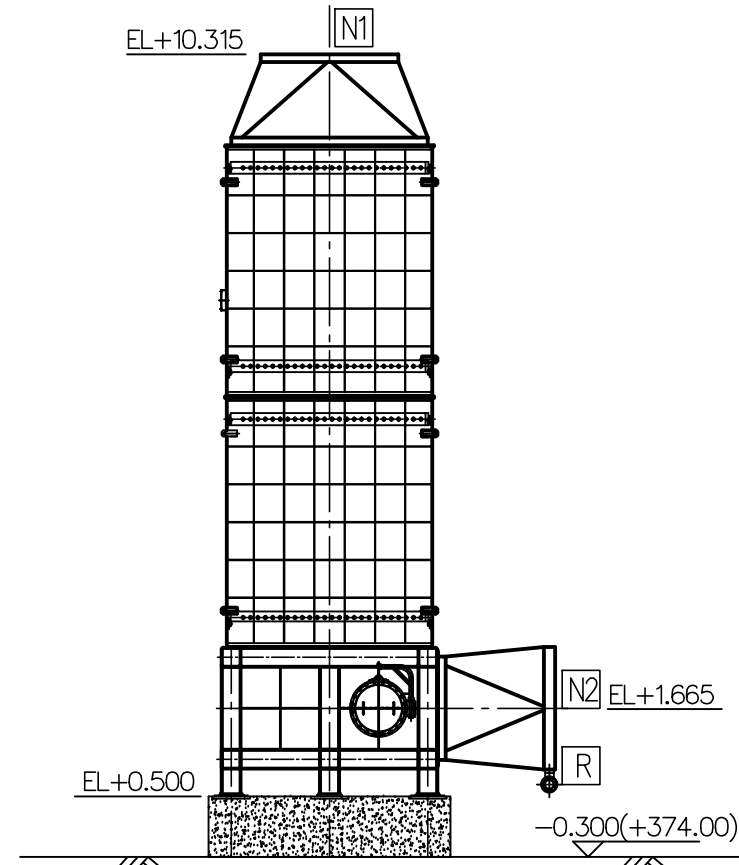

EX-11205
省煤器 3A
Углесберегающий
экономайзер 3A

G-G 剖视

Вид в разрезе G-G

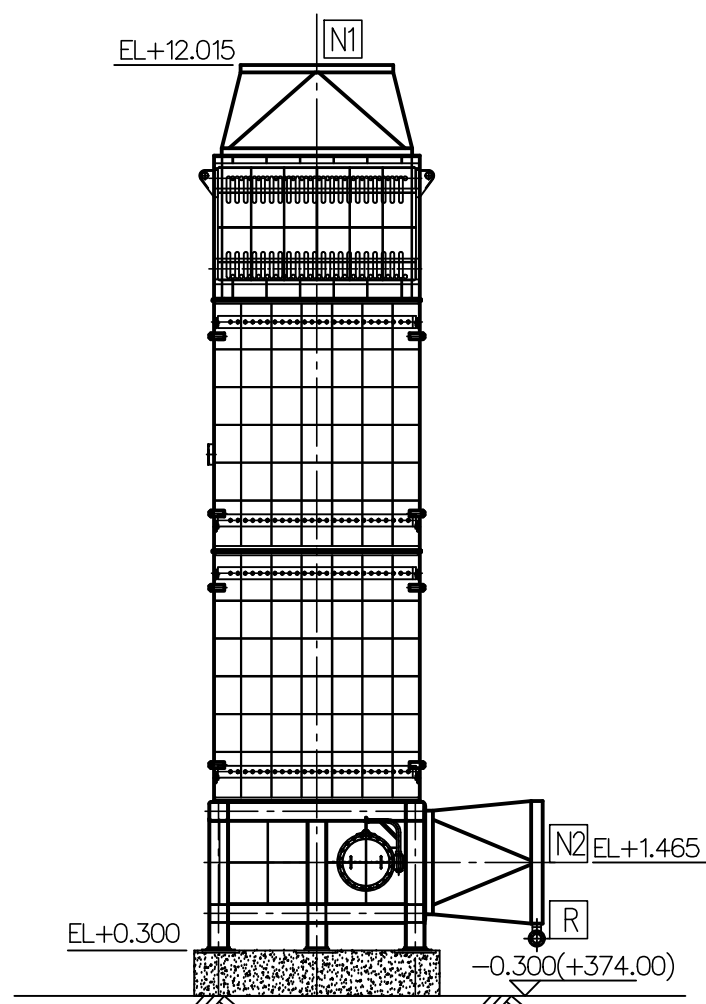

EX-11207
省煤器 4A
Углесберегающий
экономайзер 4A

H-H 剖视

Вид в разрезе H-H

云南省工程勘察设计文件《出图》专用章	
单位名称：云南化工设计院有限公司	
证书编号：53007990	
有效期至：2039年02月14日	
说明：化工石化医药行业甲级；建筑行业《建筑工程》甲级；房屋建筑工程设计甲级（本项为辅助工程、大气污染防治工程、固体废物处理工程、环境工程、给排水工程、暖通工程、电气专业工程、食品及轻工工程）乙级；建筑行业《给水工程、排水工程、城市燃气工程、环境卫生工程》乙级。	
云南省住房和城乡建设厅2025年08月15日颁发	
项目出图编号：4302599044894 项目名称：乌兹别克斯坦年产50万吨硫酸项目	
用途：施工图	

版本 Версия		说明 Примечания		日期 Дата	
云南化工设计院有限公司 YUNNAN DESIGN INSTITUTE OF CHEMICAL ENGINEERING CO., LTD.		中信建设有限责任公司 CITIC Construction Co., Ltd.		工程代号 Мод. объекта 3147	
工程名称 НАЗВАНИЕ ПРОЕКТА		乌兹别克斯坦年产50万吨硫酸项目 Uzbekistan UTMK Chemical LLC Проект завода по производству серной кислоты		设计项目 Проектируемый объект	
姓名 Фамилия и имя		签名 Подпись		日期 Дата	
审核 Рисовал		李海昆 李海昆		设备布置图 A-A~H-H剖视 Схема расположения оборудования Вид в разрезе A-A—H-H	
校核 Проверил		孔四梅 孔四梅		设计阶段 Стадия проектирования	
设计 Проектировал		郑斌斌 郑斌斌		图号 № чертежа	
专业 Специальность		工艺 Технология		比例 Масштаб	
日期 Дата		2026.03		版次 Версия	
第 1 页 Лист		共 1 张 Листы		3147-56112-07	

版权归云南化工设计院有限责任公司所有，未经本公司许可不得转让、复制、泄露给第三方或用于其他目的。

ВСЕ ПРАВА ЗАЩИЩЕНЫ ЮДС. ДАННЫЙ ЧЕРТЕЖ НЕ МОЖЕТ БЫТЬ ПЕРЕУСТУПЛЕН, ПЕРЕДАН, КОПИРОВАН, РАСПРЯТ ТРЕТЬИМ ЛИЦАМ, А ТАКЖЕ ИСПОЛЬЗОВАН ДЛЯ ДРУГИХ ЦЕЛЕЙ БЕЗ РАЗРЕШЕНИЯ ЮДС.