



会签	姓名	签名
工艺		
设备		
起运		
自控		
给排水		
电		
暖通		
建筑		
结构		
总图		
设计		
经理		

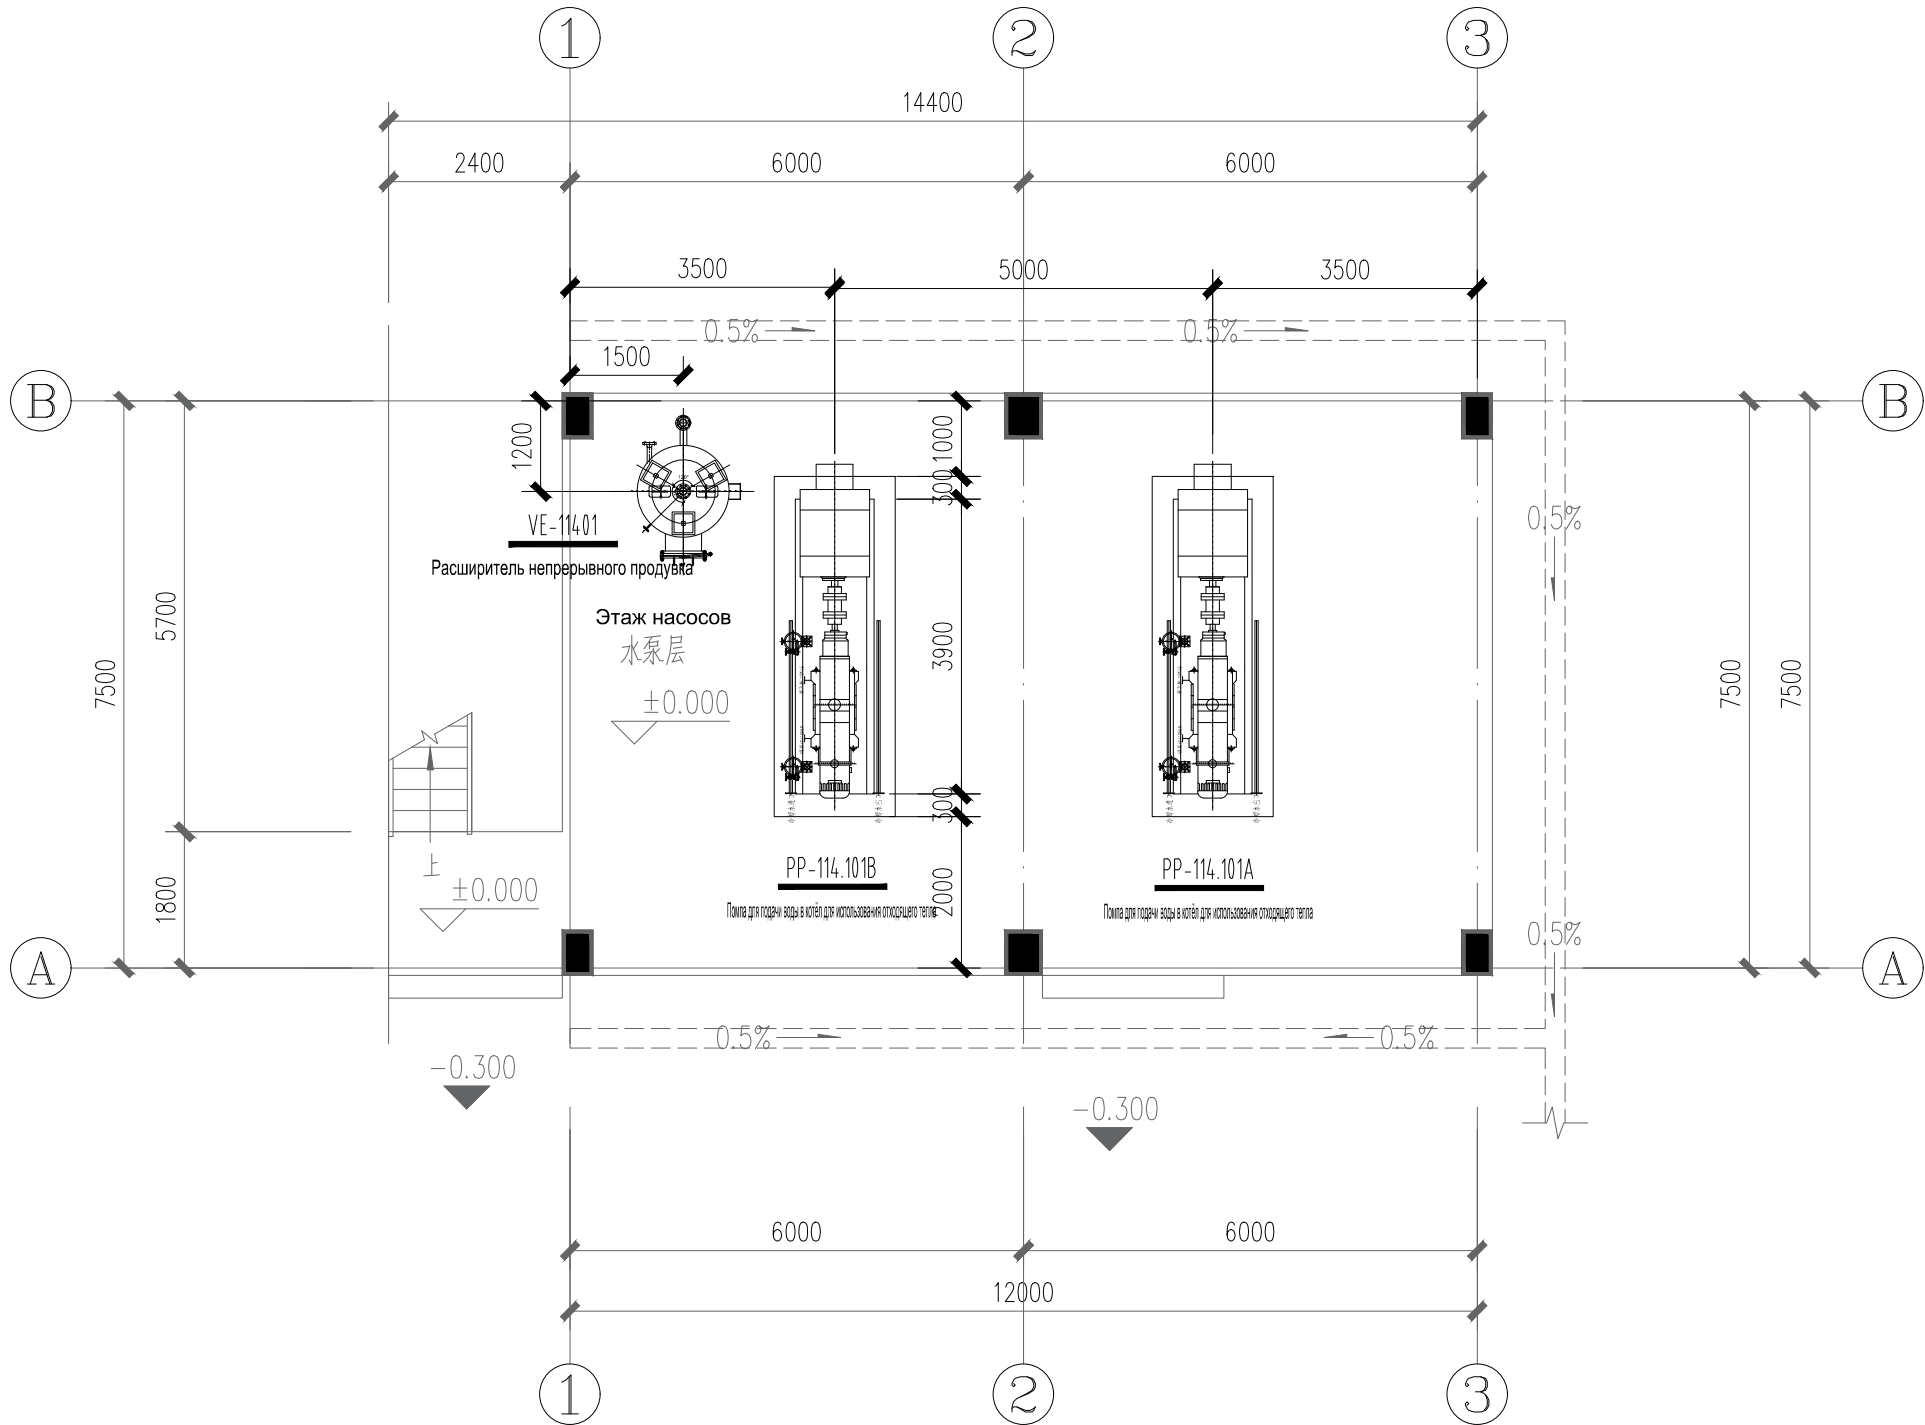

一层设备布置平面图 1:100


План размещения оборудования 1 этажа

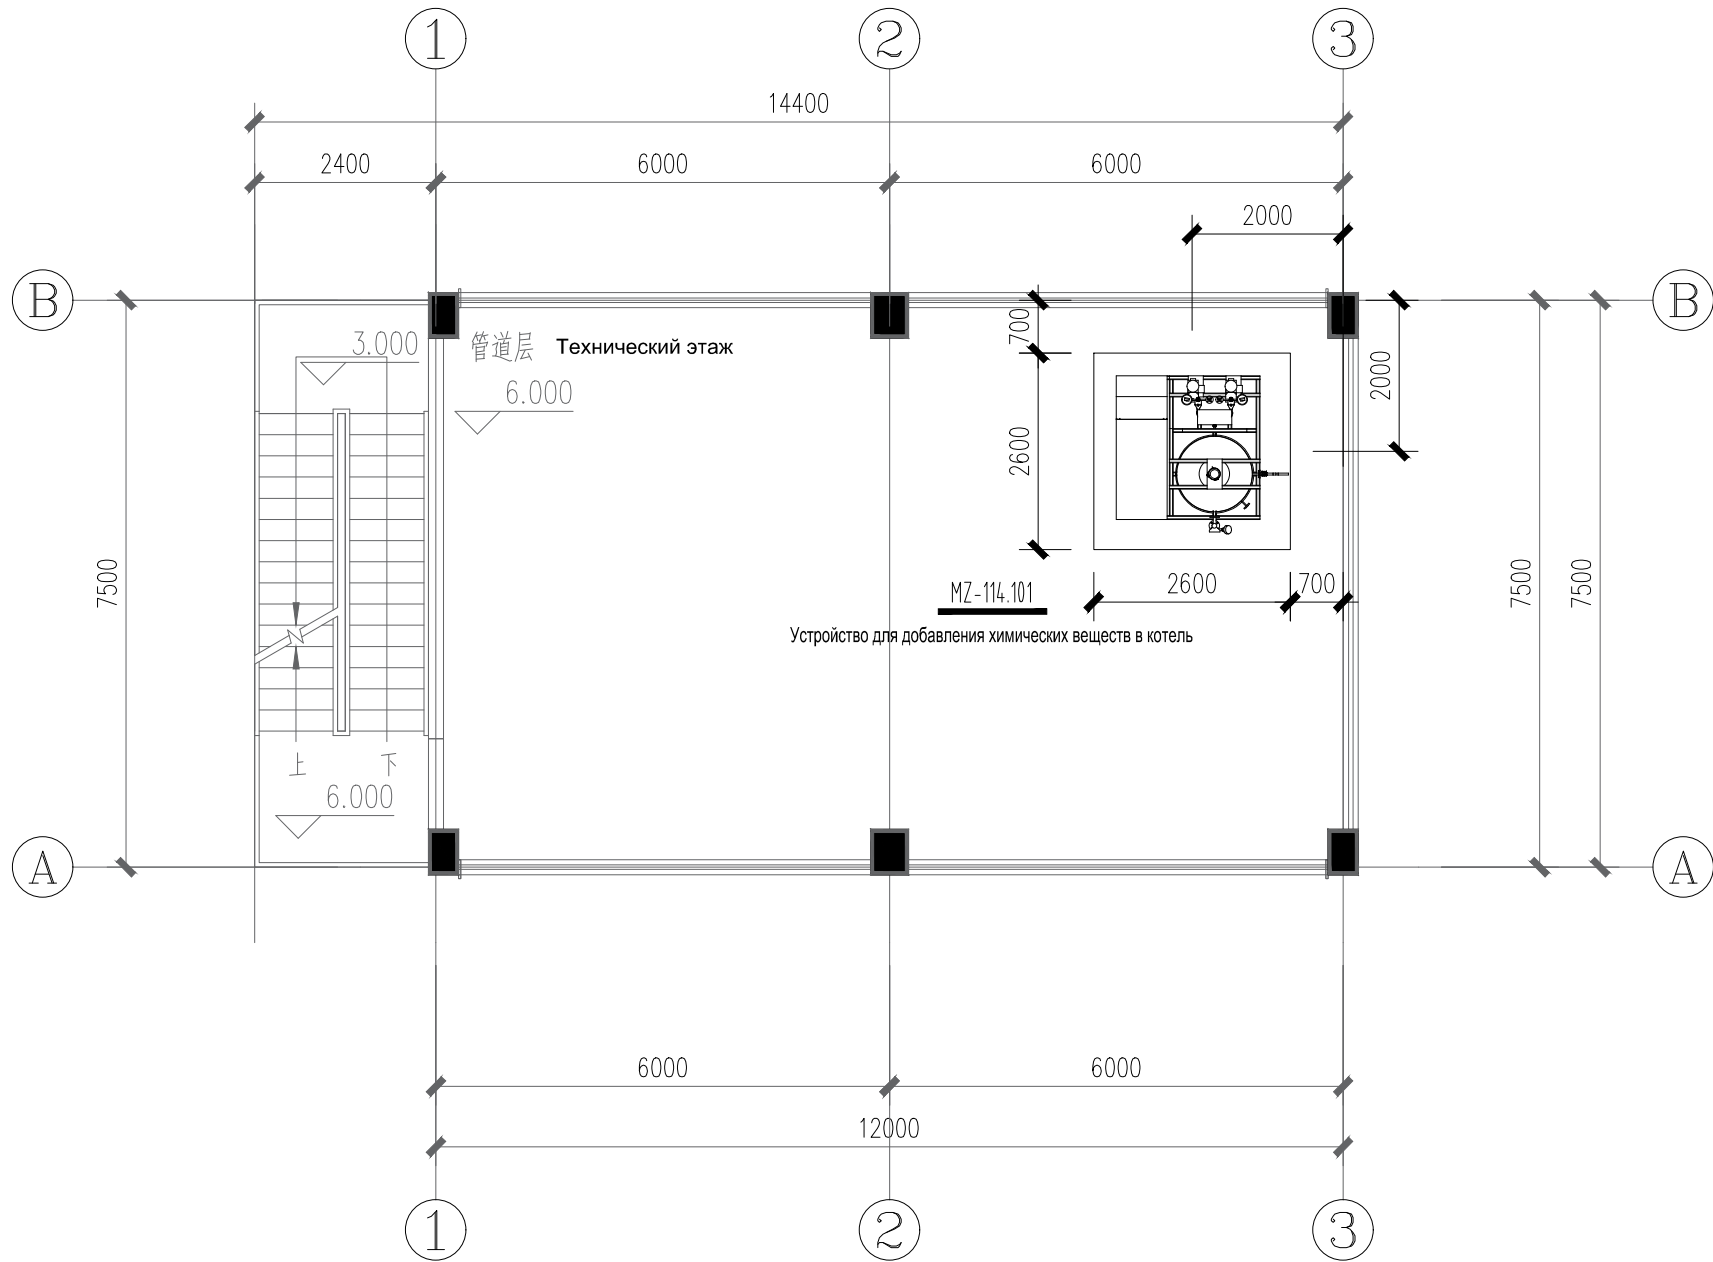

二层设备布置平面图 1:100

修改

Изм.

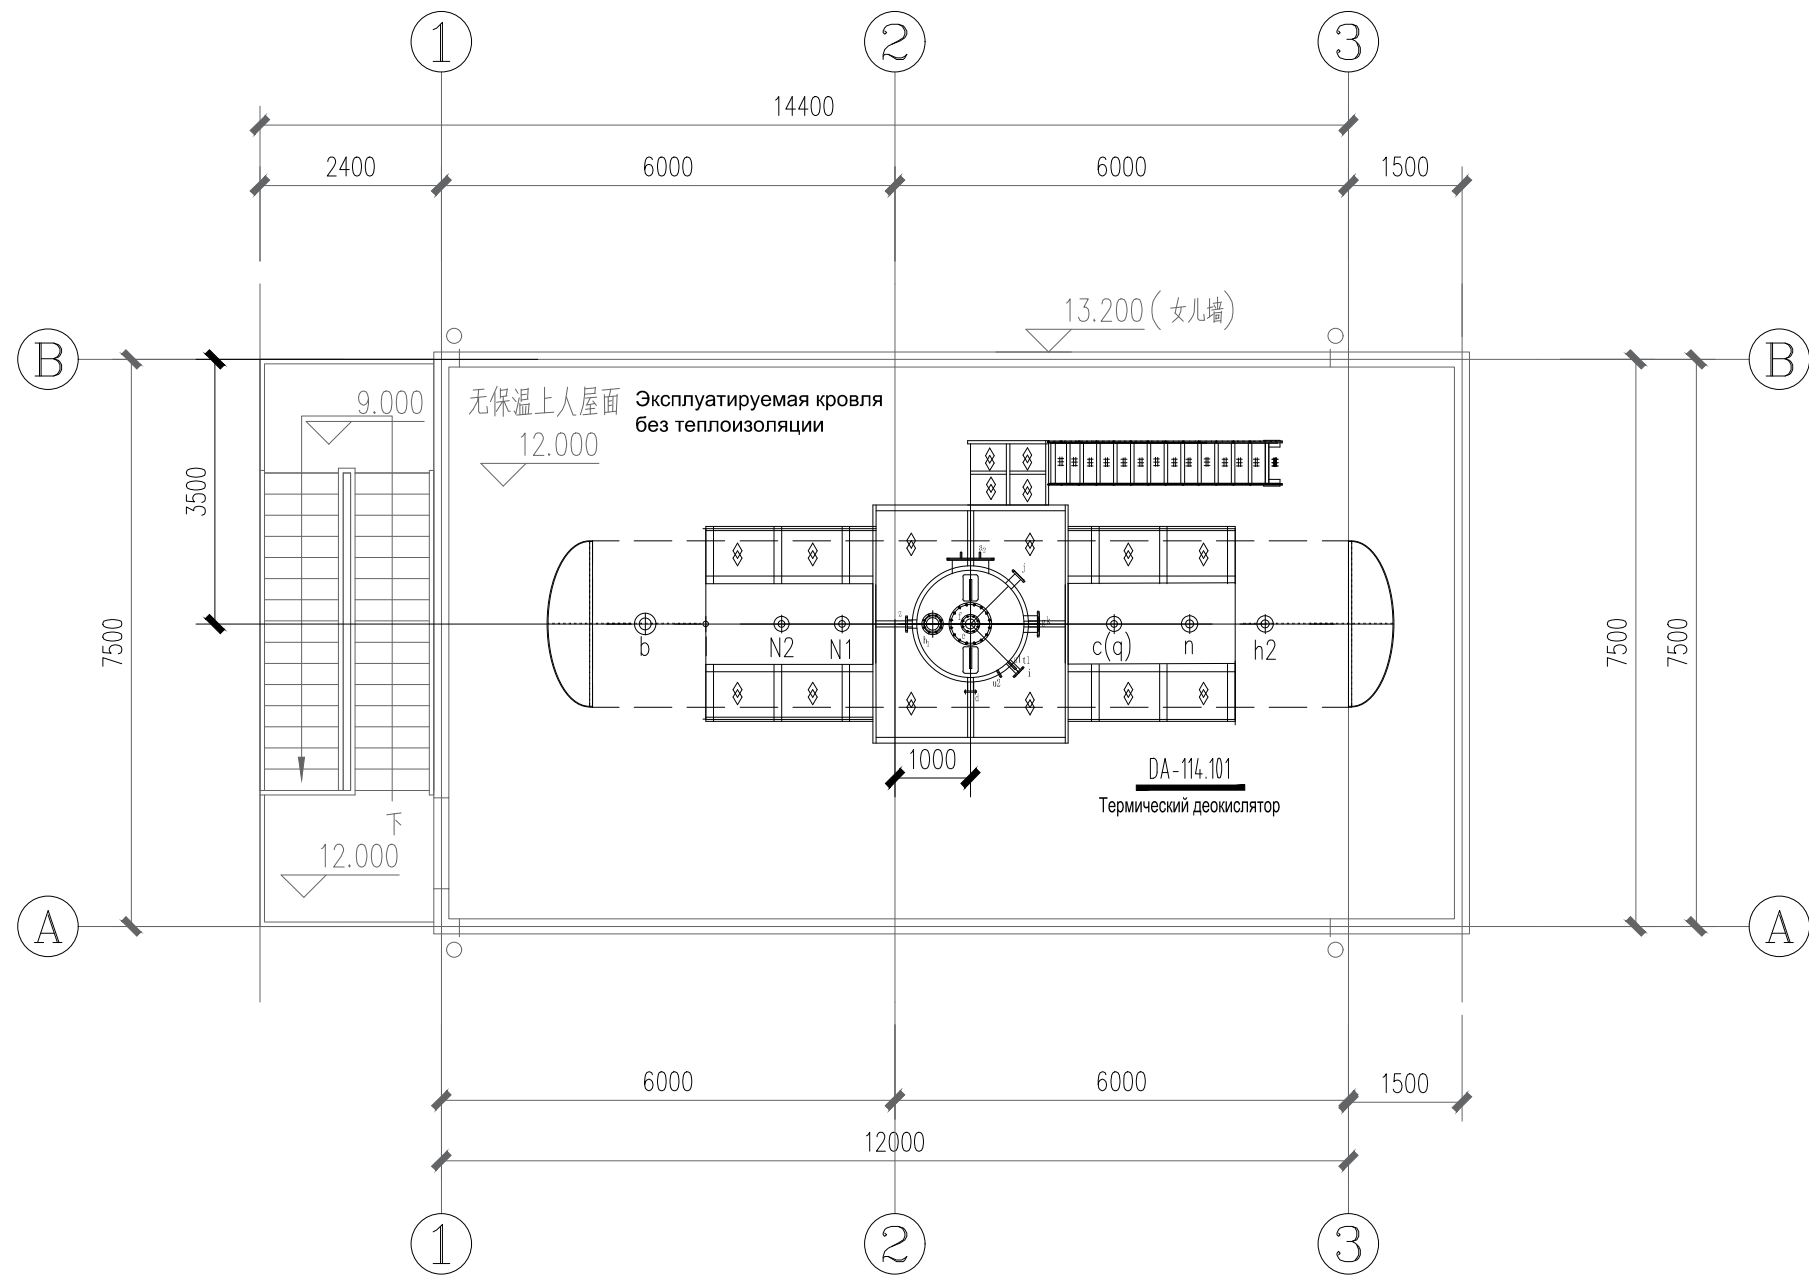

屋顶层设备布置平面图 1:100

План размещения оборудования 3 этажа

构筑物特征表

构筑物层数及层高	构筑物面积	占地面积	总构筑物面积	计容面积	构筑物高度	结构型式	耐火等级	火灾危险性类别
一层: 6.0m	103.34m ²	99.08m ²	206.68m ²	206.68m ²	构筑物高度: 12.30m 室内外高差: 0.30m	钢筋混凝土框架结构	二级	戊类
二层: 6.0m	103.34m ²							

Характеристики сооружений

Этажность и высота этажей сооружения	Площадь застройки	Площадь застройки	Расчётная площадь застройки	Высота здания	Конструктивная схема	Класс огнестойкости	Категория пожарной опасности
1 этаж: 6,0 м	103,34	99,08	206,68	Высота здания: 12,30 м разница высот между внутренней и внешней площадью: 0,30 м	Каркасная конструкция из железобетона	Второй уровень	Категория В
2 этаж: 6,0 м	103,34						



云南省工程勘察设计文件（出图）专用章

单位名称: 云南化工设计院有限公司

证书编号: 5300790

有效期至: 2030年02月14日

资质: 化工石化医药行业甲种; 建筑行业(建筑工程)甲种; 环境工程设计专项(水污染防治工程、大气污染防治工程、固体废物处理处置工程)甲种; 轻纺行业(日化及塑料工程、食品发酵工程)乙种; 市政行业(给水工程、排水工程、城镇燃气工程、环境卫生工程)乙种;

云南省住房和城乡建设厅2025年08月15日核发

项目出图章编号: 4202590044894 项目名称: 乌兹别克斯坦年产50万吨硫酸制酸项目

用途: 施工图



版次	说明	日期
Версия	Примечания	Дата
云南化工设计院有限公司	中信建设有限责任公司	
YUNNAN DESIGN INSTITUTE OF CHEMICAL ENGINEERING CO., LTD.	CITIC Construction Co., Ltd.	
工程名称	乌兹别克斯坦年产50万吨硫酸制酸项目	工程代号
НАЗВАНИЕ ПРОЕКТА	Uzbekistan UTMK Chemical LLC Проект завода по производству серной кислоты	Код объекта
3147		
姓名	签名	日期
Фамилия и имя	Подпись	Дата
审定	审核	日期
Утверждение	Рассм.	2026. 4. 20
校核	陈亮	2026. 4. 20
检查	田雨薇	2026. 4. 20
设计	田雨薇	2026. 4. 20
Проектирование		
设备布置平面图	施工图	
План размещения оборудования	Базовый проект	
设计项目	余热回收工序 - 除氧水站	
Проектируемый объект	станция деаэрированной воды	
设计阶段	施工图	
Стадия проектирования	Базовый проект	
图号	3147-5R114. 1-04	
№ чертёжа		
专业	热工	
Специальность	теплотехника	
日期	2026. 4	
比例	1:100	
Масштаб		
版次	第 1 张	
Версия	Лист	
共 1 张		
Листы		

版权归云南化工设计院有限责任公司所有, 未经本公司许可不得转让、复制、泄露给第三方或用于其他目的

ВСЕ ПРАВА ЗАЩИЩЕНЫ ЮДИС. ДАННЫЙ ЧЕРТЕЖ НЕ МОЖЕТ БЫТЬ ПЕРЕУСТУПЛЕН, ПЕРЕДАН, СКОПИРОВАН, РАСКРЫТ ТРЕТЬИМ ЛИЦАМ, А ТАКЖЕ ИСПОЛЬЗОВАН ДЛЯ ДРУГИХ ЦЕЛЕЙ БЕЗ РАЗРЕШЕНИЯ ЮДИС.