

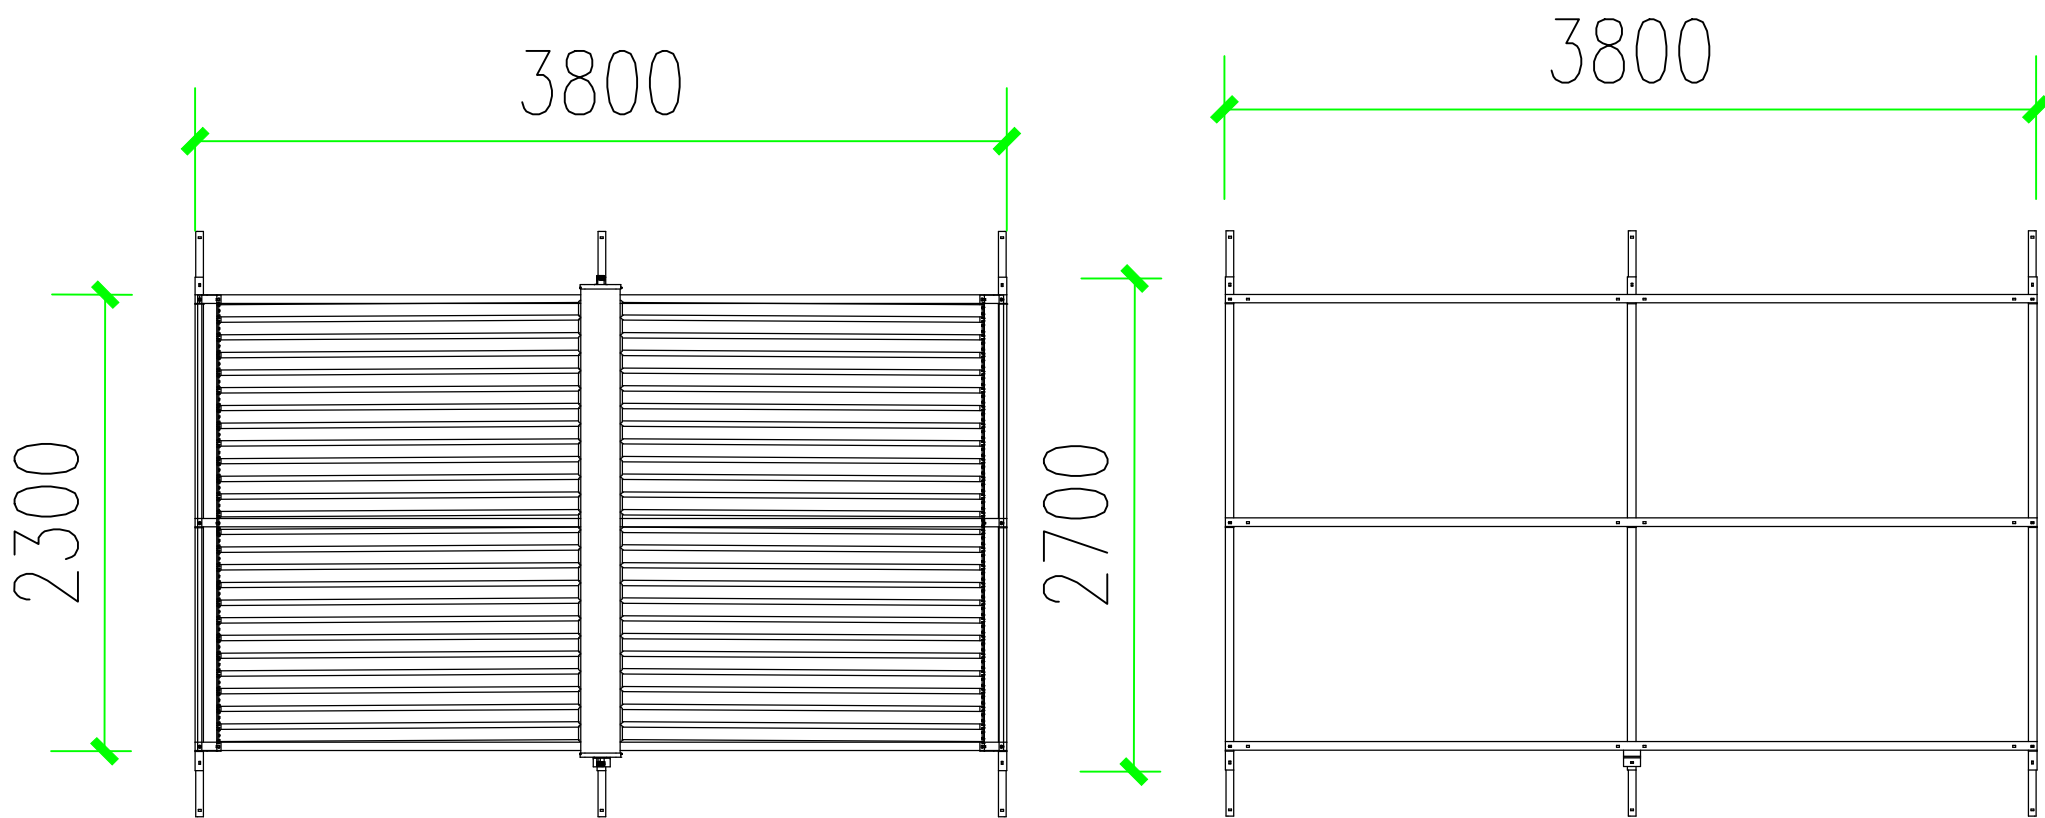


会签	姓名	签名
工艺		
设备		
起运		
自控		
给排水		
电		
热暖		
建筑		
结构		
总图		
设计		
经理		

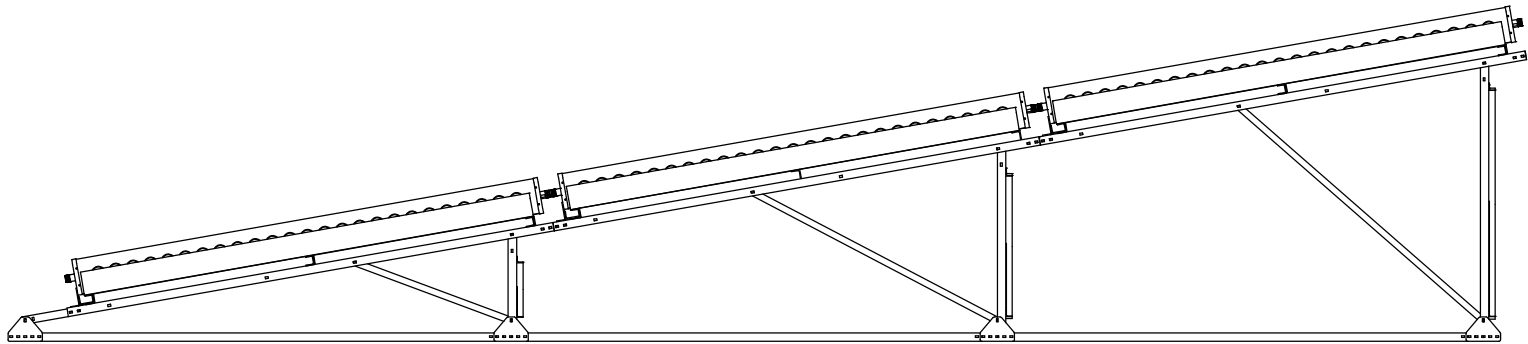


版次 ???????		说 明 ???????????		日期 ????	
 云南化工设计院有限公司 YUNNAN DESIGN INSTITUTE OF CHEMICAL ENGINEERING CO.,LTD.		 中信建设有限责任公司 CITIC Construction Co.,Ltd.			
工程名称 ??????? ?????		Uzbekistan UTMK Chemical LLC ?????? ?????? ?? ?????????????? ?????? ???????			工程代号 ??? ??????
					3147
	姓 名 ??????? ? ??	签 名 ????????	日 期 ????	设计项目 ???????????? ???? 综合楼 Администрация-бухгалтерия	
审 定 ?????????????				设计阶段 ???? ?????????????	
审 核 ?????	张 耕 Zhang Gong		2025. 12. 18	图 号 № ?????	
校 核 ??????	杨 群 Yang Qun		2025. 12. 18	专 业 ????????	第 2 张 ????
设 计 ????????????	陈俊羽 Chen Junyu		2025. 12. 18	给排水 Водосток	共 2 张 ????
				日期 ????	版 次 ????
				2025. 12	比 例 ????


修改 ???	

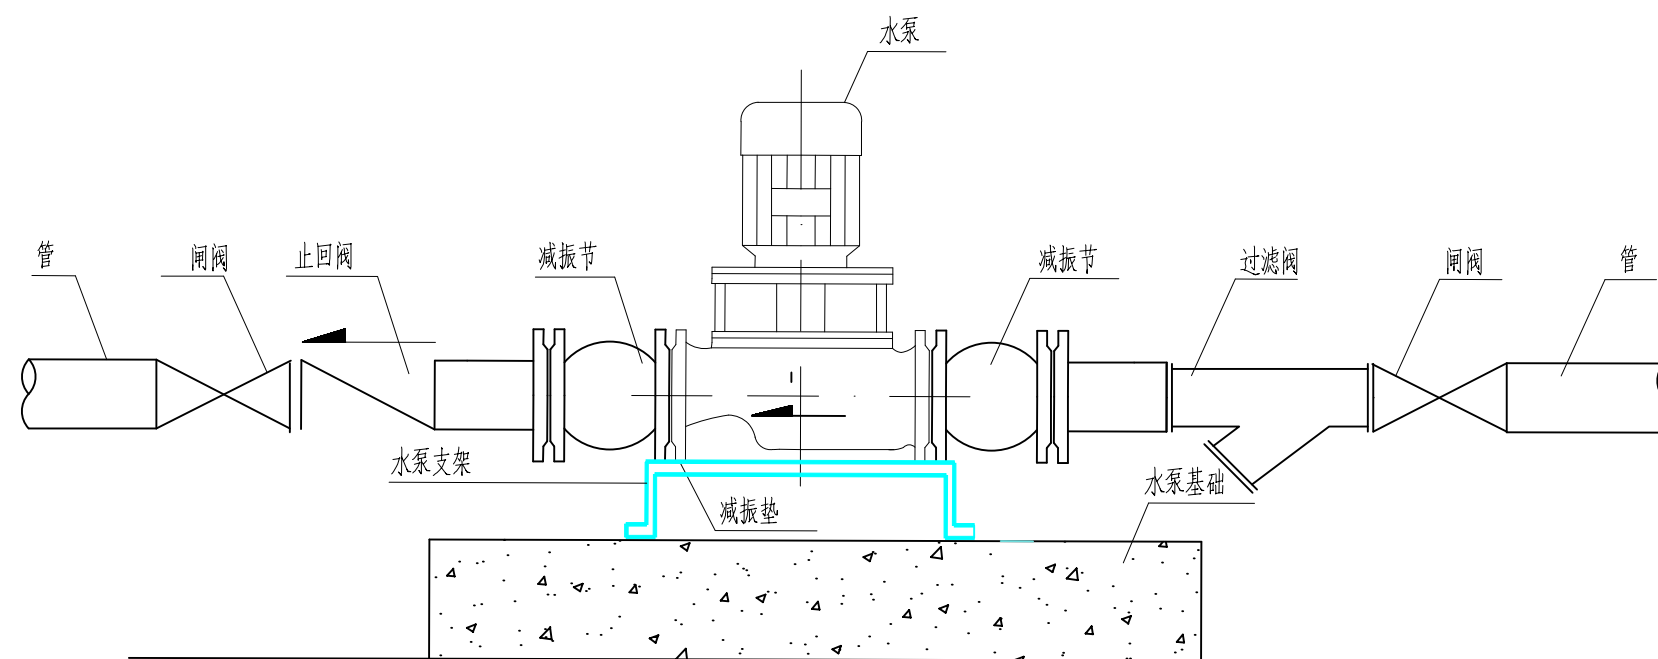


水泵安装大样图

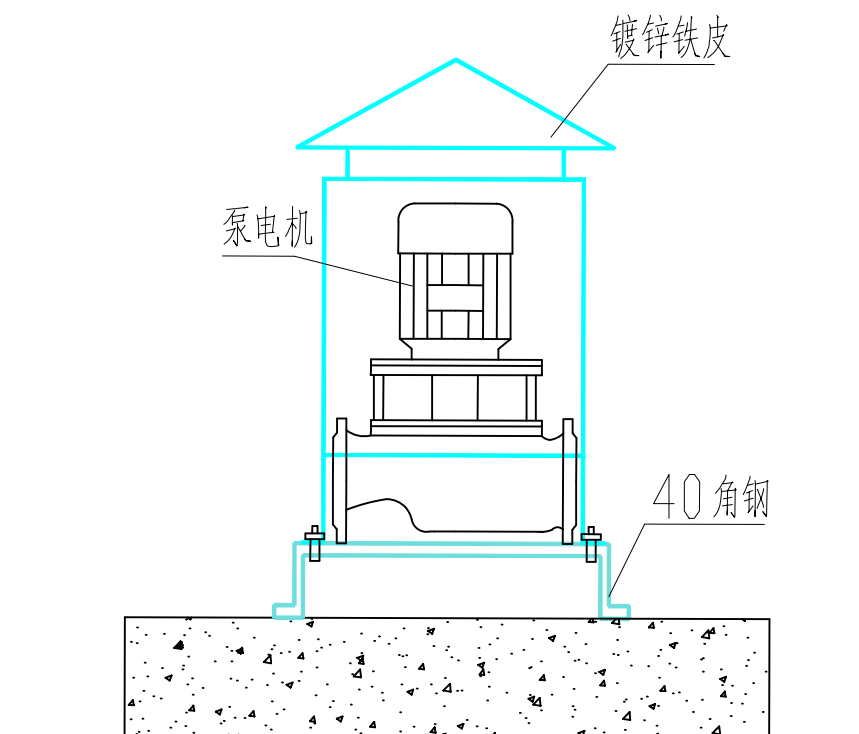

水泵防雨罩示意图

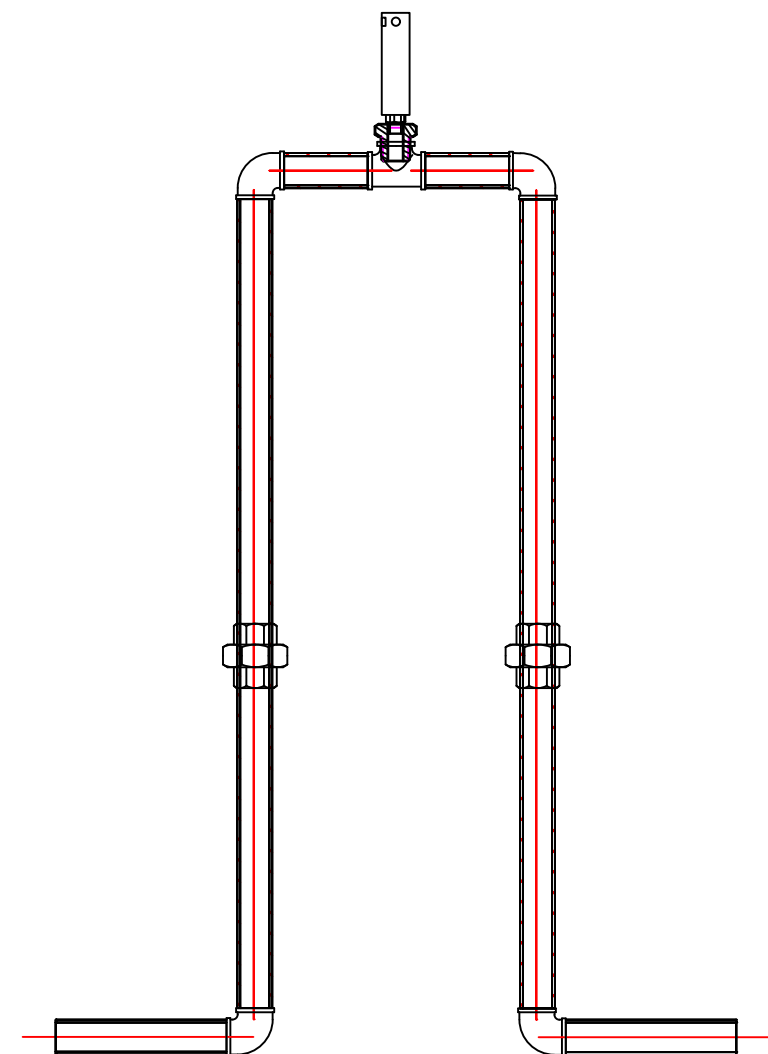

等高管安装大样图

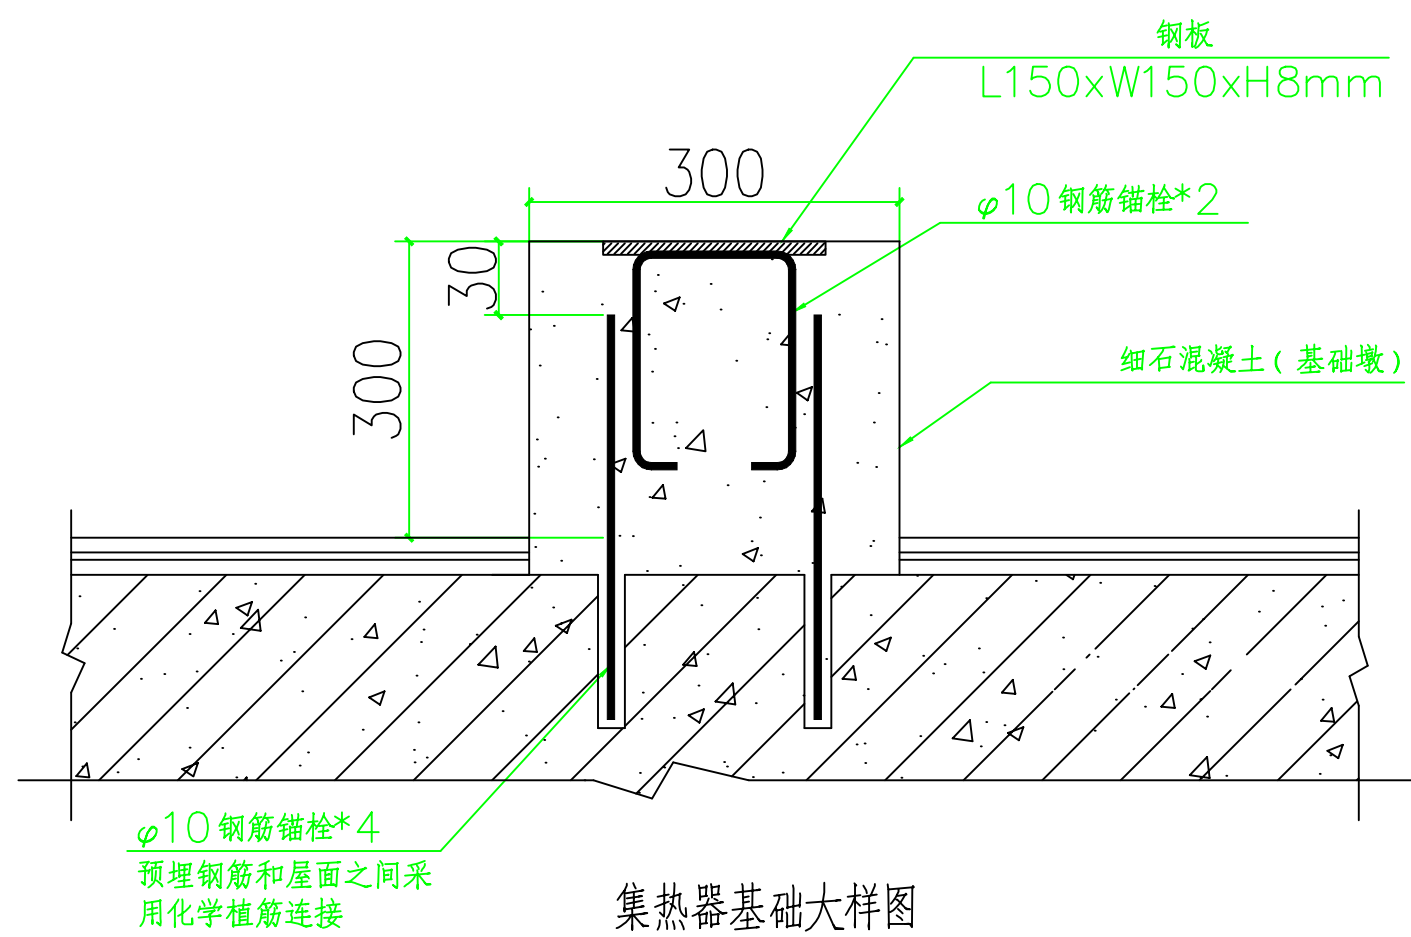



集热器基础大样图

版次 ??????	说明 ??????????	日期 ????				
 云南化工设计院有限公司 YUNNAN DESIGN INSTITUTE OF CHEMICAL ENGINEERING CO., LTD.  中信建设 CITIC CONSTRUCTION 中信建设有限责任公司 CITIC Construction Co., Ltd.						
工程名称 ??????		工程代号 ???? ???? 3147				
Uzbekistan UTMK Chemical LLC ?????? ?????? ?? ?????????????? ?????? ??????						
	姓名 ??????	签名 ??????				
	日期 ????	变更大样图				
审 定 ????????						
审 核 ????	张群 Чжан Гун					
核 核 ????	杨群 Ян Цзюнь					
设计 ????	陈俊羽 Чэн Цзюньюй	2025. 12. 18	专业 ????????	给排水 Вод.	比例 ????	第 2 张 ???
		2025. 12	日期 ????	版次 ????		共 2 张 ????

版权归云南化工设计院有限责任公司所有，未经本公司许可不得转让、复制、泄露给第三方或用于其他目的

??? ?????? ????????? YDNC. ??????? ??????? ?? ?????? ???? ??????????????, ?????????, ?????????????, ????????? ??????? ??????, ?????? ?????????????? ??? ?????? ?????? ??? ?????????? YDNC.

	修改 ???

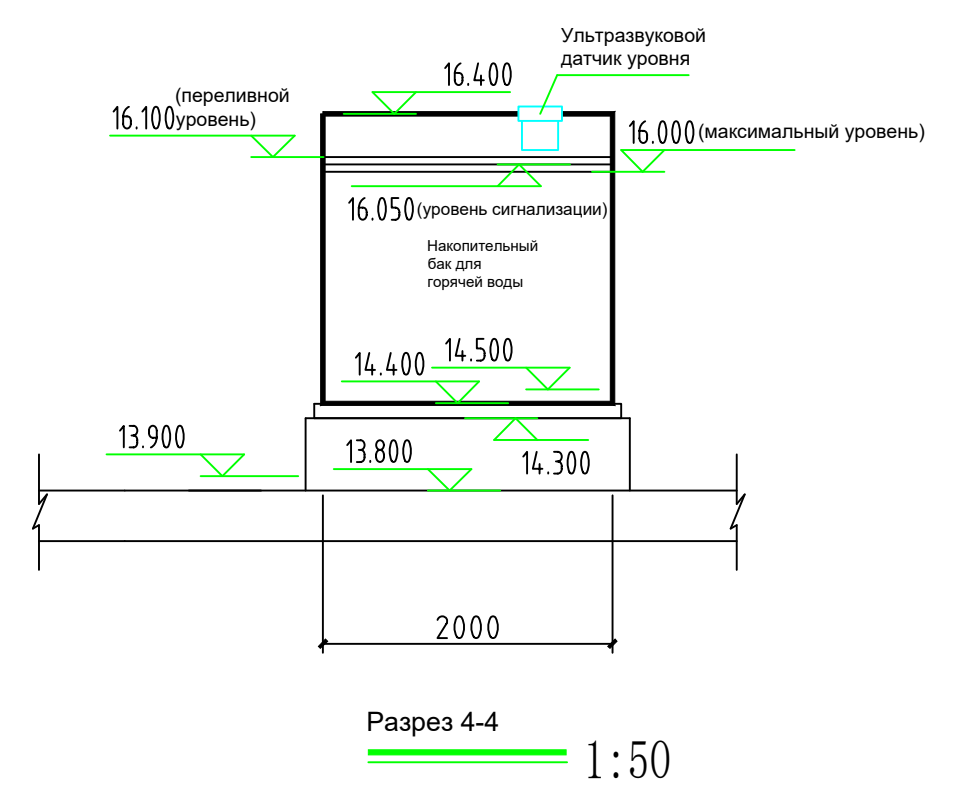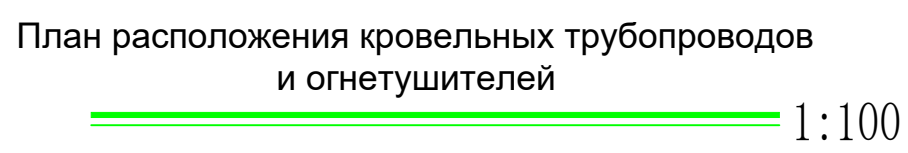

版次 ???????		说明 ?????????????				日期 ?????					
 云南化工设计院有限公司 YUNNAN DESIGN INSTITUTE OF CHEMICAL ENGINEERING CO., LTD.				 中信建设有限责任公司 CITIC Construction Co., Ltd.							
工程名称 ???????		Uzbekistan UTMK Chemical LLC ?????? ?????? ?? ?????????????? ?????? ??????						工程代号 ????????		3147	
姓名 ????????		签名 ??????		日期 ????		屋顶太阳能热水系统布置图 设计项目 设计阶段 施工图		综合楼 Администрация систем водоснабжения 施工图 Рабочие чертежи			
审定 ????????								3147-55141-05			
审核 ??????		张群 Zhang Qun		2025.12.18							
校核 ??????		张群 Zhang Qun		2025.12.18							
设计 ????????		黄俊利 Huang Junli		2025.12.18		专业 日期		给排水 2025.12		比例 版次	
								图号 1 张 共 1 张			

版权归云南化工设计院有限责任公司所有，未经本公司许可不得转让、复制、泄露给第三方或用于其他目的