


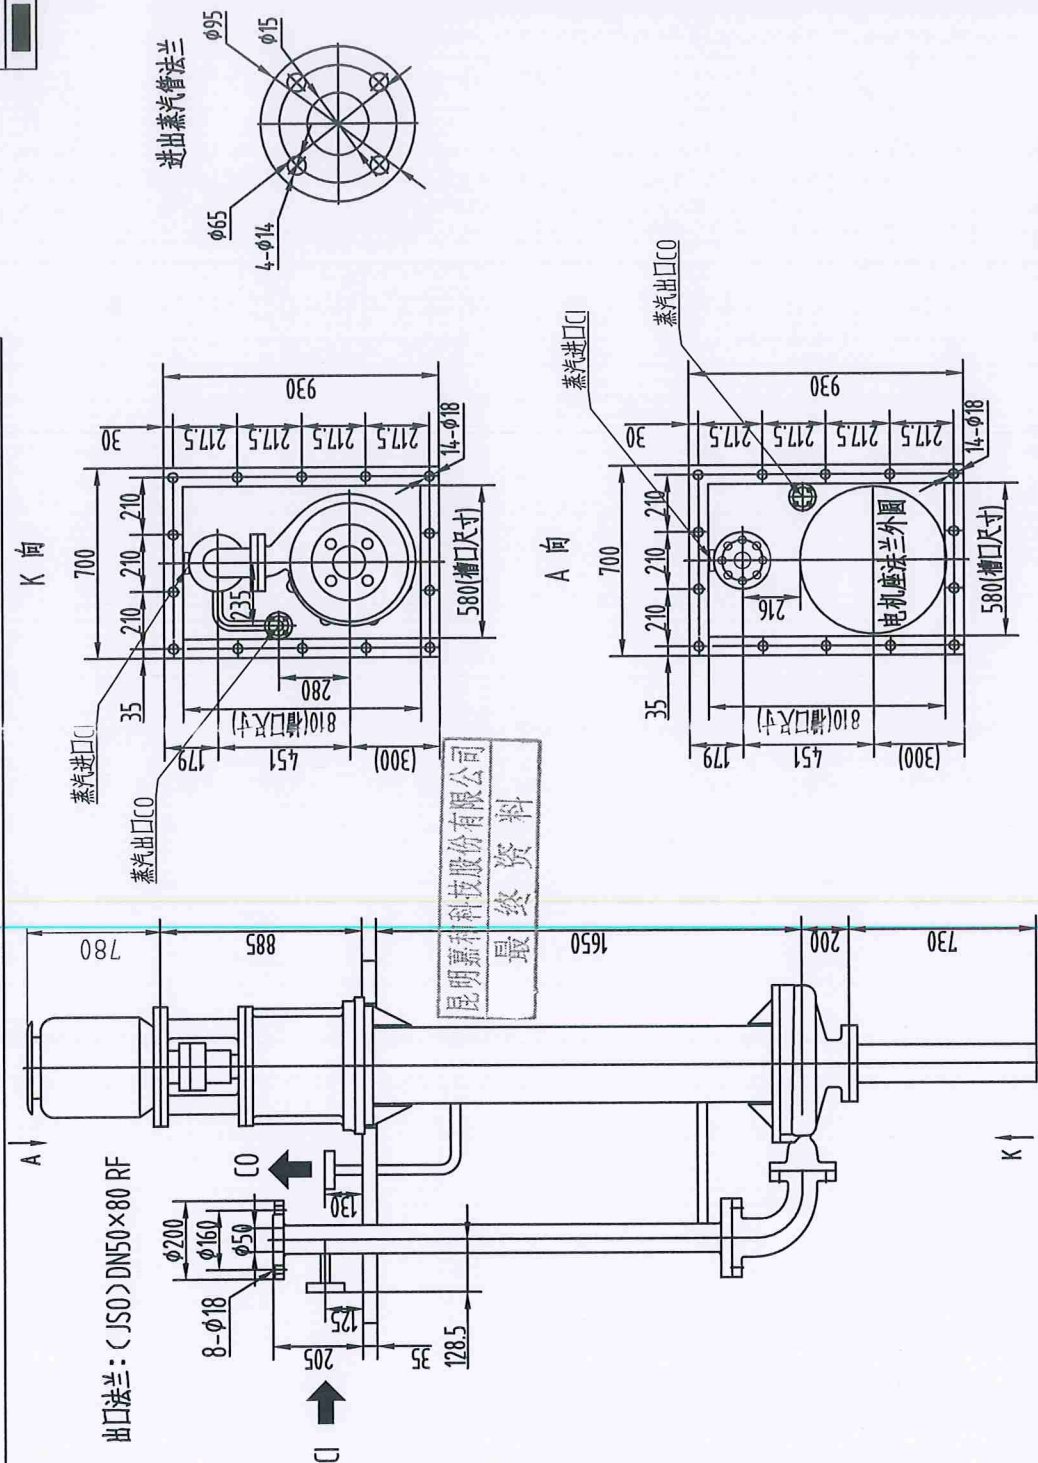

入口法兰(DNs)/Suction Flange DN80						出口法兰(DNb)/Discharge Flange DN50					
力Forces[N]			力矩Moments[Nm]			力Forces[N]			力矩Moments[Nm]		
Fx	Fy	Fz	Mx	My	Mz	Fx	Fy	Fz	Mx	My	Mz
						710	580	890	460	230	350


设备名称/Equipment.	设备型号/Serial No.	管理方案/ADIS Code.	材料	PP-1101A/B	一、概述
	设计/Designed	史加敏		JHX125-4.0	
	审核/Checked	黄益杰		外尺寸图	
	日期/Date	2006.129		General Arrangement Drawing	

外形尺寸/ General arrangement for pump and motor


版本号: 02

文件编号

外形图号/Dimensional drawing:

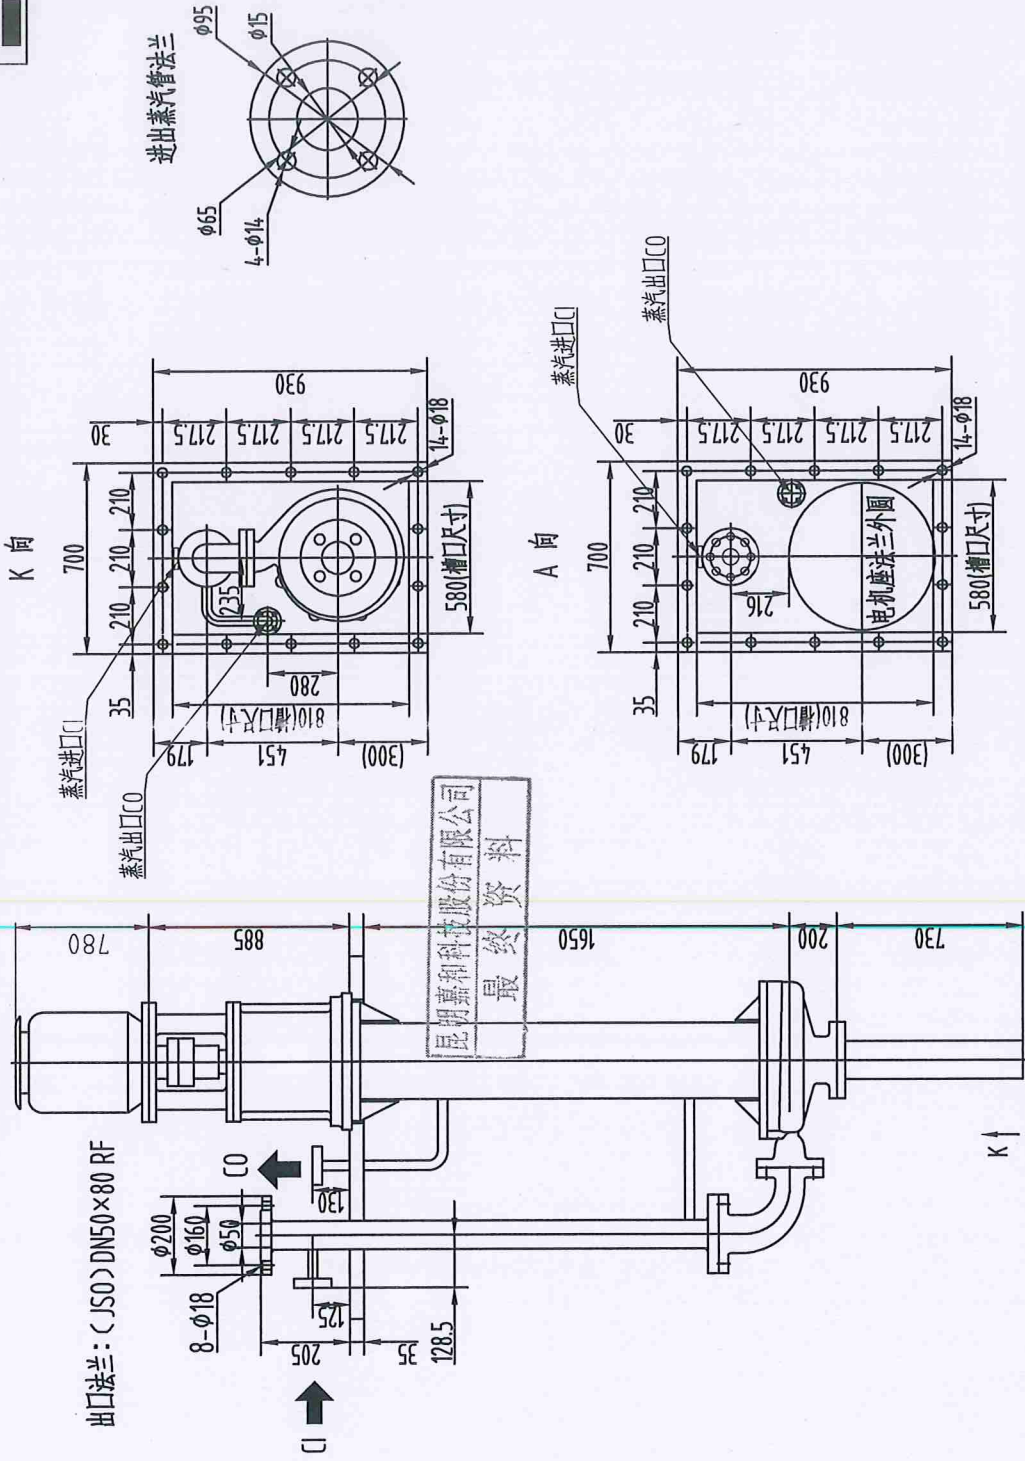

入口法兰(DNs)/Suction Flange DN80						出口法兰(DNb)/Discharge Flange DN50					
力Forces[N]			力矩Moments[Nm]			力Forces[N]			力矩Moments[Nm]		
Fx	Fy	Fz	Mx	My	Mz	Fx	Fy	Fz	Mx	My	Mz
						710	580	890	460	230	350

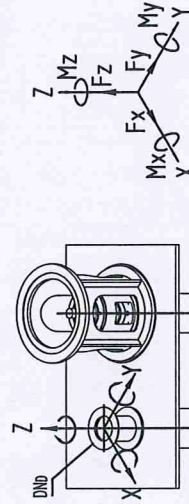

无特殊说明尺寸为：毫米 UNLESS SPECIFIED DIMENSIONS: MM	视图/Projection 	无比列尺寸 NO SCALE
☐ 投熔材料	依作为铸钢件多使用。图中长行尺寸不作为铸作加工用	
☐ 中钢材料	作为钢件多使用。管口尺寸、能可多作为铸作使用	
☒ 铸铁材料	作为灰口铸铁后的铸钢。作为加工用	

ITEM	描述/Description	尺寸/Size	流量和吸力/Range Class
DN5	真空/ump suction nozzle	DN 80	
DND	真空/ump discharge nozzle	DN 50×80	HG/720592(B) PWS RF
CO	蒸汽抽吸/Steam outlet	DN 15	HG/720593(B) PWS RF
CI	蒸汽抽吸/Steam inlet	DN 15	HG/720592(B) PWS RF

泵参数/PUMP SPECIFICATIONS	
设计转速/design speed	1450 r/min
转向/Rotation	顺时针/从驱动端看/Viewed from drivers

电机型号/Motor size	P65/F/B/MFZ/Ex II MB AZ1 Ø65 T200/380V 50Hz		
额定电压/Item No.	380V	3ph	50Hz
额定功率/Rated output.	22kW-4		
产地/原/Motor Mfr	佛山/广东		


近似重量/APPROXIMATE WEIGHTS(KG)			
泵/Pump.	800 Kg	电动机/Motor.	195 Kg
底座/Baseplate.	Kg	辅助壳/Auxiliary sp.	Kg
总重/Total.	995 Kg		

客户名称/Client:	湖南工业装备工艺装备公司
项目名称/Project:	50万吨年建筑砂浆生产线项目
设备名称/Equipment:	二破过滤器
设备位号/Series No.	PP-1102A/B
编制方案/ADNs Code:	建筑

设计/Designed	史朝竣
审核/Checked	黄凯杰
日期/Date	2026.129


JHXL80-30

外形图号/Dimensional drawing:

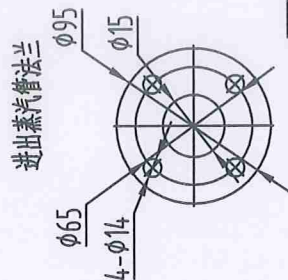

设计/Designed	史朝峻	JHXL80-30 外形尺寸图 General Arrangement Drawing
审核/Checked	黄晓杰	
日期/Date	2026.12.09	

入口法兰(DNs)/Suction Flange DN80						出口法兰(DNp)/Discharge Flange DN80					
力Forces[N]			力矩Moments[Nm]			力Forces[N]			力矩Moments[Nm]		
Fx	Fy	Fz	Mx	My	Mz	Fx	Fy	Fz	Mx	My	Mz
						1070	890	1330	950	470	720

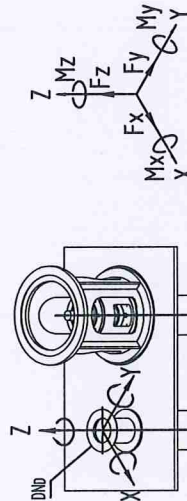



JHL30-25

版本号: 01

文件编号

外形图号/Dimensional drawing:

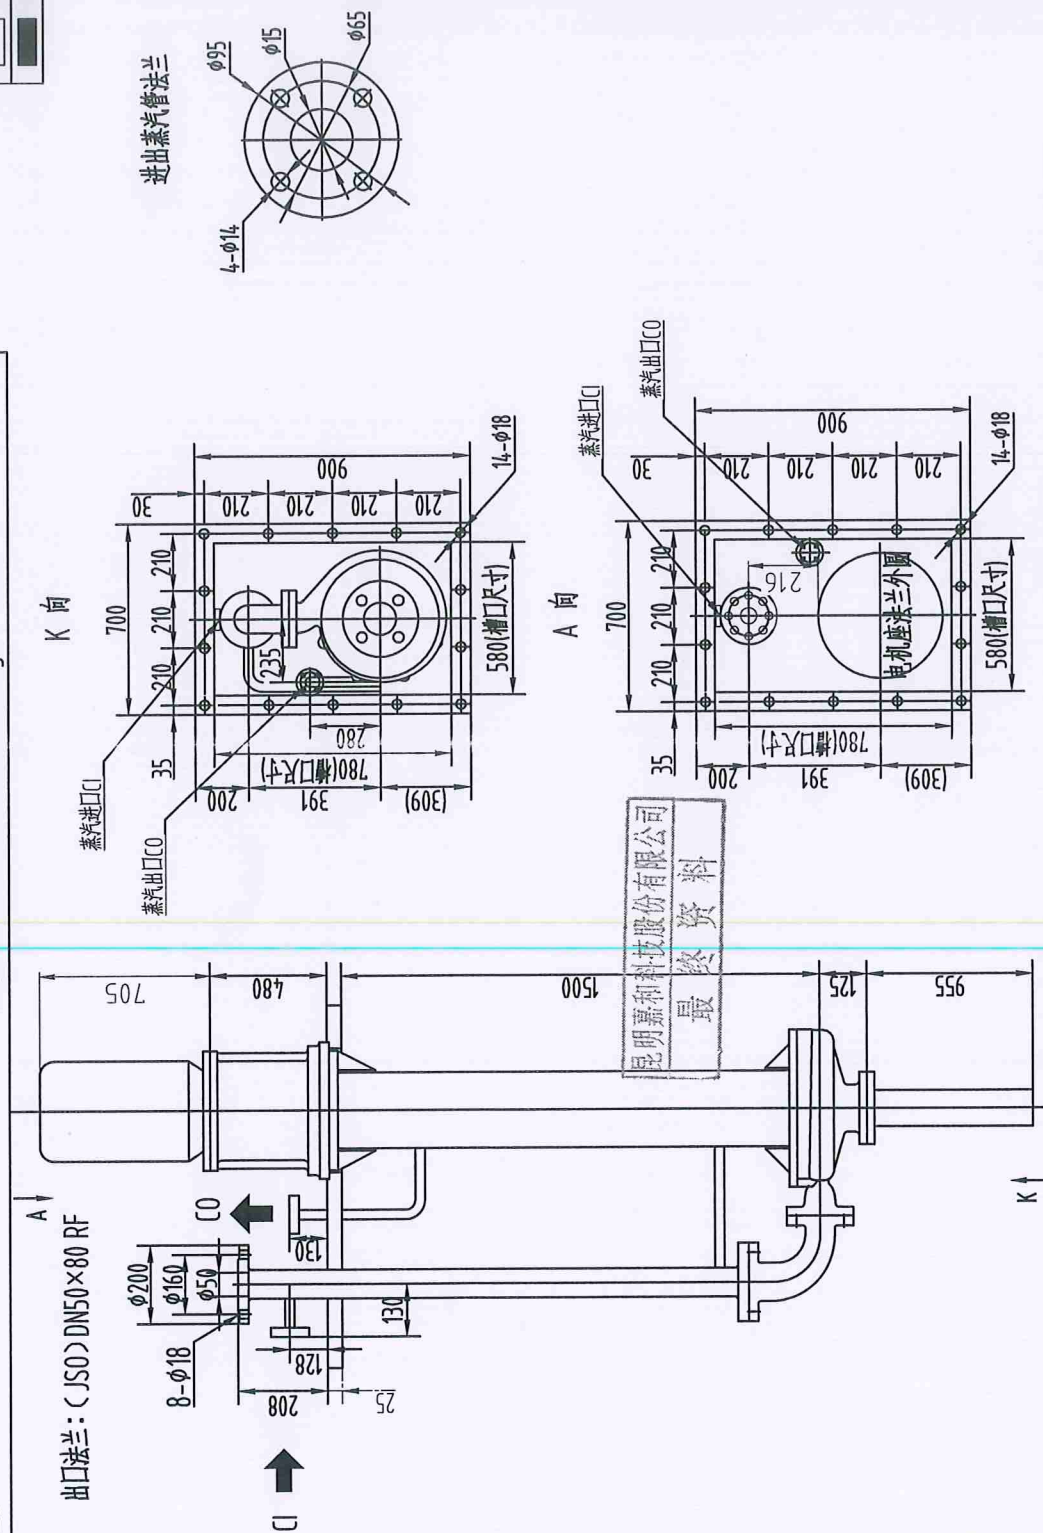

 无特殊说明尺寸为：毫米 UNLESS SPECIFIED DIMENSIONS: MM	视图/Projection 	无比例尺寸 NO SCALE
☐ 投影材料	仅作技术说明参考使用。图中任何尺寸都不能作为加工用	
☐ 中间材料	仅作加工参考使用。管口尺寸、壁厚等仅作参考使用	
☒ 最终材料	仅作加工确定制造标准、作为加工用	

ITEM	描述/Description	尺寸/Size	物料代码/Materials Class
DN15	泵入口/pump suction nozzle	DN 80	H67T05920B PENG RF
DN20	泵出口/pump discharge nozzle	DN 50×80	H67T05920B PENG RF
CO	蒸汽接口/Steam outlet	DN 15	H67T05920B PENG RF
CI	蒸汽接口/Steam inlet	DN 15	H67T05920B PENG RF


家多泵/PUMP SPECIFICATIONS	
设计转速/design speed	1450 r/min
转向/Rotation	顺时针/从驱动端看/Viewed from drivers
驱动电机/DRIWER SPECIFICATIONS	
电机型号/Motor size	P65/F60/MF2/Ex td IIB, A21 IP65 /300V50Hz
额定电压/Ren No.	V ph Hz
额定功率/Rated output.	15kW-4
电机厂家/Motor Mfr.	

泵(Pump).	650	Kg	电机/Motor.	142	Kg
底座/Baseplate.		Kg	辅助光/Auxiliary ep.		Kg
达重/Total.	792	Kg			

用户名称/Client:	湖南金工设计技术有限公司
项目名称/Project:	50万吨/年连续流化制硫项目
设备名称/Equipment:	中间制泵
设备位号/Series No.	PP-1100A/B
制泵方案/ADNs Code.	泵类

设计/Designed	史翔曼
审核/Checked	黄凯杰
日期/Date	2026.1.29


	入口法兰(Suction Flange DN80)						出口法兰(DN50)/Discharge Flange DN50	
	力F[N]			力矩Moments[Nm]			力F[N]			力矩Moments[Nm]	
	Fx	Fy	Fz	Mx	My	Mz	Fx	Fy	Fz	Mx	My	Mz	
<table><tr><td></td><td></td><td></td><td></td><td></td><td></td><td></td><td></td><td></td><td></td><td></td><td></td><td></td></tr><tr><td></td><td></td><td></td><td></td><td></td><td></td><td></td><td></td><td></td><td></td><td></td><td></td><td></td></tr><tr><td></td><td></td><td></td><td></td><td></td><td></td><td></td><td></td><td></td><td></td><td></td><td></td><td></td></tr><tr><td></td><td></td><td></td><td></td><td></td><td></td><td></td><td></td><td></td><td></td><td></td><td></td><td></td></tr><tr><td></td><td></td><td></td><td></td><td></td><td></td><td></td><td></td><td></td><td></td><td></td><td></td><td></td></tr><tr><td></td><td></td><td></td><td></td><td></td><td></td><td></td><td></td><td></td><td></td><td></td><td></td><td></td></tr><tr><td></td><td></td><td></td><td></td><td></td><td></td><td></td><td></td><td></td><td></td><td></td><td></td><td></td></tr><tr><td></td><td></td><td></td><td></td><td></td><td></td><td></td><td></td><td></td><td></td><td></td><td></td><td></td></tr><tr><td></td><td></td><td></td><td></td><td></td><td></td><td></td><td></td><td></td><td></td><td></td><td></td><td></td></tr><tr><td></td><td></td><td></td><td></td><td></td><td></td><td></td><td></td><td></td><td></td><td></td><td></td><td></td></tr><tr><td></td><td></td><td></td><td></td><td></td><td></td><td></td><td></td><td></td><td></td><td></td><td></td><td></td></tr><tr><td></td><td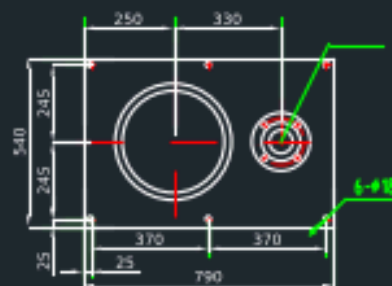



	30	m ³ /h
	40	m
	57.2	%
	2980	r/min

	Y160M1-2	
	11	kW
	2980	r/min
	380	V

	280	kg
	120	kg
	400	kg

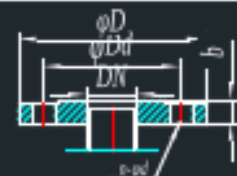

	HG/T20592-2009(B) PN1.6MPa	
DN	40	
φDd	110	
φD	150	
n-φd	4-φ18	
b	18	

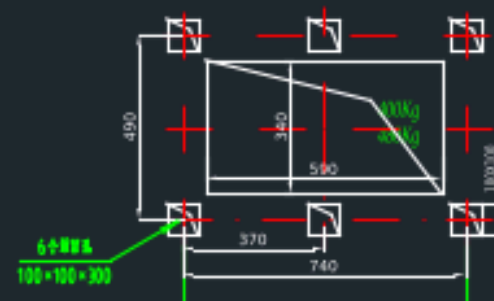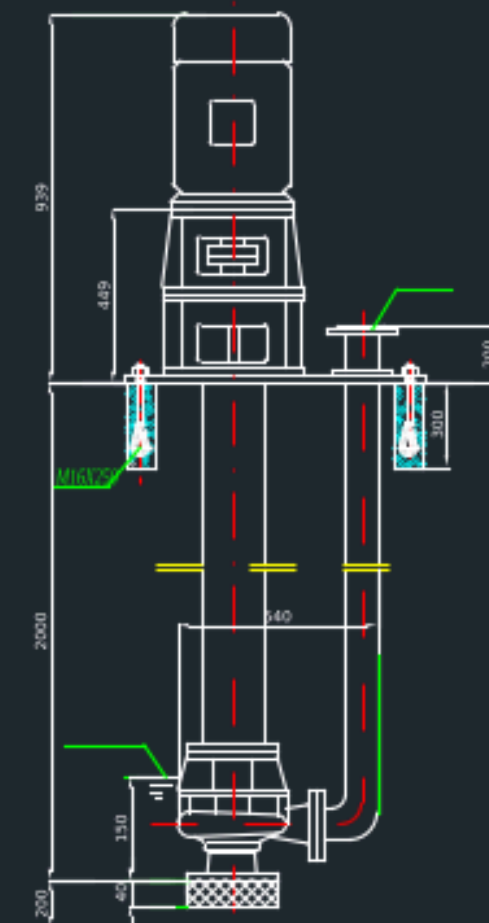

	58		
			DW40-200-Y160M1-2
	2025.12.9		