
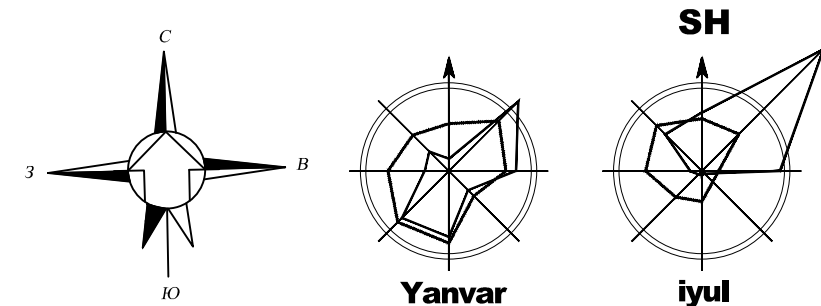
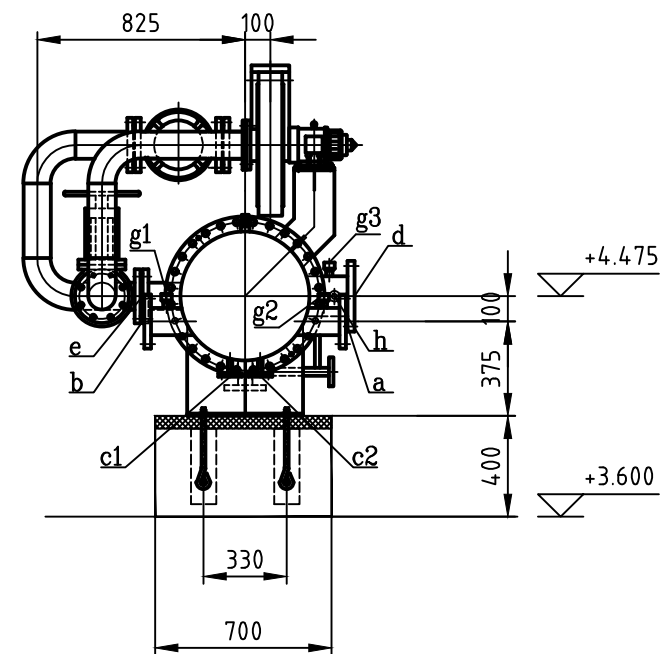


修改 REC.	

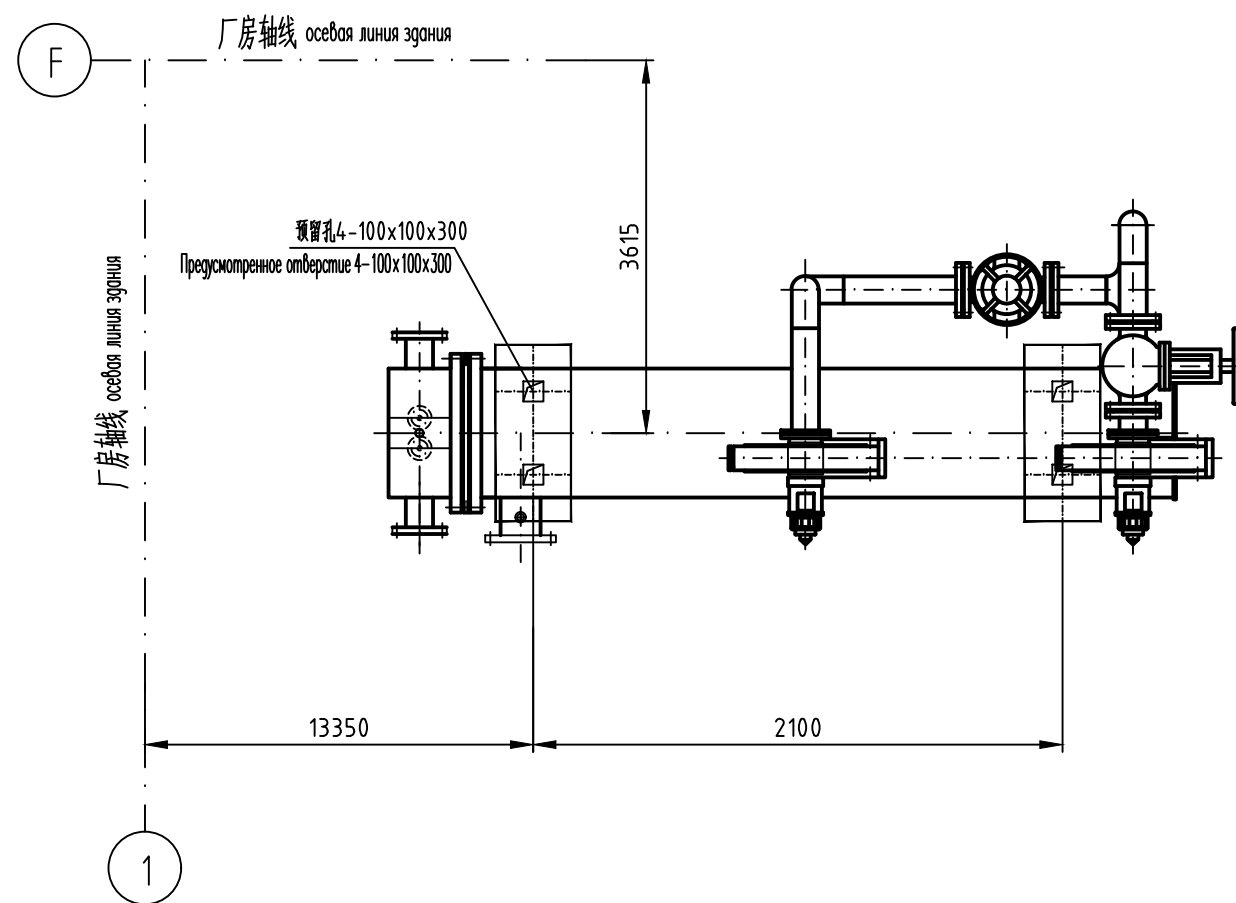

管口表						
Таблица патрубков						
序号 № п/п	用途 Назначение	接口形式 Тип соединения	公称尺寸 Номинальный диаметр (DN)	连接尺寸标准规格 Стандарт присоединительных размеров	密封面型式 Исполнение уплотнительной поверхности	备注 Примеч.
a	进出口 входной и выходной патрубки воды	法兰 фланцевое	DN100	JB/T81-2015 DN100-PN16 PL RF 2	RF	
b	进出口 входной и выходной патрубки воды	法兰 фланцевое	DN100	JB/T81-2015 DN100-PN16 PL RF 2	RF	
c1.c2	疏水口 дренажный патрубок воды	法兰 фланцевое	DN15	JB/T81-2015 DN15-PN16 PL RF 2	RF	
d	进气口 входной патрубок пара	法兰 фланцевое	DN150	JB/T81-2015 DN150-PN16 PL RF 2	RF	
e	出气口 (密封抽风机) выходной патрубок пара (эксплуататор уплотнений)	法兰 фланцевое	DN100	JB/T81-2015 DN100-PN16 PL RF 2	RF	
f	疏水口 дренажный патрубок	法兰 фланцевое	DN50	JB/T81-2015 DN50-PN16 PL RF 2	RF	
g1.g2.g3	接温度计 патрубок для установки термометра	螺纹 резьбовое	/	M27x2	/	
h	接压力表 патрубок для установки манометра	螺纹 резьбовое	/	M20x1.5	/	
i1.i2	接液位计 патрубок для установки воздухоотделителя	法兰 фланцевое	DN25	JB/T81-2015 DN25-PN16 PL RF 2	RF	

说明:

1.汽封冷却器布置在汽轮机前侧+3.60m平台上,汽封冷却器与混凝土基础上用地脚螺栓连接。




Примечание:

1. Охладитель уплотнений турбины размещается на платформе отметки +3,60 м перед турбиной. Охладитель уплотнений турбины крепится к бетонному фундаменту анкерными болтами.

0		供施工				2026. 6. 5	
版次 Версия		说明 Примечания				日期 Дата	
 云南化工设计院有限公司 YUNNAN DESIGN INSTITUTE OF CHEMICAL ENGINEERING CO., LTD.				 中信建设 CITIC Construction Co., Ltd.			
工程名称 НАЗВАНИЕ ПРОЕКТА		乌兹别克斯坦年产50万吨硫酸项目 Uzbekistan UTMK Chemical LLC Проект завода по производству серной кислоты					工程代号 Код объекта 3147
姓名 Фамилия и имя		签名 Подпись	日期 Дата	汽封冷却器安装图 Чертёж установки охладителя уплотнений пара		设计项目 Проектируемый объект	余热发电 Выработка электроэнергии на утилизации тепла
审定 Утверждение	审核 Рассм.	余雪芳	2026. 6. 5			设计阶段 Стадия проектирования	施工图 Детальное проектирование
校核 Проверка	王彦斐	王彦斐	2026. 6. 5	专业 Специальность	热工/Тепловая работа	比例 Масштаб	1:30
设计 Проектирование	陈亮	陈亮	2026. 6. 5	日期 Дата	2026. 6	版次 Версия	0
						第 1 张 Лист	Типовая рамка чертежа (версия 2020)
						共 1 张 Листы	

版权所有, 未经本公司许可不得转让 复制 泄露给第三方或用于其它目的。
ALL RIGHTS RESERVED BY TOYO. THIS DRAWING MAY NOT BE ASSIGNED, TRANSFERRED, COPIED, OR DISCLOSED TO ANY THIRD PARTIES OR USED FOR OTHER PURPOSES WITHOUT PERMISSION OF TOYO.

会签 COSTING	姓名 NAME	签名 SIGNATURE
工艺 PR		
设备 EQ		
起运 LT		
自控 IN		
给排水 WD		
电 EL		
采暖 TH&HVAC		
建筑 AR		
结构 ST		
总图 PN		
设计 经理 DESIGN MANAGER		

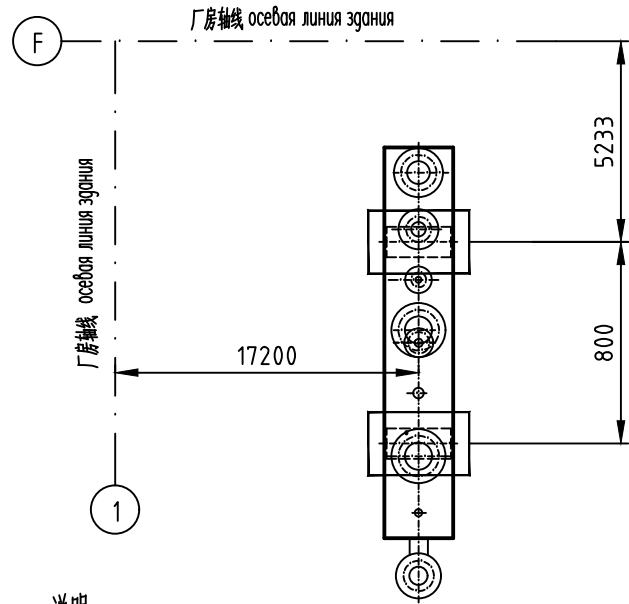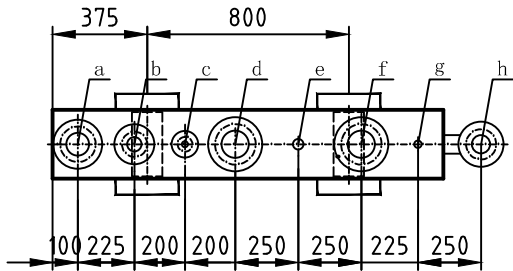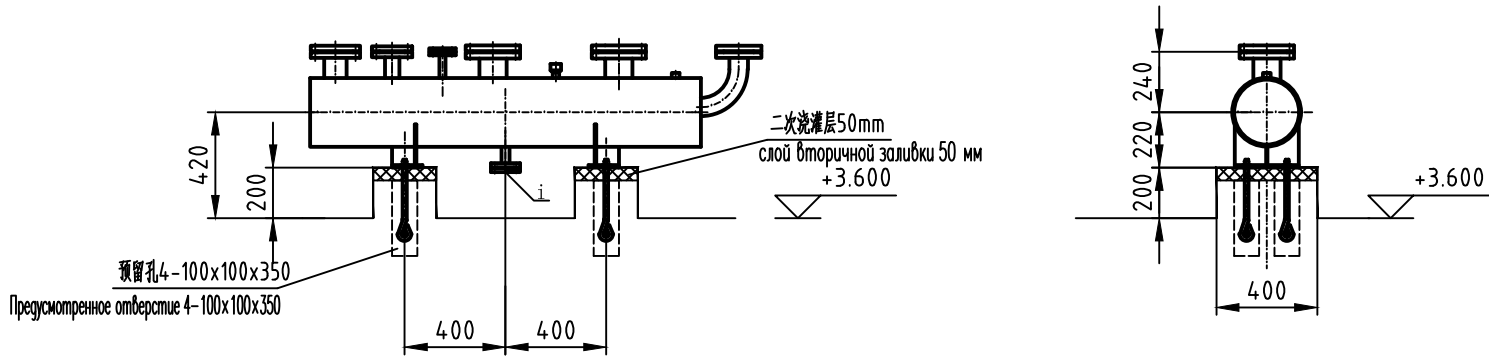

说明:

1.均压箱布置在汽轮机前侧+3.60m平台上,均压箱与混凝土基础上用地脚螺栓连接。

Примечание:

1.Камера выравнивания давления размещается на платформе отметки +3,60 м перед турбиной.
Камера выравнивания давления крепится к бетонному фундаменту анкерными болтами.

云南省工程勘察设计文件(出图)专用章

单位名称: 云南化工设计院有限公司


证书编号: 5300790

有效期至: 2030年02月14日

资质: 化工石化医药行业甲级; 建筑行业(建筑工程)甲级; 环境工程设计专项(水污染防治工程, 大气污染防治工程, 固体废物处理处置工程)甲级; 轻纺行业(日化及塑料工程, 食品发酵烟草工程)乙级; 市政行业(给水工程, 排水工程, 城镇燃气工程, 环境卫生工程)乙级;

云南省住房和城乡建设厅2025年08月15日制发

项目出图章编号: 4202590044894 项目名称: 乌兹别克斯坦年产50万吨硫磺制酸项目
用途: 施工图


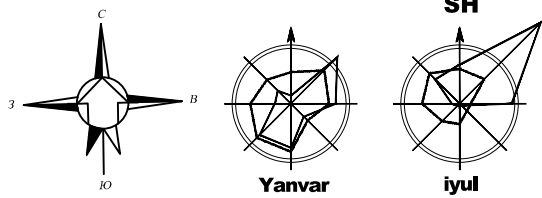


管口表

序号 № n/n	用途 Назначение	接口形式 Тип соединения	公称尺寸 Условный пропуск (DN)	连接尺寸标准规格 Стандарт присоединительных размеров	密封面型式 Исполнение уплотнительной поверхности	备注 Примеч.
a	接口 Патрубок	法兰 фланцевое	DN80	JB/T81-2015 DN80-PN16 PL RF 2	RF	
b	接口 Патрубок	法兰 фланцевое	DN50	JB/T81-2015 DN50-PN16 PL RF 2	RF	
c	接口 Патрубок 接减温水	法兰 фланцевое	DN20	JB/T81-2015 DN20-PN16 PL RF 2	RF	
d	接口 Патрубок 接温度计	法兰 фланцевое	DN100	JB/T81-2015 DN100-PN16 PL RF 2	RF	
e	接口 Патрубок 接压力表	螺纹 резьбовое		M27X2		
f	接口 Патрубок 接温度计	法兰 фланцевое	DN100	JB/T81-2015 DN100-PN16 PL RF 2	RF	
g	接口 Патрубок 接压力表	螺纹 резьбовое		M20X1.5		
h	接口 Патрубок	法兰 фланцевое	DN65	JB/T81-2015 DN65-PN16 PL RF 2	RF	
i	接口 Патрубок	法兰 фланцевое	DN25	JB/T81-2015 DN25-PN10 PL RF 2	RF	


0	供施工	2026. 6. 5
版次 Версия	说明 Примечания	日期 Дата
云南化工设计院有限公司 YUNNAN DESIGN INSTITUTE OF CHEMICAL ENGINEERING CO.,LTD.		中信建设有限责任公司 CITIC Construction Co.,Ltd.
工程名称 НАЗВАНИЕ ПРОЕКТА	乌兹别克斯坦年产50万吨硫磺制酸项目 Uzbekistan UTMK Chemical LLC Проект завода по производству серной кислоты	工程代号 Код объекта 3147
审定 Утверждение	姓名 Фамилия и имя	签名 Подпись
审核 Рассм.	余雪芳	2026. 6. 5
校核 Проверка	王彦斐	2026. 6. 5
设计 Проектирование	陈亮	2026. 6. 5
均压箱安装图 Чертеж установки уравнительного бачка		设计项目 Проектируемый объект 余热发电 Выработка электроэнергии на утилизации тепла
设计阶段 Стадия проектирования		施工图 Детальное проектирование
图号 № чертежа		3147-5R115-31
专业 Специальность		余热发电 Тепловая работа
比例 Масштаб		1:30
日期 Дата		2026. 6
版次 Версия		0
第1张 Лист		共1张 Листы

会签 COSTING	姓名 NAME	签名 SIGNATURE
工艺 PR		
设备 EQ		
起运 LT		
自控 IN		
给排水 WD		
电 EL		
采暖 TH&HVAC		
建筑 AR		
结构 ST		
总图 PN		
设计 DESIGN		
经理 MANAGER		

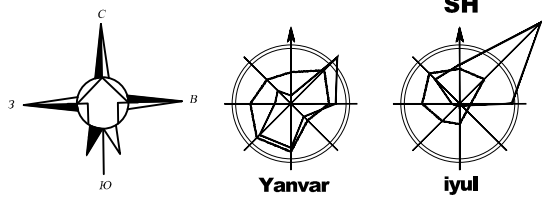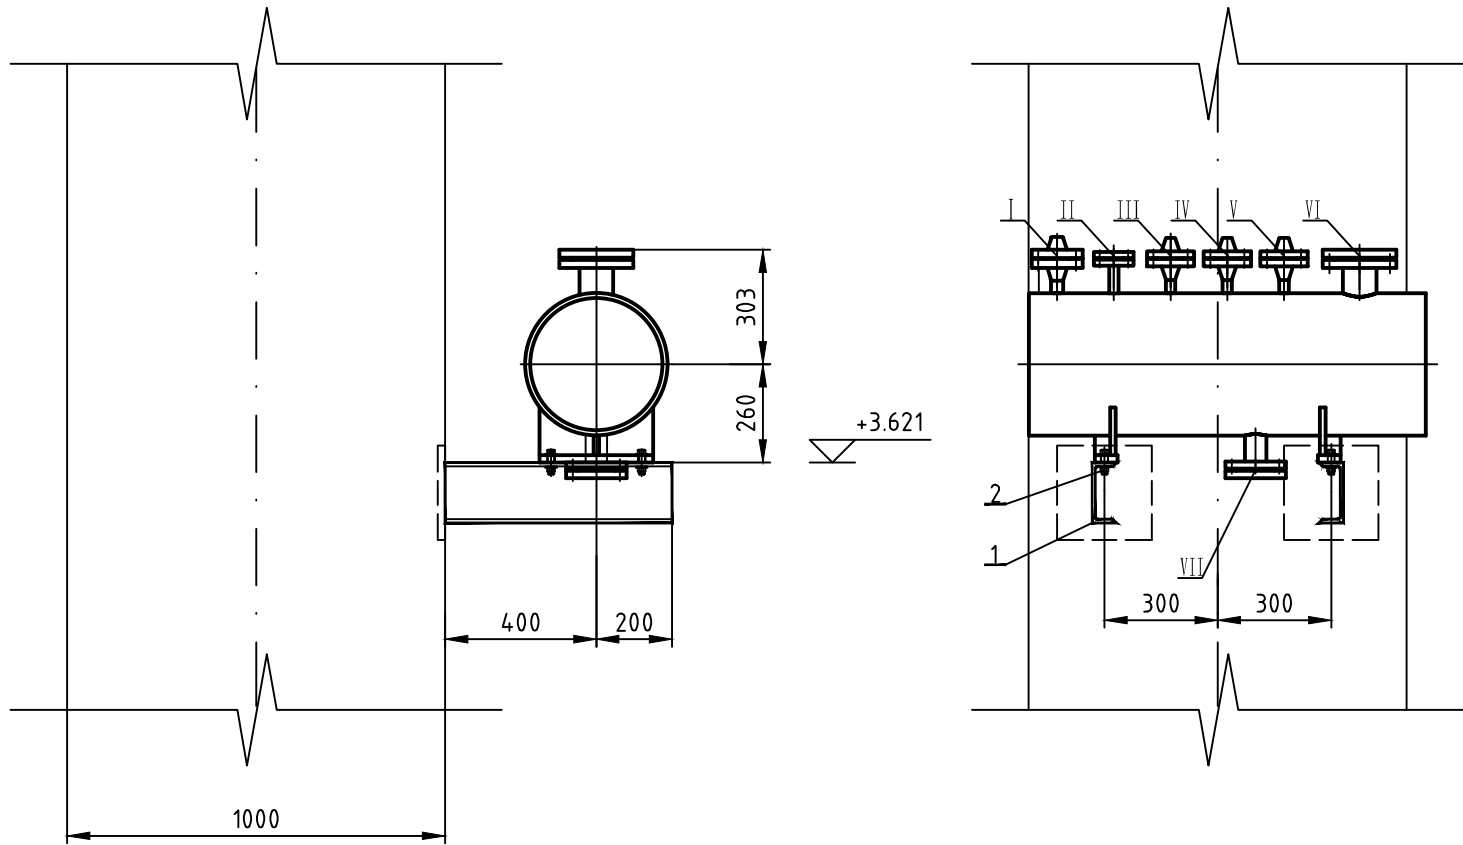

管口表
Таблица патрубков

序号 № п/п	接口型式 Тип соединения	公称压力 / 通径 Услов. давл. (PN)/проход (DN)	法兰外径 Нахв. диаметр фланца	螺栓直径 Диам. болтов	螺栓数目 Кол-во болтов
I	法兰	PN10.0 DN25	φ135	M16	4
II	法兰	PN2.5 DN20	φ105	M12	4
III	法兰	PN6.3 DN20	φ125	M16	4
IV	法兰	PN6.3 DN20	φ125	M16	4
V	法兰	PN6.3 DN20	φ125	M16	4
VI	法兰	PN1.6 DN80	φ195	M16	8
VII	法兰	PN1.6 DN50	φ160	M16	4

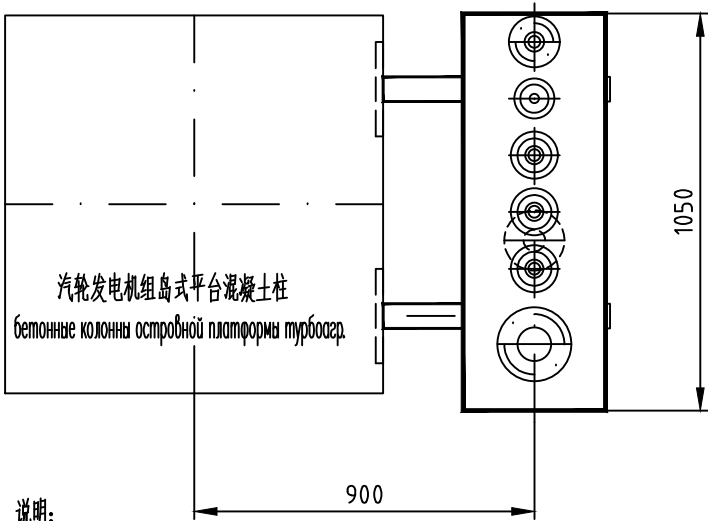

说明:

1. 疏水膨胀箱布置在汽轮发电机组岛式基础柱侧, 采用槽钢支撑, 槽钢与预埋件焊接, 疏水膨胀箱与支撑槽钢用六角头螺栓连接。

Примечание:

1. Расширитель дренажей установлен рядом с колоннами островного фундамента турбоагрегата на опорных швеллерах. Швеллеры привариваются к закладным деталям, а расширитель дренажей крепится к швеллерам шестигранными болтами.

云南省工程勘察设计文件(出图)专用章

单位名称: 云南化工设计院有限公司

证书编号: 5300790

有效期至: 2030年02月14日

资质: 化工石化医药行业甲级; 建筑行业(建筑工程)甲级; 环境工程设计专项(水污染防治工程, 大气污染防治工程, 固体废物处理处置工程)甲级; 轻纺行业(日化及塑料工程, 食品发酵烟草工程)乙级; 市政行业(给水工程, 排水工程, 城镇燃气工程, 环境卫生工程)乙级;

云南省住房和城乡建设厅2025年08月15日制发

项目出图章编号: 4202590044894 项目名称: 乌兹别克斯坦年产50万吨硫磺制酸项目
用途: 施工图



安装材料表

Монтажная спецификация

序号 № п/п	标准号 Нормативный документ	名称 Наименование	规格 Размер	单位 Ед. изм.	数量 Количество	备注 Примечание
1	GB/T706-2016	槽钢 Швеллер	[160×65 L=600mm	m	2	
2	GB/T5782-2025	六角头螺栓 Шестигранный болт	M16×75	个/шт.	4	配套螺母及垫圈 Комплектные гайки и шайбы

0	供施工	2026. 6. 5
版次 Версия	说明 Примечания	日期 Дата



云南化工设计院有限公司

YUNNAN DESIGN INSTITUTE OF CHEMICAL ENGINEERING CO., LTD.









中信建设有限责任公司

CITIC Construction Co., Ltd.

工程名称 НАЗВАНИЕ ПРОЕКТА	乌兹别克斯坦年产50万吨硫磺制酸项目 Uzbekistan UTMK Chemical LLC Проект завода по производству серной кислоты	工程代号 Код объекта	3147
姓名 Фамилия и имя	签名 Подпись	日期 Дата	设计项目 Проектируемый объект
审定 Утверждение	审核 Рассм.	校核 Проверка	设计阶段 Стадия проектирования
图号 № чертежа	第1张 Лист	共1张 Листы	余热发电 Выработка электроэнергии на утилизации тепла
专业 Специальность	热工 Тепловая работа	比例 Масштаб	1:30
日期 Дата	2026. 6	版次 Версия	0

修改 DC	
----------	--

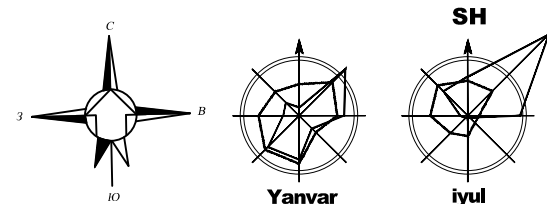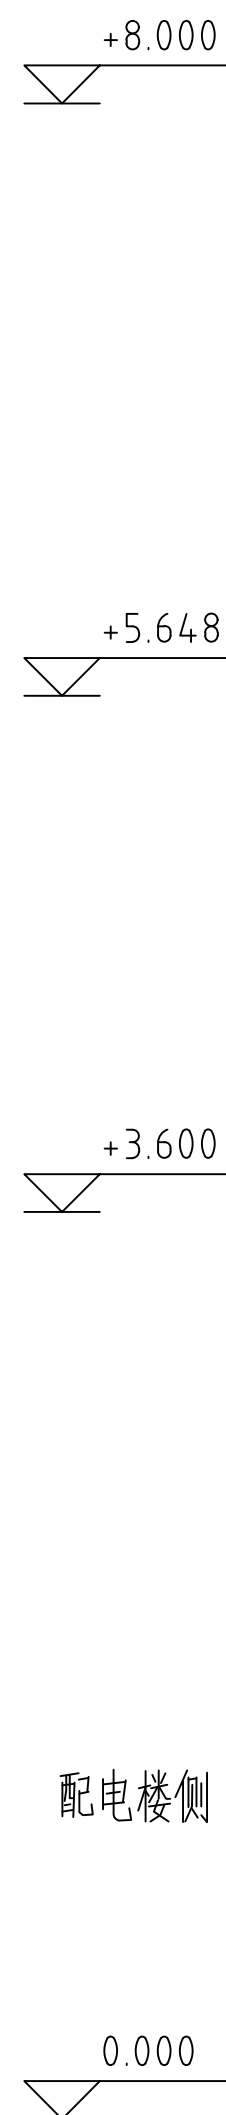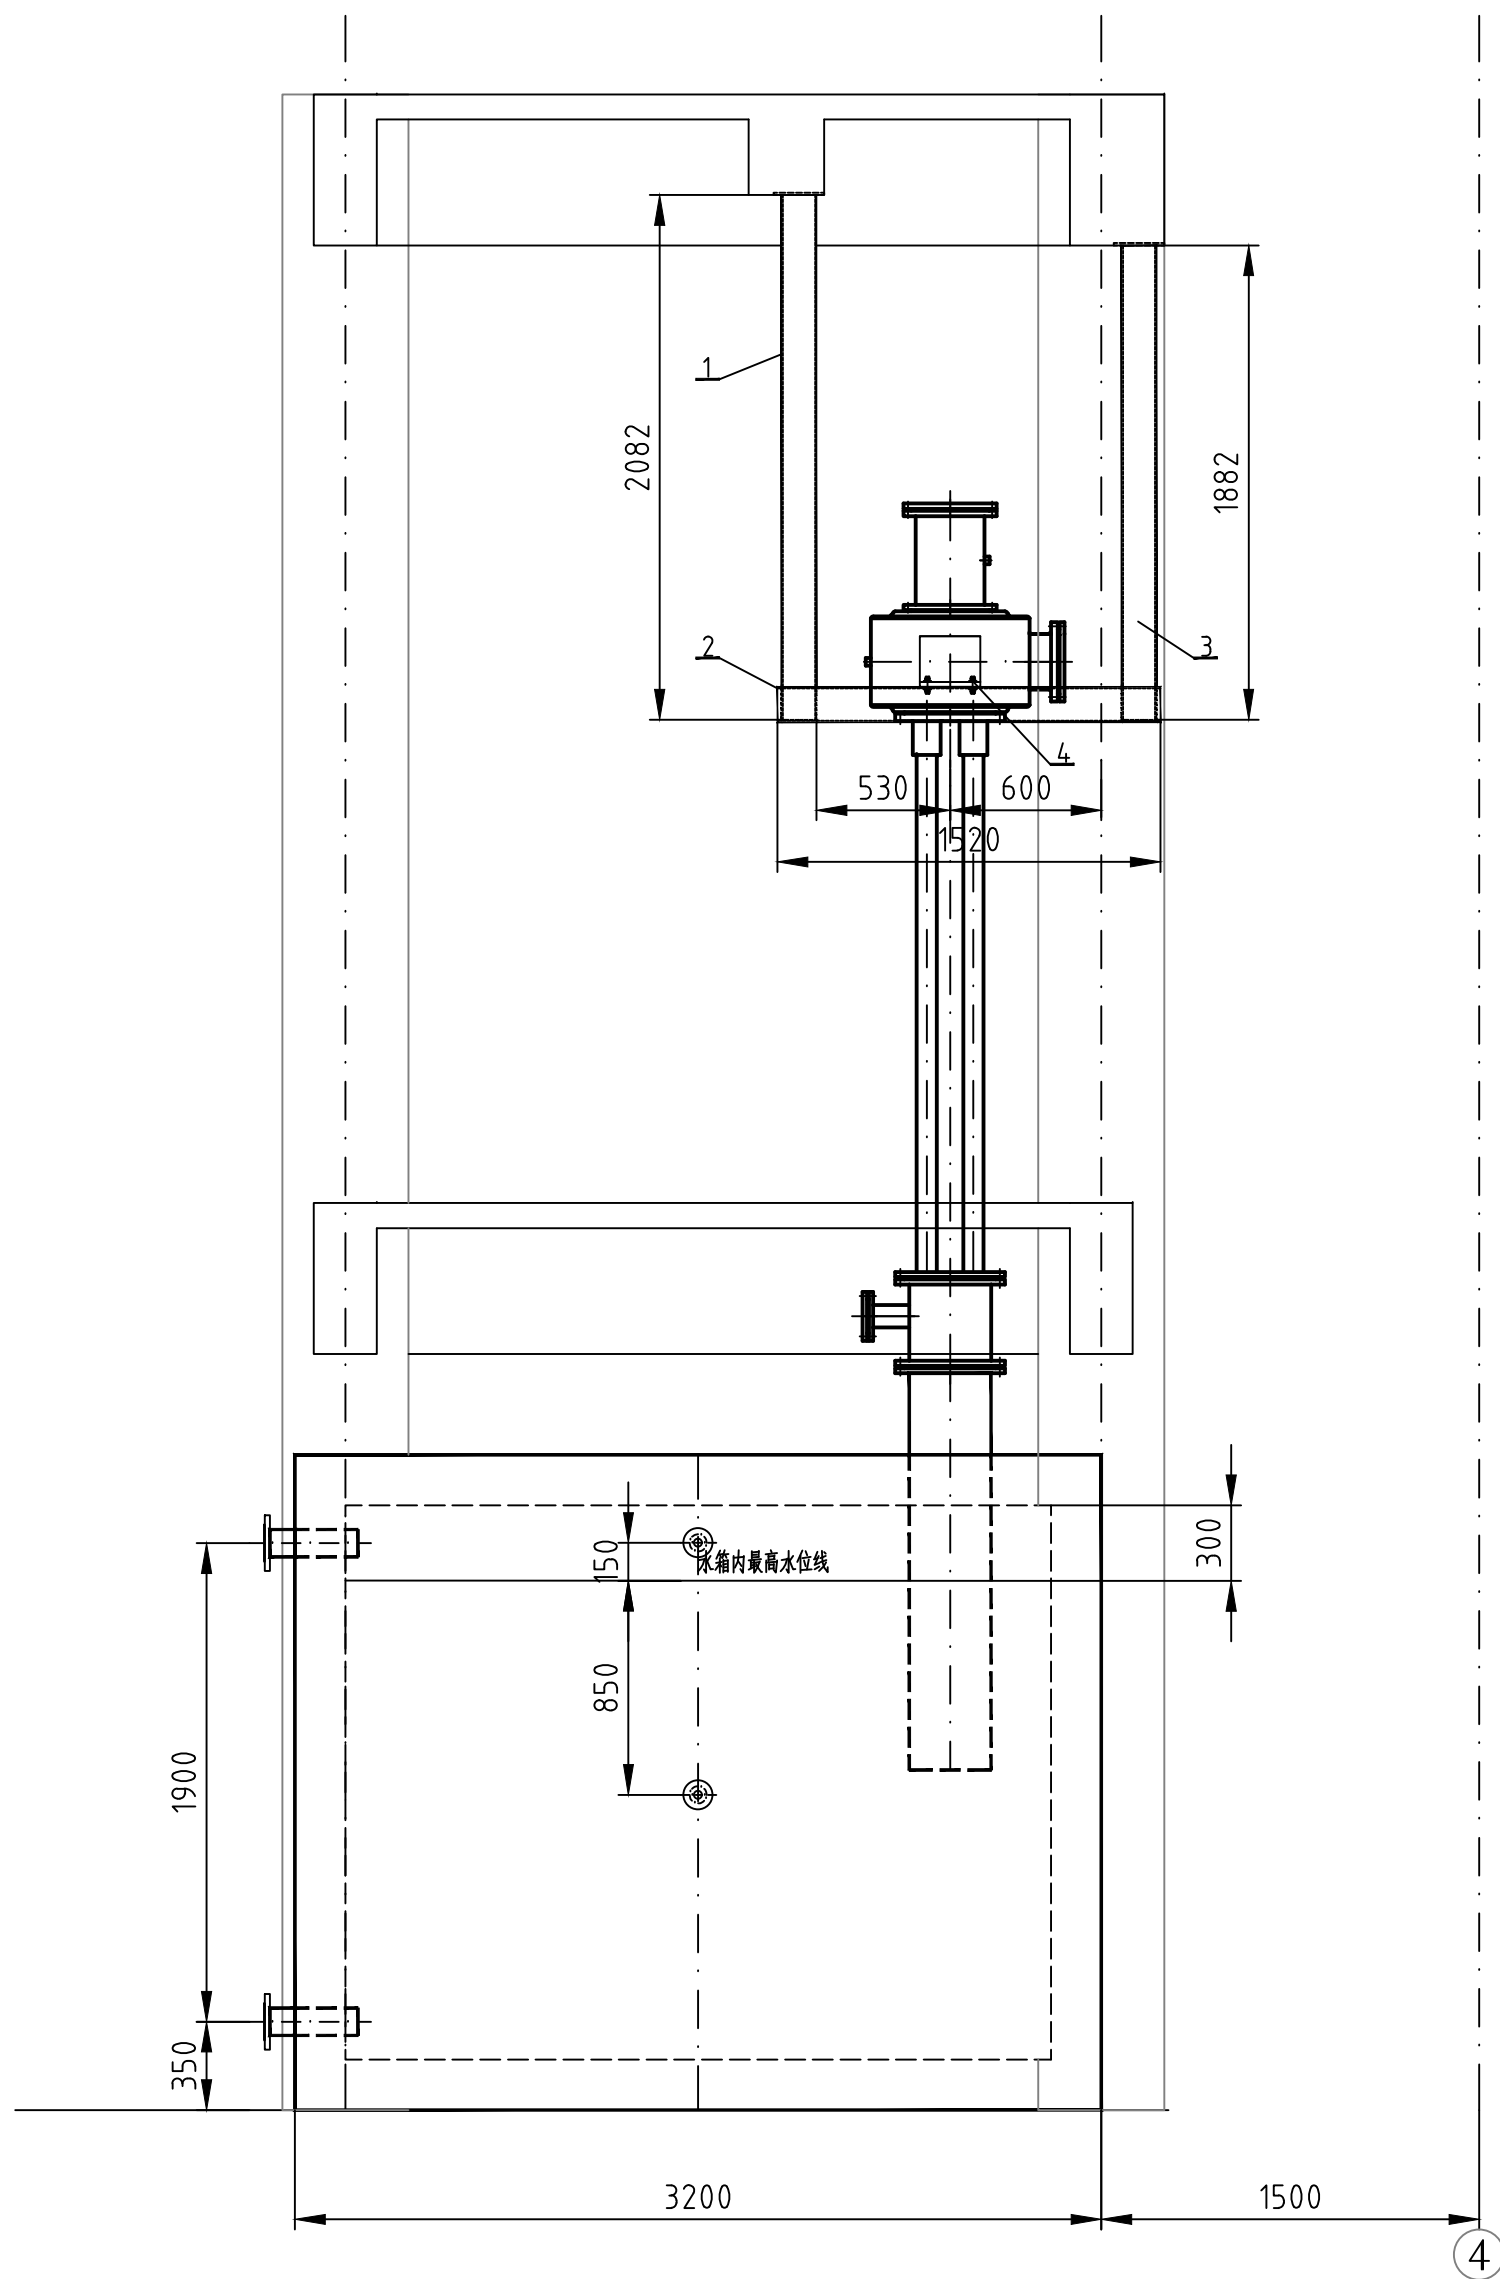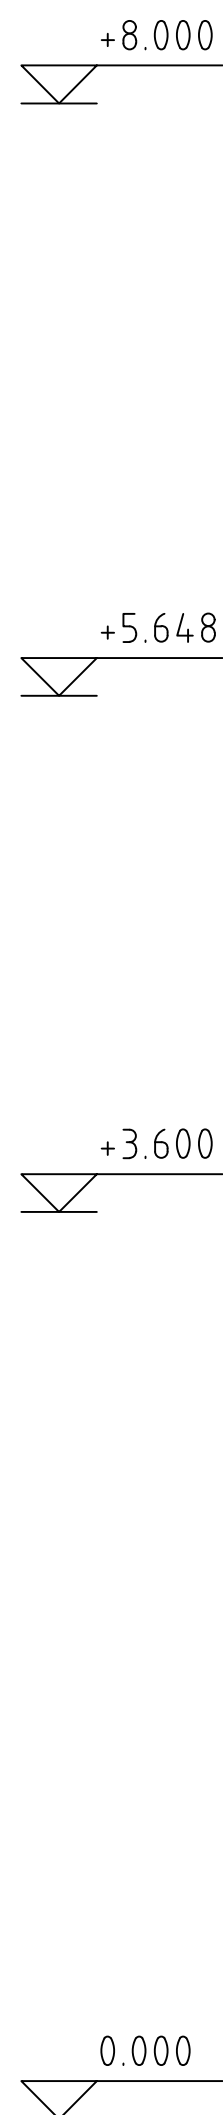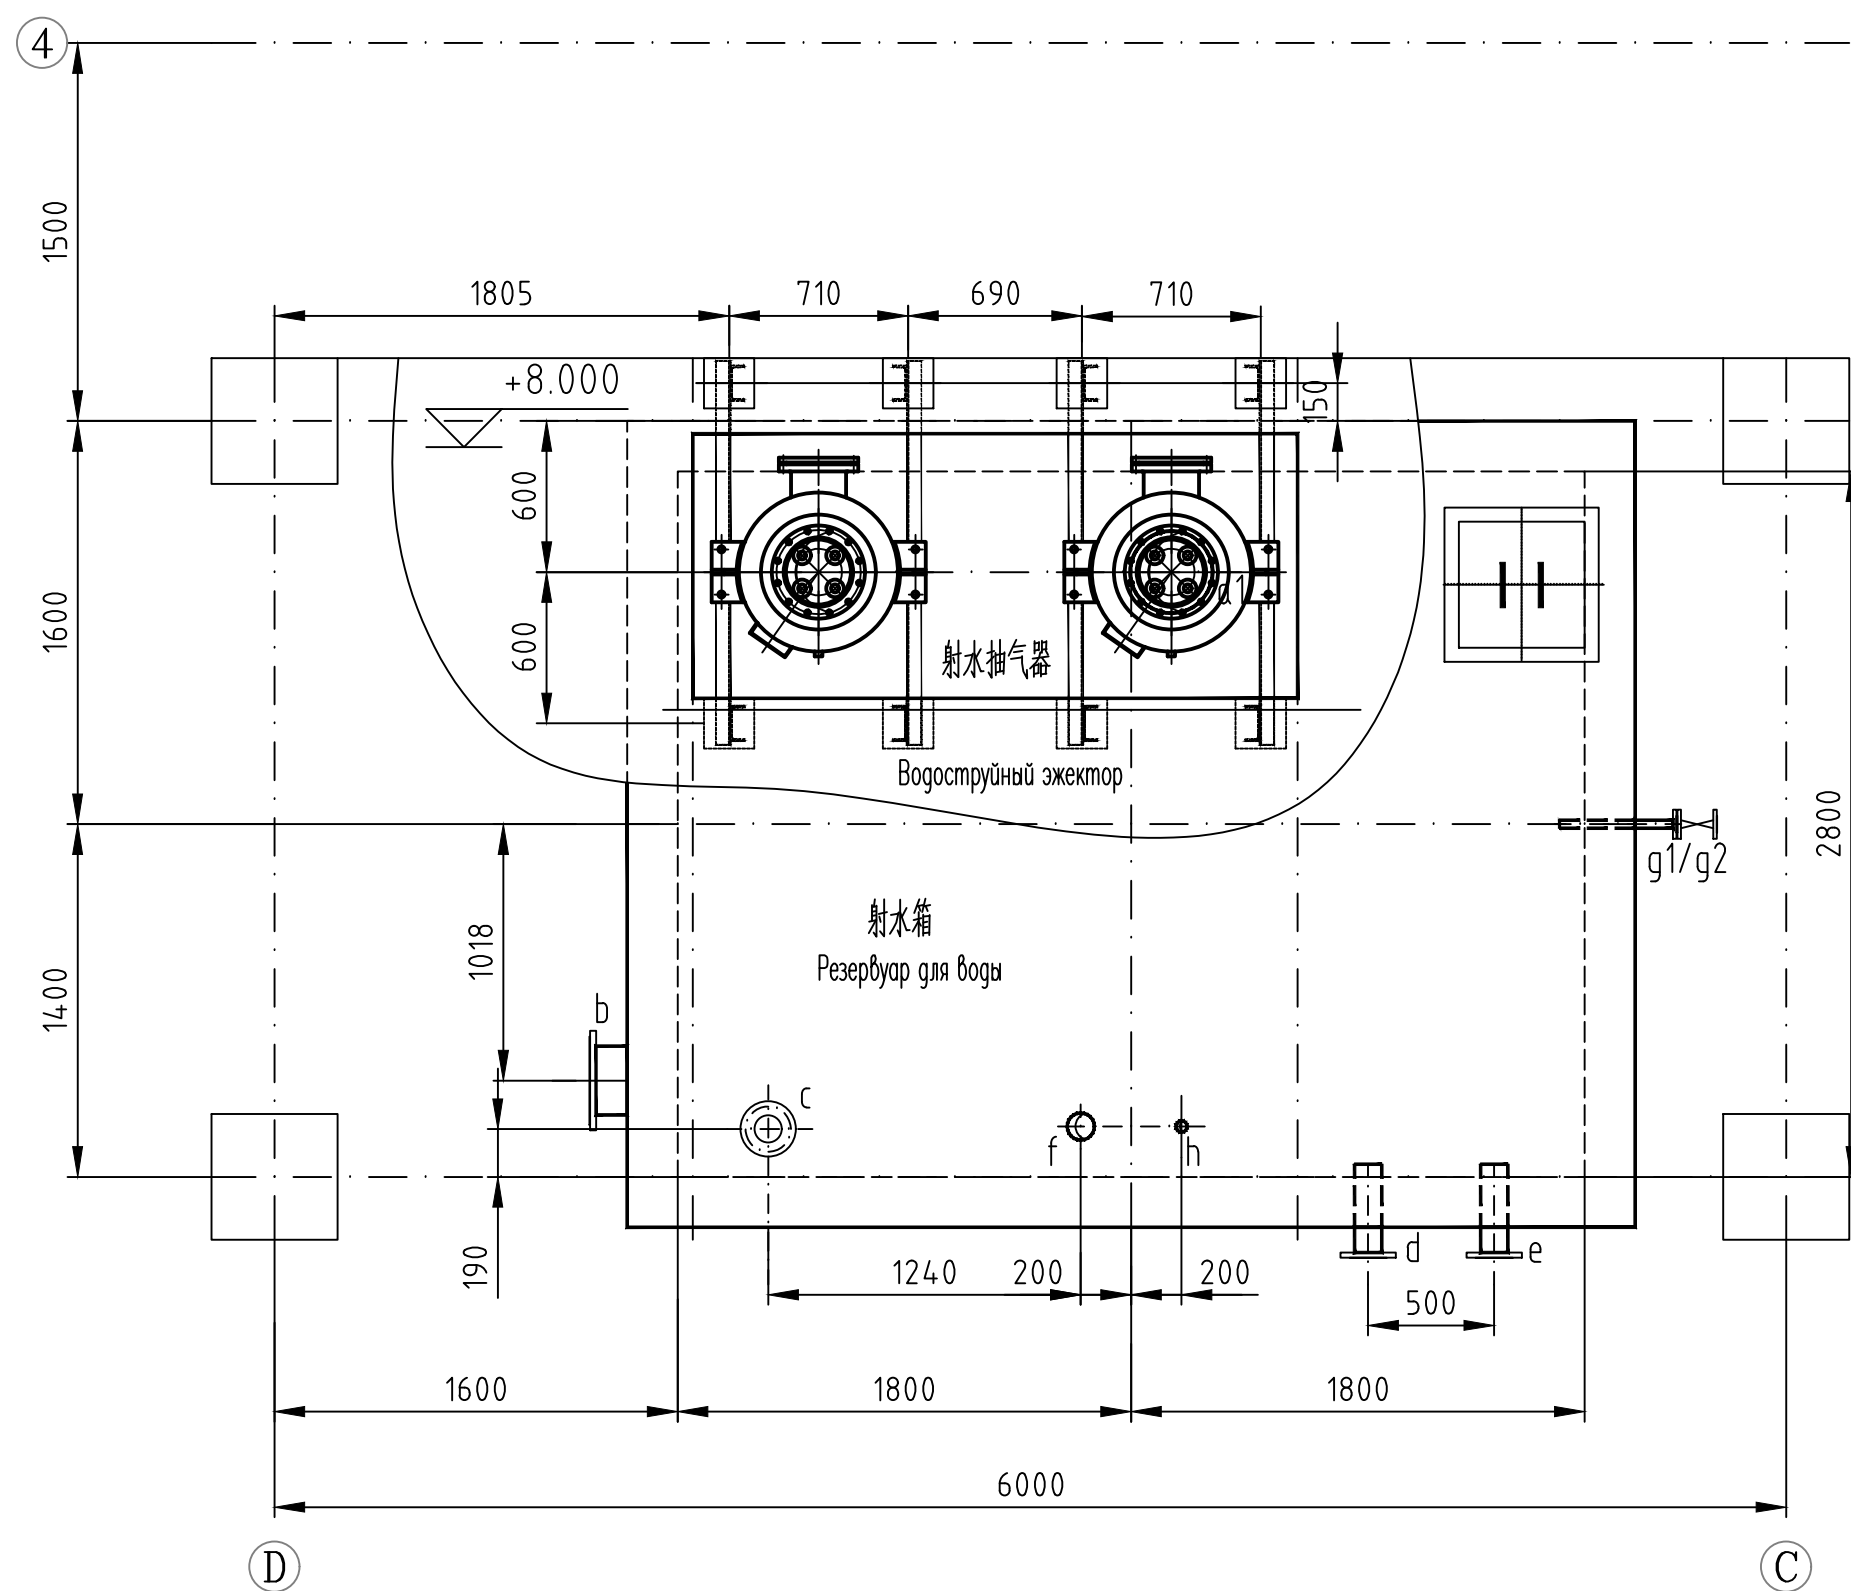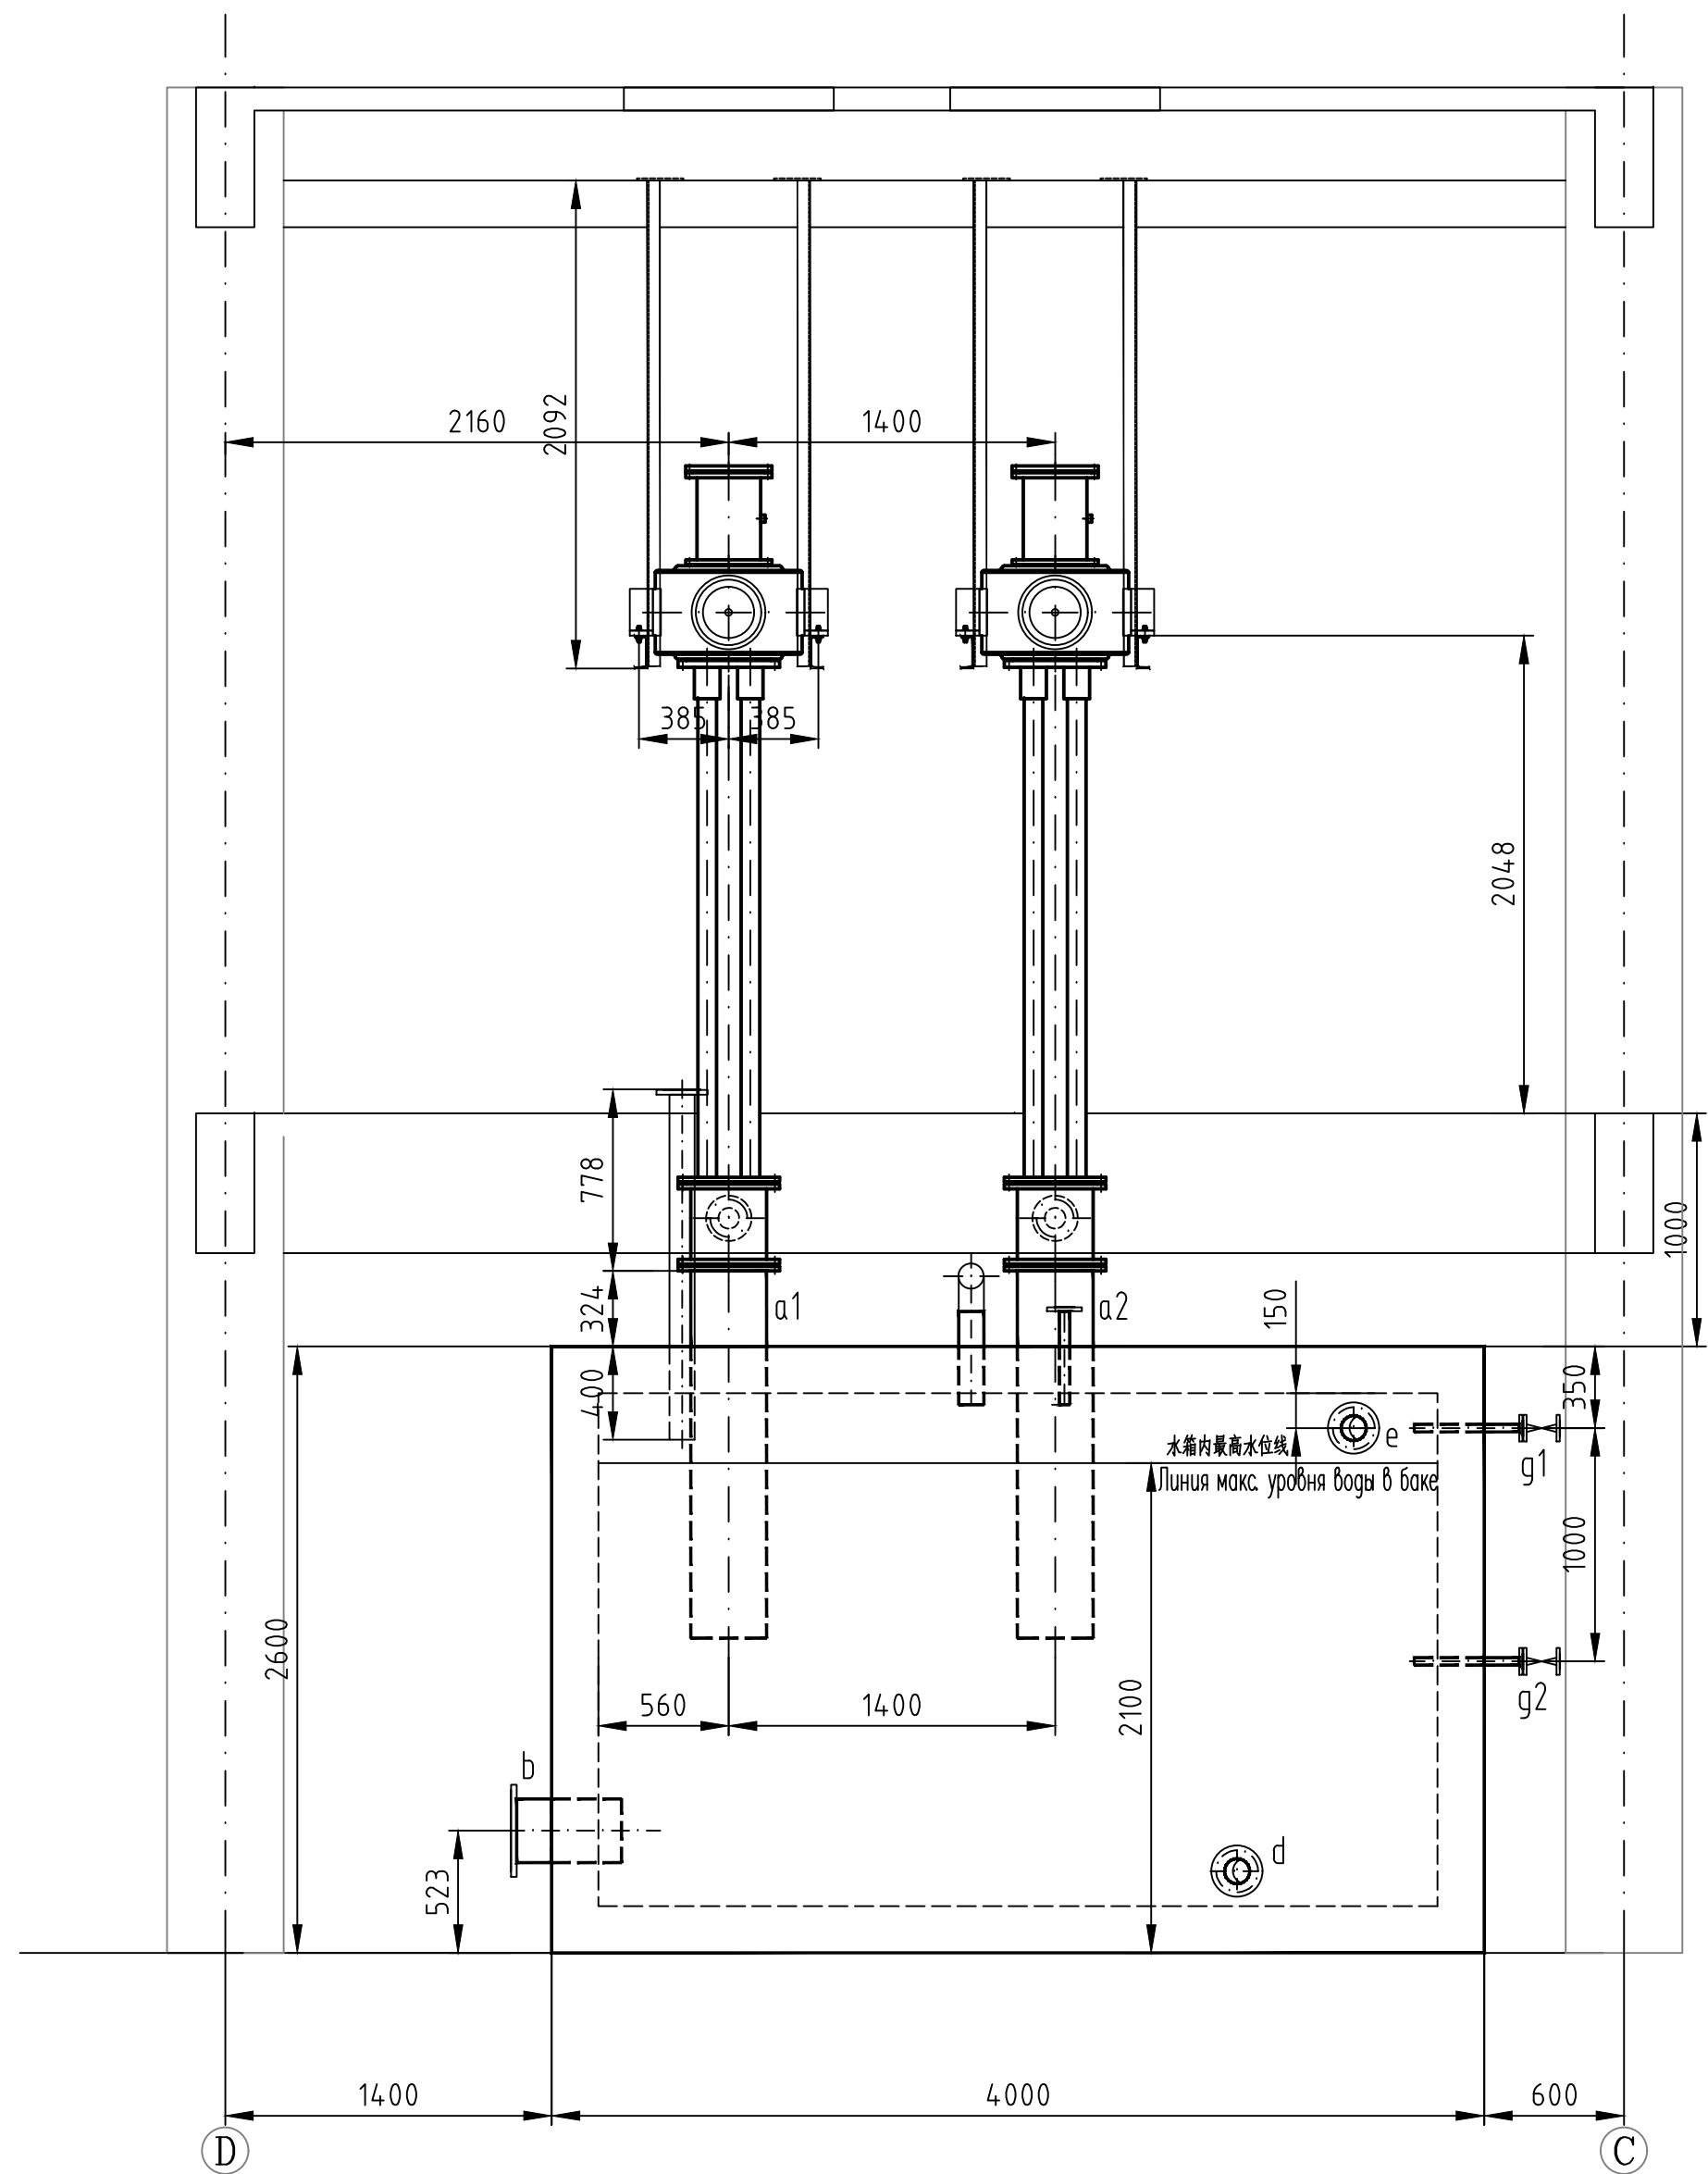

配电楼侧

管口表
Таблица патрубков

序号 № n/p	用途 Назначение	接口形式 тип соединения	公称尺寸 Условный пропуск (DN)	连接标准规格 Стандарт присоединительных размеров	备注 Примеч.
a1/a2	射水抽气器接口 Патр. отсоса пара	BW 法兰	φ325×8	GB/T8163	
b	出水口 Патр. подпит. воды	法兰 Фланц.	φ273×6	PL250(B)-10 RF HG/T20592-2009	
c	补水口 Патр. подпит. воды	法兰 Фланц.	φ108×4	PL100(B)-10 RF HG/T20592-2009	
d	排水口 Дренаж. патрубок	法兰 Фланц.	φ108×4	PL100(B)-10 RF HG/T20592-2009	
e	溢流口 Перелив. патрубок	法兰 Фланц.	φ108×4	PL100(B)-10 RF HG/T20592-2009	
f	放气口 Вентиль. патрубок	BW 法兰	φ108×4	GB/T8163	
g1/g2	液位计口 Патр. под уровнемер	法兰 Фланц.	φ32×3	截止阀 J41H-16C PL25(B)-16 RF HG/T20592-2009	
h	温度接口 Патр. под термометр	法兰 Фланц.	φ45×4	PL40(B)-16 RF HG/T20592-2009	

说明:

1. 射水箱为混凝土结构 (详见结构专业图纸), 在水箱各预埋管顶部焊接法兰, 详见管口表。
2. 射水抽气器布置在射水箱上方, 采用槽钢吊架支撑, 槽钢吊架与+8.0m预埋钢板焊接, 抽气器与槽钢吊架采用螺栓连接。
3. 射水抽气器出口法兰直接与水箱a1、a2口焊接。

Примечание:

1. Водосбор эжектора является бетонной конструкцией (см. чертежи строительной части); на верхней части всех закладных труб бака привариваются фланцы, см. таблица патрубков.
2. Водоструйный эжектор установлен над водосбором эжектора на швеллерных подвесах. Швеллерные подвесы привариваются к стальным закладным плитам отметки +8,00 м, эжектор соединяется с подвесками болтами.
3. Выходной фланец водоструйного эжектора непосредственно приваривается к патрубкам А1 и А2 водосбора эжектора.

安装材料表						
Компани спецификация						
序号 № п/п	标准号 Нормативный документ	名称 Наименование	规格 Размер	单位 Ед. изм.	数量 Количество	备注 Примечание
1	GB/T706-2016	槽钢 Швеллер	[140x60 L=2082mm	m	4	
2	GB/T706-2016	槽钢 Швеллер	[140x60 L=1520mm	m	4	
3	GB/T706-2016	槽钢 Швеллер	[140x60 L=1882mm	m	4	
4	GB/T5782-2025	六角头螺栓 Шестигранный болт	M22x65	个/套	8	配套螺母及垫圈 Комплектные гайки и шайбы

[illegible]

ALL RIGHTS RESERVED BY YDCC. THIS DRAWING MAY NOT BE ASSIGNED, TRANSFERRED, COPIED, OR DISCLOSED TO ANY THIRD PARTIES, OR USED FOR OTHER PURPOSES WITHOUT PERMISSION OF YDCC.