


会签 COSTING	姓名 NAME	签名 SIGNATURE
工艺 PR		
设备 EQ		
起运 LT		
自控 IN		
给排水 WD		
电 EL		
采暖 TH&HVAC		
建筑 AR		
结构 ST		
总图 PN		
设计 经理 DESIGN MANAGER		



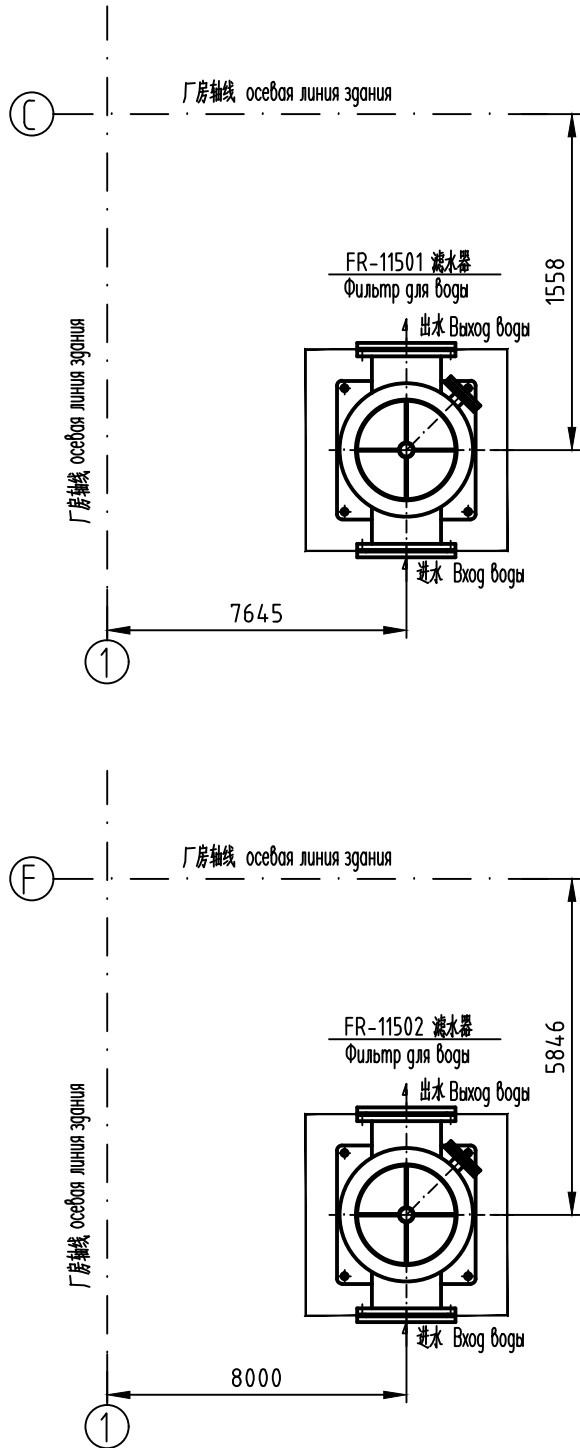


说明:

- 1.本项目中滤水器共计2台，其中FR-11501用于冷油器，FR-11502用于空气冷却器。
- 2.滤水器布置在发电厂房室内0.00m地坪上，滤水器与混凝土基础用地脚螺栓连接。

Примечание:

- 1.Количество фильтров воды в проекте – 2 шт. FR-11501 для маслоохладителя, FR-11502 для воздушного охладителя.
- 2.Фильтры воды установлены на отметке 0,00 м внутри машинного зала электростанции и закреплены на бетонном фундаменте анкерными болтами.

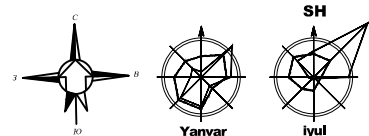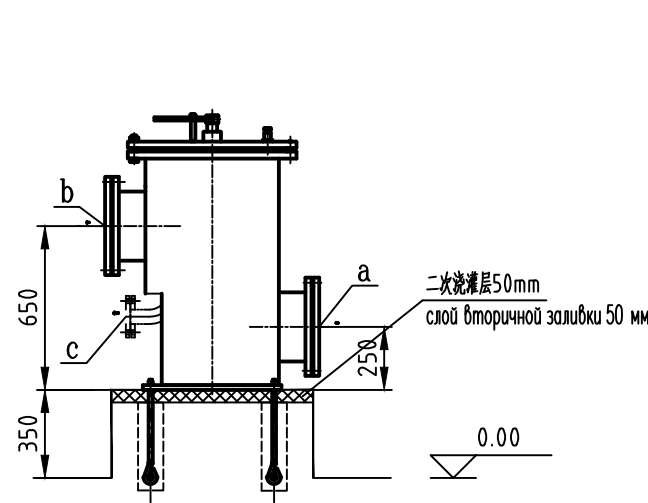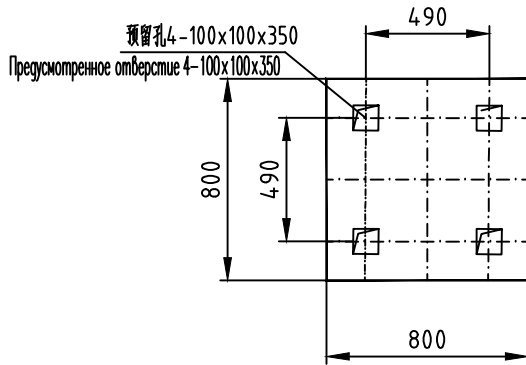

管口表 Таблица патрубков

序号 № п/п	用途 Назначение	接口形式 Тип соединения	公称尺寸 Условный проход (DN)	连接尺寸标准规格 Стандарт присоединительных размеров	密封面型式 Исполнение уплотнительной поверхности	备注 Примеч.
a	进水口 Входной патрубок воды	法兰 фланцевое	DN250	JB/T81-2015 DN250-PN10 PL RF 2	RF	
b	出水口 Выходной патрубок воды	法兰 фланцевое	DN250	JB/T81-2015 DN250-PN10 PL RF 2	RF	
c	排污口 Продувочный патрубок	法兰 фланцевое	DN50	JB/T81-2015 DN50-PN10 PL RF 2	RF	






0		供施工		2026. 6. 5	
版次 Версия		说明 Примечания		日期 Дата	
 云南化工设计院有限公司 YUNNAN DESIGN INSTITUTE OF CHEMICAL ENGINEERING CO.,LTD.		 中信建设有限责任公司 CITIC Construction Co.,Ltd.			
工程名称 НАЗВАНИЕ ПРОЕКТА		乌兹别克斯坦年产50万吨硫磺制酸项目 Uzbekistan UTMK Chemical LLC Проект завода по производству серной кислоты			工程代号 Код объекта 3147
姓名 Фамилия и имя		签名 Подпись	日期 Дата	设计项目 Проектируемый объект 余热发电 Выработка электроэнергии на утилизации тепла	
审定 Утверждение				设计阶段 Стадия проектирования 施工图 Детальное проектирование	
审核 Рассм.		余雪芳		图号 № чертежа 3147-5R115-34	
校核 Проверка		王彦斐		第1张 Лист	
设计 Проектирование		陈亮		共1张 Листы	
专业 Специальность		日期 Дата		比例 Масштаб 1: 30	
热工 Тепловая работа		2026. 6		版次 Версия 0	

云南省工程勘察设计文件（出图）专用章	
单位名称：云南化工设计院有限公司	
证书编号：5300790	
有效期至：2030年02月14日	
	
资质：化工石化医药行业甲级；建筑行业（建筑工程）甲级；环境工程设计专项（水污染防治工程，大气污染防治工程，固体废物处理处置工程）甲级；轻纺行业（日化及塑料工程，食品发酵工程）乙级；市政行业（给水工程，排水工程，城镇燃气工程，环境卫生工程）乙级；	
云南省住房和城乡建设厅2025年08月15日制发	
项目出图章编号：4202590044894 项目名称：乌兹别克斯坦年产50万吨硫磺制酸项目	
用途：施工图	

修改 REC.	
------------	--



会签 COSTING	姓名 NAME	签名 SIGNATURE
工艺 PR		
设备 EQ		
起运 LT		
自控 IN		
给排水 WD		
电 EL		
采暖 TH&HVAC		
建筑 AR		
结构 ST		
总图 PN		
设计 经理 DESIGN MANAGER		

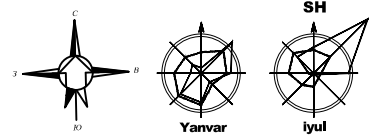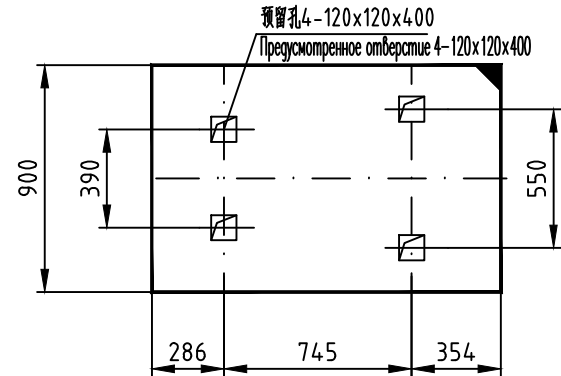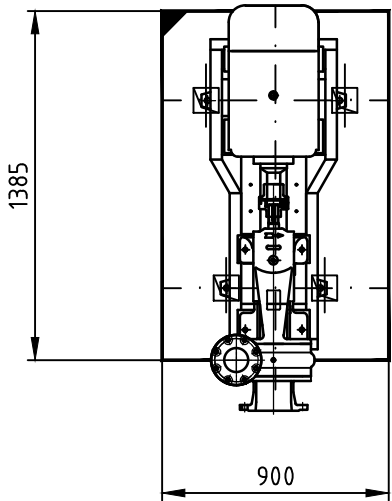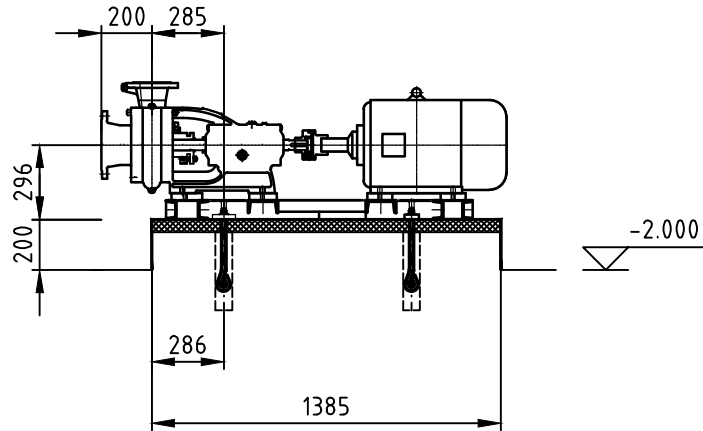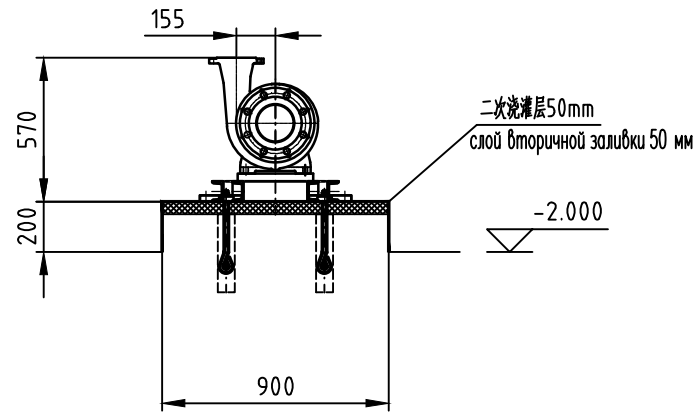

说明:

- 凝结水泵共2台，布置在汽轮发电机组基础下方地坑内。
- 本图根据业主方提供的订货资料进行绘制。
- 基础浇筑前必须与到货设备核对尺寸无误后方可进行。

Примечание:

- Два конденсатных насоса установлены в приямок под фундаментом турбоагрегата.
- Данный чертёж составлен на основании документации на поставку, предоставленной заказчиком.
- До начала бетонирования фундамента выполнить сверку размеров с оборудованием. Бетонирование разрешено только после подтверждения соответствия размеров.

云南省工程勘察设计文件（出图）专用章

单位名称：云南化工设计院有限公司

证书编号：5300790



有效期至：2030年02月14日





资质：化工石化医药行业甲级；建筑行业（建筑工程）甲级；环境工程设计专项（水污染防治工程，大气污染防治工程，固体废物处理处置工程）甲级；轻纺行业（日化及塑料工程，食品发酵烟草工程）乙级；市政行业（给水工程，排水工程，城镇燃气工程，环境卫生工程）乙级；

云南省住房和城乡建设厅2025年08月15日制发

项目出图章编号：4202590044894 项目名称：乌兹别克斯坦年产50万吨硫磺制酸项目
用途：施工图

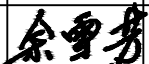
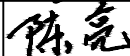
0	供施工	2026. 6. 5							
版次 Версия	说明 Примечания	日期 Дата							
 云南化工设计院有限公司 YUNNAN DESIGN INSTITUTE OF CHEMICAL ENGINEERING CO.,LTD.		 中信建设有限责任公司 CITIC Construction Co.,Ltd.							
工程名称 НАЗВАНИЕ ПРОЕКТА		工程代号 Код объекта							
Uzbekistan UTMK Chemical LLC Проект завода по производству серной кислоты		3147							
	姓名 Фамилия и имя	签名 Подпись	日期 Дата	凝结水泵安装图 Чертёж установки конденсатного насоса		设计项目 Проектируемый объект		余热发电 Выработка электроэнергии на утилизации тепла	
审 定 Утверждение						设计阶段 Стадия проектирования		施工图 Детальное проектирование	
审 核 Рассм.	余雪芳		2026. 6. 5			图 号 № чертежа		3147-5R115-35	
校 核 Проверка	王彦斐		2026. 6. 5			第 1 张 Лист			
设计 Проектирование	陈亮		2026. 6. 5	专 业 Специальность	热工 Тепловая работа	比 例 Масштаб	1: 30	共 1 张 Листы	
			日 期 Дата	2026. 6	版 次 Версия	0			

修改 REC.	

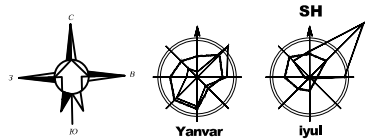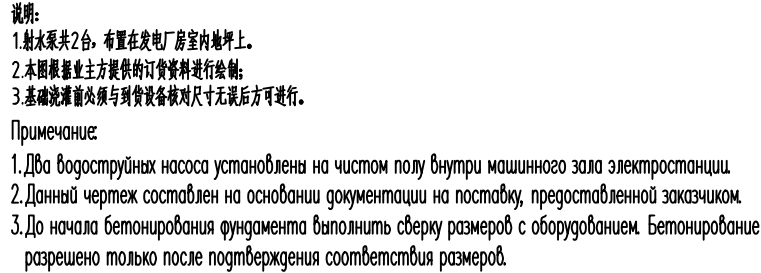

云南省工程勘察设计文件（出图）专用章		
单位名称：云南化工设计院有限公司		
证书编号：5300790		
有效期至：2030年02月14日		
资质：化工石化医药行业甲级；建筑行业（建筑工程）甲级；环境工程设计专项（水污染防治工程，大气污染防治工程，固体废物处理处置工程）甲级；轻纺行业（日化及塑料工程，食品发酵制草工程）乙级；市政行业（给水工程，排水工程，城镇燃气工程，环境卫生工程）乙级；		
云南省住房和城乡建设厅2025年08月15日制发		
项目出图章编号：4202590044894 项目名称：乌兹别克斯坦年产50万吨硫酸制酸项目 用途：施工图		

会签	姓名	签名
ORG/NO	NAME	SIGNATURE
工艺		
PR		
设备		
EQ		
起运		
L.T		
自控		
IN		
给排水		
WD		
电		
EL		
暖通		
TH/HVAC		
建筑		
AR		
结构		
ST		
总图		
PN		
设计		
经理		
DESIGN		
MANAGER		

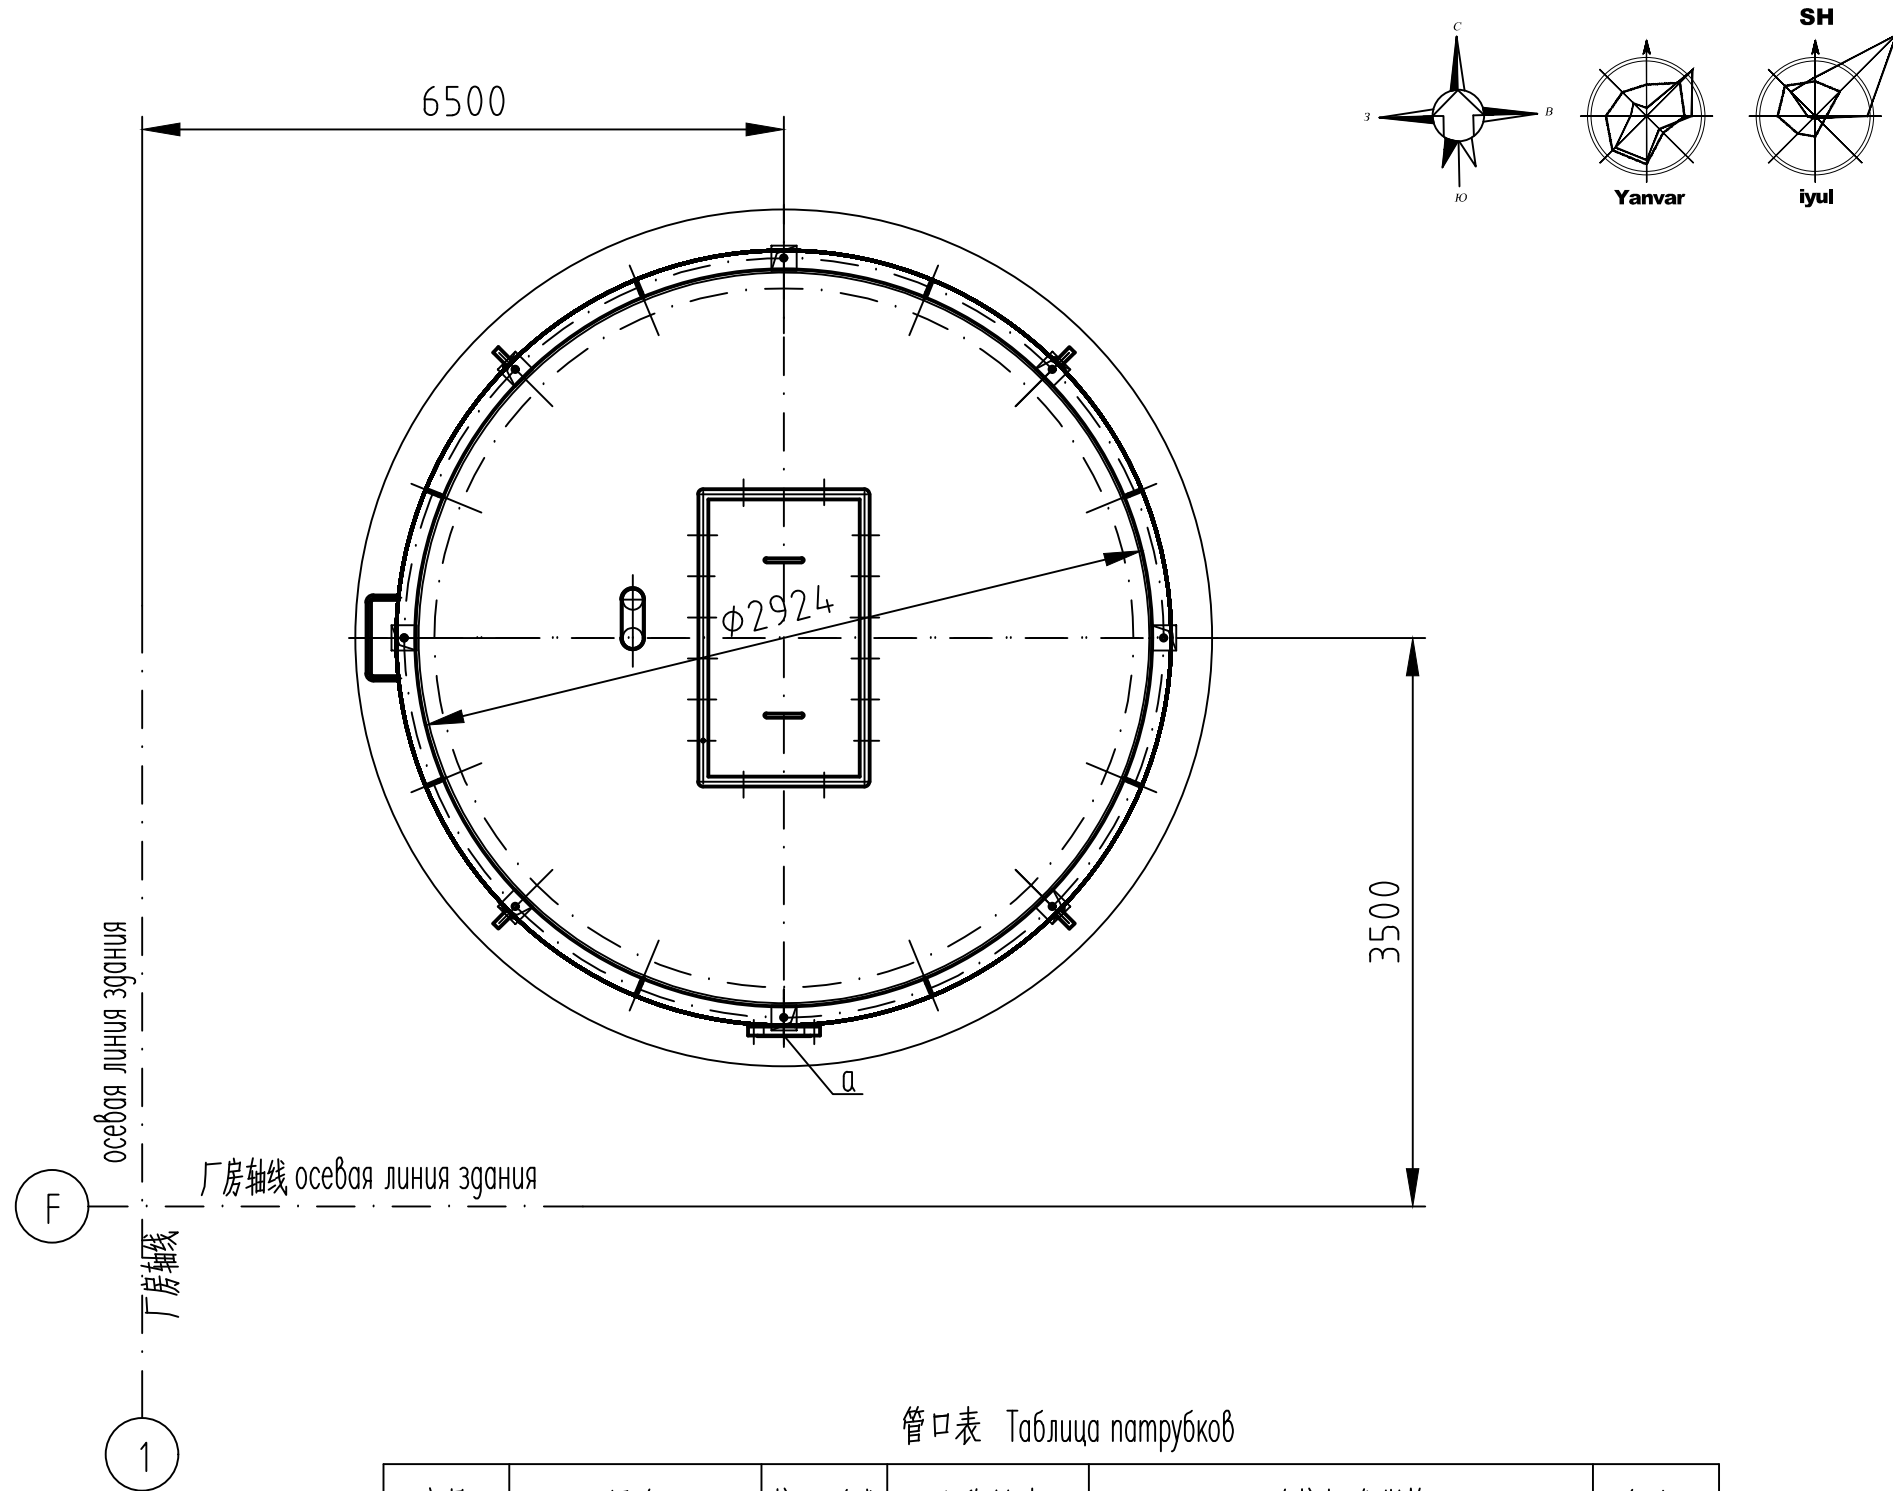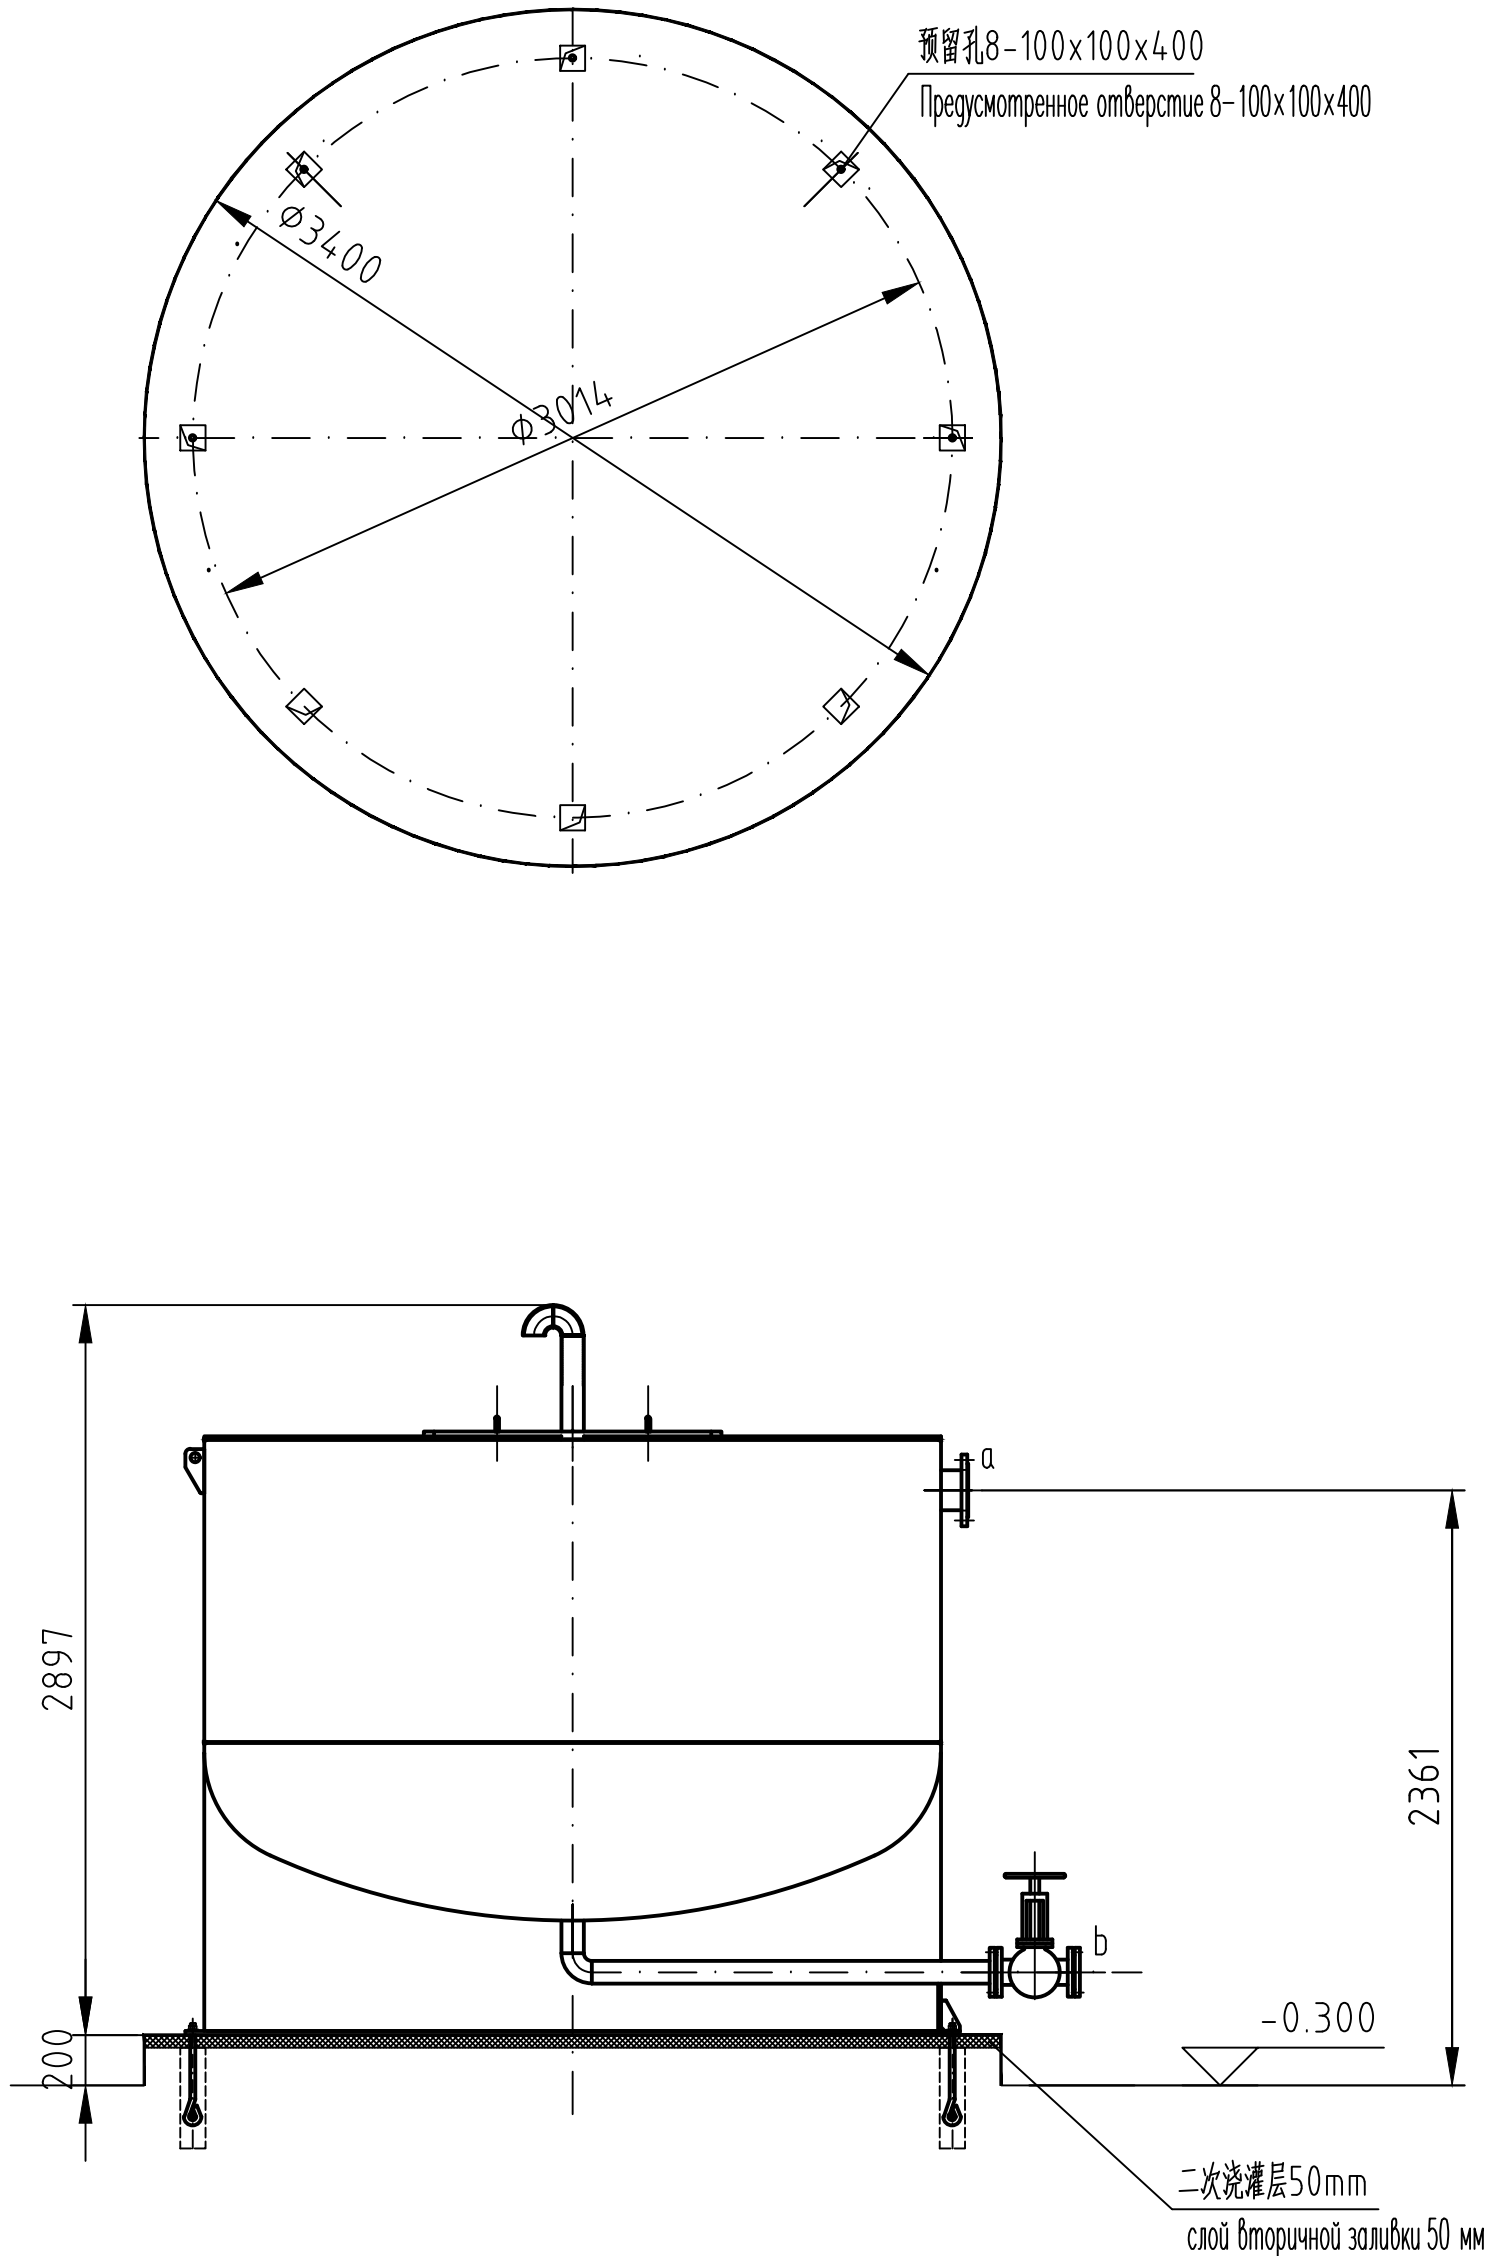



管口表 Таблица патрубков					
序号 № n/n	用途 Назначение	接口形式 Тип соединения	公称尺寸 Условный проход (DN)	连接标准规格 Станд. размеры сог.	备注 Примеч.
a	进油口 Назначение	法兰 фланцевое	$\phi 159 \times 4$	PL150(B)-16 RF HG/T20592-2009	
b	出油口 Назначение	法兰 фланцевое	$\phi 89 \times 4$	PL80(B)-16 RF HG/T20592-2009	

- 说明:
- 1.事故油箱布置在发电厂房外管廊下室外地坪上,事故油箱与混凝土基础采用地脚螺栓连接,
- Примечание:
1. Аварийный маслобак установлен на открытой площадке под эстакадой трубопроводов снаружи машинного зала электростанции и крепится к бетонному фундаменту анкерными болтами.

修改	
REC.	

云南省工程勘察设计文件(出图)专用章	
单位名称: 云南化工设计院有限公司	
证书编号: 5300790	
有效期至: 2030年02月14日	
资质: 化工石化医药行业甲种; 建筑行业(建筑工程)甲种; 环境工程设计专项(水污染防治工程、大气污染防治工程、固体废物处理处置工程)甲种; 轻纺行业(日化及塑料制品工程、食品发酵酿造工程)乙种; 市政行业(给水工程、排水工程、城镇燃气工程、环境卫生工程)乙种;	
云南省住房和城乡建设厅2025年08月15日颁发	
项目出图章编号: 4202590044894 项目名称: 乌兹别克斯坦年产50万吨硫磺制酸项目	
用途: 施工图	

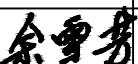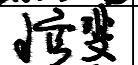

0		供施工		2026. 6. 5	
版次 Версия		说明 Примечания		日期 Дата	
 云南化工设计院有限公司 YUNNAN DESIGN INSTITUTE OF CHEMICAL ENGINEERING CO., LTD.				 中信建设有限责任公司 CITIC Construction Co., Ltd.	
工程名称 НАЗВАНИЕ ПРОЕКТА		乌兹别克斯坦年产50万吨硫磺制酸项目 Uzbekistan UTMK Chemical LLC Проект завода по производству серной кислоты			工程代号 Код объекта 3147
	姓名 Фамилия и имя	签名 Подпись	日期 Дата	设计项目 Проектируемый объект 余热发电 Выработка электроэнергии на утилизации тепла	
审定 Утверждение				设计阶段 Стадия проектирования 施工图 Детальное проектирование	
审核 Рассм.	余雪芳		2026. 6. 5	图号 № чертежа 3147-5R115-37	
校核 Проверка	王彦斐		2026. 6. 5	第1张 Лист	
设计 Проектирование	陈亮		2026. 6. 5	共1张 Листы	
专业 Специальность		热工 Тепловая работа		比例 Масштаб	Типовая рамка чертежа (Версия 2020)
日期 Дата		2026. 6	版次 Версия	0	