


Спецификация на упоры

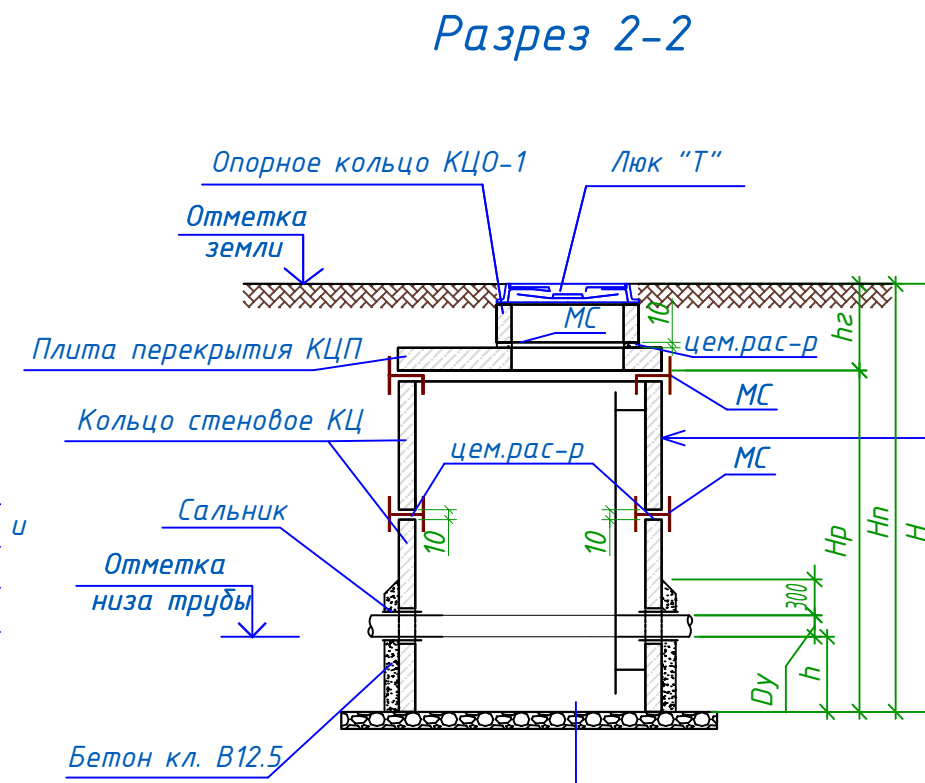

Битумная мастика за 2 раза
по битумной грунтовке
Заделка швов цементно-
песчаным р-ром 1:2.
Стена колодца.
Обмазка битумом за 2 раза
внутренних поверхностей стен и
перекрытия по одному слою
битумной грунтовки.

Угла поворота	Диаметр трубы	Размеры упора, мм					Кол.	Объем бетона наед .
		h ₂	a	H	L	B		
15°	200	100	220	530	660	550	–	0.33м³
30°		100	330	530	600	640	–	0.39м³
45°		100	350	530	630	830	–	0.49м³
60°		150	290	530	690	980	–	0.57м³
90°		200	–	530	1000	900	–	0.24м³

КЦО-1

Люк "Т"

КЦ

КЦП


Узел-1

Стремянка



Сальник

Ду

Узел-2

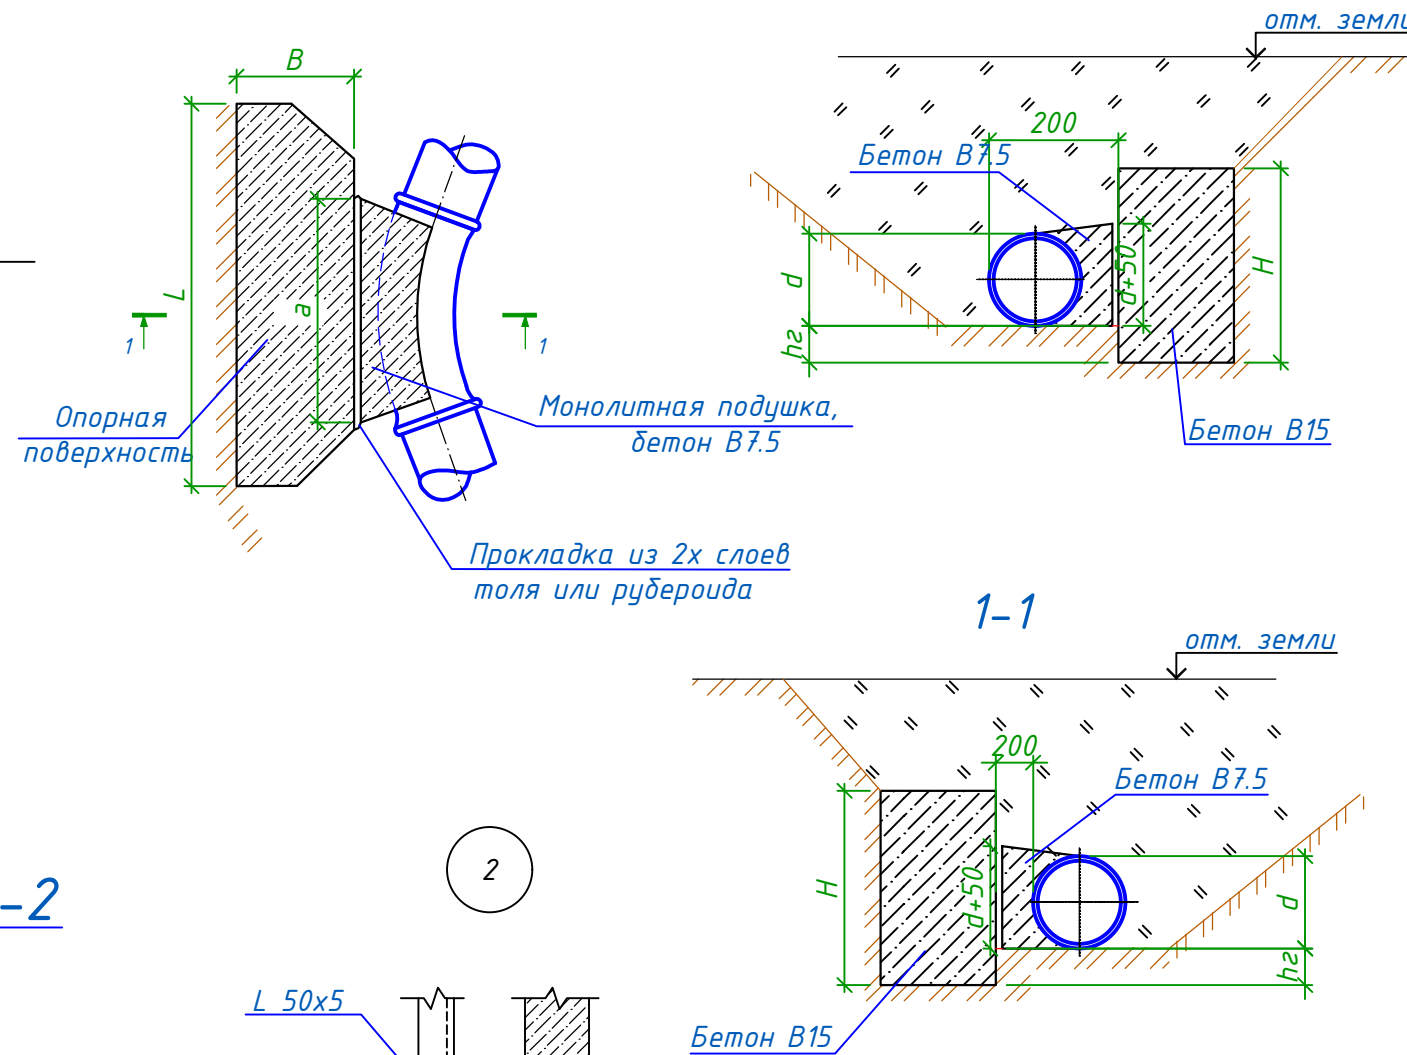


УПОР ГОРИЗОНТАЛЬНЫЙ

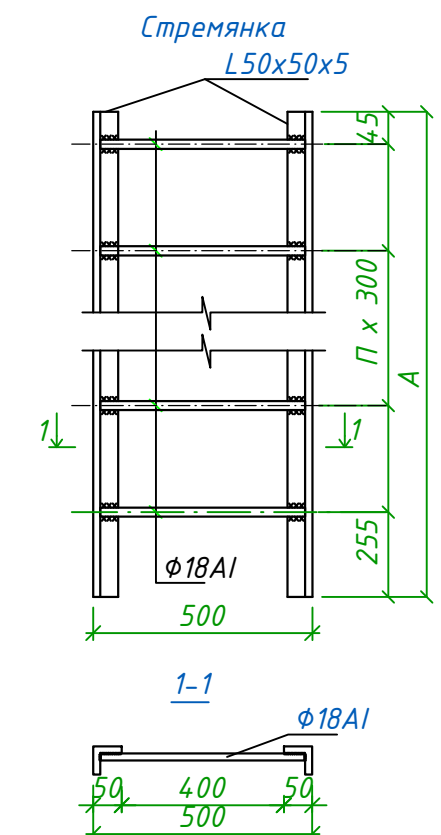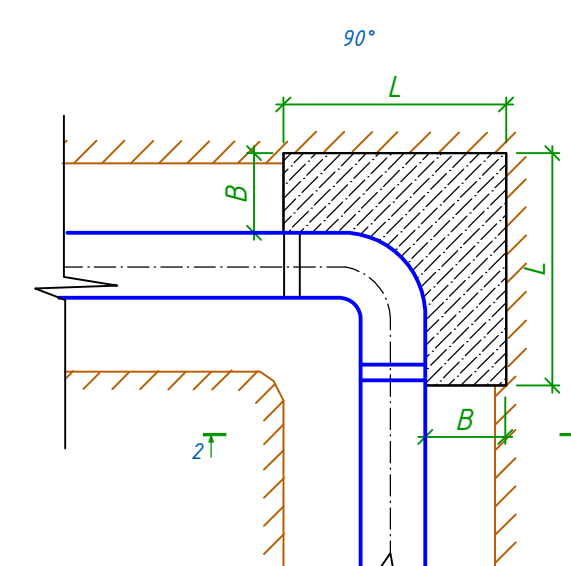

Примечание
1. Боковые поверхности опор, соприкасающиеся с грунтом, обмазать горячим битумом за 2 раза по грунтовке.


Technical drawing of a bracket (Стремянка) attached to a curved wall. The bracket consists of a horizontal base plate labeled "L 50x5" and a vertical support. The wall thickness is indicated as "-80x5". The distance from the wall to the center of the bracket is 80 mm. The total height of the bracket assembly is 100 mm.

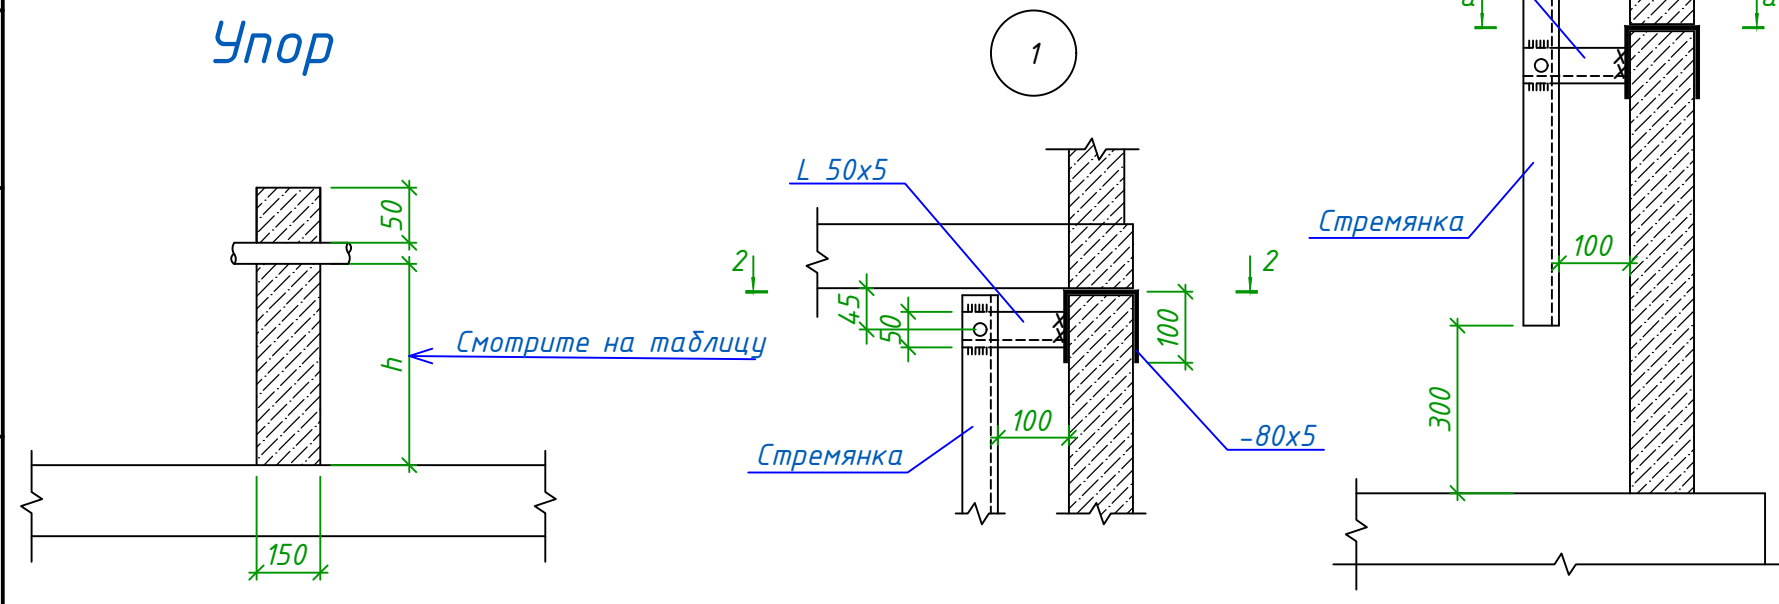


						НВ		
						РП «Подводящий газопровод среднего давления к заводу по производству серной кислоты в Кармановском районе Навоийской области»		
Изм.	Колуч.	Лист	№ док.	Подпись	Дата	Стадия	Лист	Листов
					2025	РП	4	6
Директор	Содиқов	С				Наружные сети водопровода		
Разраб.	Айдукуталиев					Стремянка Упоры.Разрез 1-1; 2-2; а-а. Узел 1,2		
						ООО "SAMANDAR IDEAL GAZ" Ташкент 2025 г.		

NN колодцев по проекту	Отметка сущ. земли	Отметка низа трубы	Размеры колодца, мм					Диаметр трубопровода мм				Размеры колодцев в плане , мм		Строительные конструкции Плиты перекрытий										Кольца Серия 3.900-3.87		Арматура вес кг		Сальники ГОСТ 10704-91, шт						Ляк " Т" по ГОСТ 3634-89, шт	Стремянка			*Бетон кл.В15, м3	Щебеночная подсыпка проп.таб. блочном м3					
														Dy	dy	φ 10A/III	φ 8A/I	dy=100	dy=250	dy=350	dy=400	dy=500	dy=700			Марка	Кол-во	Вес , кг.																
		A	B	C	D	H	I	II	III	IV	A	Б	П21-5А											П21-5В	П24-5А				П24-5В	П26-5А	П26-5В	П21-5Б	П24-5Б		П26-5Б	П21-5В	П24-5В			П26-5В	П21-5Б	П24-5Б	П26-5Б	К10-1
		Точка подключения №1	
1	380.56	378.98	360	2000	780	2360	2760	-	426	-	-	3000	3000	-	-	-	-	-	-	-	-	-	-	2	-	-	1	1	-	-	445.2	15.4	-	-	-	-	1	-	1	C-3	1	19.50	11.2	1.44

380.56

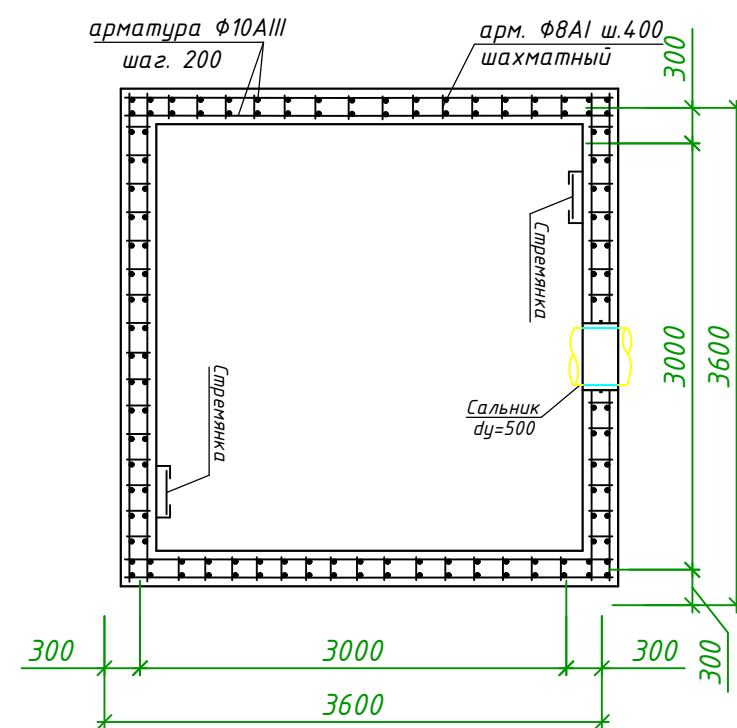

Точ.п №1

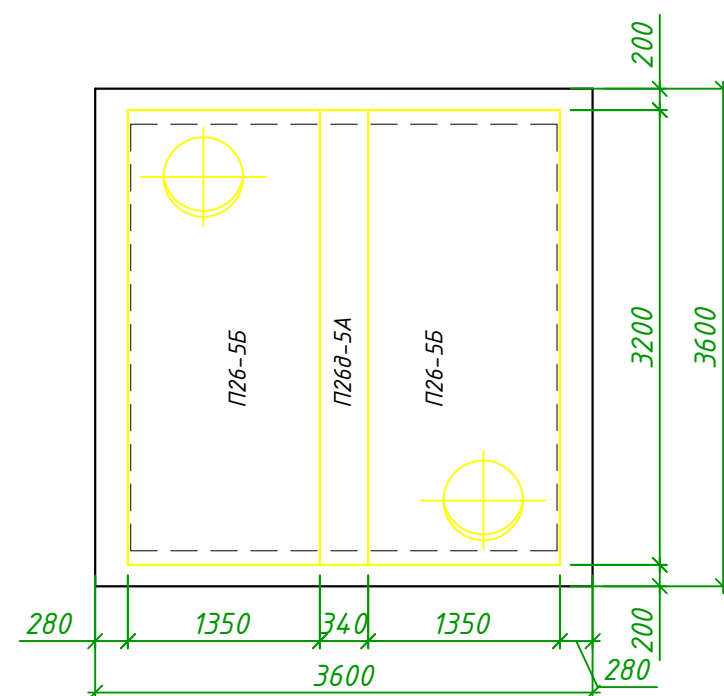

Обмазка битумом за 2 раза наружных поверхностей соприкасающихся с грунтом
Стена колодца

Отм. земли

КЦО-1

Люк "Т"

арматура $\Phi 10AIII$

Плита покрытия

Бетон В3.5

Стремянка

Сальник

Отметка
низа трубы

100 300 A, Б 300 100 100

Обмазка горячим битумом за 2 раза
Днище монолитное $t=300$ мм Бетон кл.В15*
Щебеночная подготовка протолитая битумом $t=100$ мм

арматура $\Phi 10AIII$
ш. 200

арм. $\Phi 8AI$ ш. 400
шахматный

арматура $\Phi 10AIII$
ш. 200

300
25 25

300

100 300 150 300 100

4,5

Technical drawing of a roof detail showing a cross-section of a roof with a central skylight. The drawing includes labels for "Отметка земли" (Ground level), "Люк Т" (Skylight T), "КЦО-1" (KCO-1), "арматура Ø10AIII" (reinforcement Ø10AIII), and "Плита покрытия" (Cover plate). Dimensions are given as 1000 for the width of the roof sections and 200 for the height of the cover plate.

[illegible]

Инв. № подл.	Подпись и дата	Взам. инв. №

Ведомость рабочих чертежей основного комплекта.		
Лист	Наименование	Примеч.
1	Общие данные	
2	План с сетями В0	
3	Продольный профиль В0	
4	Стремянка Упоры. Разрез 1-1; 2-2; а-а. Узелб 1,2	
5	Укладка труб в траншею Соединительные элементы МС разрез 3-3	
6	Прямоугольные колодец Точ.п №1	
7		
8	Ведомость ссылочных и прилагаемых документов.	
Обозначение		Наименование
		Примеч.
		Ссылочные документы.
КМК 3.05.04-97		Наружные сети и сооружения водоснабжения
		и канализации.
КМК 2.04.02-19		Водоснабжение. Наружные сети и сооружения.
КМК 3.02.01-97		Земляные сооружения, основания
ГОСТ 21.704-2011		Правила выполнения рабочей документации
		наружных сетей водоснабжения и канализации
ТП 901-09-11.84**		Колодцы водопроводные
ТП 902-09-22.84**		Колодцы канализационные
		Прилагаемые документы.
НВ.С		Спецификация оборудования и материалов.
		на 2-листах

Общие указания

Проект раздела НВ для объекта РП «Подводящий газопровод среднего давления к заводу по производству серной кислоты в Кармановском районе Навоийской области» выполнен на основании следующих материалов и данных:

а) Генплана участка застройки М 1:500;

б) Проекта вертикальной планировки и благоустройства М 1:500;

в) Заключения об инженерно-геологических условиях площадки строительства, выполненного -сейсмичность баллов -8

-глубина промерзания грунтов-0,7м. от поверхности земли.

-тип грунтовых условий по просадочности - I.

Водопровод В1.

Водоснабжение территории осуществляется от существующий насосной станции. Сеть В0 монтируется из стальных электросварных труб диаметром ф219х5 мм по ГОСТ 10704-91.

На сети устраиваются колодцы с отключающей арматурой из сборных железобетонных элементов по ТПР 901-09-11.84.

Монтаж трубопроводов



При монтаже трубопроводов водоснабжения и канализации необходимо составлять освидетельствования скрытых работ согласно КМК 3.01.01-97 по следующим видам работ с оставление акта:

- подготовка основания по трубопроводы;
- устройству упоров;
- противокоррозионная защита трубопроводов;
- герметизация мест прохода трубопроводов через стенки колодцев и камер;
- засыпка трубопроводов с уплотнением;
- соответствие уклона трубопровода проекту;
- прямолинейность участков "на свет";
- испытание трубопроводов и сооружений.

						НВ			
						РП «Подводящий газопровод среднего давления к заводу по производству серной кислоты в Кармановском районе Навоийской области»			
Изм.	Кол.уч.	Лист	№док.	Подпись	Дата	Наружные сети водопровода	Стадия	Лист	Листов
Директор	Содилов С.				2025		РП	1	6
Разраб.	Абдумуталиев						ООО "SAMANDAR IDEAL GAZ" Ташкент 2025 г.		
						Общие данные			

План с сетями В0 М1:500

Футляр Сечение

 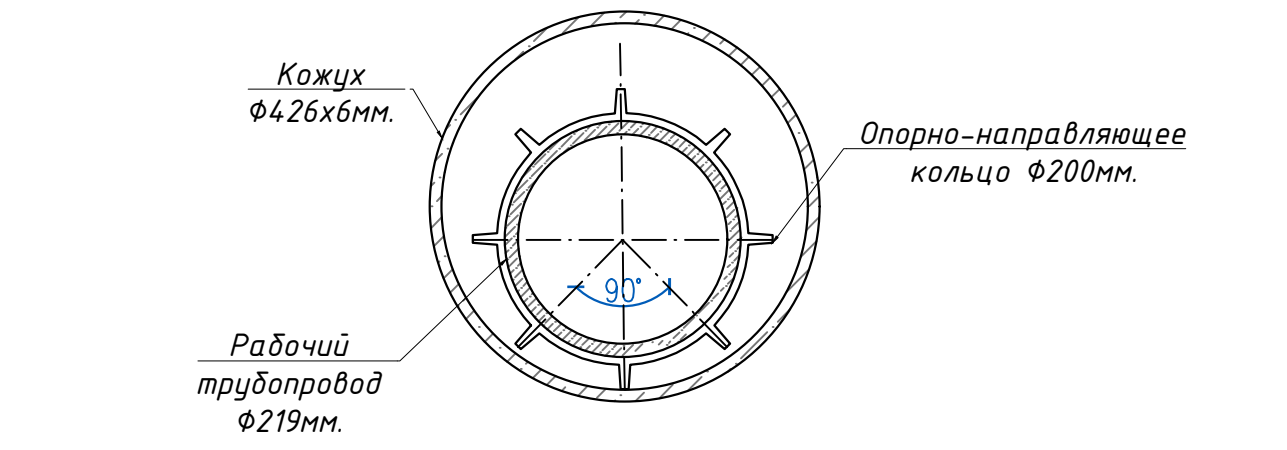

При производстве земляных работ вызвать представителей организаций эксплуатирующих инженерно-подземные коммуникации.			НВ		
Договор	ООО "GEO PREMIUM SERVICE"		2026 й. II		
Объект:	Тошкент вил.		Заказчик:		
Изм.	получ.	Лист	N док.	Подпись	Дата
Директор	Азимова Ф.				2025
Топограф	Илхомов А.				
Топографическая съемка масштаба 1:500			сечение рельефа 0.5м		
система координат СК-1942			Стация Лист-1 Листов-1		
Изм. Колуч			Лист № док.		
Директор			Подпись Дата		
Разраб.			Идентификация		
РП «Подводящий газопровод среднего давления к заводу по производству серной кислоты в Кармановском районе Навоийской области»			Наружные сети водопровода		
План с сетями В0 М1:500			ООО "SAMANDAR IDEAL GAZ" Ташкент 2025 г.		