

会签 Совм. подп.	姓名 Фамилия и имя	签名 Подпись
工艺 Технология		
设备 Оборудование		
起运 Отгрузка		
自控 Автоматический контроль		
给排水 ВиК		
电 Электричество		
热暖 Теплообеспечение и отопление		
建筑 Архитектура		
结构 Конструкции		
总图 Генплан		
设计经理 Директор по проектированию		

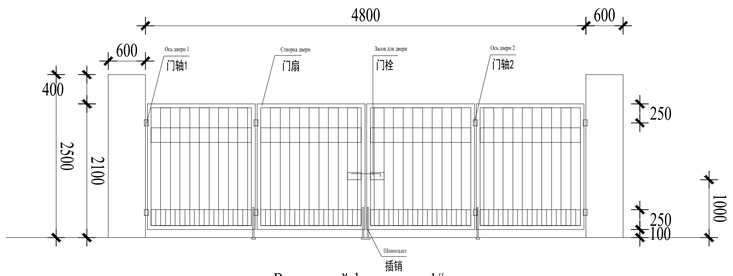


Внутренний фасад ворот 1#

1#门内立面图

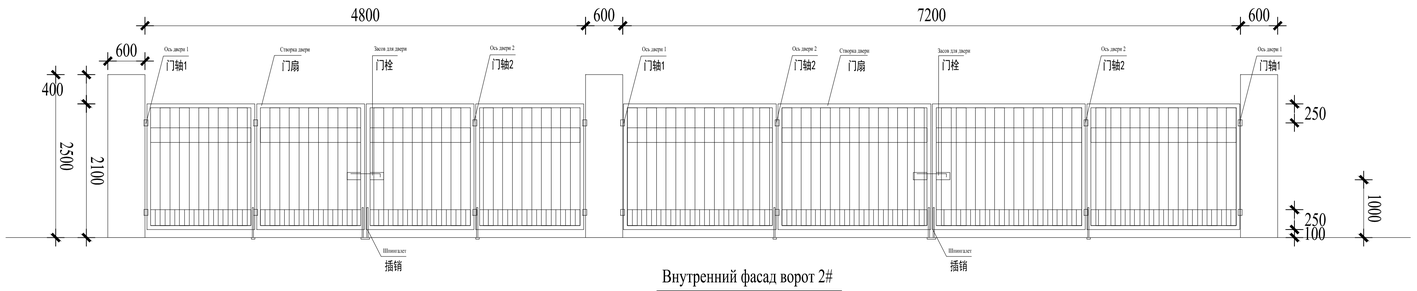


Внутренний фасад ворот 2#

2#门内立面图

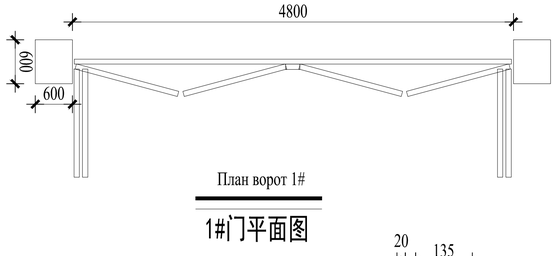


План ворот 1#

1#门平面图

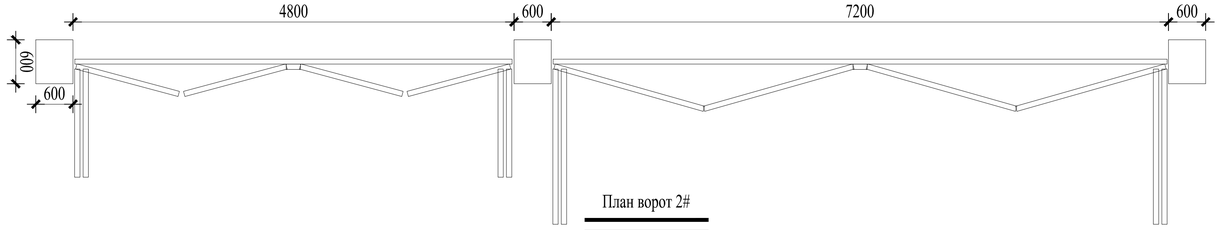


План ворот 2#

2#门平面图

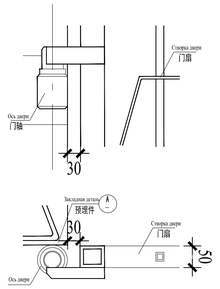


Детальный чертеж оси двери 1

门轴1大样图

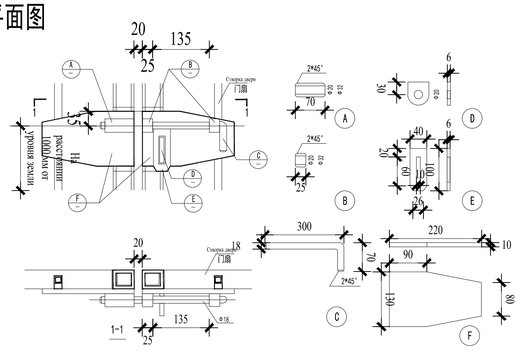


Детальный чертеж засова для двери

门栓大样图

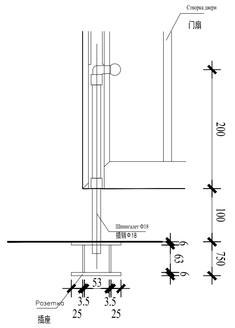


Детальный чертеж шпингалета

插销大样图

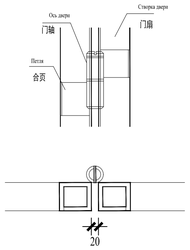


Детальный чертеж оси двери 2

门轴2大样图

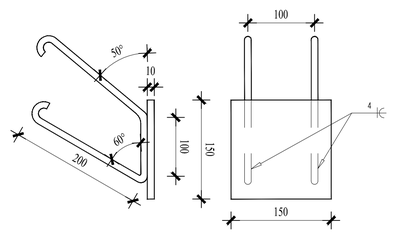


Детальный чертеж закладных деталей оси двери

门轴预埋件大样图

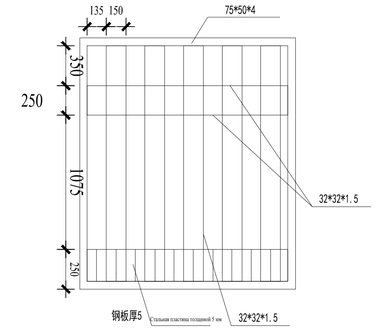


Детальный чертеж створки двери

门扇大样图

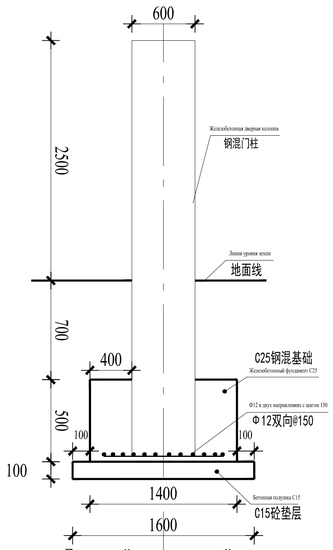

Детальный чертеж дверной колонны

门柱大样图

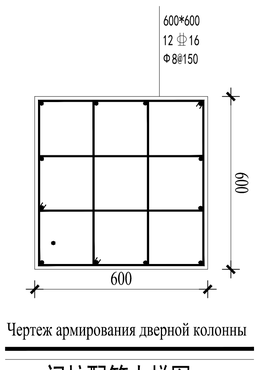

Чертеж армирования дверной колонны

门柱配筋大样图

说明：

1. 厂区东侧物流出入口及人流出入口处大门采用伸缩门，后期根据实际开口大小整套采购即可；厂区西侧火车轨道入口处大门采用钢制折叠无轨大门，大门具体尺寸参照本图中平面图及大样图。
2. 本图中门扇及五金零件采用电弧焊接，焊缝须挫平磨光。
3. 钢门表面要做防锈防腐处理，具体采用何种防锈工艺由业主与施工方确认。
4. 当基础置于回填土内时，需要对基础下回填土进行处理。要求开挖至基础下1米，对其下回填土碾压2-3遍，后采用级配砂石回填至设计标高。回填应分层夯实，每层厚不大于300mm，压实系数不小于 0.93。夯实后的级配砂石地基承载力特征值fak≥120kpa。
5. 本图参照国家建筑标准设计图集《围墙大门》15J001进行设计，其中大门选型参照本图集第80页折叠无轨大门进行设计，未详事宜参照本图集进行施工。

Техническое описание:

1 Ворота на восточной стороне заводской территории, у въезда-выезда для логистики и входа-выхода для пешеходов, выполняются в виде телескопических ворот; на последующем этапе их можно закупить в комплекте в соответствии с фактическим размером проёма. Ворота на западной стороне территории, у въезда к железнодорожным путям, выполняются из стали в виде складных ворот без рельсов. Конкретные размеры ворот см. на плане и детализированных чертежах, представленных в данном чертеже.

2 В данном чертеже створки двери и скобяные изделия соединяются дуговой сваркой, сварительные швы должны быть зачищены и отполированы.

3 Поверхность стальной двери должна быть обработана антикоррозионной обработкой и защитой от ржавчины. Конкретная антикоррозионная технология должна быть подтверждена Заказчиком и застройщиком.

4 При размещении фундамента в грунте обратной засыпки требуется обработка грунта обратной засыпки под фундаментом. Требуется выемка грунта на 1 м ниже фундамента, с уплотнением грунта обратной засыпки под ним за 2-3 прохода, с последующей обратной засыпкой песчано-гравийной смесью с заданным гранулометрическим составом до проектной отметки. Обратная засыпка должна выполняться послойным уплотнением с толщиной каждого слоя не более 300 мм и коэффициентом уплотнения не менее 0,93. Характеристическое значение несущей способности уплотненного песчано-гравийного основания после трамбовки fak ≥ 120 кПа.

5 Настоящий чертёж выполнен с учётом требований национального строительного стандартного альбома «Ворота забора» 15J001, при этом выбор модели ворот выполнен по образцу складных бесрельсовых ворот на странице 80 данного альбома, а вопросы, не отражённые в деталях, следует выполнять в соответствии с данным альбомом.

版次 Версия	说明 Примечания	日期 Дата

云南化工设计院有限公司
YUNNAN DESIGN INSTITUTE OF CHEMICAL ENGINEERING CO.,LTD.

中信建设有限责任公司
CITIC Construction Co.,Ltd.

工程名称 НАЗВАНИЕ ПРОЕКТА	乌兹别克斯坦年产50万吨硫磺制酸项目 Uzbekistan UTMK Chemical LLC Проект завода по производству серной кислоты	工程代号 Код объекта
		3147

	姓名 Фамилия и имя	签名 Подпись	日期 Дата
审定 Утверждение			
审核 Рассм.	颜炜		2026.03
校核 Проверка	白友军		2026.03
设计 Проектирование	吴俊		2026.03

大门大样图
Детальный чертеж ворот

设计项目 Проектируемый объект	总图运输 Генеральный план и транспорт
设计阶段 Стадия проектирования	施工图 Рабочие чертежи
图号 № чертежа	3147-4T100-08
第 1 张 Лист	
共 1 张 Листы	

专业 Специальность	总图	比例 Масштаб	
日期 Дата	2026.03	版次 Версия	Rev.B

云南省工程勘察设计文件（出图）专用章
单位名称：云南化工设计院有限公司
证书编号：S300790
有效期至：2030年02月14日
资质：化工石化医药行业甲级；建筑行业（建筑工程）甲级；环境工程设计专项（水污染防治工程，大气污染防治工程，固体废物处理处置工程）甲级；轻纺行业（日化及塑料工程，食品发酵烟草工程）乙级；市政行业（给水工程，排水工程，城镇燃气工程，环境卫生工程）乙级；
云南省住房和城乡建设厅2025年08月15日制发
项目出图章编号：4202590044894 项目名称：乌兹别克斯坦年产50万吨硫磺制酸项目
用途：施工图

修改 Изм.			

版权归云南化工设计院有限责任公司所有，未经本公司许可不得转让、复制、泄露给第三方或用于其他目的
ВСЕ ПРАВА ЗАЩИЩЕНЫ YDIC. ДАННЫЙ ЧЕРТЕЖ НЕ МОЖЕТ БЫТЬ ПЕРЕУСТУПЛЕН, ПЕРЕДАН, СКОПИРОВАН, РАСКРЫТ ТРЕТЬИМ ЛИЦАМ, А ТАКЖЕ ИСПОЛЬЗОВАН ДЛЯ ДРУГИХ ЦЕЛЕЙ БЕЗ РАЗРЕШЕНИЯ YDIC.