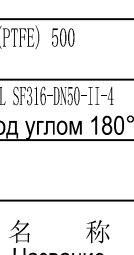
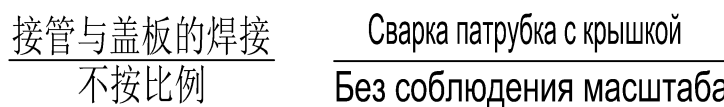
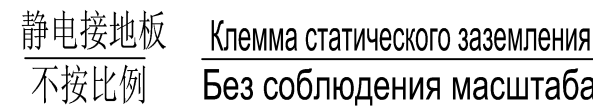
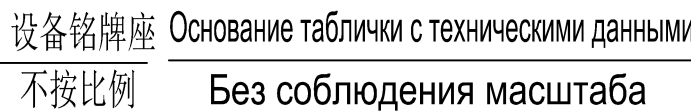
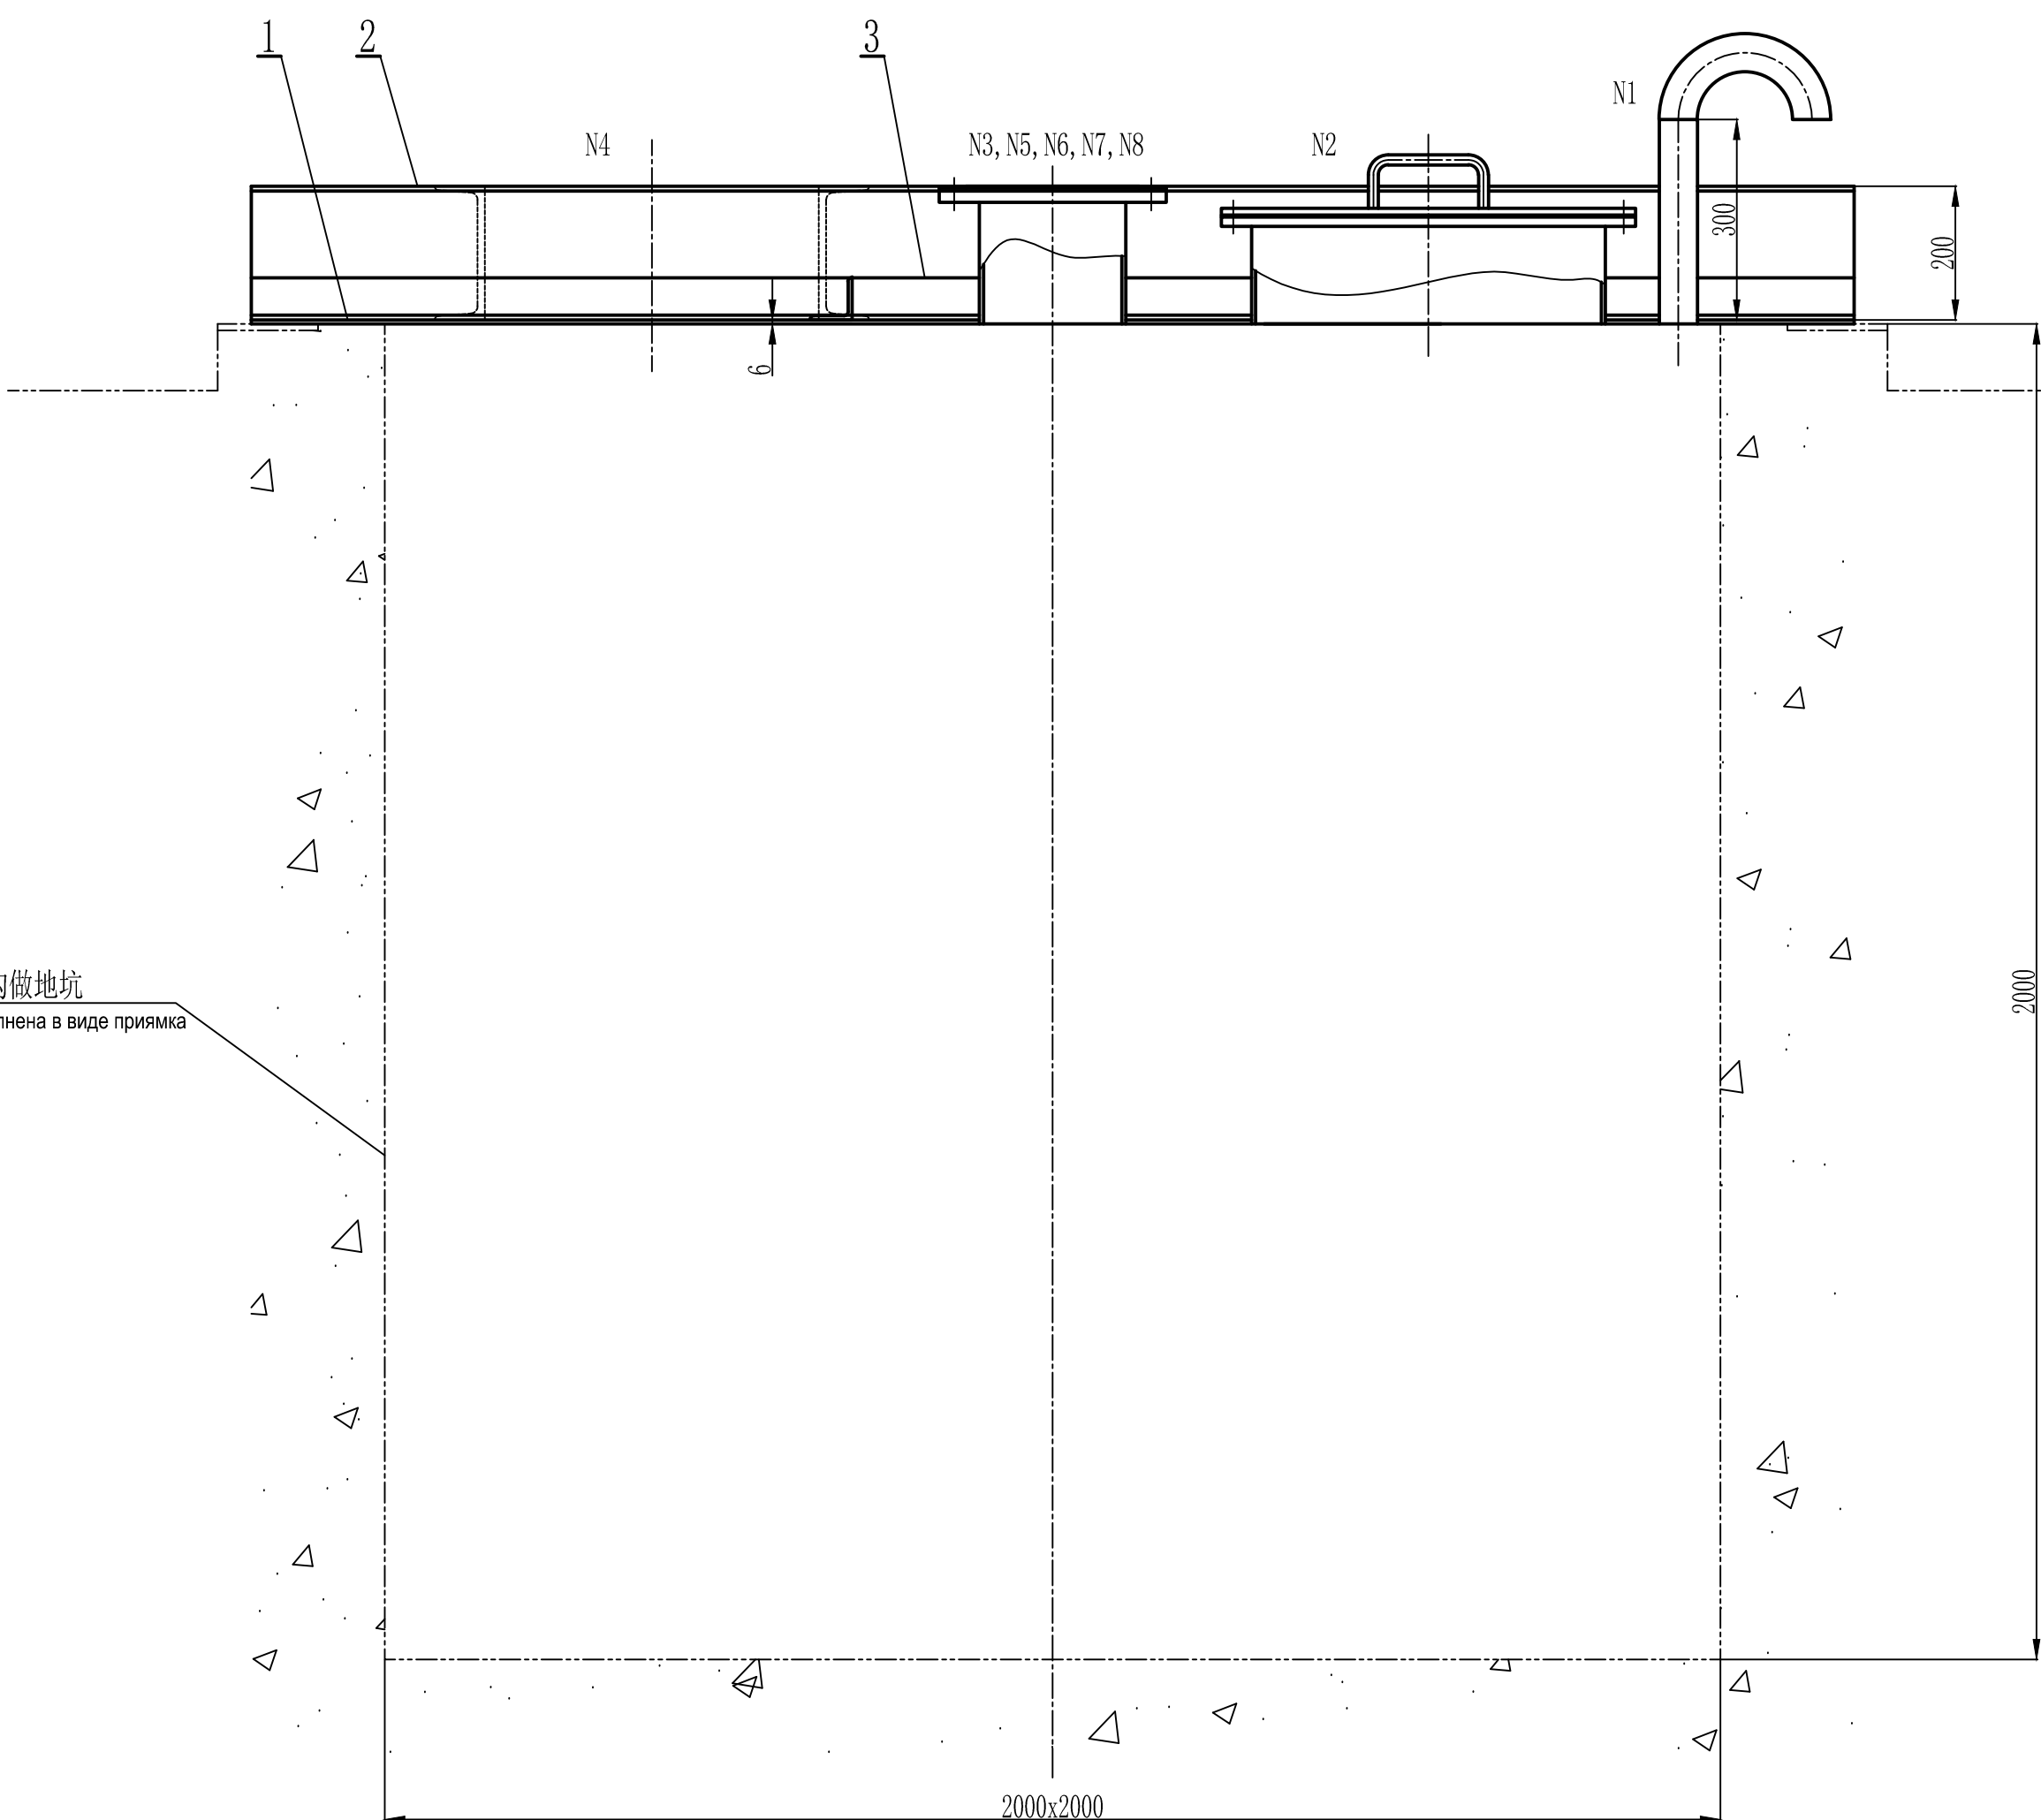
 


陈立	
陈立	

[illegible]

YUNAN DESIGN INSTITUTE OF CHEMICAL ENGINEERING CO.,LTD.				 中信建投 CITIC Construction Co., Ltd.	
工程名称 НАЗВАНИЕ ПРОЕКТА		乌兹别克克斯坦年产50万吨硫酸制酸项目 Uzbekistan UTMK Chemical LLC Проект завода по производству серной кислоты			工程代号 Код объекта
					3147
审定 Утверждение	姓名 Фамилия и имя	签名 Подпись	日期 Дата	设计阶段 Проектный этап	设计阶段工作 Период деятельности проектной организации
审核 Проверка	徐辉		2026. 1. 19	设计阶段 Этап проектирования	施工图 Детальный дизайн
校核 Проверка	曾元润		2026. 1. 19	专业 Специальность	比例 Масштаб
设计 Проектирование	段晓强		2026. 1. 19	日期 Дата	第 张 Всего листов
			2026. 01	版次 Версия	共 1 张
				Rev. 0	 7 696 129 637914

Все права защищены ЮДС. Данный чертеж не может быть переступлен, передан, скопирован, раскрыт третьим лицам, а также использован для других целей без разрешения ЮДС.