
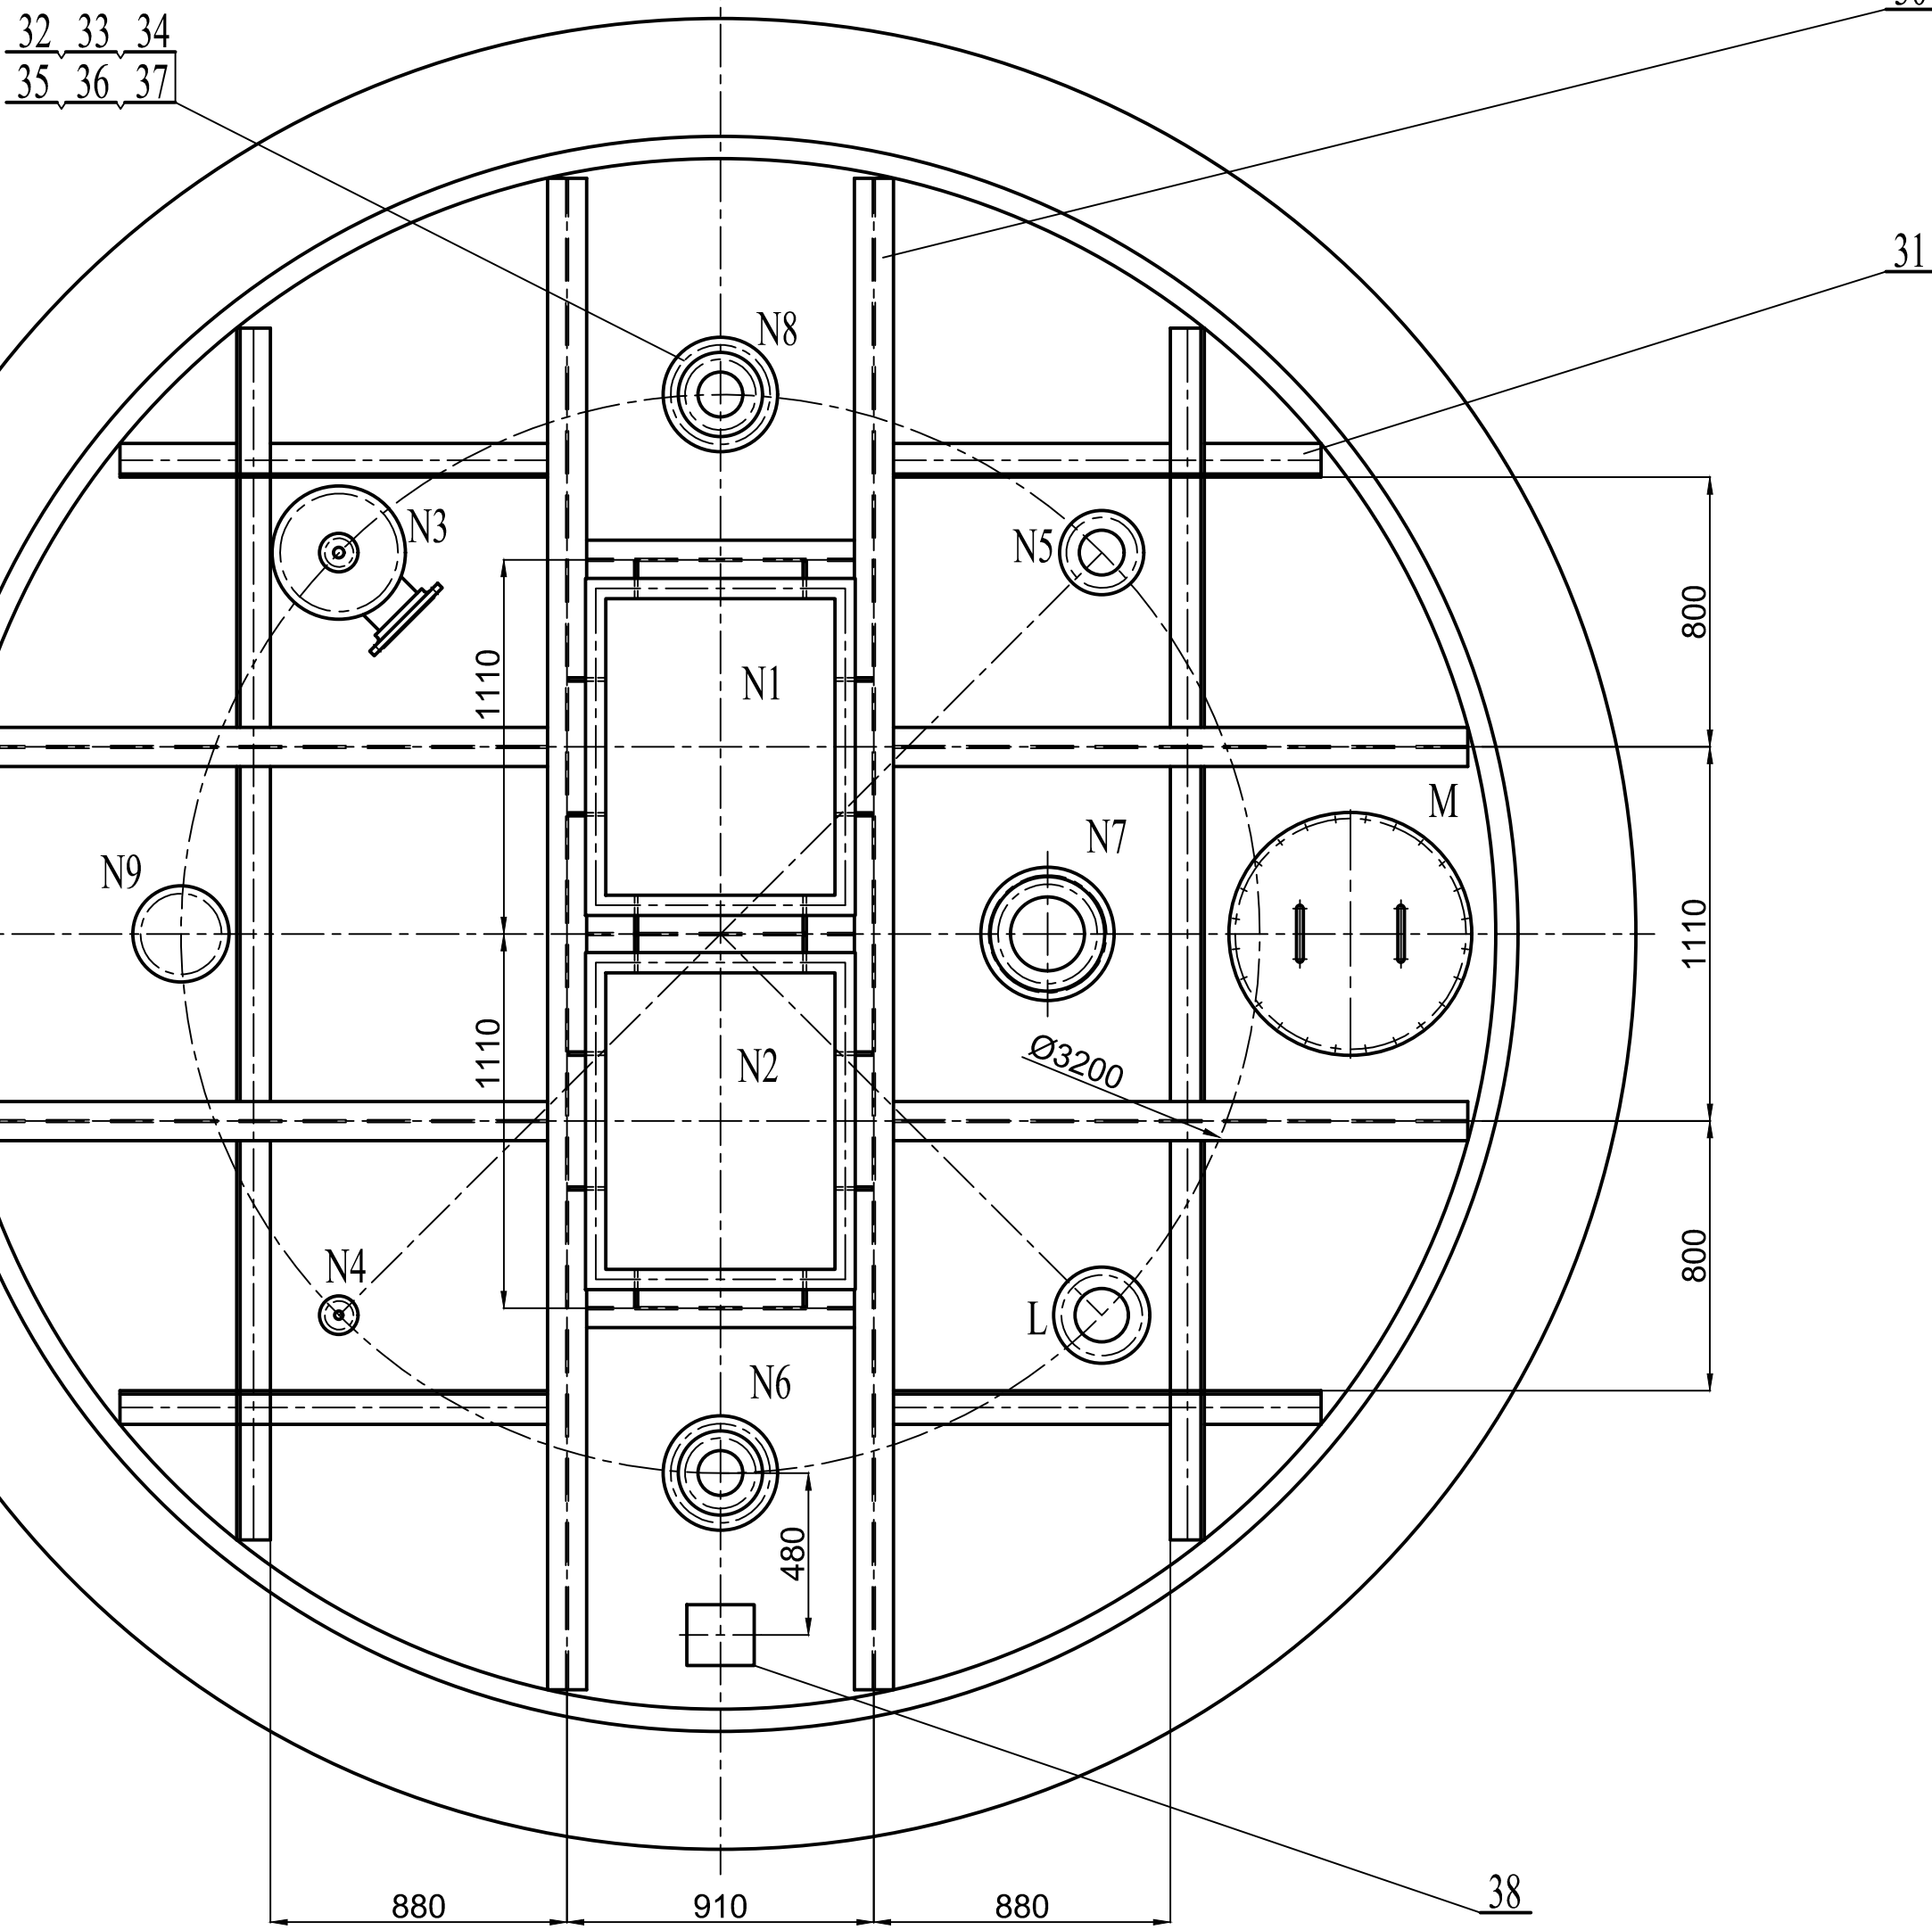


方案 Schemes	姓名 Имя	姓名 Имя
工艺 Technology	孔结构	
设备 Equipment		
起吊 Hoisting		
自控 Automation	等阻联	
给排水 Water supply and drainage		
电 Electrical		
采暖 Heating		
建筑 Architecture		
结构 Structure		
总图 General		
设计 Design	设计 Design	设计 Design
修改 Modification		

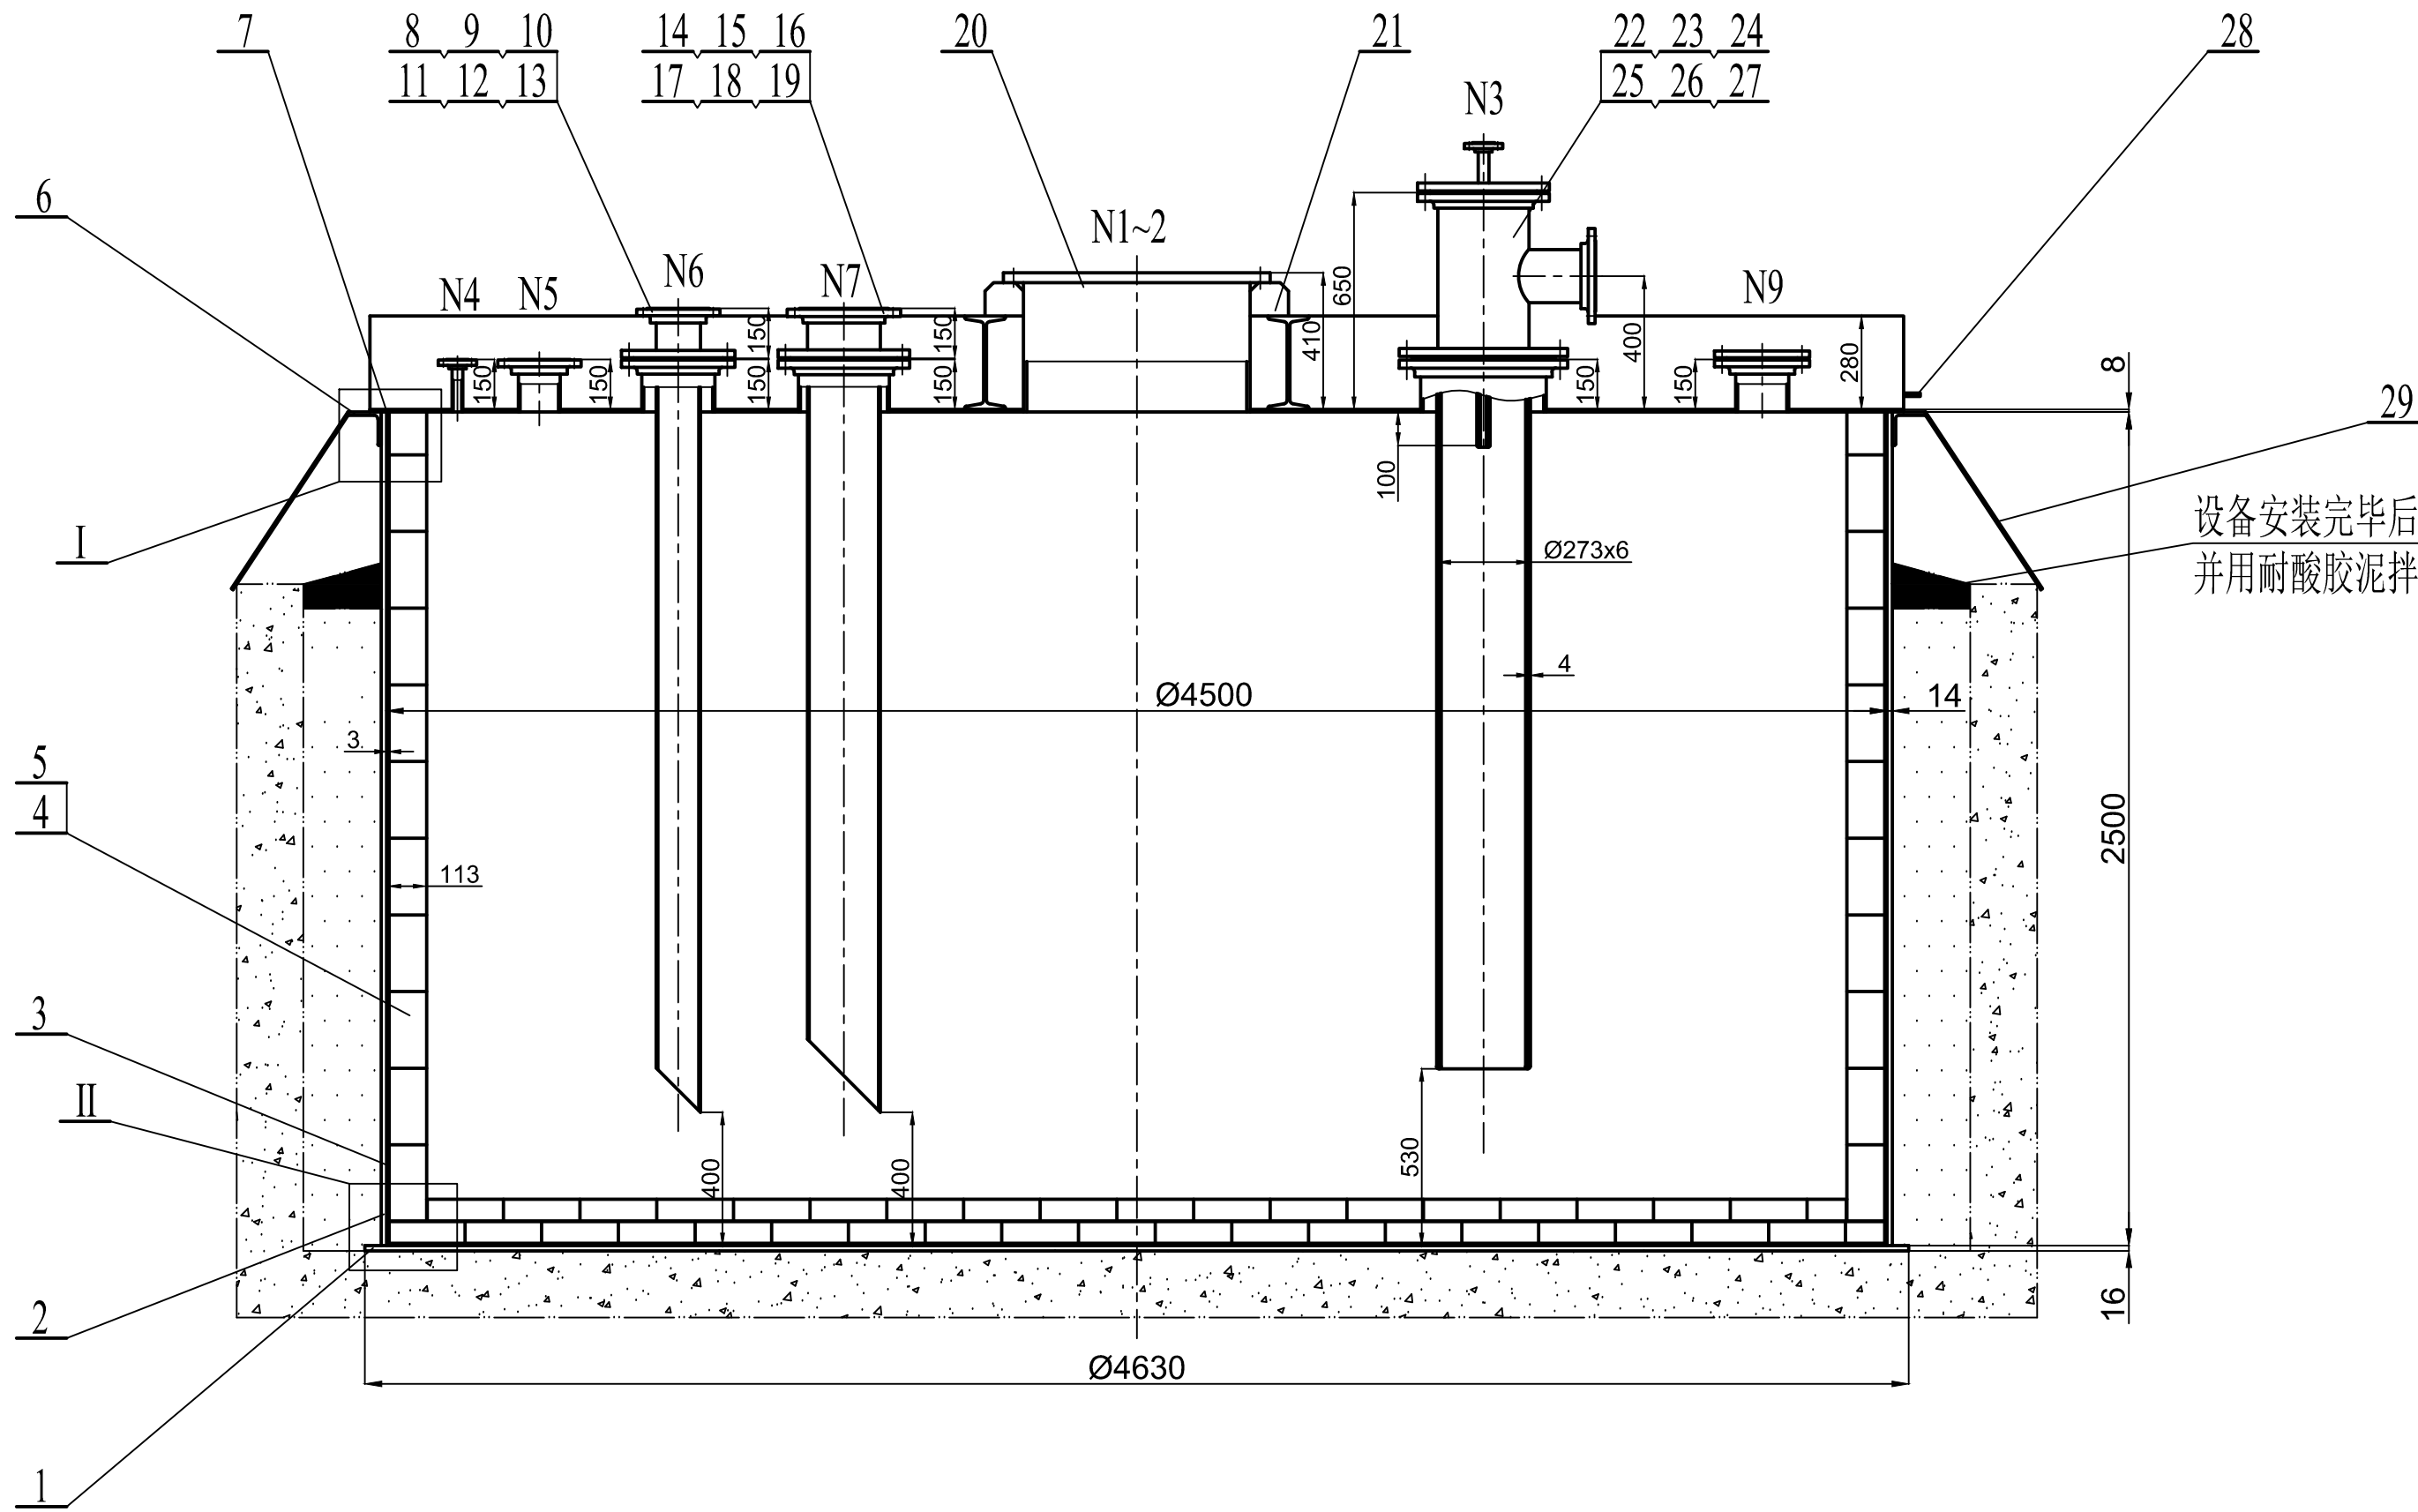

管口符号	图号或标准号 Номер чертежа или номер стандарта	名称 Название	数量 Количество	材料 Материал	单 位 Единица	备 注 Примечания
管口材料表						
38		设备底座 Корытце для таблички	1	Q235B	2.0	
37	GB/T 6170-2015	螺母 M20 Гайка M20	12	8	0.058	1.2
36	GB/T 5782-2016	螺栓 M20x80 Болт M20x80	12	8.8	0.282	5.6
35	HG/T 20606-2009	垫片 RF 200-16 Прокладка RF 200-16	1	PTFE	/	
34		接管 $\phi 159 \times 6$ L=150 Патрубок $\phi 159 \times 6$ L=150	1	S31603	4.7	
33	HG/T 20602-2009	法兰 SO 150(B)-16 RF Фланец SO 150(B)-16 RF	1	S31603 II	10.0	
32	3147-5H113-06-06	产品酸进口 N8 Вход продуктовой кислоты N8	1	组合件 Сбор	78.6	
31		角钢 $\angle 100 \times 8$ L=1980 Уголок $\angle 100 \times 8$ L=1980	1	Q235B	241.1	
30		工字钢 $I 28a$ L=15800 Стальная балка I-beam I 28a L=15800	1	Q235B	687.3	
29	3147-5H113-06-05	挡雨板 Щиток от дождя	1	Q235B	519.6	
28		静电接地板 Пластина заземления	2	S30408	0.25	0.5
27	GB/T 6170-2015	螺母 M24 Гайка M24	16	8	0.1	1.6
26	GB/T 5782-2016	螺栓 M24x85 Болт M24x85	16	8.8	0.5	8.0
25	HG/T 20606-2009	垫片 RF 350-16 Прокладка RF 350-16	1	PTFE	/	
24		接管 $\phi 177 \times 8$ L=150 Патрубок $\phi 177 \times 8$ L=150	1	S31603	10.9	
23	HG/T 20602-2009	法兰 SO 150(B)-16 RF Фланец SO 150(B)-16 RF	1	S31603 II	28.5	
22	3147-5H113-06-06	工艺水进口/废酸出口 N3 Технологической воды / восараз кислоты N3	1	组合件 Сбор	254.3	
21		盖板 S=20 Решетка S=20	16	Q235B	2.2	35.2
20	3147-5H113-06-04	成品酸安装出口 N1~2 Оверлей для установки массы готовой кислоты N1~2	2	S31603	153.4	306.8
19	GB/T 6170-2015	螺母 M24 Гайка M24	12	8	0.1	1.2
18	GB/T 5782-2016	螺栓 M24x85 Болт M24x85	12	8.8	0.464	5.6
17	HG/T 20606-2009	垫片 RF 250-16 Прокладка RF 250-16	1	PTFE	/	
16		接管 $\phi 219 \times 6$ L=150 Патрубок $\phi 219 \times 6$ L=150	1	S31603	5.9	
15	HG/T 20602-2009	法兰 SO 250(B)-16 RF Фланец SO 250(B)-16 RF	1	S31603 II	14.0	
14	3147-5H113-06-03	浓硫酸进口 N7 Вход кислоты на паровые N7	1	组合件 Сбор	115.0	
13	GB/T 6170-2015	螺母 M20 Гайка M20	12	8	0.058	0.7
12	GB/T 5782-2016	螺栓 M20x80 Болт M20x80	12	8.8	0.282	3.4
11	HG/T 20606-2009	垫片 RF 300-16 Прокладка RF 200-16	1	PTFE	/	
10		接管 $\phi 219 \times 6$ L=150 Патрубок $\phi 219 \times 6$ L=150	1	S31603	4.7	
9	HG/T 20602-2009	法兰 SO 200(B)-16 RF Фланец SO 200(B)-16 RF	1	S31603 II	10.0	
8	3147-5H113-06-03	排液酸进口 N6 Впускной патрубок кислоты на выпуск N6	1	组合件 Сбор	64.6	
7		盖板 $\phi 4600$ S=8 Крышка $\phi 4600$ S=8	1	S31603	1053.8	
6		包边角钢 $\angle 100 \times 8$ L=1300 Уголок обвязочный $\angle 100 \times 8$ L=14300	1	Q235B	176.0	
5	GB/T 8488-2012	耐腐蚀 Кислотостойкий металл	3.8m ²			1276.0
4		耐腐蚀 Кислотостойкий металл	0.5m ²			1000
3		耐腐蚀 Кислотостойкий металл	0.5m ²			810
2		耐腐蚀 Кислотостойкий металл	1	Q235B	3863.1	
1		耐腐蚀 Кислотостойкий металл	1	Q235B	2113.6	

设计、制造、检验与验收主要数据表													
设计参数					设计、制造、检验与验收标准								
Параметры проектирования					Стандарты проектирования, изготовления, испытаний и приемки								
容器类别/类别	/				标准 Standards и нормы	NB/T 47003.1-2022 《常压容器》 NB/T 47003.1-2022 «Сосуды, работающие под атмосферным давлением»							
设计使用年限 Проектный срок службы	年 год	/				HG/T 20676-1990 《钢板衬里化工设备》 HG/T 20676-1990 «Химические аппараты, футерованные металлом и пластиком»							
介质名称 Наименование параметра	介质 Сред	管道 Труба	/			HG/T 20678-2000 《衬里钢壳设计技术规定》 HG/T 20678-2000 «Технические требования к проектированию футерованных стальных сосудов»							
工作压力 Рабочее давление	MPa МПа	管压 Атмосферное	/										
设计压力 Расчетное давление	MPa МПа	管压 Атмосферное	/										
工作温度 Рабочая температура	℃ °C	70.5/88.5											
设计温度 Расчетная температура	℃ °C	100											
设计温度 Расчетная температура	℃ °C	100											
