
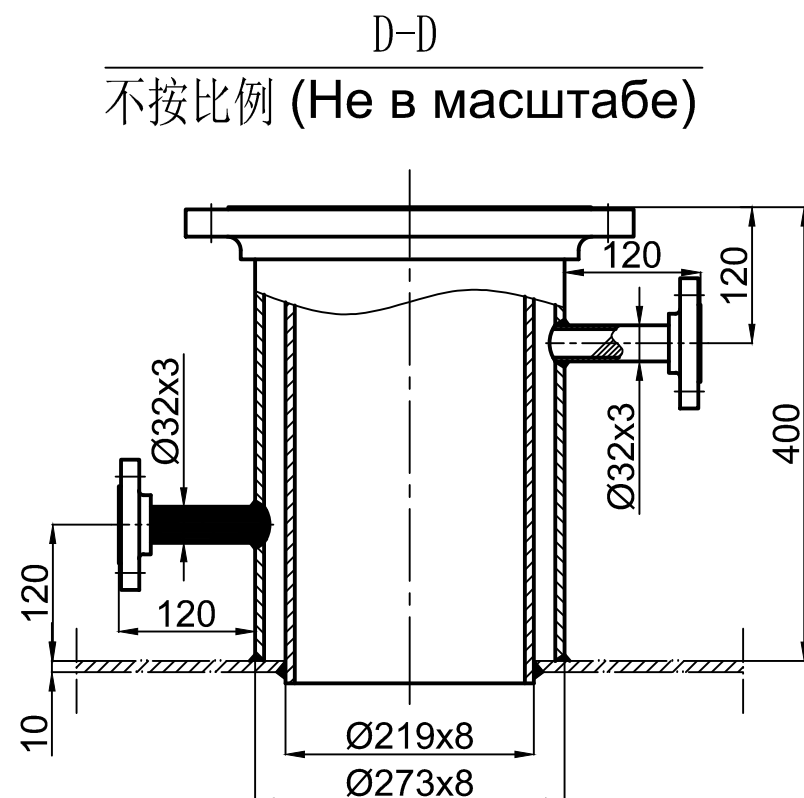
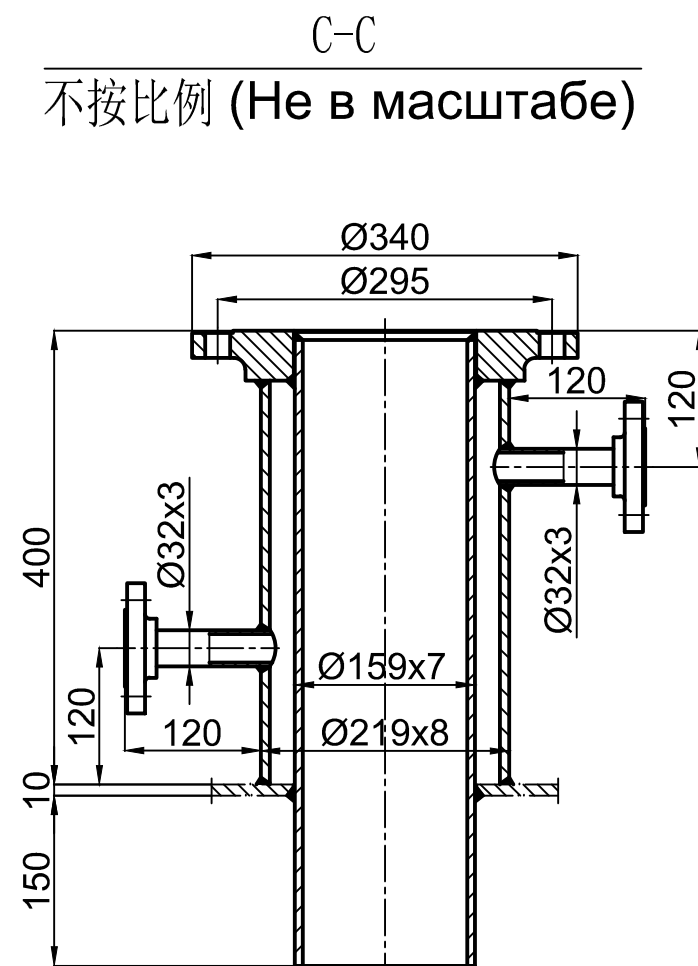
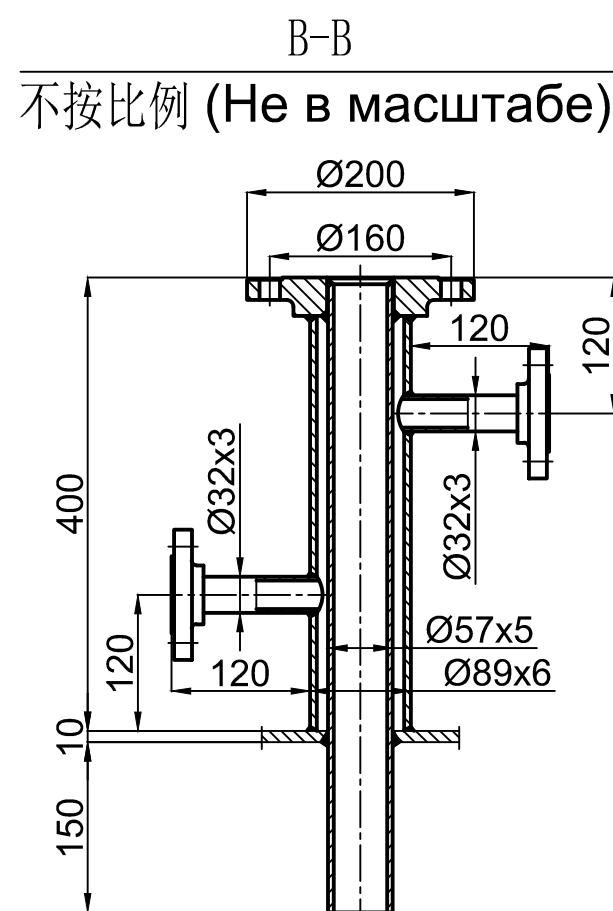


修改 Rev.	
------------	--

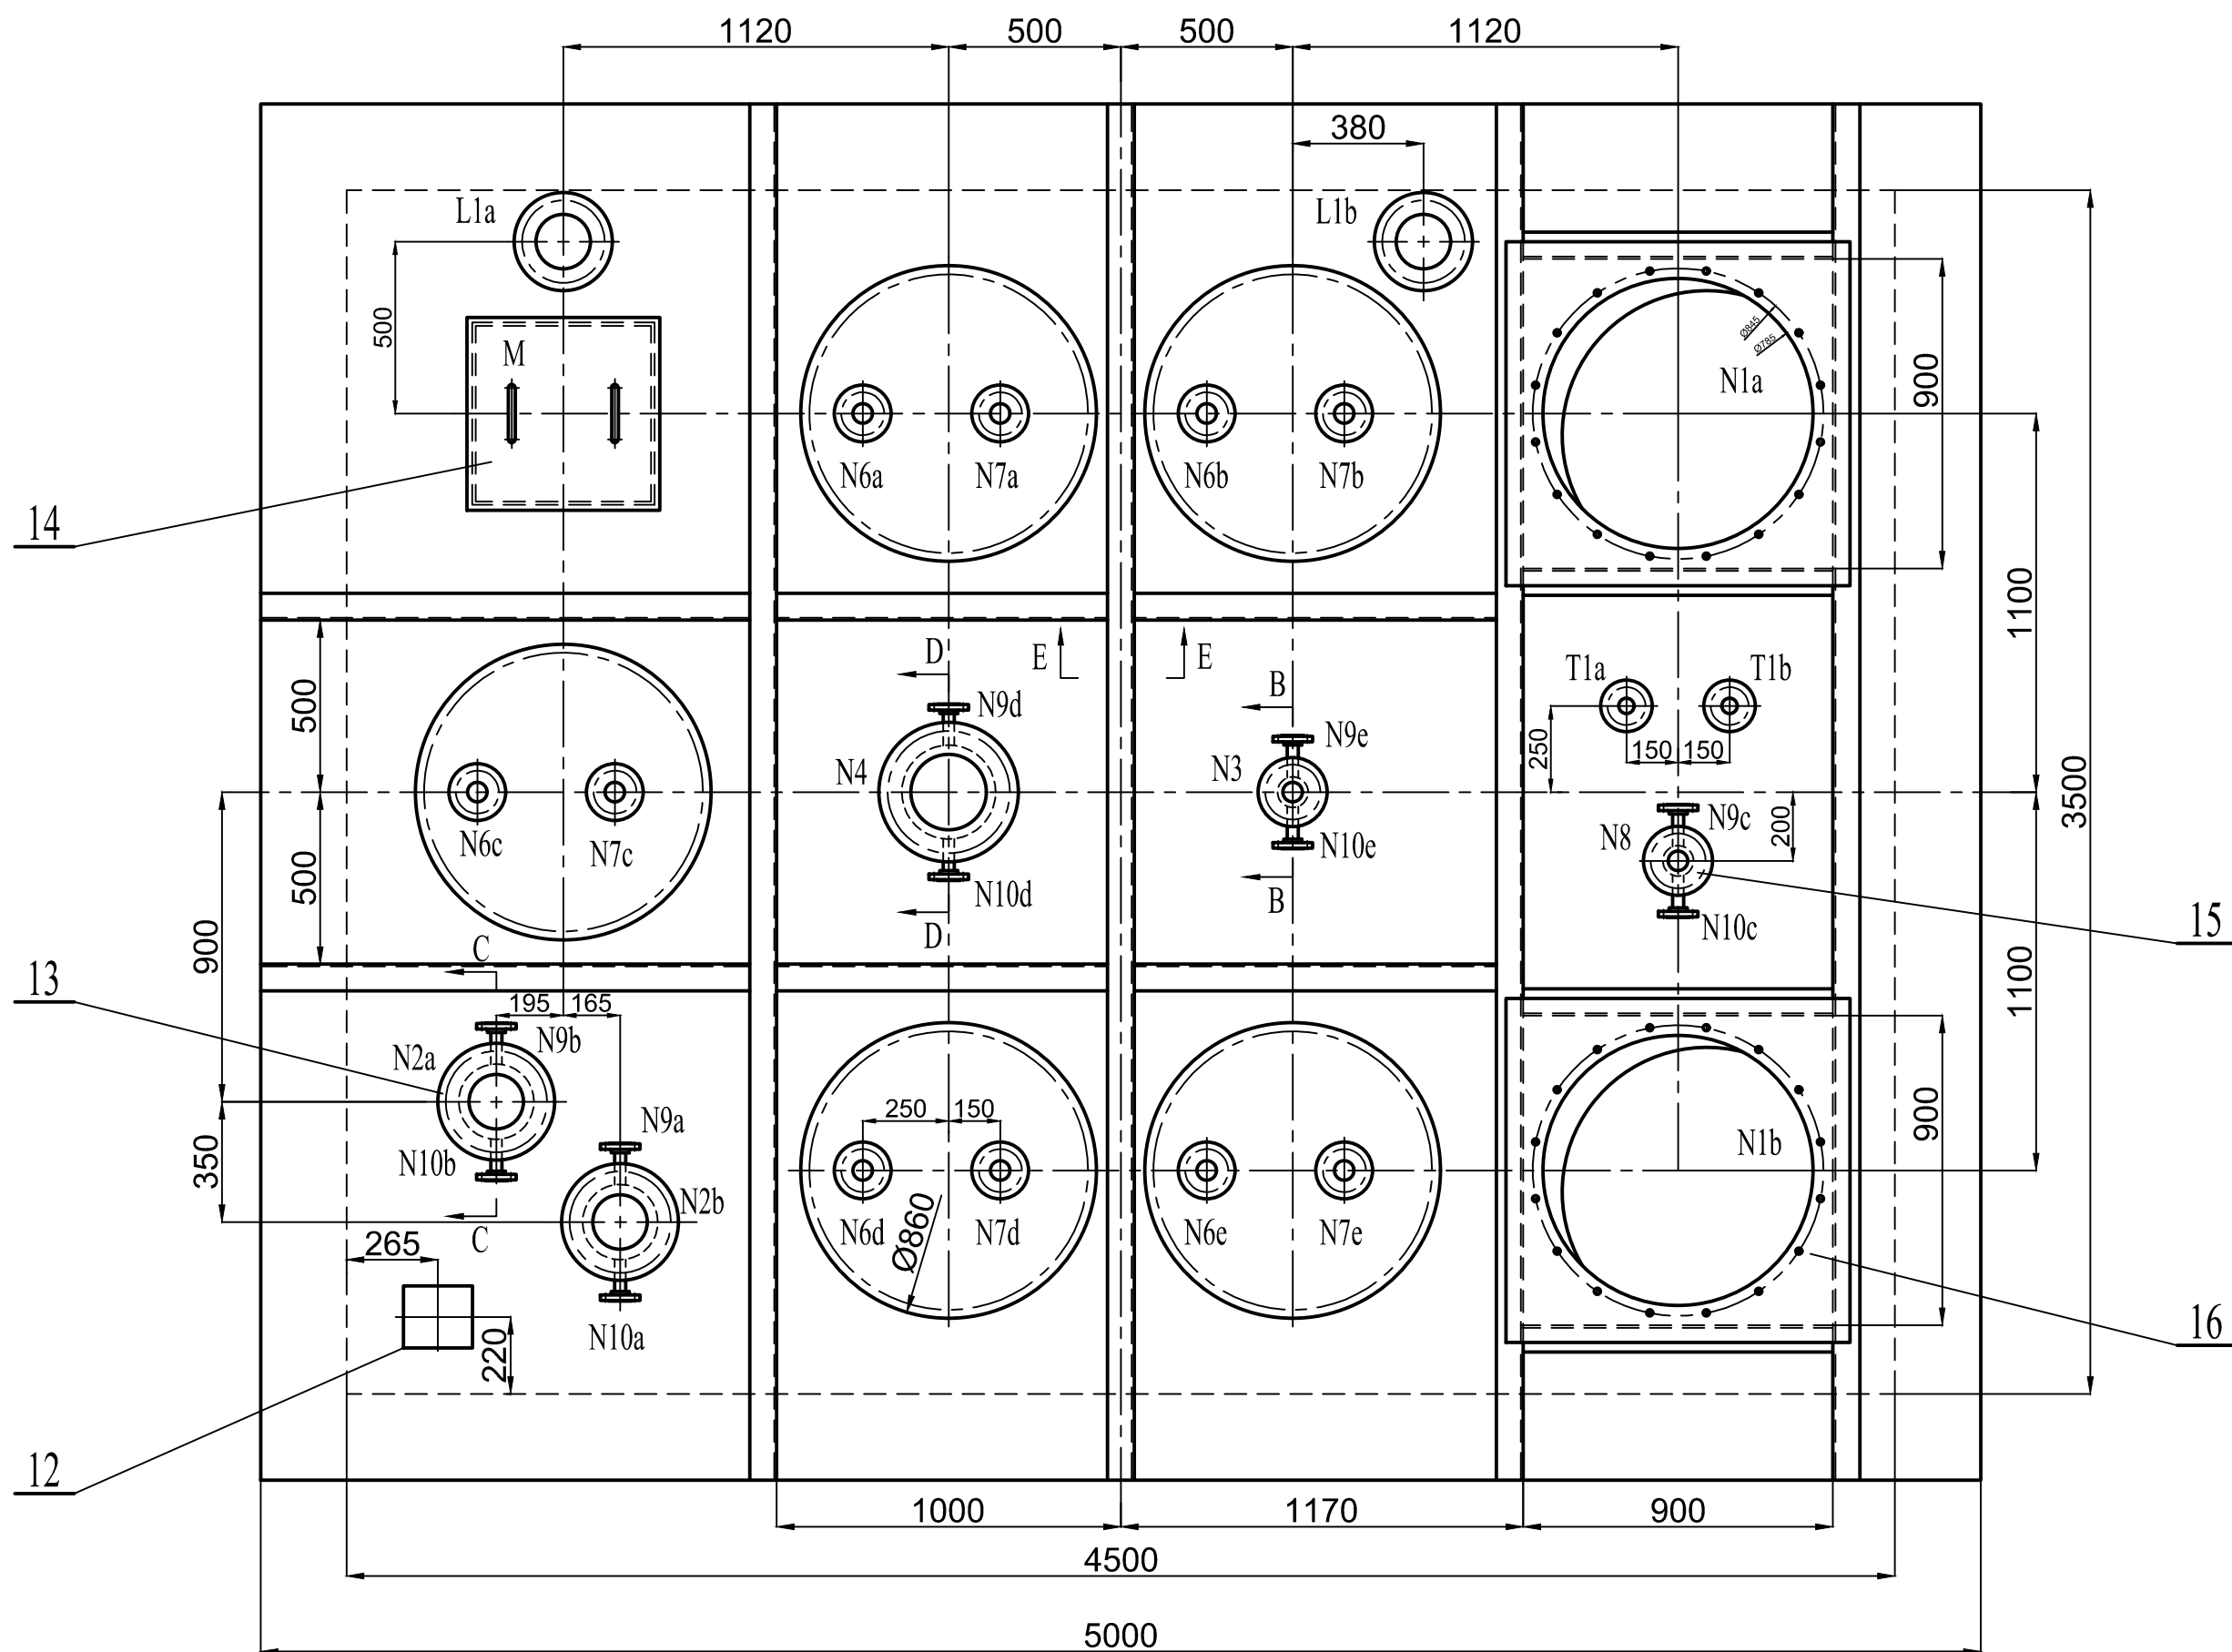



设计、制造、检验与验收主要依据标准									
设计参数					设计、制造、检验与验收标准				
Parameters for design					Standards for design, manufacturing, inspection and acceptance				
各系列别简称 Категория/класс сосуда					NB/T 47003.1-2022 《常压容器》 NB/T 4703-2022 《储罐、加工制造用压力容器》				
设计使用年限 Проектный срок службы					年 /				
主要设计参数 Основные параметры					容器 Сосуд				
工作压力 Рабочее давление					MPa MPa				
设计压力 Расчетное давление					MPa MPa				
工作温度 Рабочая температура					°C °C				
设计温度 Расчетная температура					°C °C				
介质名称 Наименование среды					液态金属 Жидкий металл				
介质特性 Характеристики среды					腐蚀性 Коррозия				
介质密度 Плотность среды					kg/m³ kg/m³				
介质流量 Расход среды					m³/h m³/h				
腐蚀裕量 Запас прочности на коррозию					mm mm				
容积系数 Коэффициент заполнения					/				
重量系数 Коэффициент веса					/				
基本风压 Базовое давление ветра					kPa kPa				
基本雪压 Базовое снежное давление					kPa kPa				
抗震设防烈度 Категория сейсмостойкости					/				
按地上安装/埋地安装 Установка на поверхности/в грунте					/				
结构及材料说明 Конструкция и материалы					硅酸铝纤维毯 (盖板保温) Силкатоволокнистый мат (крышка теплоизоляция)				
板厚/管径 Толщина листов/диаметр труб					mm mm				
连接形式 Формы соединения					/				
密封形式 Формы герметизации					/				
重量 Масса					kg kg				
其中: 不锈钢重量 в том числе: нержавеющая сталь					kg kg				

主 要 建 筑 工 程 材 料 Материалы основных объектов строительства					
名 称 Наименование	规 格 Стандарт	单 位 Единица	备 注 Состояние	备 注 Дополнительные требования	备 注 Дополнительные требования
板 材 Листовые материалы	GB/T 3274-2017	Q235B	热轧 Горячая прокатка		/
联 件 Крепежные детали	NB/T 47008-2017	20 II	正火 Нормализация		/
管 材 Трубы	GB/T 9948-2025	20	正火 Нормализация		/

Технические требования:

1. Изготовление изделий в соответствии с требованиями заказчика,合格后交付使用。
2. Провести анализ соответствия изделий: провести поэлементную проверку функционала в соответствии с архитектурно - структурными чертами и соответствующими требованиями черт, чтобы достичь поставленных результатов и обеспечить соответствие с требованиями;
3. 2. 完成需求及设计/使用说明书的编写和校对。
4. 2. 3. 制定并实施产品性能提升方案，在用户反馈和当前产品使用状况的基础上与产品组沟通，明确产品性能提升需求，制定提升计划并快速进行提升验证，以验证提升是否合格；
5. 3. 制定设备维护计划，制定设备维护计划/培训/修理/消耗品采购清单等，设备维护由 D41 处负责定期维护。消耗品清单作为维护的附件提供。
6. 3. 1. 制定管理维护计划，制定 D41 用户操作使用手册。
7. 4. 制定设备性能提升方案，制定提升计划/培训/修理/消耗品采购清单等，设备性能提升由 D41 处负责定期提升。
8. 6. 制定 D41 设备使用计划/维护计划/培训/修理/消耗品采购清单。
9. 6. 1. 制定设备性能提升方案，制定提升计划/培训/修理/消耗品采购清单等，设备性能提升由 D41 处负责定期提升。
10. 7. 制定并实施产品性能提升方案，在用户反馈和当前产品使用状况的基础上与产品组沟通，明确产品性能提升需求，制定提升计划并快速进行提升验证，以验证提升是否合格；
11. 7. 1. 制定设备维护计划，制定设备维护计划/培训/修理/消耗品采购清单等，设备维护由 D41 处负责定期维护。消耗品清单作为维护的附件提供。

管 号 Символ	公称尺寸 Номинальный размер	公称压力 Номинальное давление	连接标准 Стандарт соединения	法兰形式 Тип фланца	管口名称 Назначение фланцевого ракет	用途或名称 Назначение или название	外形长度 Высотная длина
N1a-b			/	/	/	粗颈或安装接口 Установка «хвостовых» деталей	/
N2a-b	DN150/200	PN16	HGT120592-2009	JSO	RF	液碱进口 Ввод жидкой щелочи	400
N3	DN50/80	PN16	HGT120592-2009	JSO	RF	液碱或出口 Питание жидкостями	400
N4	DN200/250	PN16	HGT120592-2009	JSO	RF	蒸汽口 Питание паром	400
N6a-e	DN50	PN16	HGT120592-2009	SO	RF	微负压进口 Ввод пара (вакуум)	见图 См. чертёж
N7a-e	DN50	PN16	HGT120592-2009	SO	RF	微负压水出口 Выход воды (вакуум)	见图 См. чертёж
N8	DN50/80	PN16	HGT120592-2009	JSO	RF	微负压进口 Ввод пара для нагрева	400
N8a-e	DN25	PN16	HGT120592-2009	SO	RF	夹套蒸汽进口 Пароснагреватель паром	见图 См. чертёж
N10a-e	DN25	PN16	HGT120592-2009	SO	RF	夹套冷却水出口 Конденсатор паром	见图 См. чертёж
M	500x500	/	/	/	/	人孔 Люк	250
L1a-b	DN150	PN16	HGT120592-2009	JSO	RF	液碱进口 Конденсатор паром	150
T1a-b	DN40	PN16	HGT120592-2009	SO	RF	温度接口 Гнездо термометра	150

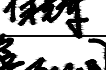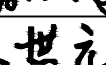版次 Версия		说明 Примечания				日期 Дата			
云南化工设计院有限公司 YUNNAN DESIGN INSTITUTE OF CHEMICAL ENGINEERING CO., LTD.				中信建设有限责任公司 CITIC Construction Co., Ltd.					
工程名称 НАЗВАНИЕ ПРОЕКТА		乌兹别克斯坦年产50万吨硫酸磺酸项目 Uzbekistan UTMK Chemical LLC Проект завода по производству серной кислоты						工程代号 Код объекта	
								3147	
审定 Утверждение	姓名 Фамилия	签名 Подпись	日期 Дата	精硫磺(一) VE-12202 Резервуар для рафинированной серы			设计项目 Проектирование		
审核 Разраб.	徐辉		01.27				设计阶段 Стадия проектирования		图号 № чертежа
设计 Проектирование	曹元润		01.27	专业 Специальность	设备 Оборудование	比例 Масштаб	1: 20	第 1 张 Лист	
	王世元		01.27	日期 Дата	版次 Версия	Rev. 0		共 1 张 Листов	
						施工图 Детальная разработка проекта		3147-5H122-02-01 	