


方案	姓名	签名
工艺	姓名	签名
设备	姓名	签名
电气	姓名	签名
暖通	姓名	签名
给排水	姓名	签名
自控	姓名	签名
结构	姓名	签名
总图	姓名	签名
设计	姓名	签名
审核	姓名	签名
批准	姓名	签名

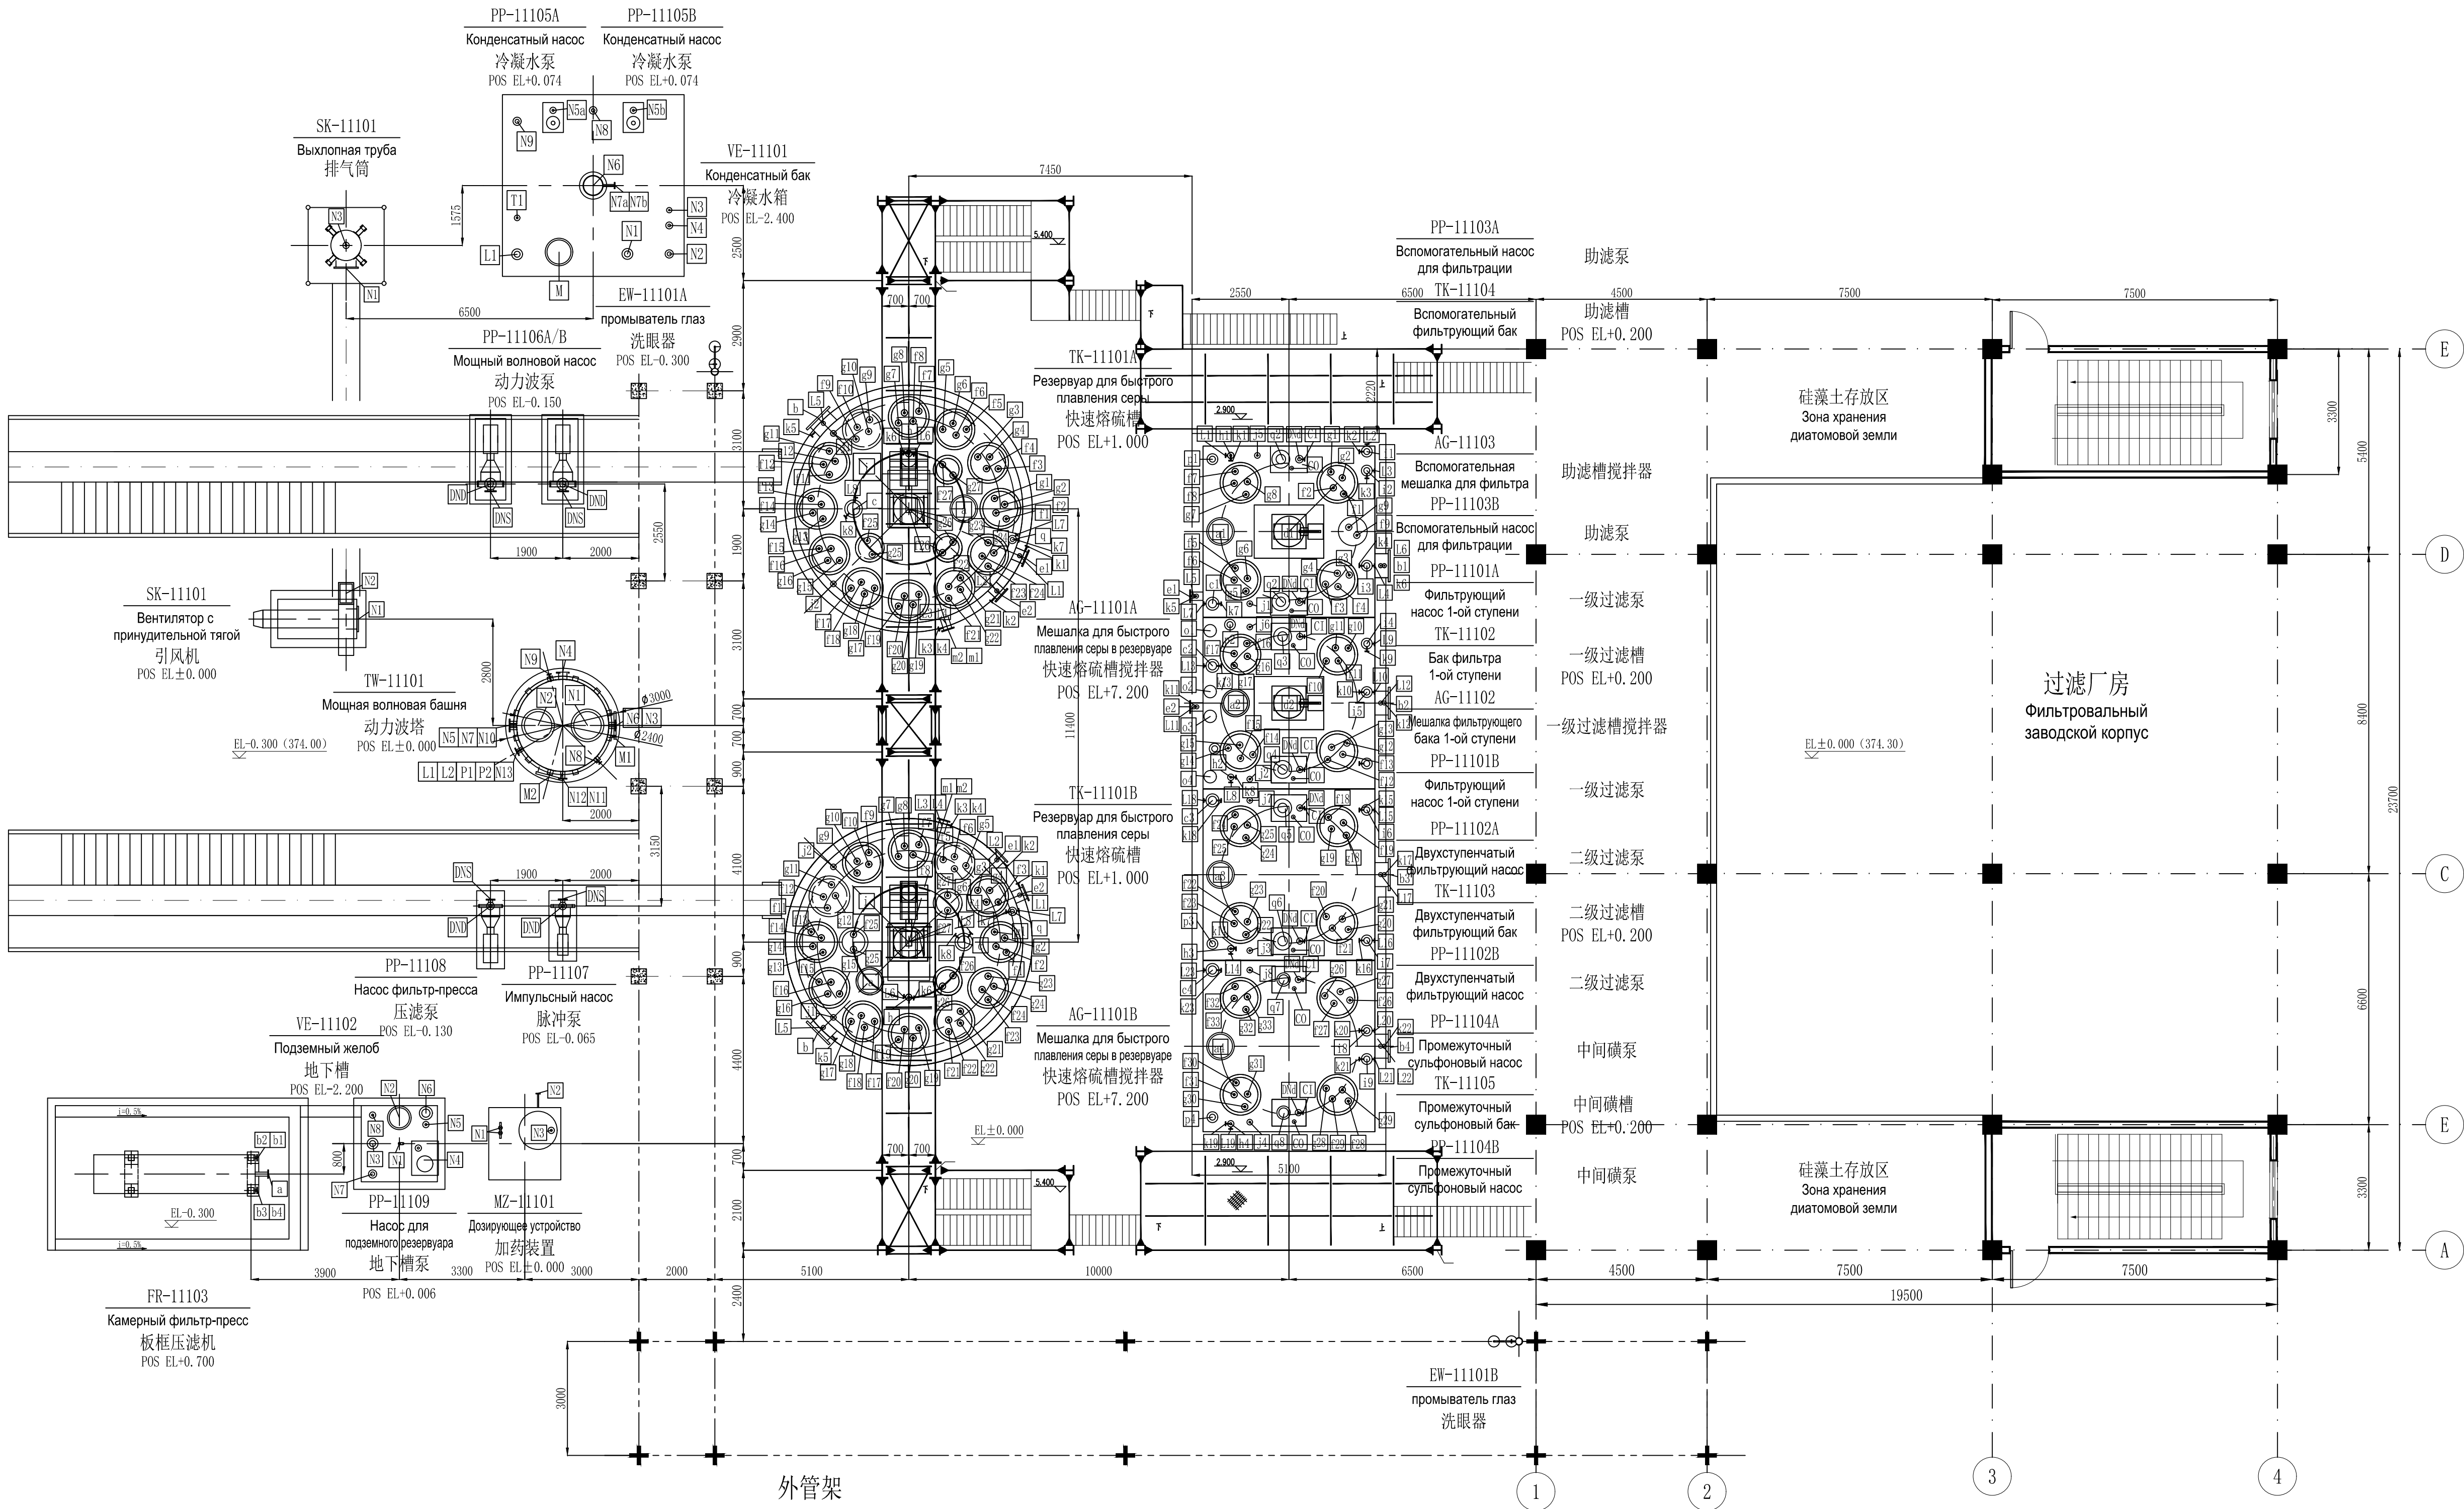

Площадь с
отметкой EL±0.000
EL±0.000平面

版本 Версия		说明 Примечания		日期 Дата
云南化工设计院有限公司 YUNNAN DESIGN INSTITUTE OF CHEMICAL ENGINEERING CO., LTD.		中信建设有限责任公司 CITIC Construction Co., Ltd.		
工程名称 НАЗВАНИЕ ПРОЕКТА		乌兹别克斯坦年产50万吨硫酸制酸项目 Uzbekistan UTMK Chemical LLC Проект завода по производству серной кислоты		工程代号 Код объекта 3147
审定 Утверждение	姓名 Фамилия и имя	签名 Подпись	日期 Дата	设计项目 Проектируемый объект EL±0.000平面
审核 Риском.	李海品	李海品		设计阶段 Стадия проектирования 图号 № чертежа 3147-56111-07
校核 Проверка	张斌斌	张斌斌		第1章 Лист
设计 Проектирование	董俊	董俊		共1张 Листы
专业 Специальность		工艺 Технология	比例 Масштаб	图例 Легенда
日期 Дата		2026.05	版次 Версия	