

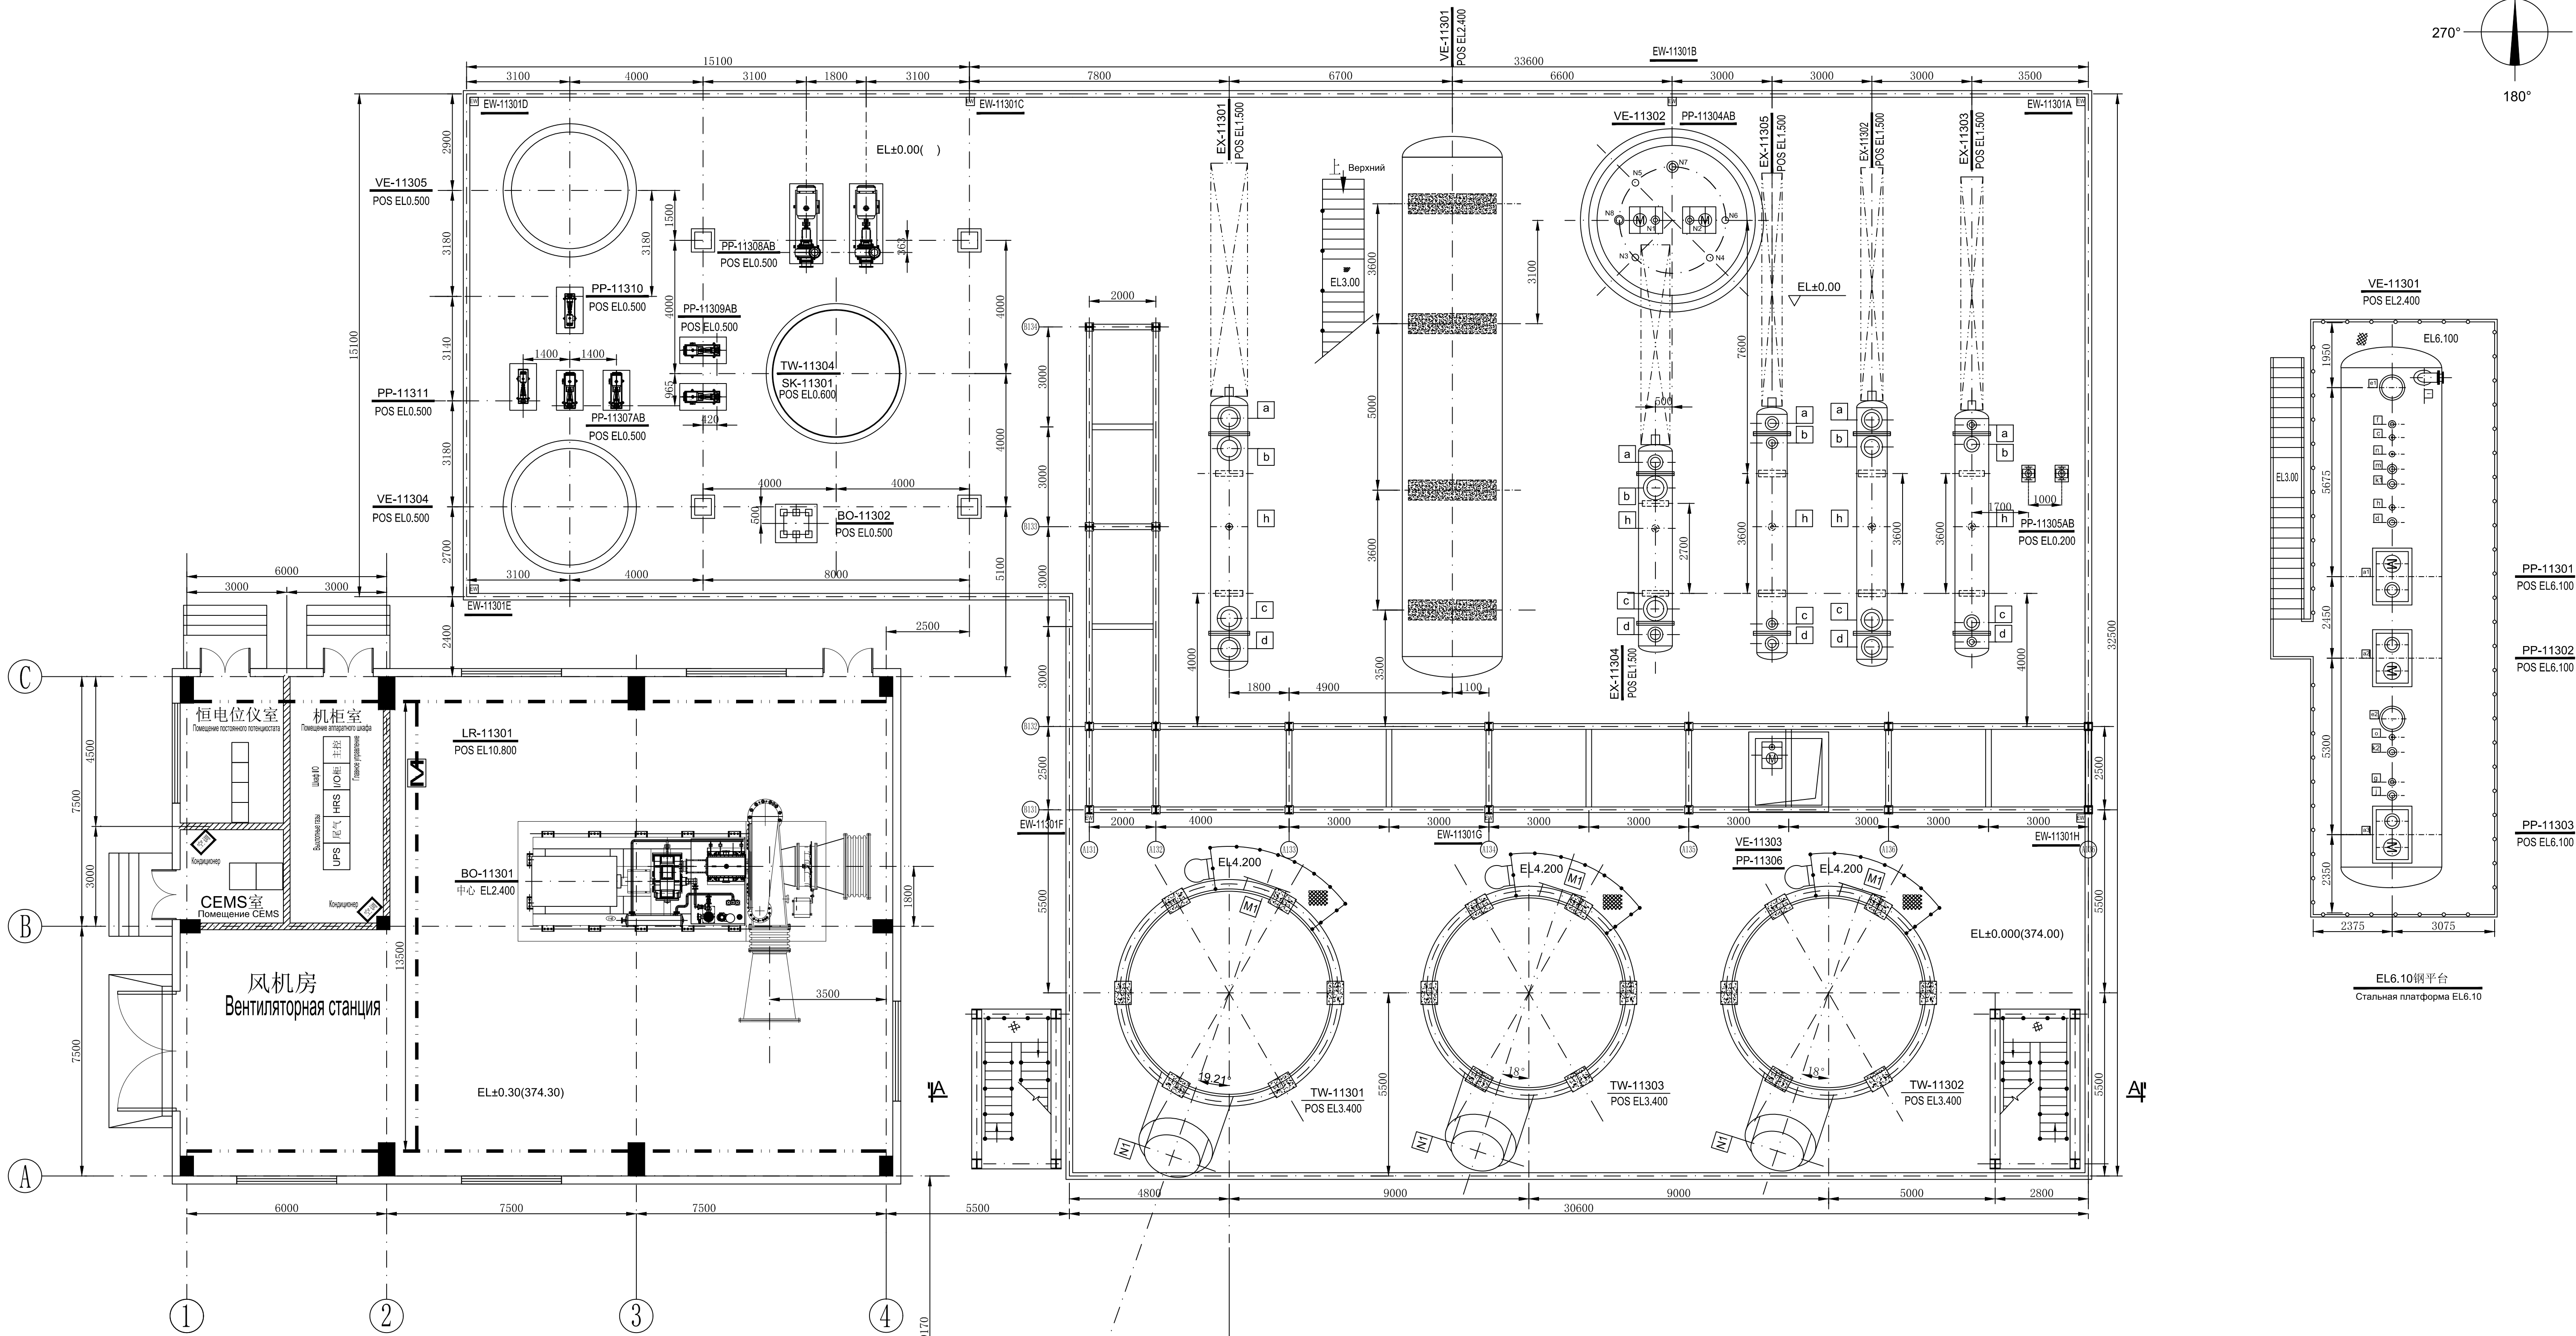


会签	姓名	签名
工艺	张	
设备	张	
电气	张	
自控	张	
给排水	张	
电	张	
热质	张	
建筑	张	
结构	张	
总图	张	
设计	张	
审核	张	
校对	张	
制图	张	

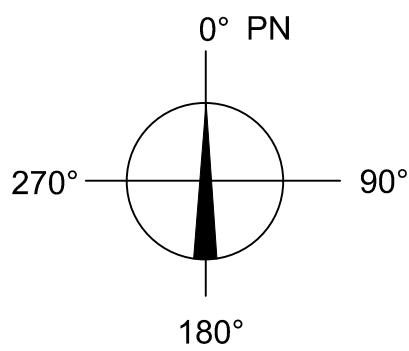

PP-11311	разгрузочный щелочной насос 卸碱泵		
PP-11310	Транзитный насос Сульфат натрия 硫酸钠中转泵		
PP-11309AB	Насос для перекачки сульфата натрия 硫酸钠输送泵	SK-11301	Труба выхлопных газов 尾气排气筒
PP-11308AB	Циркуляционный насос щелочного промывки 碱洗循环泵	VE-11305	Резервуар для раствора Na2SO4 Na2SO4溶液储罐
PP-11307AB	Насос для перекачивания щелочного раствора 碱液输送泵	VE-11304	Резервуар для раствора NaOH NaOH溶液储罐
PP-11306	Насос для подачи отработанной кислоты 废酸输送泵	TW-11304	абсорбционная башня 吸收塔
PP-11305AB	насос опреснения воды 脱盐水加压泵	BO-11302	Окислительный вентилятор 氧化风机
PP-11304AB	Насос готовой кислоты 成品酸泵		
PP-11303	Циркуляционный кислотный насос второй абсорбционной колонны 二吸塔循环泵	BO-11301	Воздуходувка 空气风机
PP-11302	Циркуляционный кислотный насос первой абсорбционной колонны 一吸塔循环泵	EW-11301A-F	Очиститель, плав с безопасным опреснением 安全喷淋洗眼器
PP-11301	Циркуляционный кислотный насос в сушильной башне 干燥塔循环泵	LR-11301	Электронный переключатель край 电动单梁起重机
VE-11303	Подземный резервуар для отработанной кислоты 废酸地下槽	SM-11301	Воздушный фильтр 空气过滤器
VE-11302	Подземная ёмкость для готовой кислоты 成品酸地下槽	EX-11305	Охладитель готовой кислоты 成品酸冷却器
VE-11301	Комбинированный циркуляционный кислотный бак 联合循环酸槽	EX-11304	Охладитель кислоты второй абсорбции 二吸酸冷却器
TW-11303	Вторая абсорбционная колонна 二吸塔	EX-11303	Водонагреватель для обессоленной воды 脱盐水产热器
TW-11302	Первая абсорбционная колонна 一吸塔	EX-11302	Охладитель кислоты первой абсорбции 一吸酸冷却器
TW-11301	Сушильная колонна 干燥塔	EX-11301	Охладитель осушенной кислоты 干燥酸冷却器

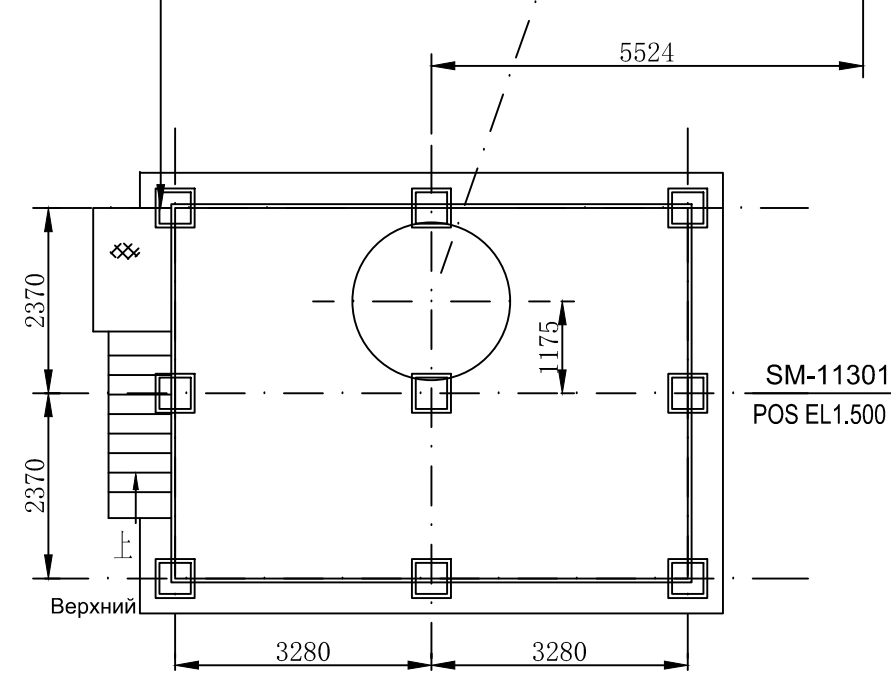


Отметка ±0.000
EL±0.000平面

D:\2020新图框\2020集中统一新图框\2020管道表格\施工图.png

版次 Версия		说明 Примечания		日期 Дата	
云南化工设计院有限公司 YUNNAN DESIGN INSTITUTE OF CHEMICAL ENGINEERING CO., LTD.		中信建设有限责任公司 CITIC Construction Co., Ltd.		工程代号 Код объекта	
工程名称 НАЗВАНИЕ ПРОЕКТА		乌兹别克斯坦年产50万吨硫酸项目 Uzbekistan UTMK Chemical LLC Проект завода по производству серной кислоты		3147	
姓名 Фамилия и имя		签名 Подпись		日期 Дата	
审定 Расм.		李海昆 李海昆		日期 Дата	
审核 Проверка		董俊 董俊		日期 Дата	
设计 Проектирование		沈开豪 沈开豪		日期 Дата	
设计阶段 Стадия проектирования		设计项目 Проектный объект		干吸工序 Процесс сухой абсорбции	
图号 № чертежа		比例 Масштаб		施工阶段 Рабочий проект	
专业 Специальность		工艺 Технология		图号 № чертежа	
日期 Дата		2026.4		版次 Версия	
比例 Масштаб		1:100		第1张 Лист	
共1张 Листы				3147-5G113-05	

修改 Изм.	

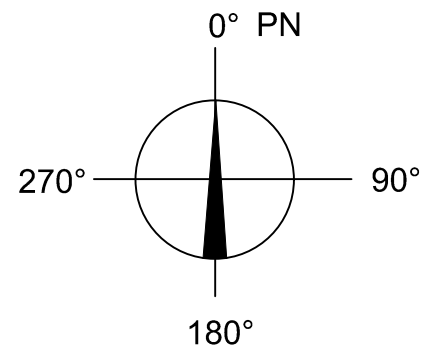

Отметка 11.50



EL11.50 平面



版次 Версия		说明 Примечания		日期 Дата	
 云南化工设计院有限公司 YUNNAN DESIGN INSTITUTE OF CHEMICAL ENGINEERING CO., LTD.		 中信建设有限责任公司 CITIC Construction Co., Ltd.			
工程名称 НАЗВАНИЕ ПРОЕКТА		乌兹别克斯坦年产50万吨硫酸项目 Uzbekistan UTMK Chemical LLC Проект завода по производству серной кислоты			工程代号 Код объекта 3147
审定 Утверждение 审核 Рассм. 校核 Проверка 设计 Проектирование		姓名 Фамилия и имя 李海昆 董俊 沈开宽		签名 Подпись 李海昆 董俊 沈开宽	
日期 Дата		设备布置图 EL11.50 EL14.00平面 Schema размещения оборудования Отметка 11.50、14.00		设计项目 Проектируемый объект 设计阶段 Стадия проектирования 图号 № чертежа 第1张 Лист 共1张 Листы	
专业 Специальность 日期 Дата		工艺 Технология 比例 Масштаб 1:100		干吸工序 Процесс сухой абсорбции 施工图 Рабочий проект 3147-56113-06  7 799687 231595	


ВЕРХНИЙ ЭТАЖ

会签	姓名	签名
工艺	Фамилия и имя	Подпись
设备		
起运		
自控		
给排水		
电		
采暖		
建筑		
结构		
总图		
设计		
经理		
审批		

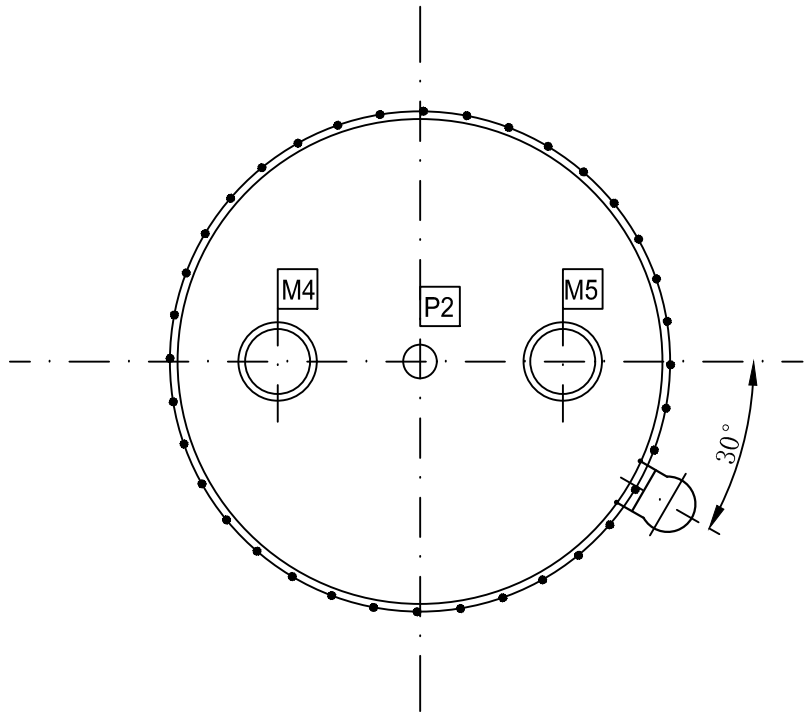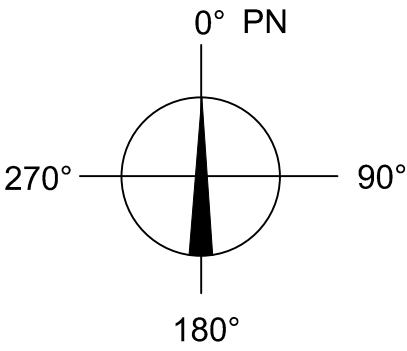

TW-11303
POS EL3.400

Отметка 23.90
EL23.90平面

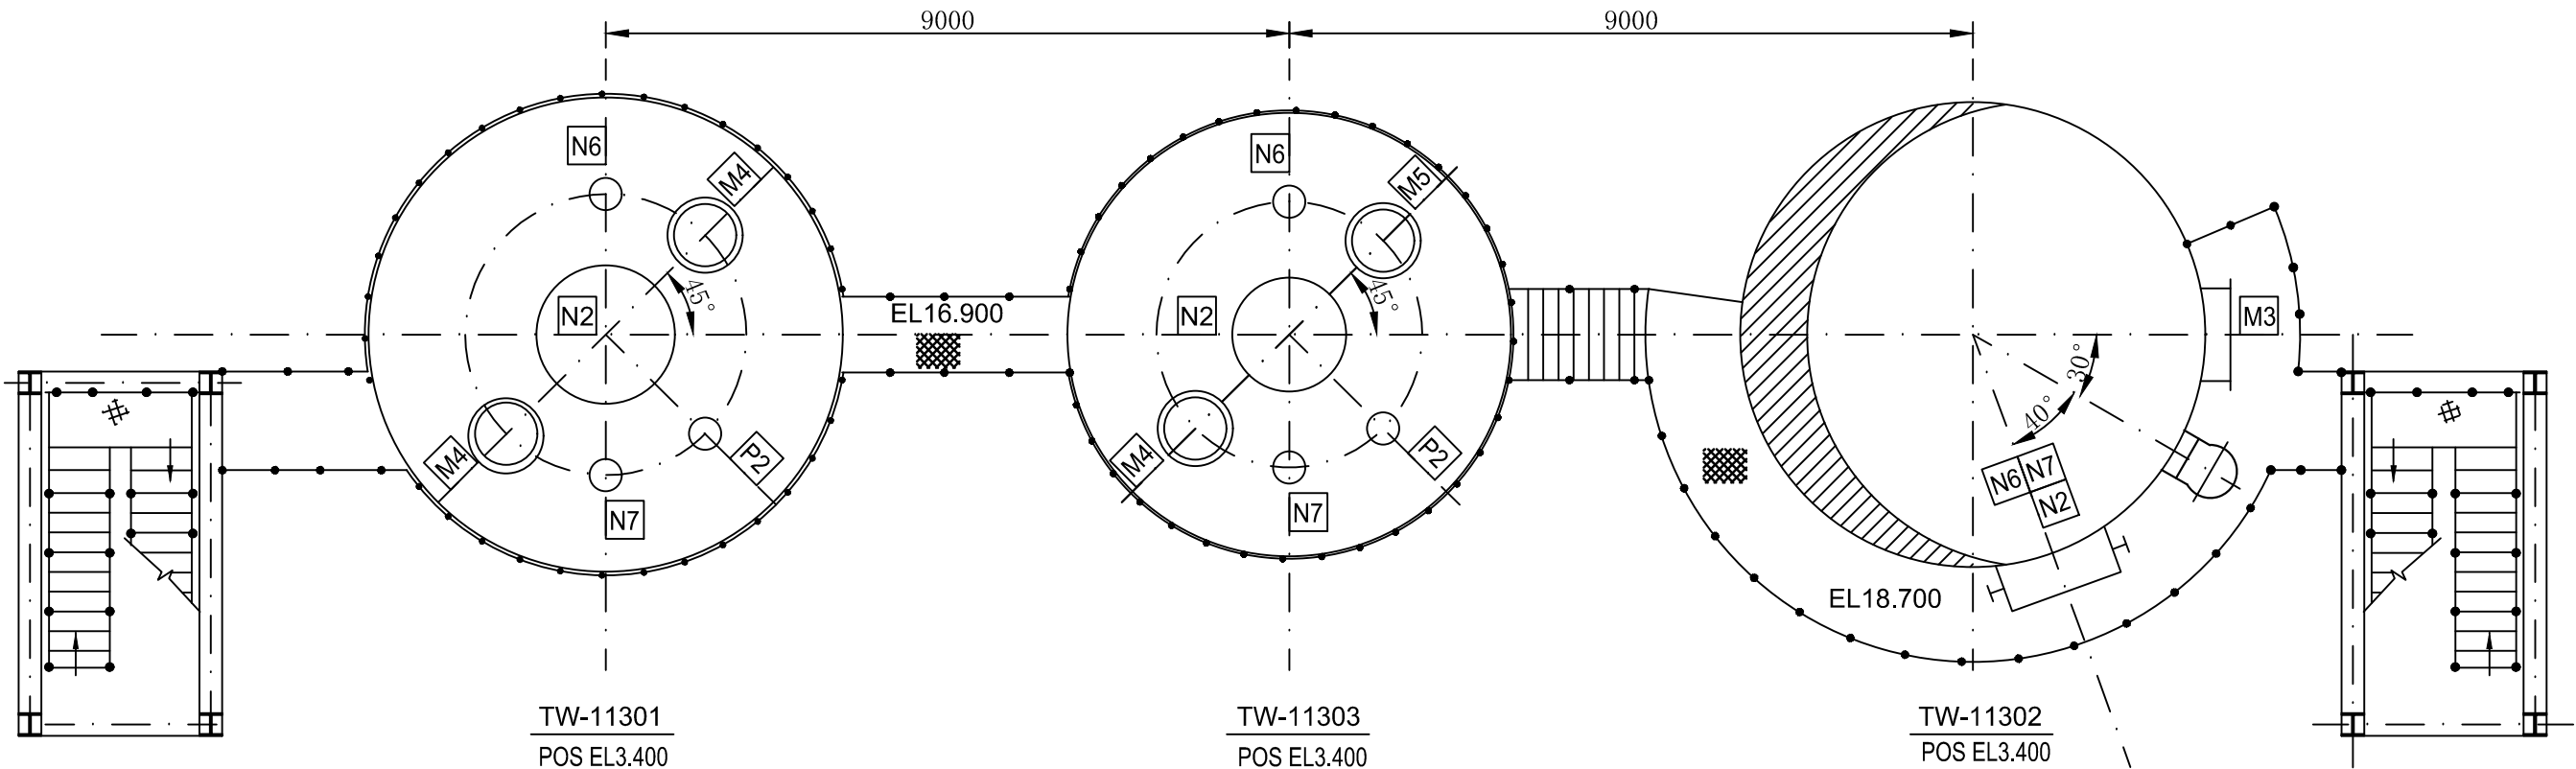


Отметка 16.90
EL16.90 平面

TW-11303	Вторая абсорбционная колонна 二吸塔		
TW-11302	Первая абсорбционная колонна 一吸塔		
TW-11301	Сушильная колонна 干燥塔		

版次	说明	日期
Версия	Примечания	Дата
 云南化工设计院有限公司	 中信建设有限责任公司	
YUNNAN DESIGN INSTITUTE OF CHEMICAL ENGINEERING CO.,LTD.	CITIC Construction Co.,Ltd.	
工程名称	乌兹别克斯坦年产50万吨硫磺制酸项目	工程代号
НАЗВАНИЕ ПРОЕКТА	Uzbekistan UTMK Chemical LLC Проект завода по производству серной кислоты	Код объекта
		3147
	姓名	签名
	Фамилия и имя	Подпись
		日期
		Дата
审定		
Утверждение		
审核	李海昆	李海昆
Рассм.		
校核	董俊	董俊
Проверка		
设计	沈开蜜	沈开蜜
Проектирование		
设备布置图	EL16.90 EL23.90平面	设计项目
Схема размещения оборудования	Отметка 16.90、23.90	Проектируемый объект
图号	第1张	干吸工序
№ чертежа	Лист	Процесс сухой абсорбции
专业	工艺	设计阶段
Специальность	Технология	Стадия проектирования
日期	2026.4	图号
Дата	Версия	№ чертежа
		第1张
		Лист
		共1张
		Листы
		7 7 9 9 6 8 7 1 8 2 8 3 5

D:\2020新图框\2020集中统一新图框\2020管道表格\施工图.png

会签	姓名	签名
工艺	Фамилия и имя	Подпись
设备		
起运		
自控		
给排水		
电		
采暖		
建筑		
结构		
总图		
设计		
经理		
审批		

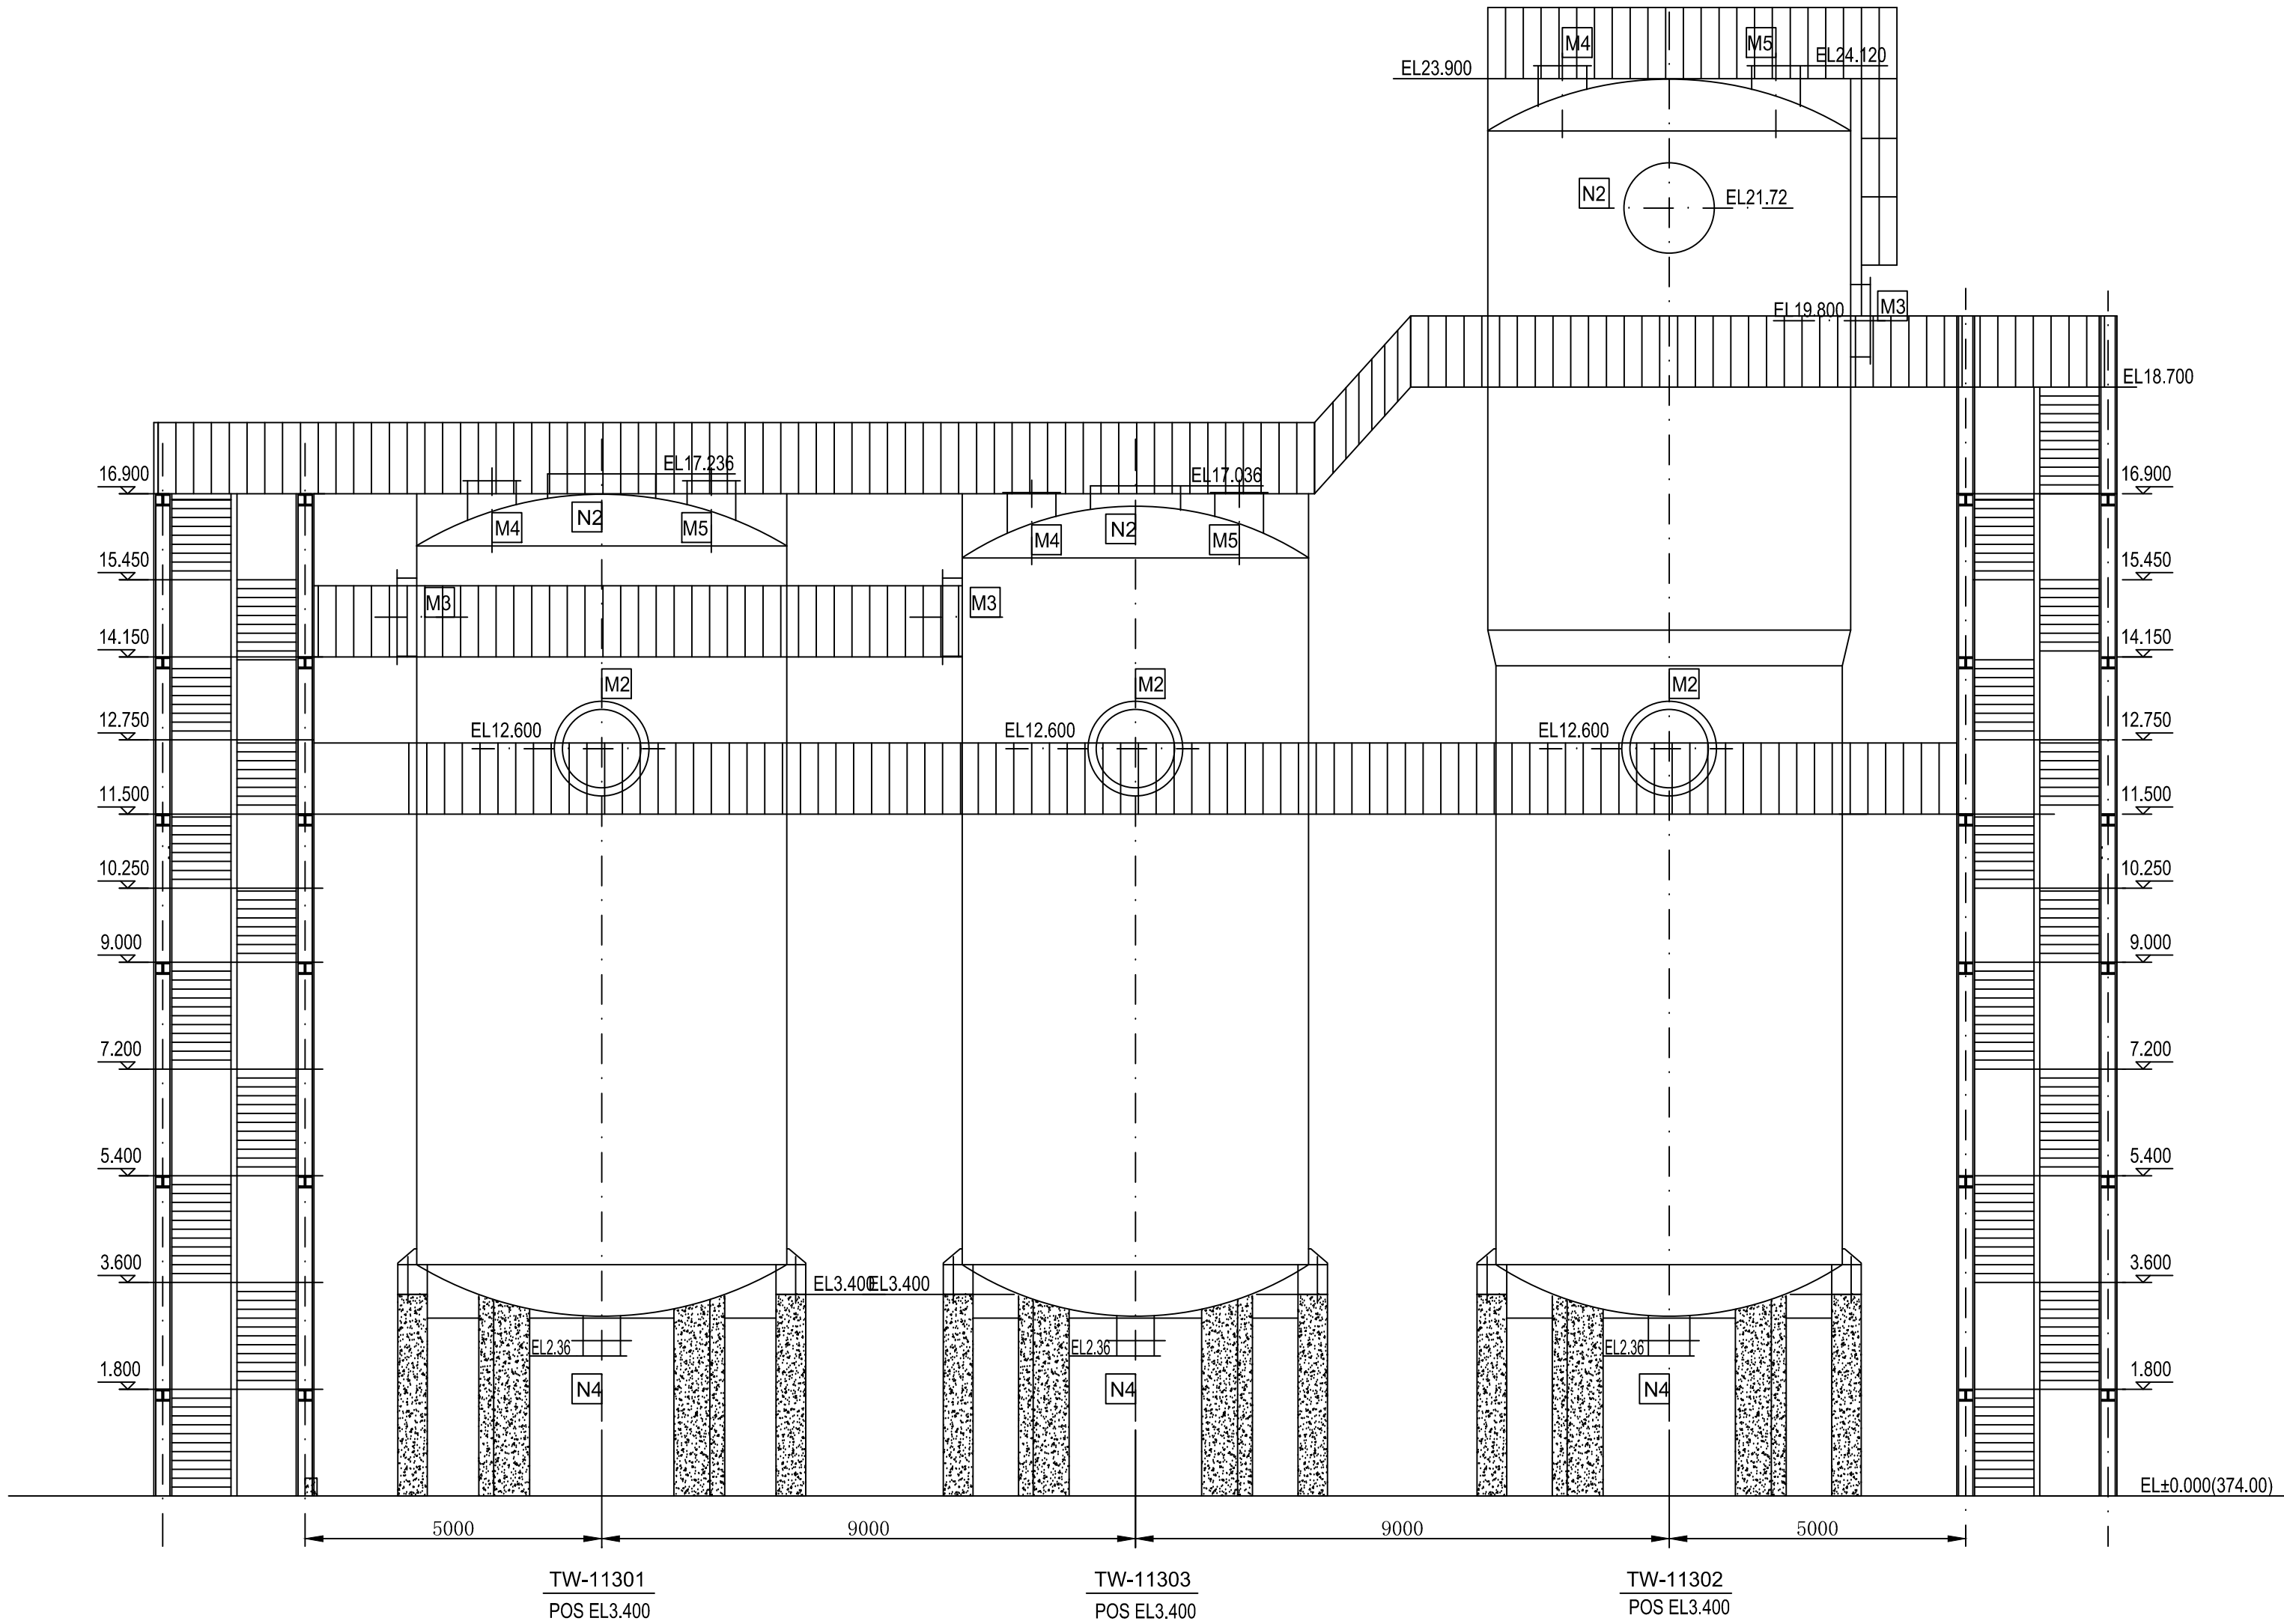

Разрез A-A

A-A 剖面

TW-11303	Вторая абсорбционная колонна 二吸塔		
TW-11302	Первая абсорбционная колонна 一吸塔		
TW-11301	Сушильная колонна 干燥塔		

版次 Версия		说明 Примечания		日期 Дата	
YUNNAN DESIGN INSTITUTE OF CHEMICAL ENGINEERING CO.,LTD.		中信建设 CITIC Construction Co.,Ltd.			
工程名称 НАЗВАНИЕ ПРОЕКТА		乌兹别克斯坦年产50万吨硫磺制酸项目 Uzbekistan UTMK Chemical LLC Проект завода по производству серной кислоты			工程代号 Код объекта 3147
审定 Утверждение	姓名 Фамилия и имя	签名 Подпись	日期 Дата	设备布置图 A-A 剖面 Схема размещения оборудования Разрез A-A	设计项目 Проектируемый объект Процесс сухой абсорбции
审核 Рассм.	李海昆	李海昆		设计阶段 Стадия проектирования 施工图 Рабочий проект	
校核 Проверка	董俊	董俊		图号 № чертёжа 3147-5G113-08	
设计 Проектирование	沈开蜜	沈开蜜		专业 Специальность 工艺 Технология 比例 Масштаб 1:100	第1张 Лист
		日期 Дата 2026.4		版次 Версия	共1张 Листы
				7 799687 165852	