


修改 Изм.	

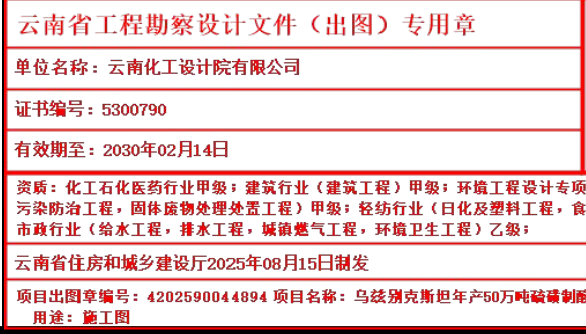

版次		说明		日期					
		Примечания		Дата					
 云南化工设计院有限公司 YUNNAN DESIGN INSTITUTE OF CHEMICAL ENGINEERING CO., LTD.				 中信建设有限责任公司 CITIC Construction Co., Ltd.					
工程名称				乌兹别克斯坦年产50万吨硫磺制酸项目				工程代号	
НАЗВАНИЕ ПРОЕКТА				Uzbekistan UTMK Chemical LLC Проект завода по производству серной кислоты				Код объекта	
								3147	
姓名		签名		日期		设计项目		硫磺库及上料系统	
Фамилия Имя		Подпись		Дата		Проектный объект		Стелла для и системы подачи	
审定 Утверждение		徐晖		2026. 3. 31		(12) 硫磺库及上料系统平面布置图 (12) Сульфидные и системы подачи генеральный план		设计阶段	
								设计阶段 Стadia проектирования	
审核 Рассм.		王伟民		2026. 3. 31		专业 Специальность		详细设计 детальное проектирование	
设计 Проектирование		鲁元润		2026. 3. 31		日期 Дата		图号 № чертежа	
								3147-5t/m2121-04	
						比例 Масштаб		1:200	
						版次 Версия		第 1 张 Листы	
						Rev. 0		共 1 张 Листы	

ВЕСЕ ПРАВА ЗАШТИЩЕНИ УДИС. ДАНИЈИ ЧЕРТЕЖ НЕ МОЖЕ БИТИ ПРЕУСТУПЛЕН, ПЕРЕДАН, СКОПИРОВАН, РАСКРИТ ТРЕЋИМ ЛИЦАМ, А ТАКЖЕ ИСПОЛЪЗОВАН ПОЯ ДРУГИХ ЦЕЛЕЙ БЕЗ РАЗРЕШЕНИЯ УДИС.

修改 1/3M	



云南省工程勘察设计文件《出图》专用章

单位名称：云南化工设计研究院有限公司

证书编号：53300790

有效期限：2025年02月14日

类别：化工石化医药行业甲类；建筑行业甲类（建筑工程专业）；环境工程设计专业乙类；给排水领域专业设计工程；给排水专业（给水及排水工程、市政行业（给水工程）、排水工程、城镇燃气工程、环境卫生工程）乙类；

云南省住房和城乡建设厅2025年08月15日核发


项目工程编号：420250944894 项目名称：乌兹别克前年生产40万吨碱金属

输出：盖图

版次 Версия		说明 Примечания		日期 Дата	
 云南化工设计院有限公司 YUNNAN DESIGN INSTITUTE OF CHEMICAL ENGINEERING CO., LTD.		 中信建设有限责任公司 CITIC Construction Co., Ltd.			
工程名称 НАЗВАНИЕ ПРОЕКТА		乌兹别克斯坦年产50万吨硫酸项目 Uzbekistan UTMK Chemical LLC Проект завода по производству серной кислоты			
工程代号 Код объекта		3147			
姓名 Фамилия	签名 Подпись	日期 Дата	(12) 硫酸库及上料系统总平面布置图 А-1剖面图 (12) Склад серы и система подачи сыпучей серы Профиль А-А		
审定 Утверждение	徐琛	2026. 3. 31	设计项目 Проектный этап 硫酸库及上料系统 Склад серы и система подачи		
审核 Рассм.	王伟民	2026. 3. 31	设计阶段 Стадия проектирования 图号 Лист		
设计 Проектирование	曹元润	2026. 3. 31	专业 Специальность 机运 Механизация 比例 Масштаб 1:60 版次 Версия Rev. 0 共 1 系 Листы 3147-5hg121-05		

ВЕСЕ ПРАВА ЗАШТИЩЕНИ УДИС. ДАНИЈИ ЧЕРТЕЖ НЕ МОЖЕ БИТИ ПРЕУСТУПЛЕН, ПЕРЕДАН, СКОПИРОВАН, РАСКРИТ ТРЕЋИМ ЛИЦАМ, А ТАКЖЕ ИСПОЛЪЗОВАН ПОЯ ДРУГИХ ЦЕЛЕЙ БЕЗ РАЗРЕШЕНИЯ УДИС.

会签	姓名	签名
1. 设计	姓名	签名
2. 设备	姓名	签名
3. 总图	姓名	签名
4. 自控	姓名	签名
5. 给排水	姓名	签名
6. 电	姓名	签名
7. 暖通	姓名	签名
8. 建筑	姓名	签名
9. 结构	姓名	签名
10. 总图	姓名	签名
11. 设计	姓名	签名

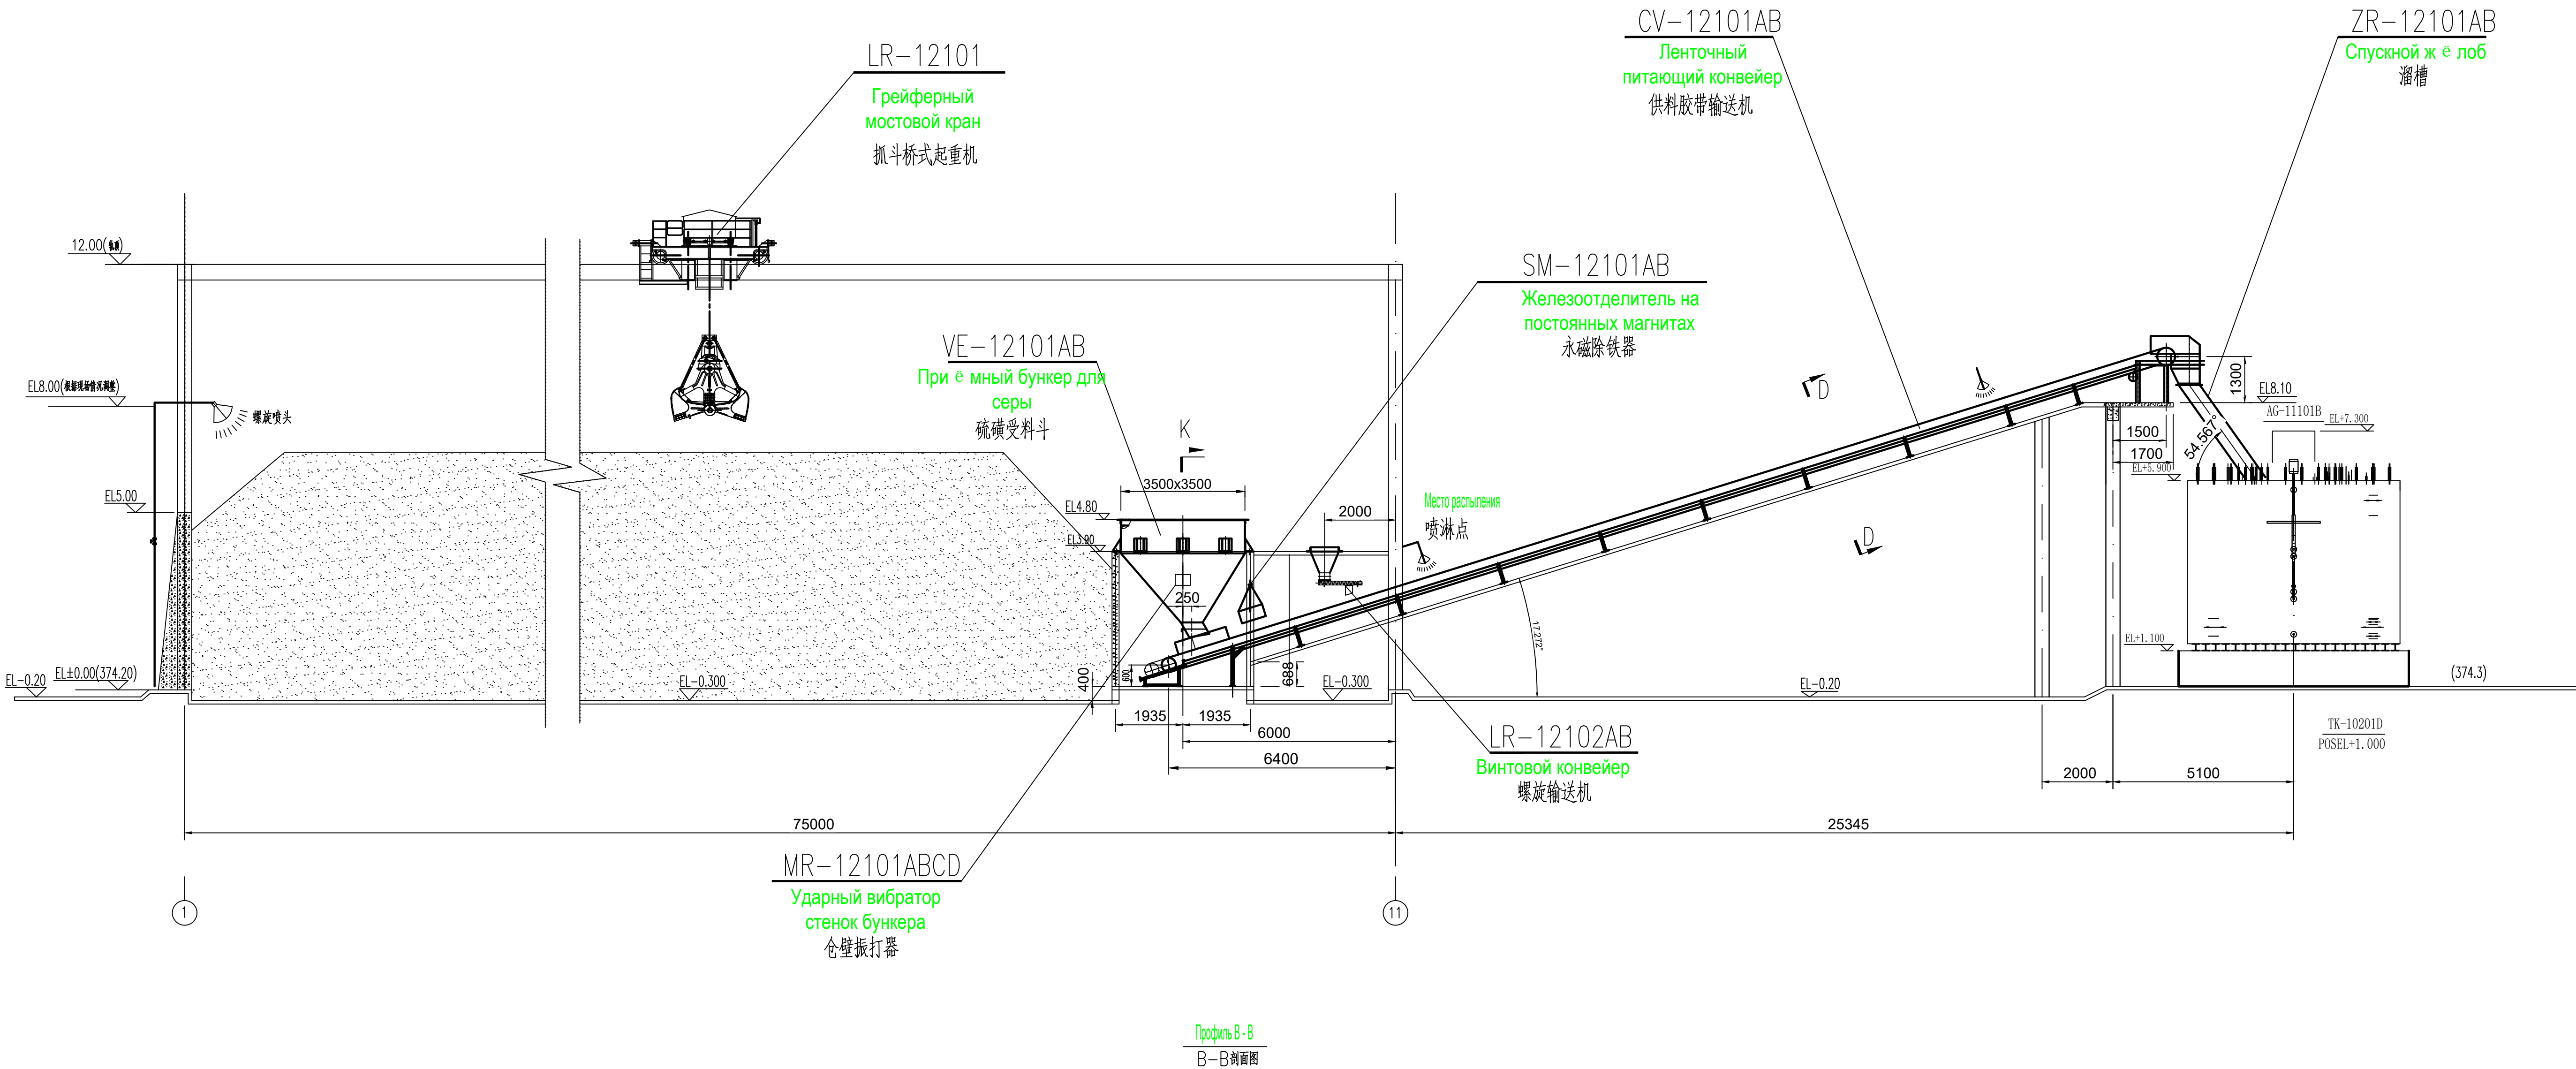

版次	说明	日期
Версия	Примечания	Дата
云南化工设计院有限公司 YUNNAN DESIGN INSTITUTE OF CHEMICAL ENGINEERING CO., LTD.		
中信建设有限责任公司 CITIC Construction Co., Ltd.		
工程名称	乌兹别克斯坦年产50万吨硫酸制酸项目	工程代号
НАЗВАНИЕ ПРОЕКТА	Uzbekistan UTMK Chemical LLC Проект завода по производству серной кислоты	Код объекта
姓名	签名	日期
Фамилия и имя	Подпись	Дата
审核	徐辉	2026. 3. 31
Рассм.	徐辉	2026. 3. 31
校核	王伟民	2026. 3. 31
Проверка	王伟民	2026. 3. 31
设计	鲁元润	2026. 3. 31
Проектирование	鲁元润	2026. 3. 31
专业	机运	比例
Специальность	Механизация	Масштаб
日期	2026	版次
Дата	2026	Версия
Rev. 0	1:100	第 1 张
Лист	共 1 张	Листы
1	1	1

云南省工程勘察设计院有限公司	单位名称：云南化工设计院有限公司	证书编号：S3007960	有效期至：2030年02月14日
设计阶段	施工图设计	图号	3147-Slg121-06
设计项目	硫酸库及上料系统	设计阶段	施工图设计
设计项目	硫酸库及上料系统	设计阶段	施工图设计

版权所有云南化工设计院有限责任公司所有，未经本公司许可不得转让、复制、泄露给第三方或用于其他目的
ВСЕ ПРАВА ЗАЩИЩЕНЫ ЮИС. ДАННЫЙ ЧЕРТЕЖ НЕ МОЖЕТ БЫТЬ ПЕРЕУСТУПЛЕН, ПЕРЕДАН, СКОПИРОВАН, РАСКРЫТ ТРЕТЬИМ ЛИЦАМ, А ТАКЖЕ ИСПОЛЬЗОВАН ДЛЯ ДРУГИХ ЦЕЛЕЙ БЕЗ РАЗРЕШЕНИЯ ЮИС.