


会签	姓名	签名
Design	Signature	Signature
1. 设计		
设备		
Design		
总图		
Design		
自控		
Design		
给排水		
Design		
电		
Design		
热工		
Design		
建筑		
Design		
结构		
Design		
总图		
Design		

设计	姓名	签名
Design	Signature	Signature
1. 设计		
设备		
Design		
总图		
Design		
自控		
Design		
给排水		
Design		
电		
Design		
热工		
Design		
建筑		
Design		
结构		
Design		
总图		
Design		

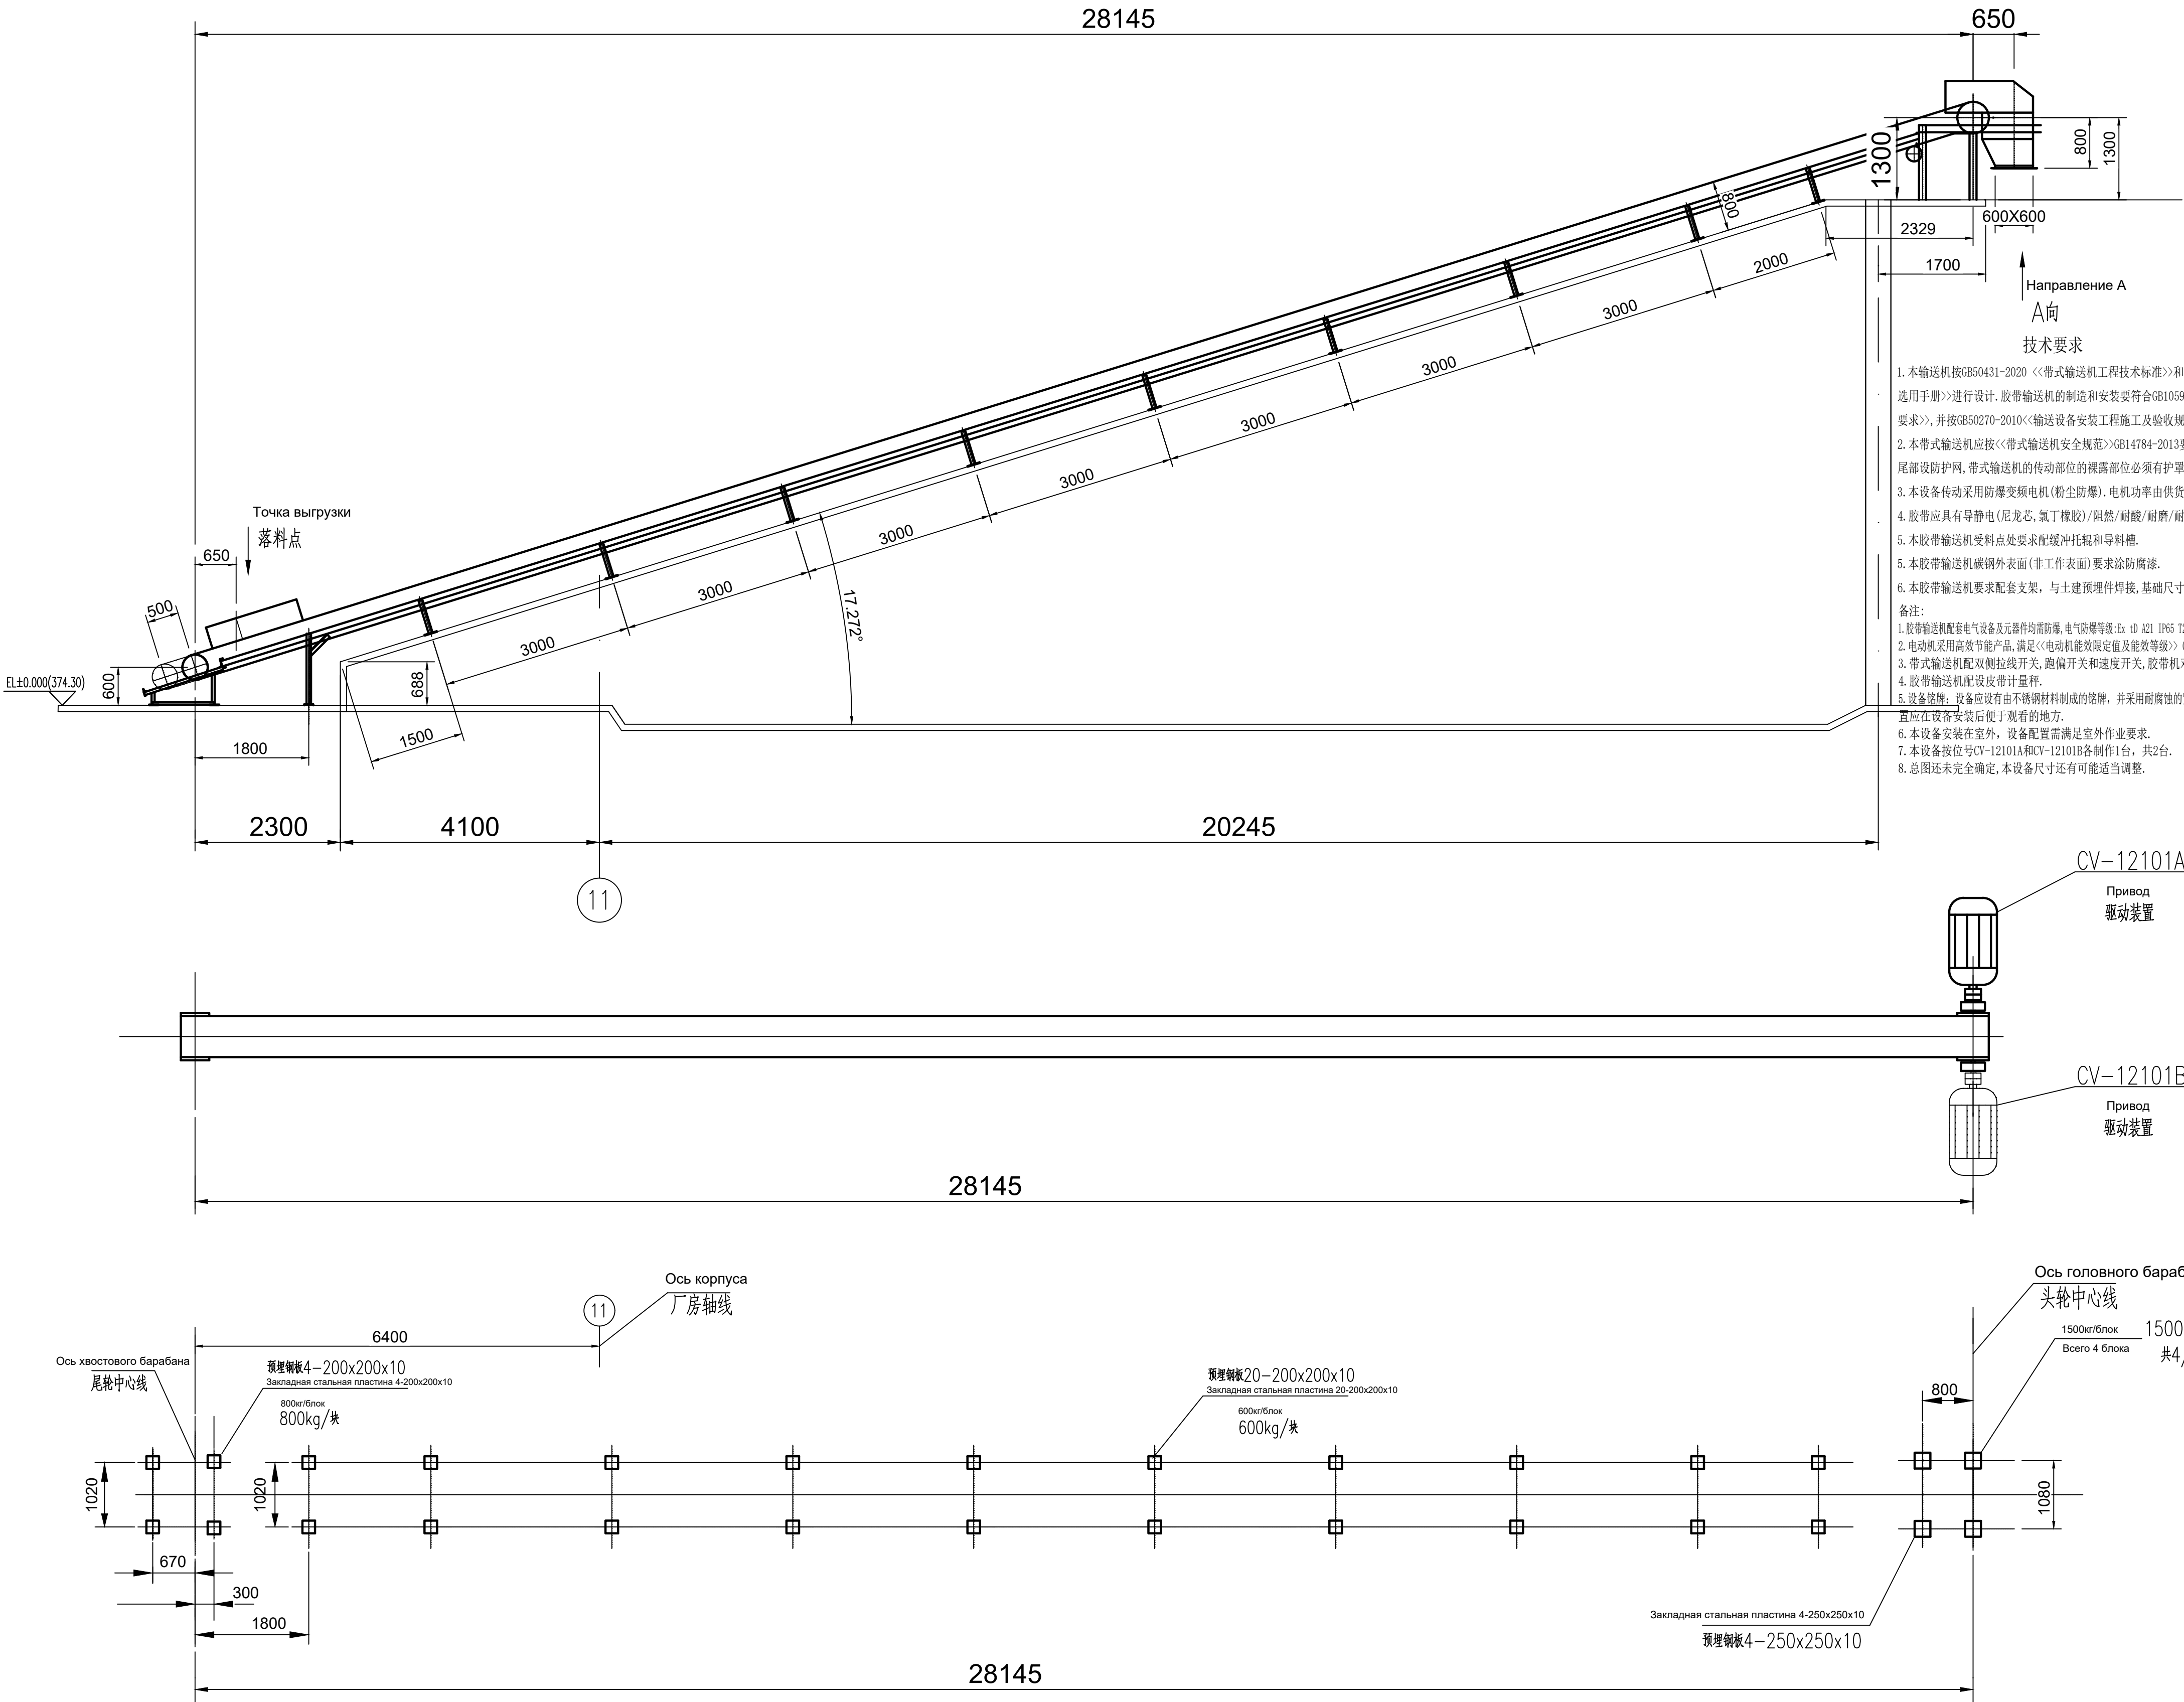

- 技术要求
1. 本输送机按GB50431-2020《带式输送机工程技术标准》和《TD75型通用固定式带式输送机选用手册》进行设计, 胶带给送机的制造和安装要符合GB10595-2009《带式输送机技术条件的要求》, 并按GB50270-2010《输送设备安装工程施工及验收规范》进行安装和验收。
 2. 本带式输送机应按《带式输送机安全规范》GB14784-2013要求配置安全防护设施, 胶带机尾部设防护网, 带式输送机的传动部位的裸露部位必须有护栏, 并固定牢固。
 3. 本设备传动采用防爆变频电机(粉尘防爆), 电机功率由供货前核实确定。
 4. 胶带应具有防静电(尼龙芯、氯丁橡胶)/阻燃/耐酸/耐磨/耐寒性能。
 5. 本胶带给送机受料点处要求配缓冲托辊和导料槽。
 5. 本胶带给送机碳钢外表面(非工作表面)要求涂防腐漆。
 6. 本胶带给送机要求配支架, 与土建预埋件焊接, 基础尺寸应按本图要求配置。
- 备注:
1. 胶带给送机配套电气设备元件均需防腐, 电气防爆等级: Ex d IIB T200°C, IP55(防护等级), F(绝缘等级)。
 2. 电动机采用高效节能产品, 满足《电动机能效限定值及能效等级》GB18613-2020 中的能效Ⅱ级要求。
 3. 带式输送机配双侧拉线开关, 跑偏开关和速度开关, 胶带机双侧设可拆卸防护网。
 4. 胶带给送机配皮带计量秤。
 5. 设备铭牌: 设备应设有由不锈钢材料制成的铭牌, 并用耐腐蚀的紧固件将其固定在设备上, 其位置应在设备安装后便于观看的地方。
 6. 本设备安装在室外, 设备配置需满足室外作业要求。
 7. 本设备按位号CV-12101A和CV-12101B各制作1台, 共2台。
 8. 总图还未完全确定, 本设备尺寸还有可能适当调整。



技术特征表		Таблица технических характеристик	
Transportation materials 输送物料	Material 物料	Твердый сера 固体硫磺	Ширина ленты 胶带宽
	Размер частиц материала 物料粒度	0~10mm	Кол-во слоев ленты 胶带层数
	Удельный вес шихты 物料堆比重	1.35~1.44t/m ³	Материал ленты 胶带材质
	Рабочая температура 工作温度	Температура окружающей среды 环境温度	Толщина верхнего клея 上胶厚
Ленточный конвейер 槽型输送机	Объем транспортируемого 输送量	0~70t/h	Толщина нижнего клея 下胶厚
	Скорость ленты 胶带速度	<0.8m/s	Способ соединения 接头方式
	Длина горизонтальной проекции 水平投影长度	28145 mm	Длина кольца ленты 胶带环长
	Угол наклона транспортировки 输送倾角	17.272°	Тип натяжения ленты 胶带张紧形式
Привод 驱动装置	Тип привода 驱动装置类型	Стандарт 规格	Тормоз и реверс 制动器和反转器
	Мощность электродвигателя 电机功率	11 KW	Расстояние между роликми 托辊间距
			Расстояние между осями роликов 胶带支腿间距

Технические требования

1. Данный ленточный конвейер проектируется в соответствии с GB50431-2020 «Технический стандарт на ленточный конвейер» и «Руководство по выбору универсального стационарного ленточного конвейера типа TD75». Изготовление и монтаж ленточного конвейера должны соответствовать требованиям GB10595-2009 «Технические условия ленточного конвейера», а монтаж и приемка должны проводиться в соответствии с GB50270-2010 «Правила производства и приемки работ по монтажу конвейерного оборудования».
2. Данный ленточный конвейер должен быть оборудован защитными средствами в соответствии с «Правилами безопасности ленточного конвейера» GB14784-2013, хвостовая часть ленточного конвейера должна иметь защитную сетку, открытая часть приводной части ленточного конвейера должна иметь защитный кожух и быть надежно закреплена.
3. Для привода данного оборудования применяется взрывобезопасный электродвигатель с переменной частотой (пылезащитный). Мощность электродвигателя определяется поставщиком.
4. Лента должна обладать электростатическими свойствами (нейлоновый сердечник, неопрен)/огнестойкостью/кислотостойкостью/износостойкостью/морозостойкостью.
5. На месте приема материала ленточного конвейера необходимо предусмотреть буферный опорный ролик и направляющий желоб.
5. Наружная поверхность углеродистой стали (нерабочая поверхность) ленточного конвейера должна быть покрыта антикоррозийной краской.
6. Для ленточного конвейера требуется комплектная опора, которая сваривается с архитектурно - строительными закладными деталями, размеры фундамента должны соответствовать требованиям в данном чертеже.

Примечание:

1. Электрооборудование и комплектующие элементы ленточного конвейера должны быть взрывозащитными, класс взрывозащитности: Ex ID A21 IP65 T200 °C, IP55 (класс защиты), F (класс изоляции).
2. Для электродвигателя применяется высокоэффективная и энергосберегающая продукция, которая отвечает требованиям класса II по энергоэффективности в GB18613-2020.
3. Ленточный конвейер оснащается с обеих сторон тросовыми выключателями (аварийными стопорами), датчиками схода ленты и датчиками контроля скорости. По обеим сторонам конвейера устанавливаются съёмные защитные сетки.
4. Ленточный конвейер оборудован ленточными измерительными весами.
5. Табличка оборудования: на оборудовании следует установить табличку из нержавеющей стали, закрепить ее на оборудовании коррозионностойкими крепежами, ее место должно быть удобным для просмотра после монтажа оборудования.
6. Данное оборудование устанавливается на открытом воздухе, компоновка оборудования должна соответствовать требованиям к наружным работам.
7. Данное оборудование изготовлено по поз. CV-12101A и CV-12101B по 1 шт., всего 2 шт.
8. Генплан еще не полностью определен, размеры данного оборудования могут регулироваться соответствующим образом.

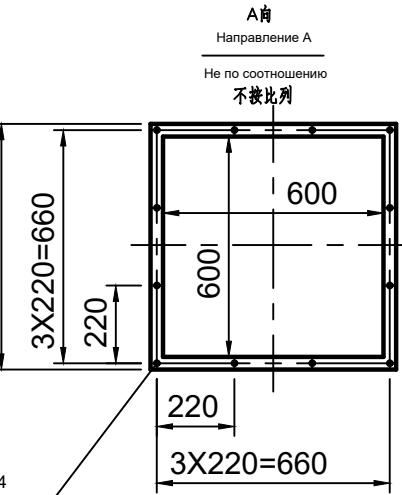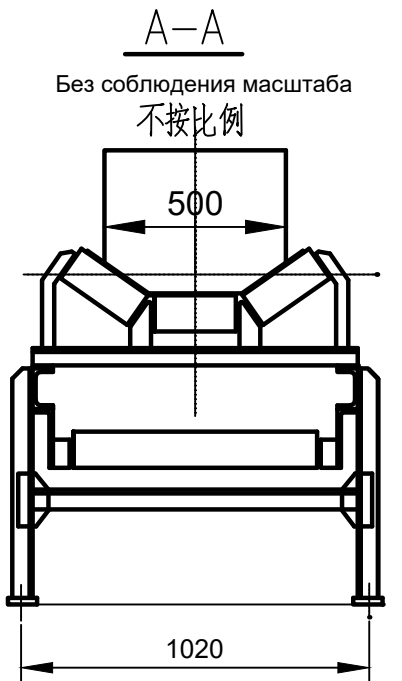

版本		说明	日期
Версия		Примечания	Дата
云南化工设计院有限公司		中信建设有限责任公司	
YUNNAN DESIGN INSTITUTE OF CHEMICAL ENGINEERING CO., LTD.		CITIC Construction Co., Ltd.	
工程名称	乌兹别克斯坦年产50万吨硫磺制酸项目		工程代号
НАЗВАНИЕ ПРОЕКТА	Uzbekistan UTMK Chemical LLC Проект завода по производству серной кислоты		3147
姓名	签名	日期	设计项目
Фамилия и имя	Подпись	Дата	Проектный объект
审核	审核	2026. 3. 31	硫磺库及上料系统
Рис.	Рис.		Склад серы и система подачи
校核	王保民	2026. 3. 31	设计阶段
Проверка	王保民		Статус проектирования
设计	崔元刚	2026. 3. 31	图号
Проектирование	崔元刚		3147-Slg121-07
专业	机运	比例	1:60
Специальность	Мехатроника	Масштаб	1:60
日期	2026	版次	第 1 张
Дата	2026	Версия	Лист
			共 1 张
			Листы

云南省工程勘察设计院(出图)专用章

单位名称: 云南化工设计院有限公司

证书编号: S300790

有效期至: 2030年02月14日

说明: 化工石化医药行业甲级、建筑行业(建筑工程)甲级、环境工程设计专项(水污染防治工程、大气污染防治工程、固体废物处理处置工程)甲级、市政公用工程(给水及排水工程、食品工业工程、乙类危险品工程、燃气工程、热力工程、城镇燃气工程、环境卫生工程)乙级。

云南省住房和城乡建设厅2025年08月15日颁发

项目北图章编号: 4302590844894 项目名称: 乌兹别克斯坦年产50万吨硫磺制酸项目

用途: 出图用