





净水站流程图

Water Purification Station Flow Diagram

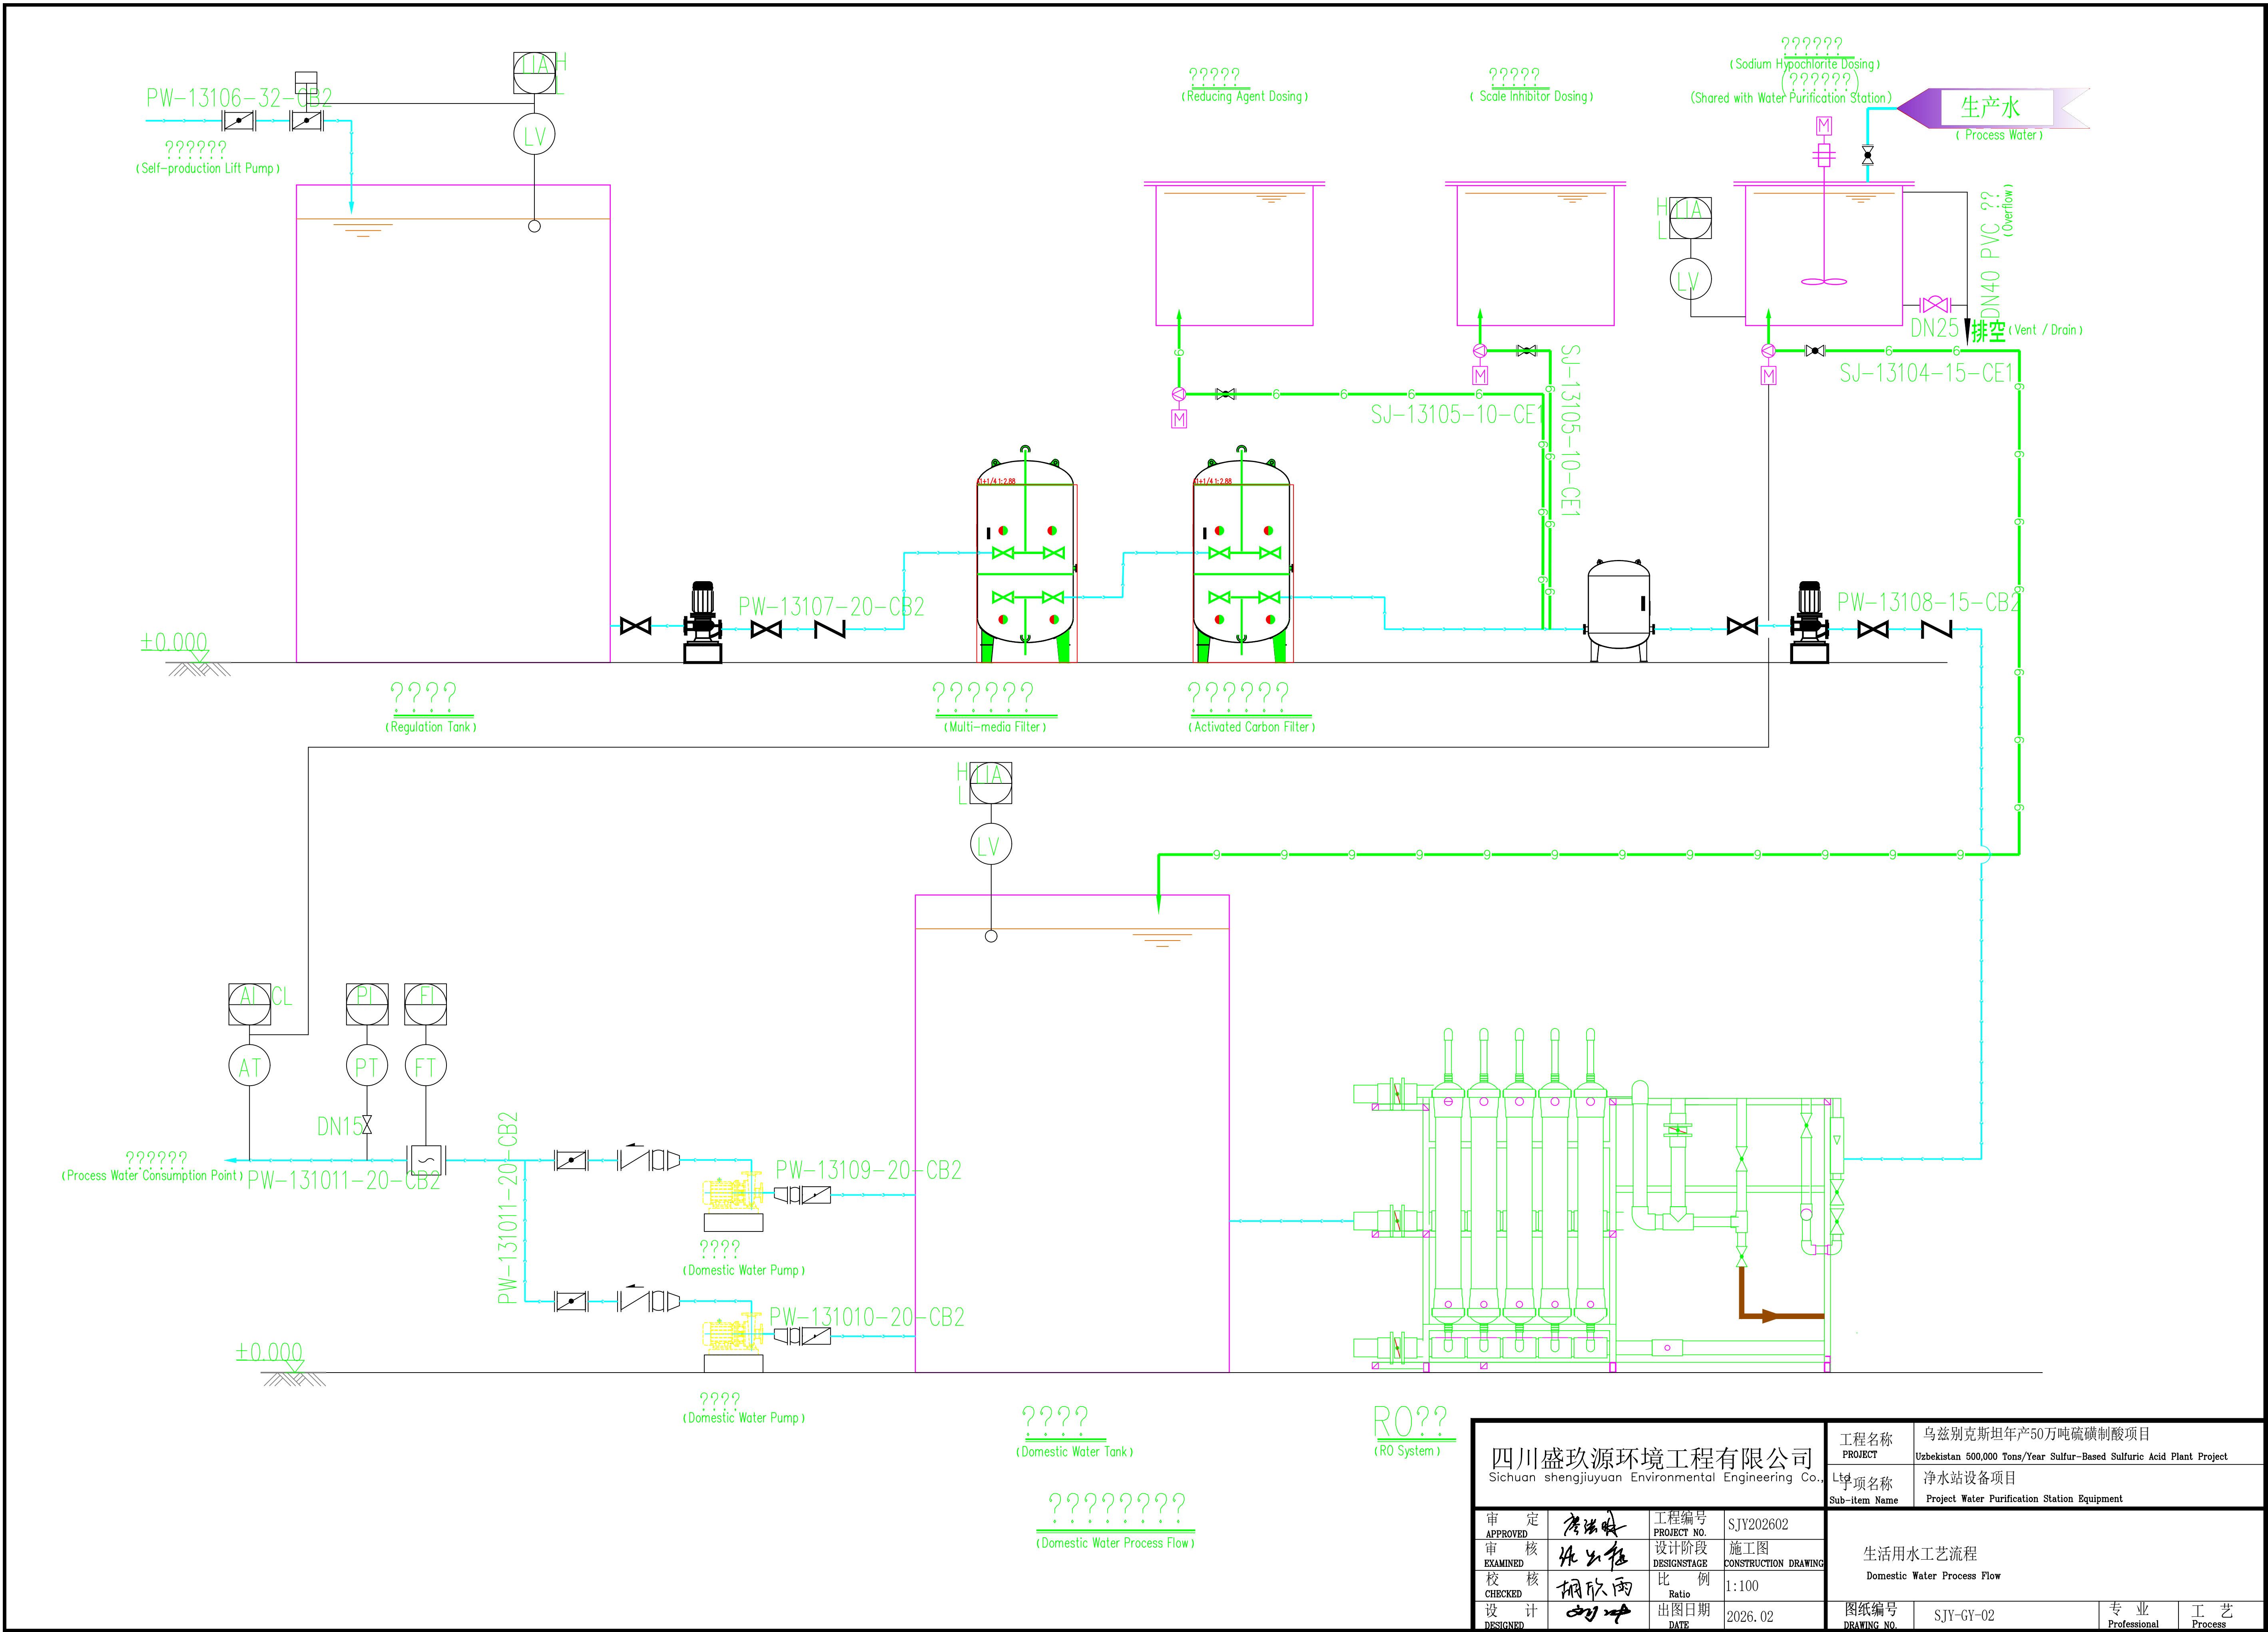

四川盛玖源环境工程有限公司 Sichuan shengjiuyuan Environmental Engineering Co.,		工程名称 PROJECT	乌兹别克斯坦年产50万吨硫磺制酸项目 Uzbekistan 500,000 Tons/Year Sulfur-Based Sulfuric Acid Plant Project		
		子项名称 Sub-Item Name	净水站设备项目 Project Water Purification Station Equipment		
审定 APPROVED	设计阶段 DESIGNSTAGE	工程编号 PROJECT NO.	生活用水工艺流程 Domestic Water Process Flow		
审核 EXAMINED	比例 Ratio	施工图 CONSTRUCTION DRAWING			
校核 CHECKED	出图日期 DATE	比例 Ratio	图纸编号 DRAWING NO.	SJY-GY-02	专业 Professional
设计 DESIGNED		2026. 02			工艺 Process

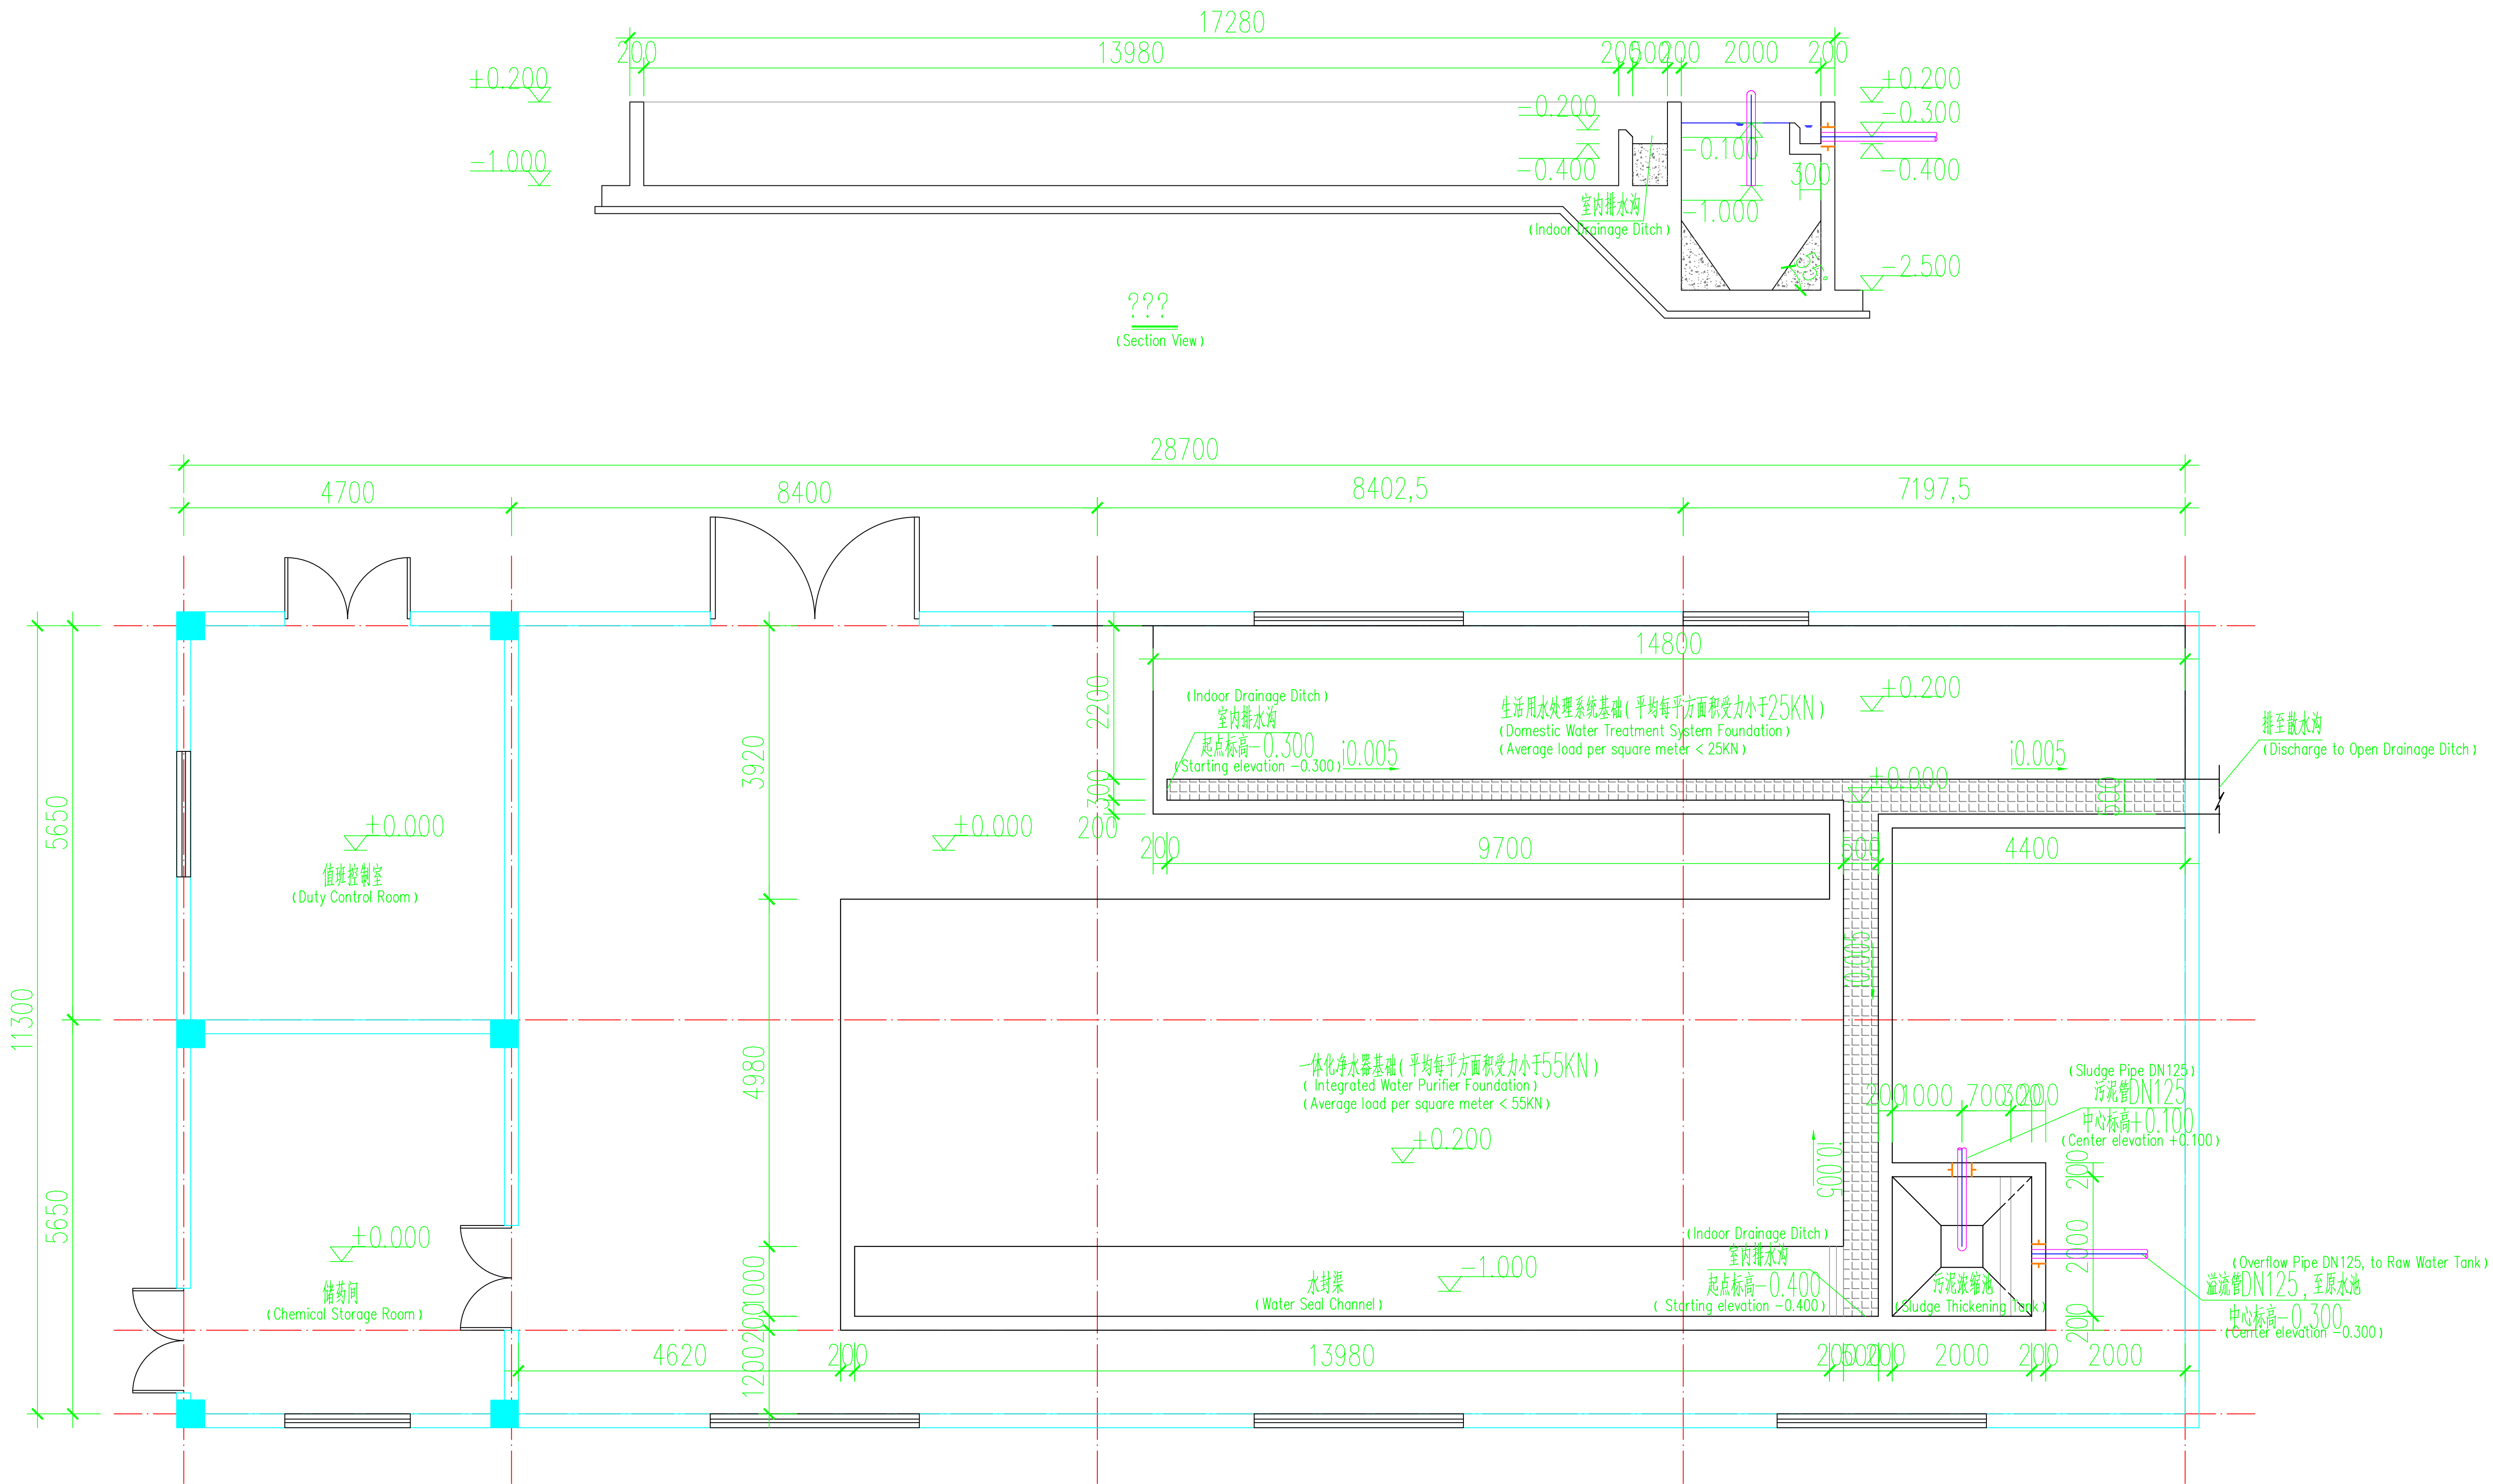

说明:


- 1、本设计尺寸单位: 标高以米计, 其余以毫米计。
- 2、本工程设计一套一体化净水器、一套生活水净水系统。
- 3、一体化净水器设计处理水量200m³/h。
- 4、室内排水沟需加盖板, 以便操作人员通行。

Notes:

- 1.Units of measurement in this design: Elevations are in meters, all other dimensions are in millimeters.
- 2.This project includes one integrated water purifier and one domestic water purification system.
- 3.Design flow rate of the integrated water purifier is 200m³/h.
- 4.Indoor drainage ditches shall be covered with plates for operator access.


????????
(Water Purification Station Civil Layout Drawing)

四川盛玖源环境工程有限公司 Sichuan shengjiuyuan Environmental Engineering Co.,				工程名称 PROJECT		乌兹别克斯坦年产50万吨硫磺制酸项目 Uzbekistan 500,000 Tons/Year Sulfur-Based Sulfuric Acid Plant Project		
				子项名称 Sub-item Name		净水站设备项目 Project Water Purification Station Equipment		
审 定 APPROVED		张洪林	工程编号 PROJECT NO.	SJY202602	净水站土建布置图 Water Purification Station Civil Layout Drawing			
审 核 EXAMINED		张洪林	设计阶段 DESIGNSTAGE	施工图 CONSTRUCTION DRAWING				
校 核 CHECKED		胡欣雨	比 例 Ratio	1:100				
设 计 DESIGNED		胡欣雨	出图日期 DATE	2026. 02				
				图纸编号 DRAWING NO.		SJY-GY-03	专 业 Professional	工 艺 Process

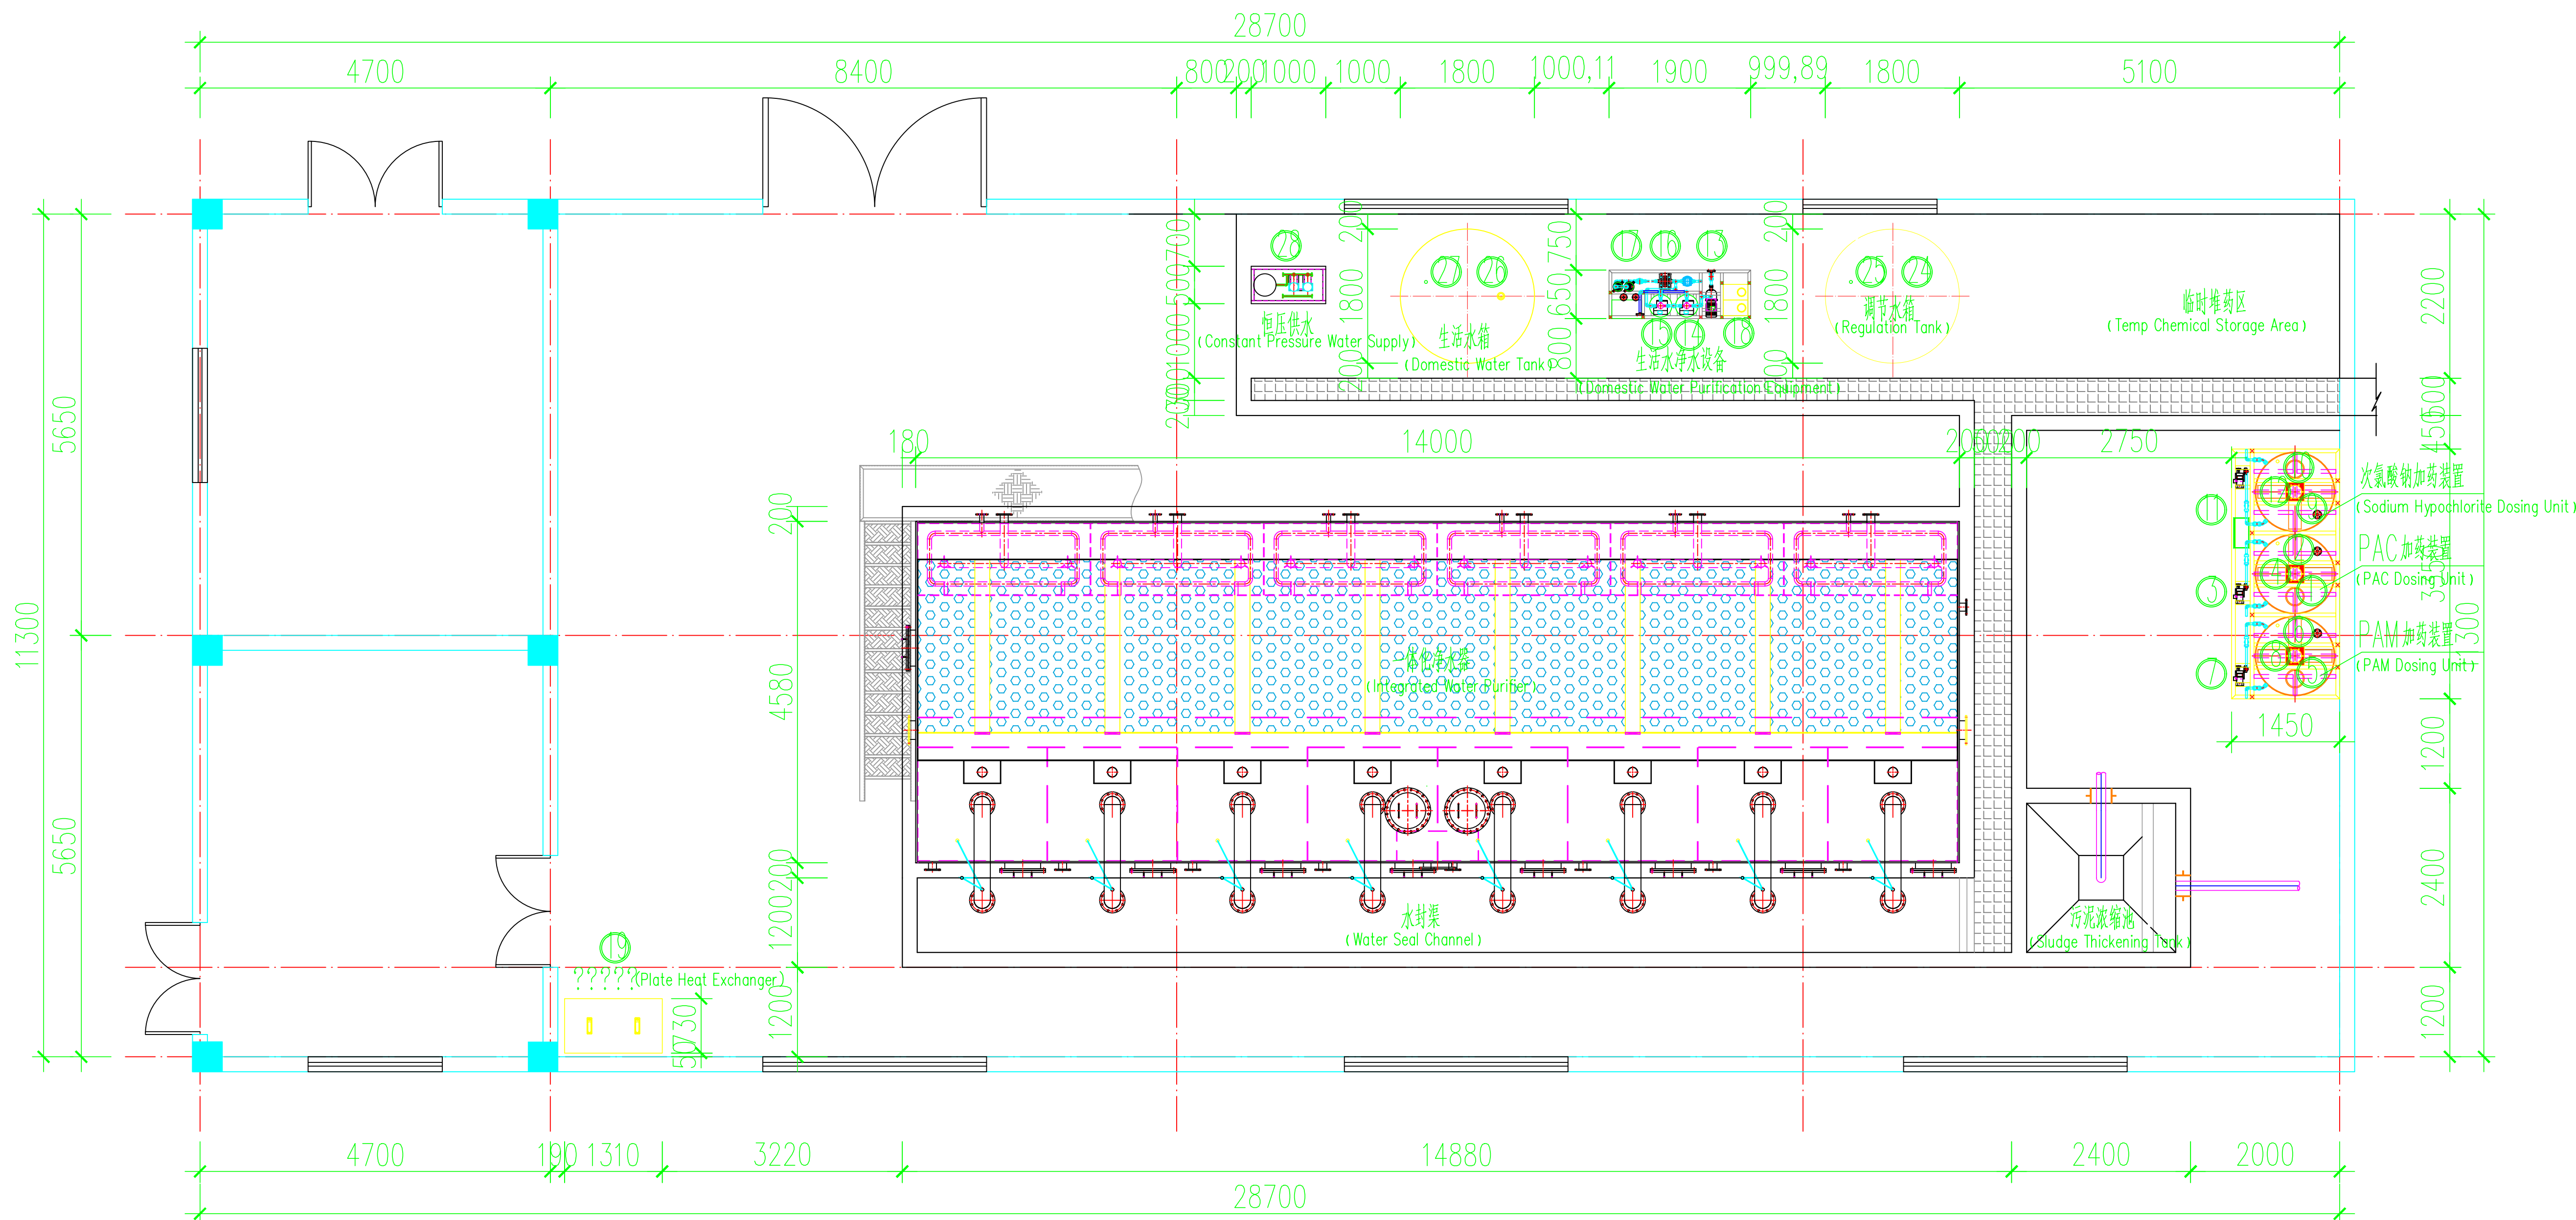

????????????
(Water Purification Station Equipment Layout Plan)

四川盛玖源环境工程有限公司 Sichuan shengjiuyuan Environmental Engineering Co.,				工程名称 PROJECT	乌兹别克斯坦年产50万吨硫磺制酸项目 Uzbekistan 500,000 Tons/Year Sulfur-Based Sulfuric Acid Plant Project		
				子项名称 Sub-Item Name	净水站设备项目 Project Water Purification Station Equipment		
审 定 APPROVED	张洪林	工程编号 PROJECT NO.	SJY202602	净水站设备定位平面布置 Water Purification Station Equipment Layout Plan			
审 核 EXAMINED	张公征	设计阶段 DESIGNSTAGE	施工图 CONSTRUCTION DRAWING				
校 核 CHECKED	胡欣雨	比 例 Ratio	1:100				
设 计 DESIGNED	胡欣雨	出图日期 DATE	2026.02				
				图纸编号 DRAWING NO.	SJY-GY-04	专 业 Professional	工 艺 Process

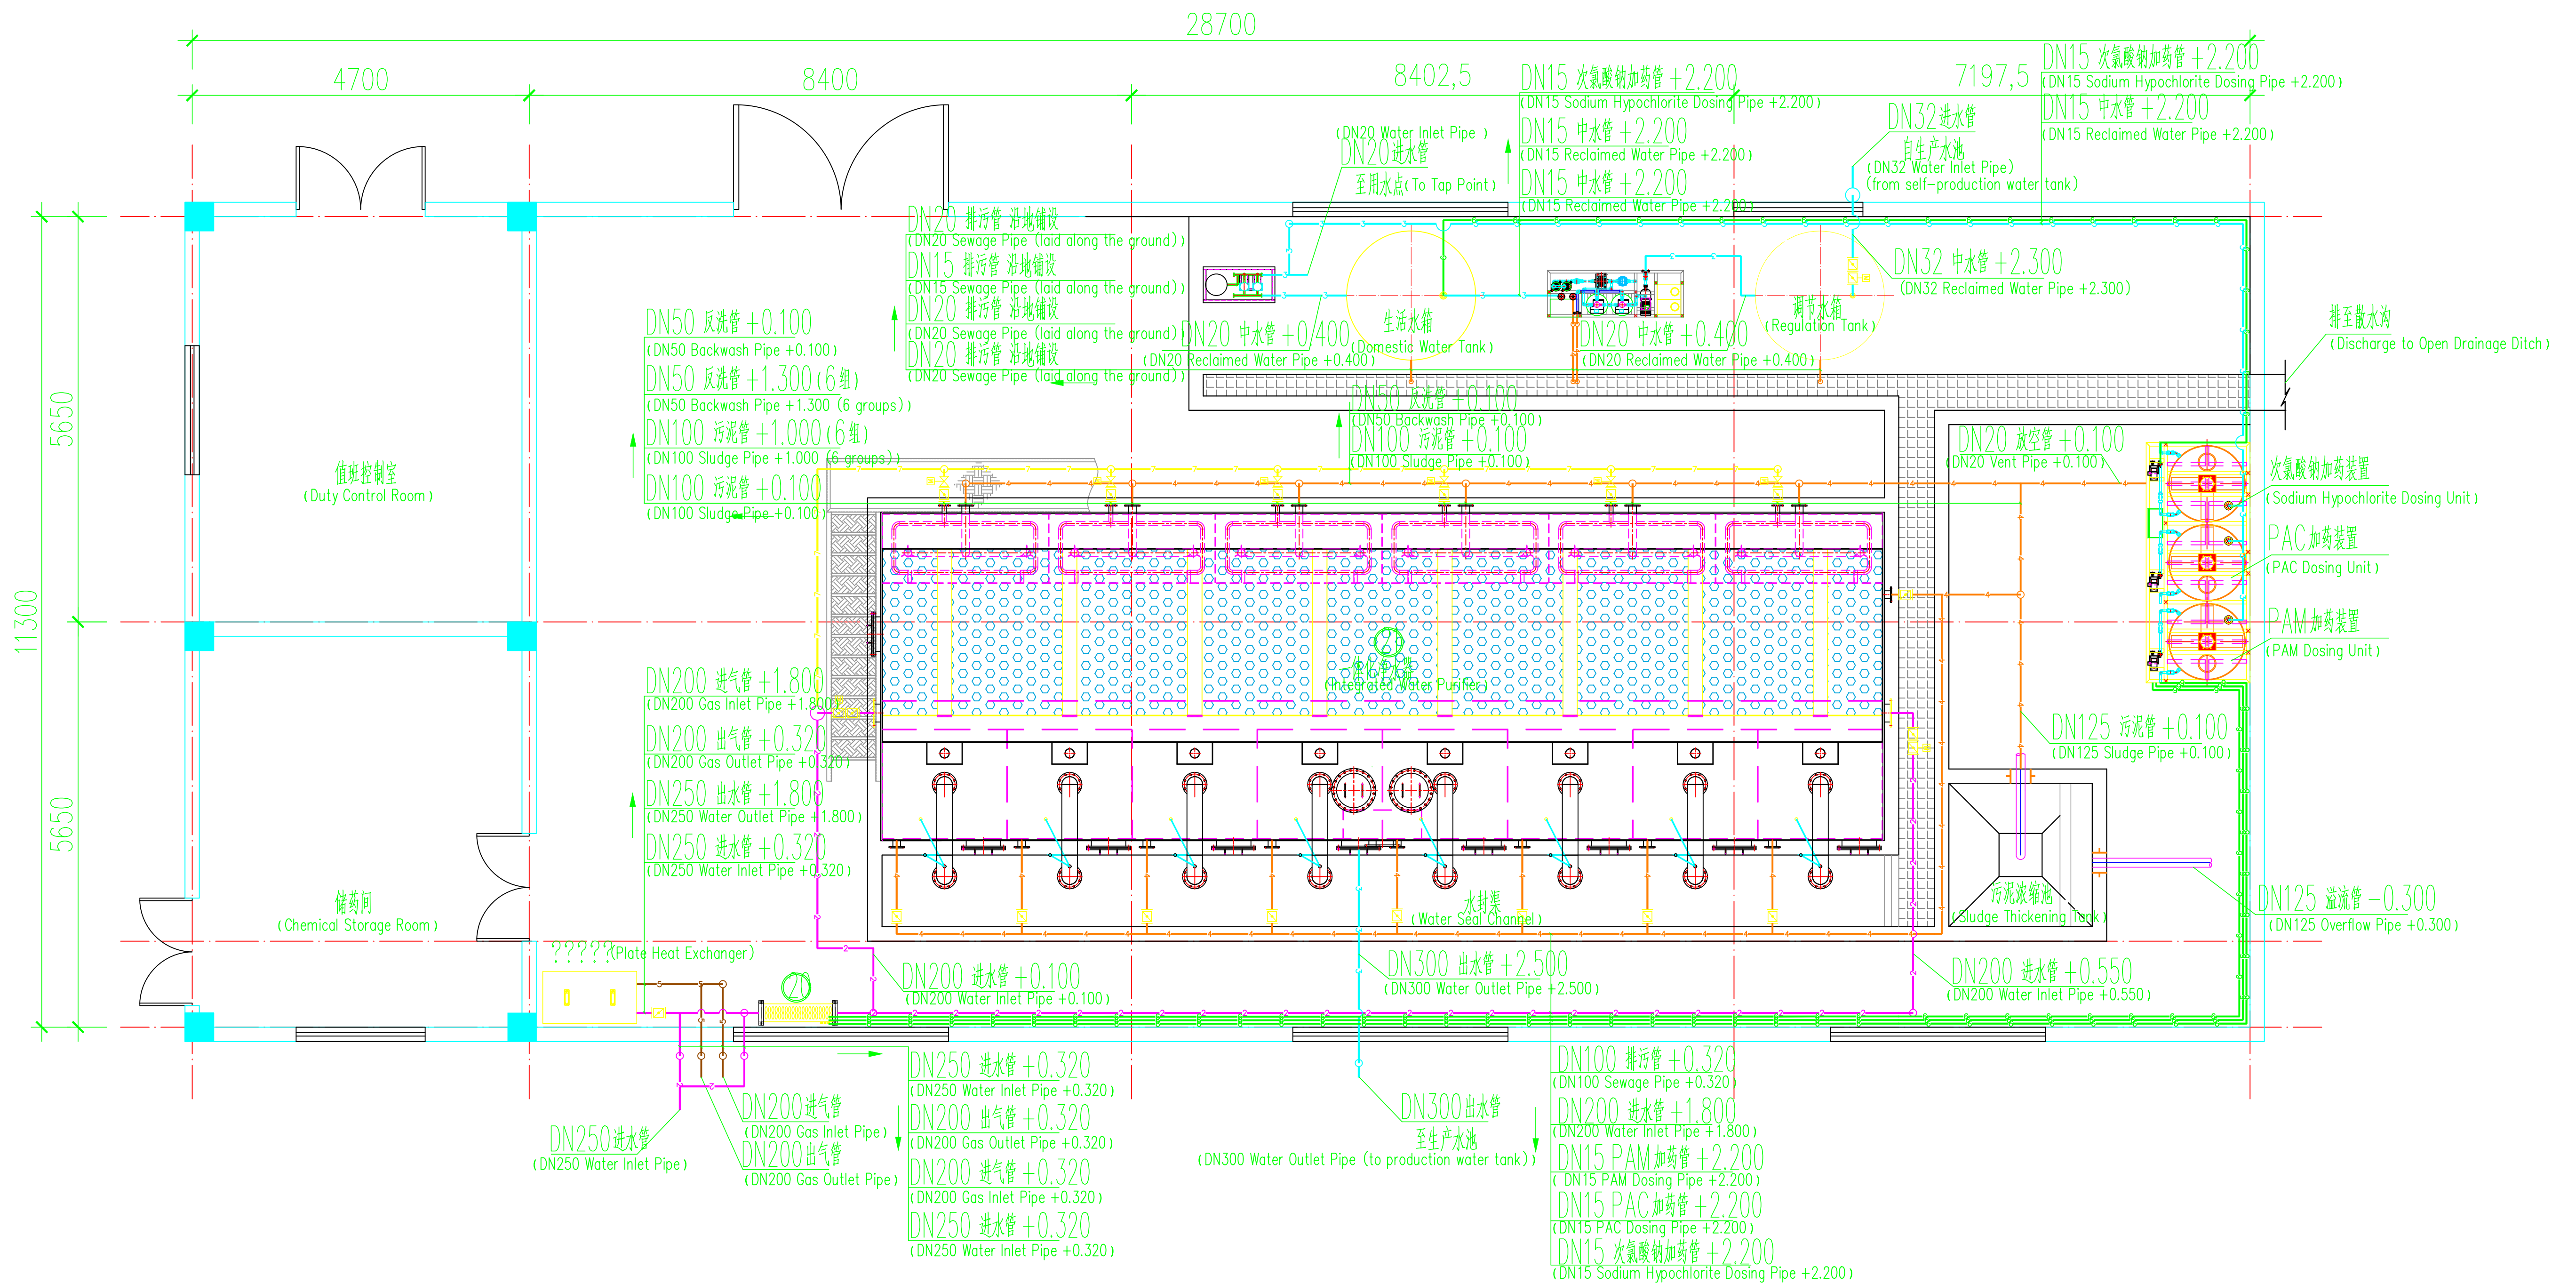


????????????
(Water Purification Station Integrated Pipeline Layout Plan)

四川盛玖源环境工程有限公司 Sichuan shengjiuyuan Environmental Engineering Co., Ltd.				工程名称 PROJECT	乌兹别克斯坦年产50万吨硫磺制酸项目 Uzbekistan 500,000 Tons/Year Sulfur-Based Sulfuric Acid Plant Project		
				子项名称 Sub-item Name	净水站设备项目 Project Water Purification Station Equipment		
审 定 APPROVED	张洪林	工程编号 PROJECT NO.	SJY202602	净水站综合管线平面布置 Water Purification Station Integrated Pipeline Layout Plan			
审 核 EXAMINED	张公征	设计阶段 DESIGNSTAGE	施工图 CONSTRUCTION DRAWING				
校 核 CHECKED	胡欣雨	比 例 Ratio	1:100				
设 计 DESIGNED	刘冲	出图日期 DATE	2026. 02	图纸编号 DRAWING NO.	SJY-GY-05	专 业 Professional	工 艺 Process

???

- 溢流管 (Overflow Pipe)
- 原水管 (Raw Water Pipe)
- 产水管 (Product Water Pipe)
- 污泥管 (Sludge Pipe)
- 蒸汽管 (Steam Pipe)
- 药剂管 (Chemical Pipe)
- 反洗管 (Backwash Pipe)

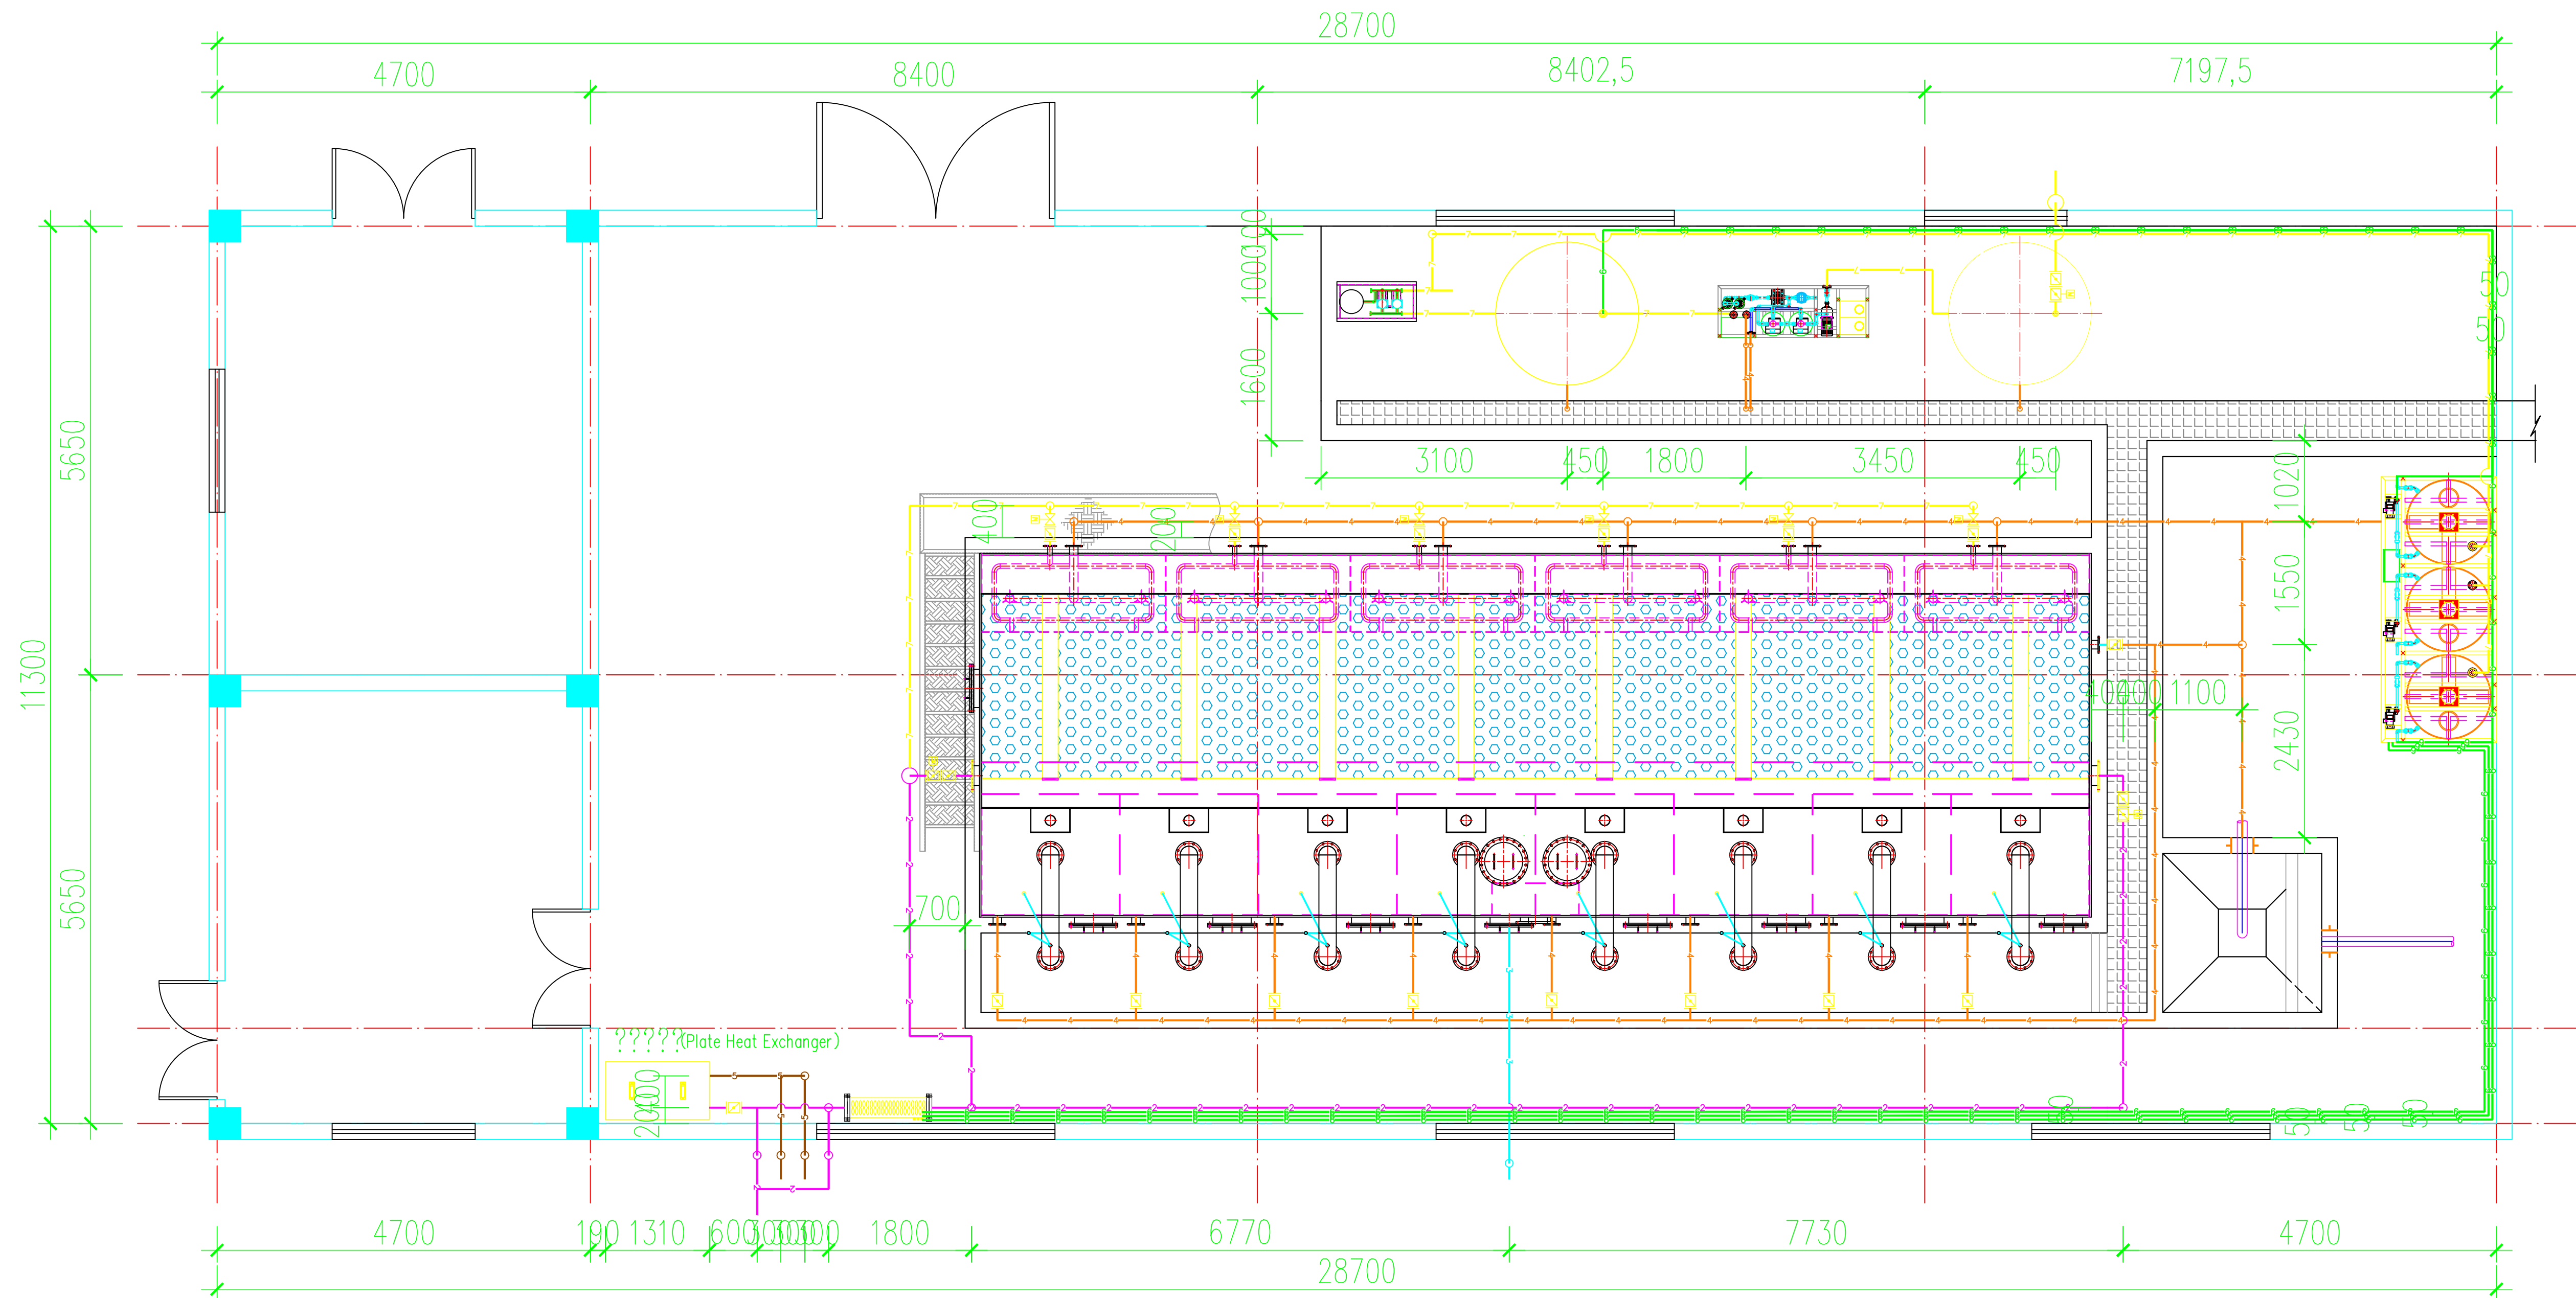


??????????
(Water Purification Station Pipeline Layout Plan)

四川盛玖源环境工程有限公司 Sichuan shengjiuyuan Environmental Engineering Co.,		工程名称 PROJECT	乌兹别克斯坦年产50万吨硫磺制酸项目 Uzbekistan 500,000 Tons/Year Sulfur-Based Sulfuric Acid Plant Project
		子项名称 Sub-item Name	净水站设备项目 Project Water Purification Station Equipment
审 定 APPROVED	廖洪林	工程编号 PROJECT NO.	SJY202602
审 核 EXAMINED	张山松	设计阶段 DESIGNSTAGE	施工图 CONSTRUCTION DRAWING
校 核 CHECKED	胡欣雨	比 例 Ratio	1:100
净水站管线定位平面布置 Water Purification Station Pipeline Layout Plan			


其他设备清单 Other Equipment List						
序号No.	名称 Name	规格型号 Model & Spec	单位 Unit	数量 Qty.	材质 Material	备注 Remarks
19	板式换热器 Plate Heat Exchanger	处理能力200m3/h Capacity: 200m3/h	套 /set	1	板片304 Plate material	
20	管式混合器 Pipeline Mixer	DN250 , PN1.0MPa	套 /set	1	PVC	
21	一体化净水器 Integrated Water Purifier	处理能力200m3/h , 含系统配件 Capacity: 200m3/h, with system accessories	台 /unit	1		
22	在线浊度仪 Online Turbidity Meter	0--50 NTU	台 /unit	2		
23	温度计 Thermometer	0-100℃	台 /unit	1	不锈钢 Stainless Steel	
24	调节水箱 Regulating Water Tank	非标, 不锈钢成品水箱, 容积: 5m3 Custom-made finished SS water tank, Volume: 5m3	套 /set	1		
25	液位计 Level Gauge	MD-UK221/0-5m	套 /set	1	不锈钢 Stainless Steel	
26	生活水箱 Domestic Water Tank	非标, 不锈钢成品水箱, 容积: 5m3 Custom-made finished SS water tank, Volume: 5m3	套 /set	1		
27	液位计 Level Gauge	MD-UK221/0-5m	套 /set	1		
28	恒压供水Constant Pressure Water Supply	5.0m3/d , 变频控制, N=0.55*2kW VFD control	套 /set	1		
29	流量计 Flow Meter	5.0m3/d	台 /unit	1		
30	余氯监测仪 Residual Chlorine Monitor	0--5mg/L	台 /unit	1		
31	压力传感器 Pressure Sensor	0--1.0MPa	套 /set	1		

主要管配件 (Main Pipe Fittings)							
管道类别Pipeline Category	序号 No.	名 称Name	规 格 性 能Spec	单位 Unit	数量 Qty.	材质 Material	备注 Remarks
一体化净水器进水 Integrated Water Purifier Inlet	1	手动蝶阀/Manual Butterfly Valve	DN250 PN1.0MPa	只 /piece	3	UPVC	
	2	手动蝶阀/Manual Butterfly Valve	DN200 PN1.0MPa	只 /piece	2	UPVC	
	3	电动蝶阀/Electric Butterfly Valve	DN200 PN1.0MPa	只 /piece	2	UPVC	
	4	管道 / Pipe	DN250	米 /meter	8	UPVC	
	5	管道 / Pipe	DN200	米 /meter	28	UPVC	其中8米不锈钢, 蒸汽用 8 meters stainless steel for steam service
	6	大小头 / Reducer	DN250×DN200	只 /piece	1	UPVC	
	7	正三通 / Equal Tee	DN250×DN250	只 /piece	1	UPVC	
	8	异径三通 / Reducing Tee	DN250×DN200	只 /piece	1	UPVC	
	9	正三通 / Equal Tee	DN200×DN200	只 /piece	1	UPVC	
	10	90° 弯管 / 90° Elbow	DN250	只 /piece	4	UPVC	
	11	90° 弯管 / 90° Elbow	DN200	只 /piece	7	UPVC	其中3个不锈钢, 蒸汽用 3 pcs are stainless steel for steam service
一体化净水器反洗 Integrated Water Purifier Backwash	12	手动蝶阀Manual Butterfly Valve	DN50 PN1.0MPa	只 /piece	6	UPVC	
	13	电磁阀 / Solenoid Valve	DN50 PN1.0MPa	只 /piece	6	UPVC	
	14	管道 / Pipe	DN50	米 /meter	30	UPVC	
	15	大小头 / Reducer	DN200×DN50	只 /piece	1	UPVC	
	16	正三通 / Equal Tee	DN50×DN50	只 /piece	5	UPVC	
	17	90° 弯管 / 90° Elbow	DN50	只 /piece	8	UPVC	
一体化净水器产水 Integrated Water Purifier Outlet Water	18	管道 / Pipe	DN300	米 /meter	6	UPVC	
	19	90° 弯管 / 90° Elbow	DN50	只 /piece	2	UPVC	
一体化净水器排污 Integrated Water Purifier Wastewater Discharge	20	手动蝶阀Manual Butterfly Valve	DN100 PN1.0MPa	只 /piece	13	UPVC	
	21	电动蝶阀/Electric Butterfly Valve	DN100 PN1.0MPa	只 /piece	6	UPVC	
	22	管道 / Pipe	DN125	米 /meter	5	UPVC	
	23	管道 / Pipe	DN100	米 /meter	58	UPVC	
	24	大小头 / Reducer	DN125×DN100	只 /piece	1	UPVC	
	25	大小头 / Reducer	DN100×DN20	只 /piece	1	UPVC	
	26	异径三通 / Reducing Tee	DN125×DN100	只 /piece	1	UPVC	
	27	正三通 / Equal Tee	DN100×DN100	只 /piece	12	UPVC	
	28	90° 弯管 / 90° Elbow	DN125	只 /piece	1	UPVC	
	29	90° 弯管 / 90° Elbow	DN100	只 /piece	10	UPVC	
加药 Chemical Dosing	30	球阀 / Ball Valve	DN15	只 /piece	1	UPVC	
	31	球阀 / Ball Valve	DN15	只 /piece	1	UPVC	
	32	管道 / Pipe	DN15	米 /meter	85	UPVC	配直接, 弯头配件 With couplings & elbows
	33	管道 / Pipe	DN15	米 /meter	25	UPVC	配直接, 弯头配件 With couplings & elbows
生活水系统 Domestic Water System	34	手动球阀/Manual Ball Valve	DN32 PN1.0MPa	只 /piece	13	UPVC	
	35	电动球阀 / Electric Ball Valve	DN32 PN1.0MPa	只 /piece	6	UPVC	
	36	管道 / Pipe	DN32	米 /meter	4	UPVC	
	37	管道 / Pipe	DN20	米 /meter	12	UPVC	配直接, 弯头配件 With couplings & elbows
	38	管道 / Pipe	DN15	米 /meter	25	UPVC	配直接, 弯头配件 With couplings & elbows
	39	球阀 / Ball Valve	DN15	只 /piece	5	UPVC	

四川盛玖源环境工程有限公司 Sichuan shengjiuyuan Environmental Engineering Co.,				工程名称 PROJECT	乌兹别克斯坦年产50万吨硫磺制酸项目 Uzbekistan 500,000 Tons/Year Sulfur-Based Sulfuric Acid Plant Project				
				子项名称 Sub-Item Name	净水站设备项目 Project Water Purification Station Equipment				
审 定 APPROVED	张洪林	工程编号 PROJECT NO.	SJY202602		设备、材料一览表 Equipment & Material List				
审 核 EXAMINED	张洪林	设计阶段 DESIGNSTAGE	施工图 CONSTRUCTION DRAWING						
校 核 CHECKED	胡欣雨	比 例 Ratio	1:100						
设 计 DESIGNED	刘 冲	出图日期 DATE	2026. 02		图纸编号 DRAWING NO.	SJY-GY-07		专 业 Professional	工 艺 Process

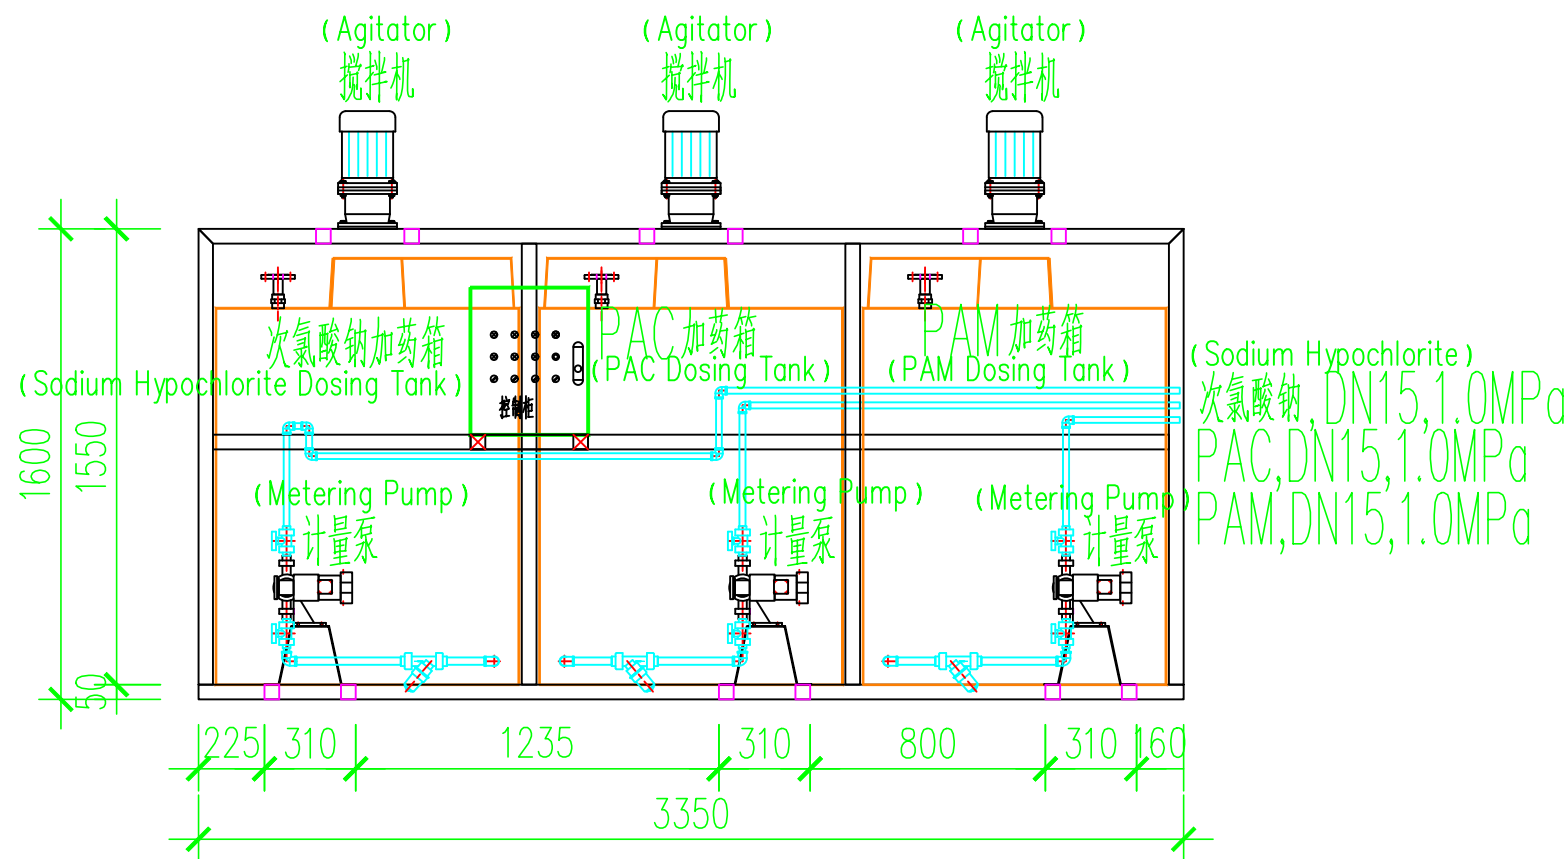

正视图
(Front View)

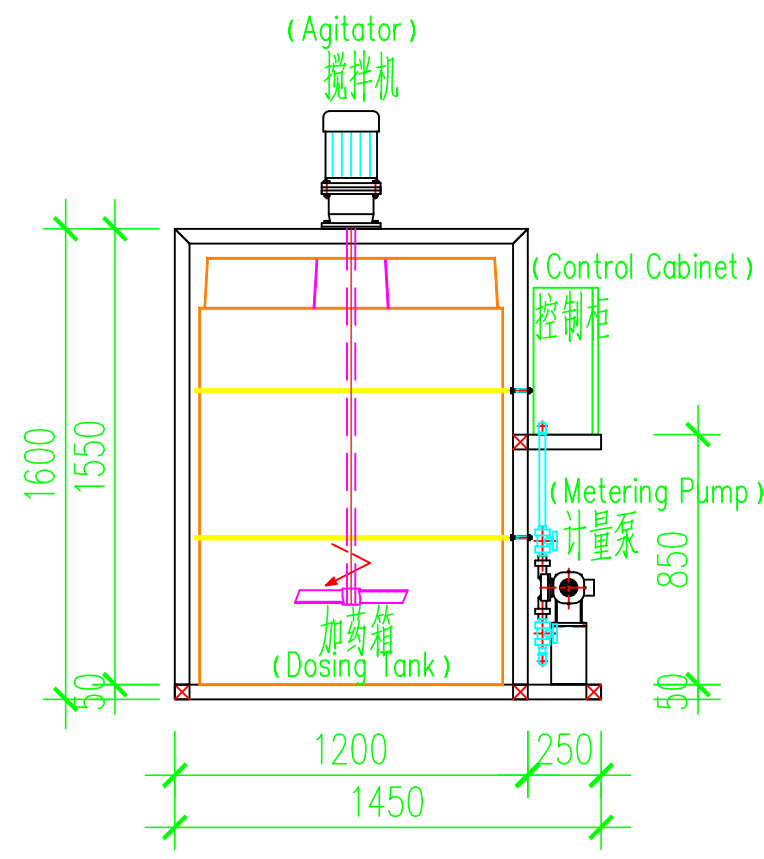


左视图
(Left View)

说明:

- 1、本设计尺寸单位: 标高以米计, 其余以毫米计。
- 2、加药设备集成于一个机架上, 配套集成管阀件和就地控制箱。

Notes:


- 1.Units of measurement in this design: Elevations are in meters, all other dimensions are in millimeters.
- 2.The chemical dosing equipment is integrated on one frame, with integrated pipe fittings and local control cabinet.

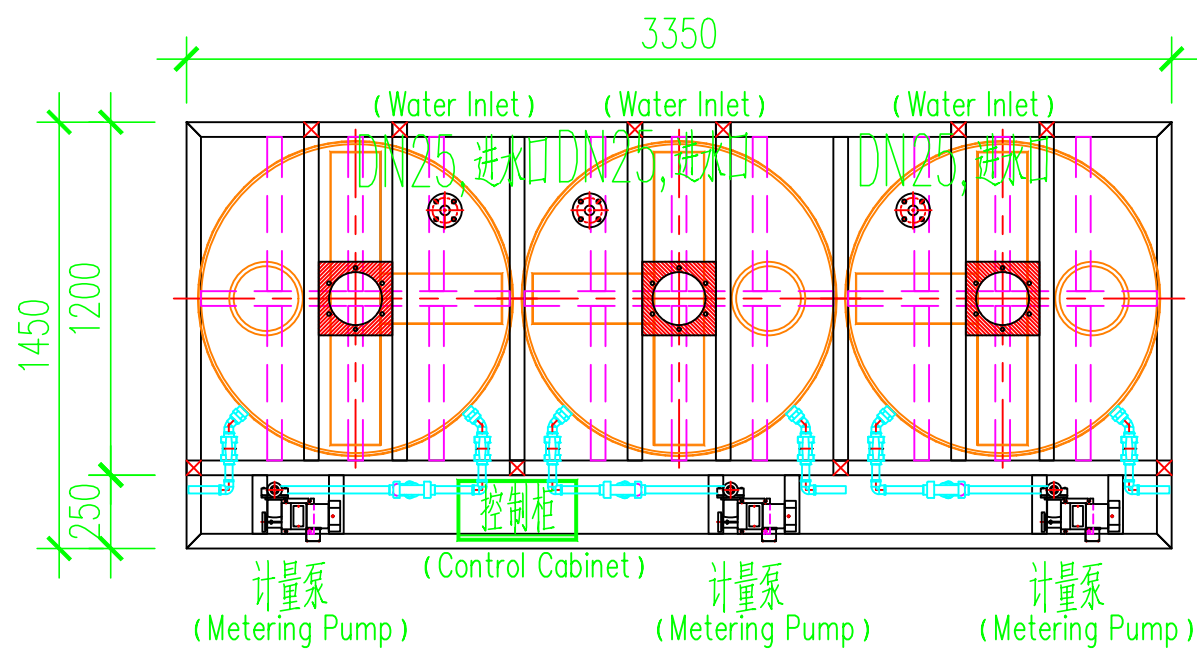

俯视图
(Top View)

加药装置设备清单 Chemical Dosing Unit List						
序号No.	名称 Name	规格型号 Model & Spec	单位 Unit	数量 Qty.	材质 Material	备注 Remarks
1	PAC加药箱 PAC Dosing Tank	1000L/ $\varnothing$ 1180×1300	台 /unit	1	PE	
2	液位计 Level Gauge	MD-UK221/0-5m	套 /set	1	工程塑料 Engineering Plastic	24V
3	计量泵 Metering Pump	Q=60L/h, 压力P=1.0MPa Q=60L/h, Pressure P=1.0MPa	台 /unit	1	PVC泵头 PVC Pump Head	380V,50Hz
4	搅拌电机 Agitator Motor	0.55KW, 70-100r/min	台 /unit	1	304叶轮 304 Impeller	380V,50Hz
5	PAM加药箱 PAM Dosing Tank	1000L/ $\varnothing$ 1180×1300	台 /unit	1	PE	
6	液位计 Level Gauge	MD-UK221/0-5m	套 /set	1	工程塑料 Engineering Plastic	24V
7	计量泵 Metering Pump	Q=60L/h, 压力P=1.0MPa Q=60L/h, Pressure P=1.0MPa	台 /unit	1	PVC泵头 PVC Pump Head	380V,50Hz
8	搅拌电机 Agitator Motor	0.55KW, 70-100r/min	台 /unit	1	304叶轮 304 Impeller	380V,50Hz
9	次氯酸钠加药箱 Sodium Hypochlorite Dosing Tank	1000L/ $\varnothing$ 1180×1300	台 /unit	1	PE	
10	液位计 Level Gauge	MD-UK221/0-5m	套 /set	1	工程塑料 Engineering Plastic	24V
11	计量泵 Metering Pump	Q=15L/h, 压力P=1.0MPa Q=60L/h, Pressure P=1.0MPa	台 /unit	1	PVC泵头 PVC Pump Head	380V,50Hz
12	搅拌电机 Agitator Motor	0.55KW, 70-100r/min	台 /unit	1	304叶轮 304 Impeller	380V,50Hz

四川盛玖源环境工程有限公司 Sichuan shengjiuyuan Environmental Engineering Co.,				工程名称 PROJECT	乌兹别克斯坦年产50万吨硫磺制酸项目 Uzbekistan 500,000 Tons/Year Sulfur-Based Sulfuric Acid Plant Project				
				子项名称 Sub-Item Name	净水站设备项目 Project Water Purification Station Equipment				
审 定 APPROVED	李洪林	工程编号 PROJECT NO.	SJY202602		加药设备外形尺寸图 External Dimension Drawing of Chemical Dosing Unit				
审 核 EXAMINED	张公程	设计阶段 DESIGNSTAGE	施工图 CONSTRUCTION DRAWING						
校 核 CHECKED	桐欣雨	比 例 Ratio	1:100						
设 计 DESIGNED	刘 冲	出图日期 DATE	2026. 02		图纸编号 DRAWING NO.	SJY-GY-09		专 业 Professional	工 艺 Process

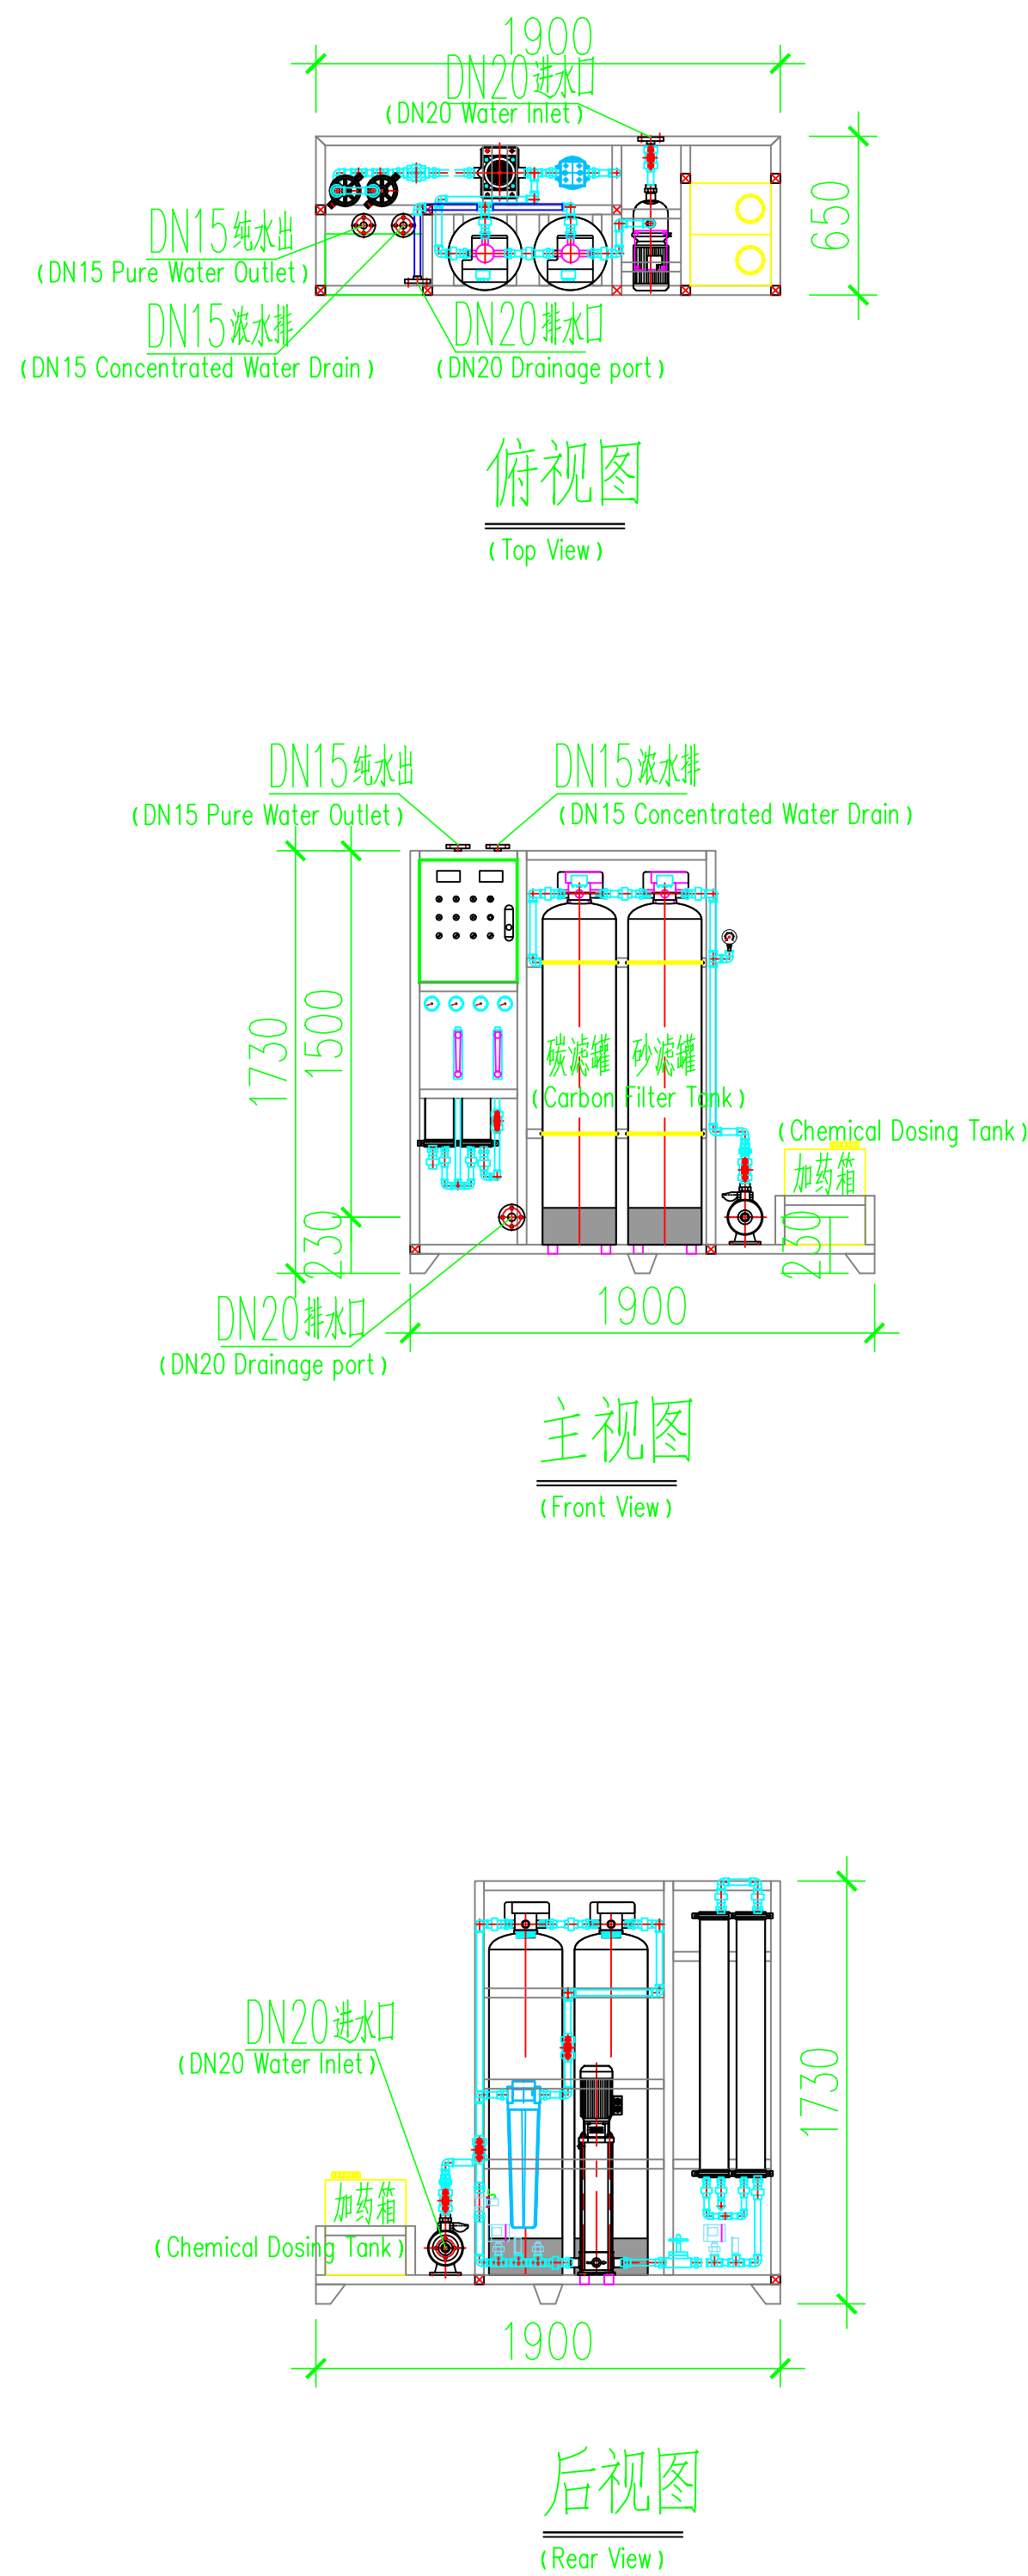

说明:

1、本设计尺寸单位: 标高以米计, 其余以毫米计。


2、生活水净水设备集成于一个机架上, 配套集成管阀件和就地控制箱。

Notes:


1.Units of measurement in this design: Elevations are in meters, all other dimensions are in millimeters.

2.The domestic water purification equipment is integrated on one frame, with integrated pipe fittings and local control cabinet.

生活水净水设备清单 Domestic Water Purification Equipment List						
序号No.	名称 Name	规格型号 Model & Spec	单位 Unit	数量 Qty.	材质 Material	备注 Remarks
13	增压泵1 Booster Pump 1	生活水净水设备配套, 提升能力≥5m3/d, N=0.55kW For domestic water purification system, lifting capacity ≥5m3/d, N=0.55kW	台 /unit	1		380V,50Hz
14	多介质过滤器 Multi-media Filter	处理能力: Q≥5m3/d Capacity: Q≥5m3/d	套 /set	1		
15	活性炭过滤器 Activated Carbon Filter	处理能力: Q≥5m3/d Capacity: Q≥5m3/d	套 /set	1		
16	增压泵2 Booster Pump 2	生活水净水设备配套, 提升能力≥5m3/d, N=1.1kW For domestic water purification system, lifting capacity ≥5m3/d, N=1.1kW	台 /unit	1		380V,50Hz
17	RO机组 RO Unit	处理能力: Q≥5m3/d, 配套膜/仪表、连接管道 / Pipe/管件/阀门等 /fittings/valves, etc.	台 /unit	1		
18	清洗系统 Cleaning System	生活水净水设备配套, 加药泵N=12W For domestic water purification system, dosing pump N=12W	套 /set	2		380V,50Hz

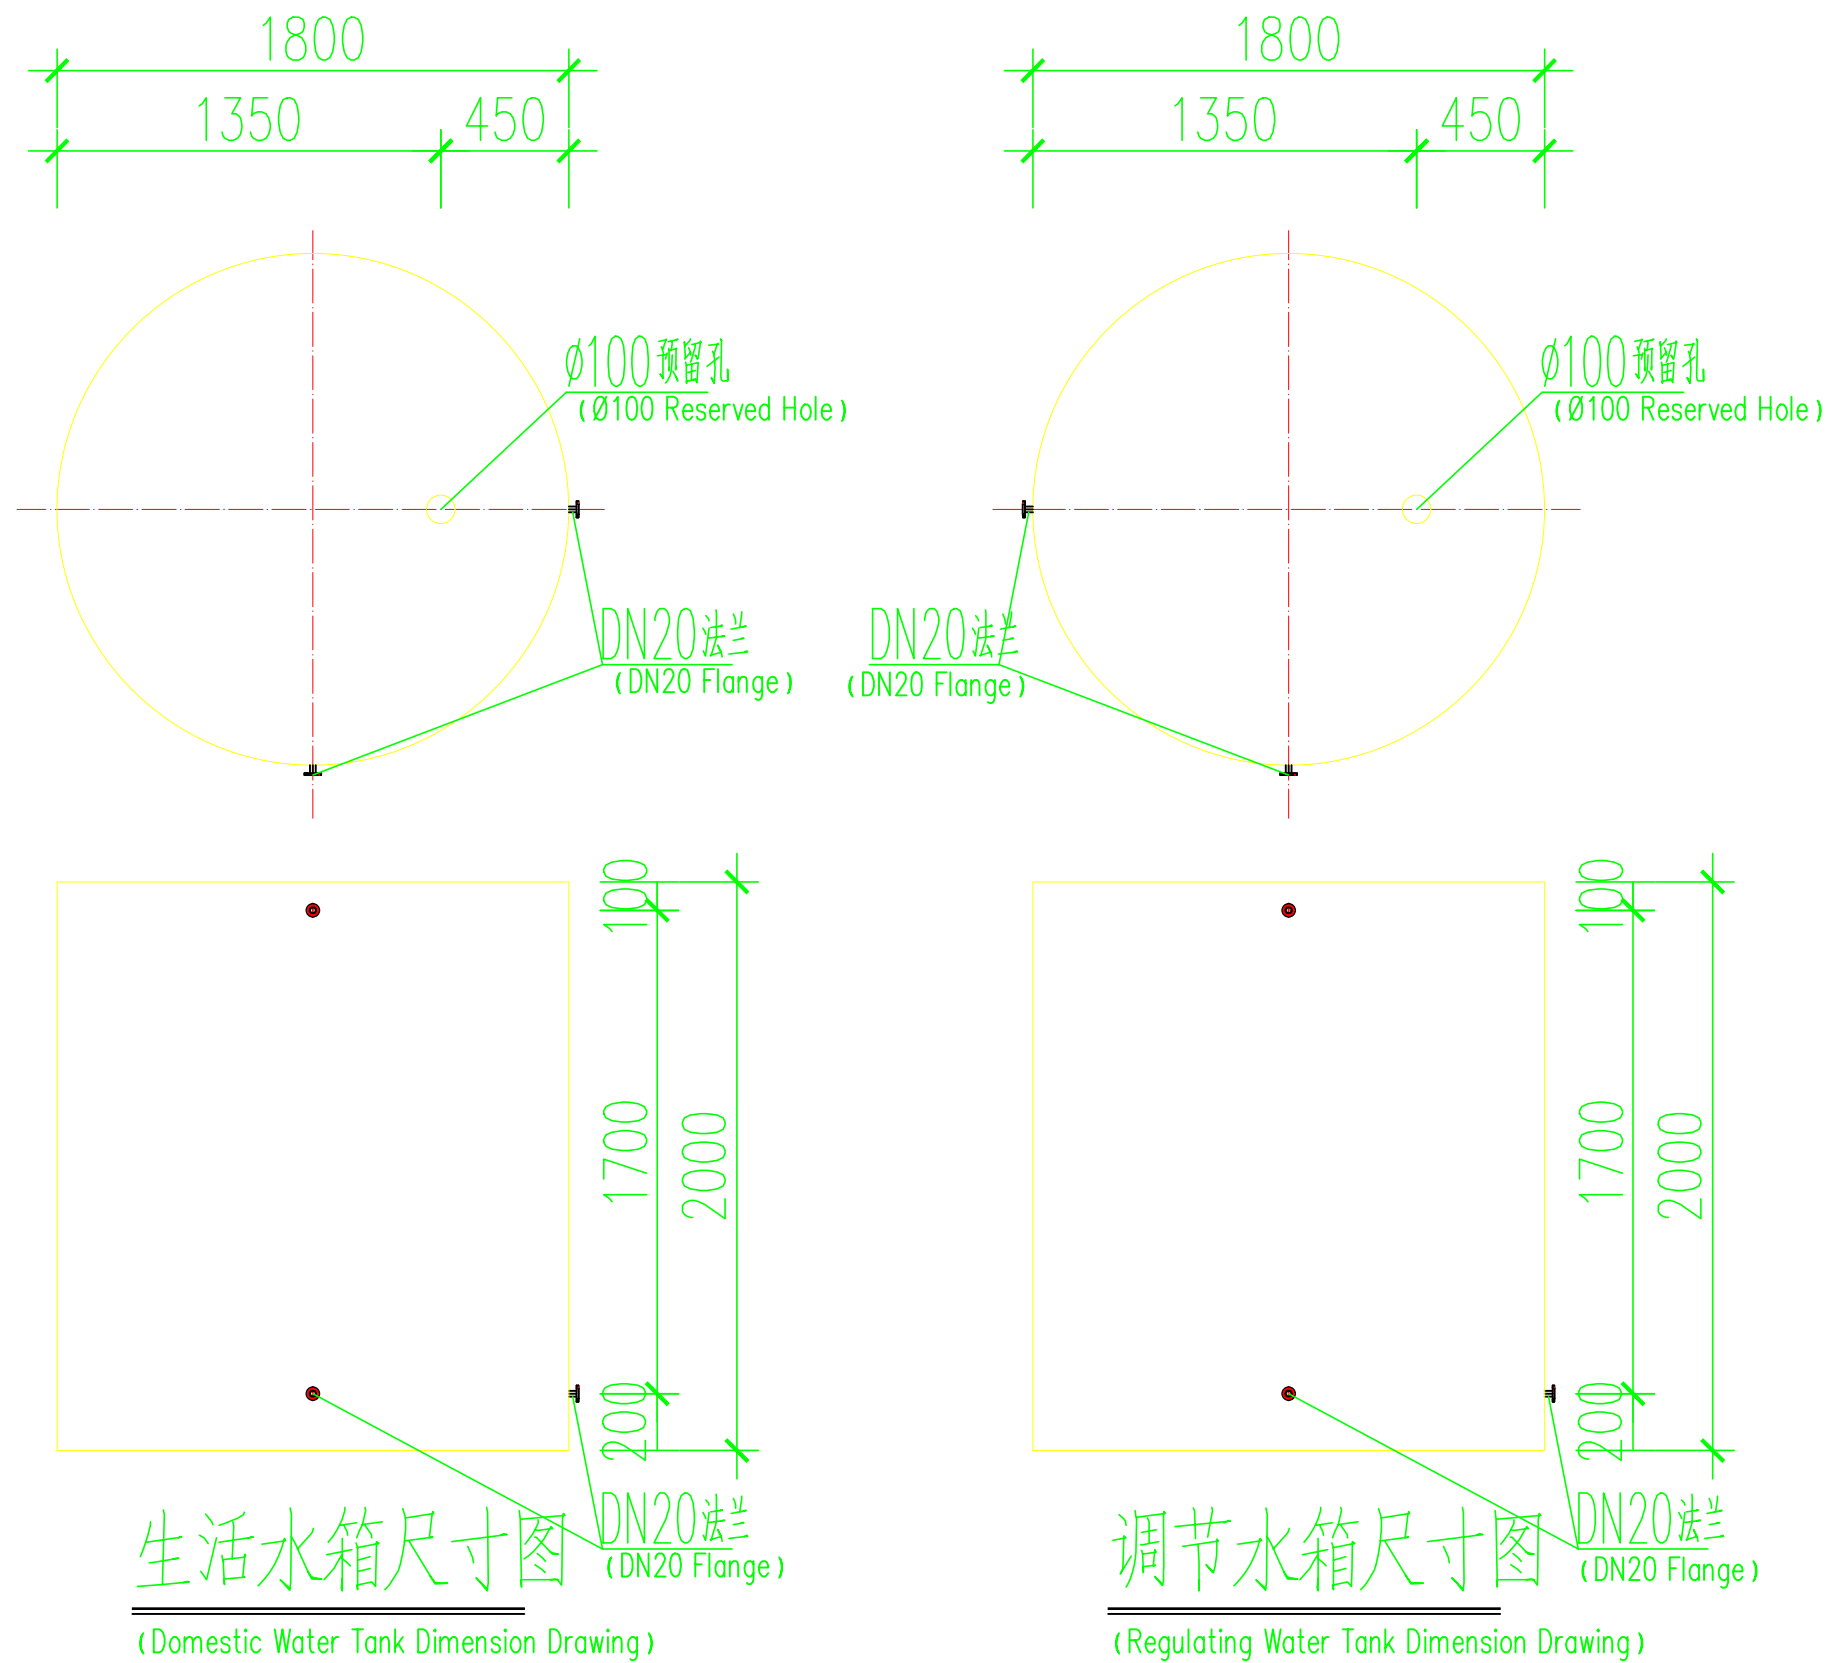


四川盛玖源环境工程有限公司 Sichuan shengjiuyuan Environmental Engineering Co., Ltd.				工程名称 PROJECT		乌兹别克斯坦年产50万吨硫磺制酸项目 Uzbekistan 500,000 Tons/Year Sulfur-Based Sulfuric Acid Plant Project	
				子项名称 Sub-item Name		净水站设备项目 Project Water Purification Station Equipment	
审 定 APPROVED		唐洪林		工程编号 PROJECT NO.		SJY202602	
审 核 EXAMINED		任公权		设计阶段 DESIGNSTAGE		施工图 CONSTRUCTION DRAWING	
校 核 CHECKED		胡欣雨		比 例 Ratio		1:100	
设 计 DESIGNED		刘冲		出图日期 DATE		2026. 02	
				图纸编号 DRAWING NO.		SJY-GY-10	
						专 业 Professional	
						工 艺 Process	

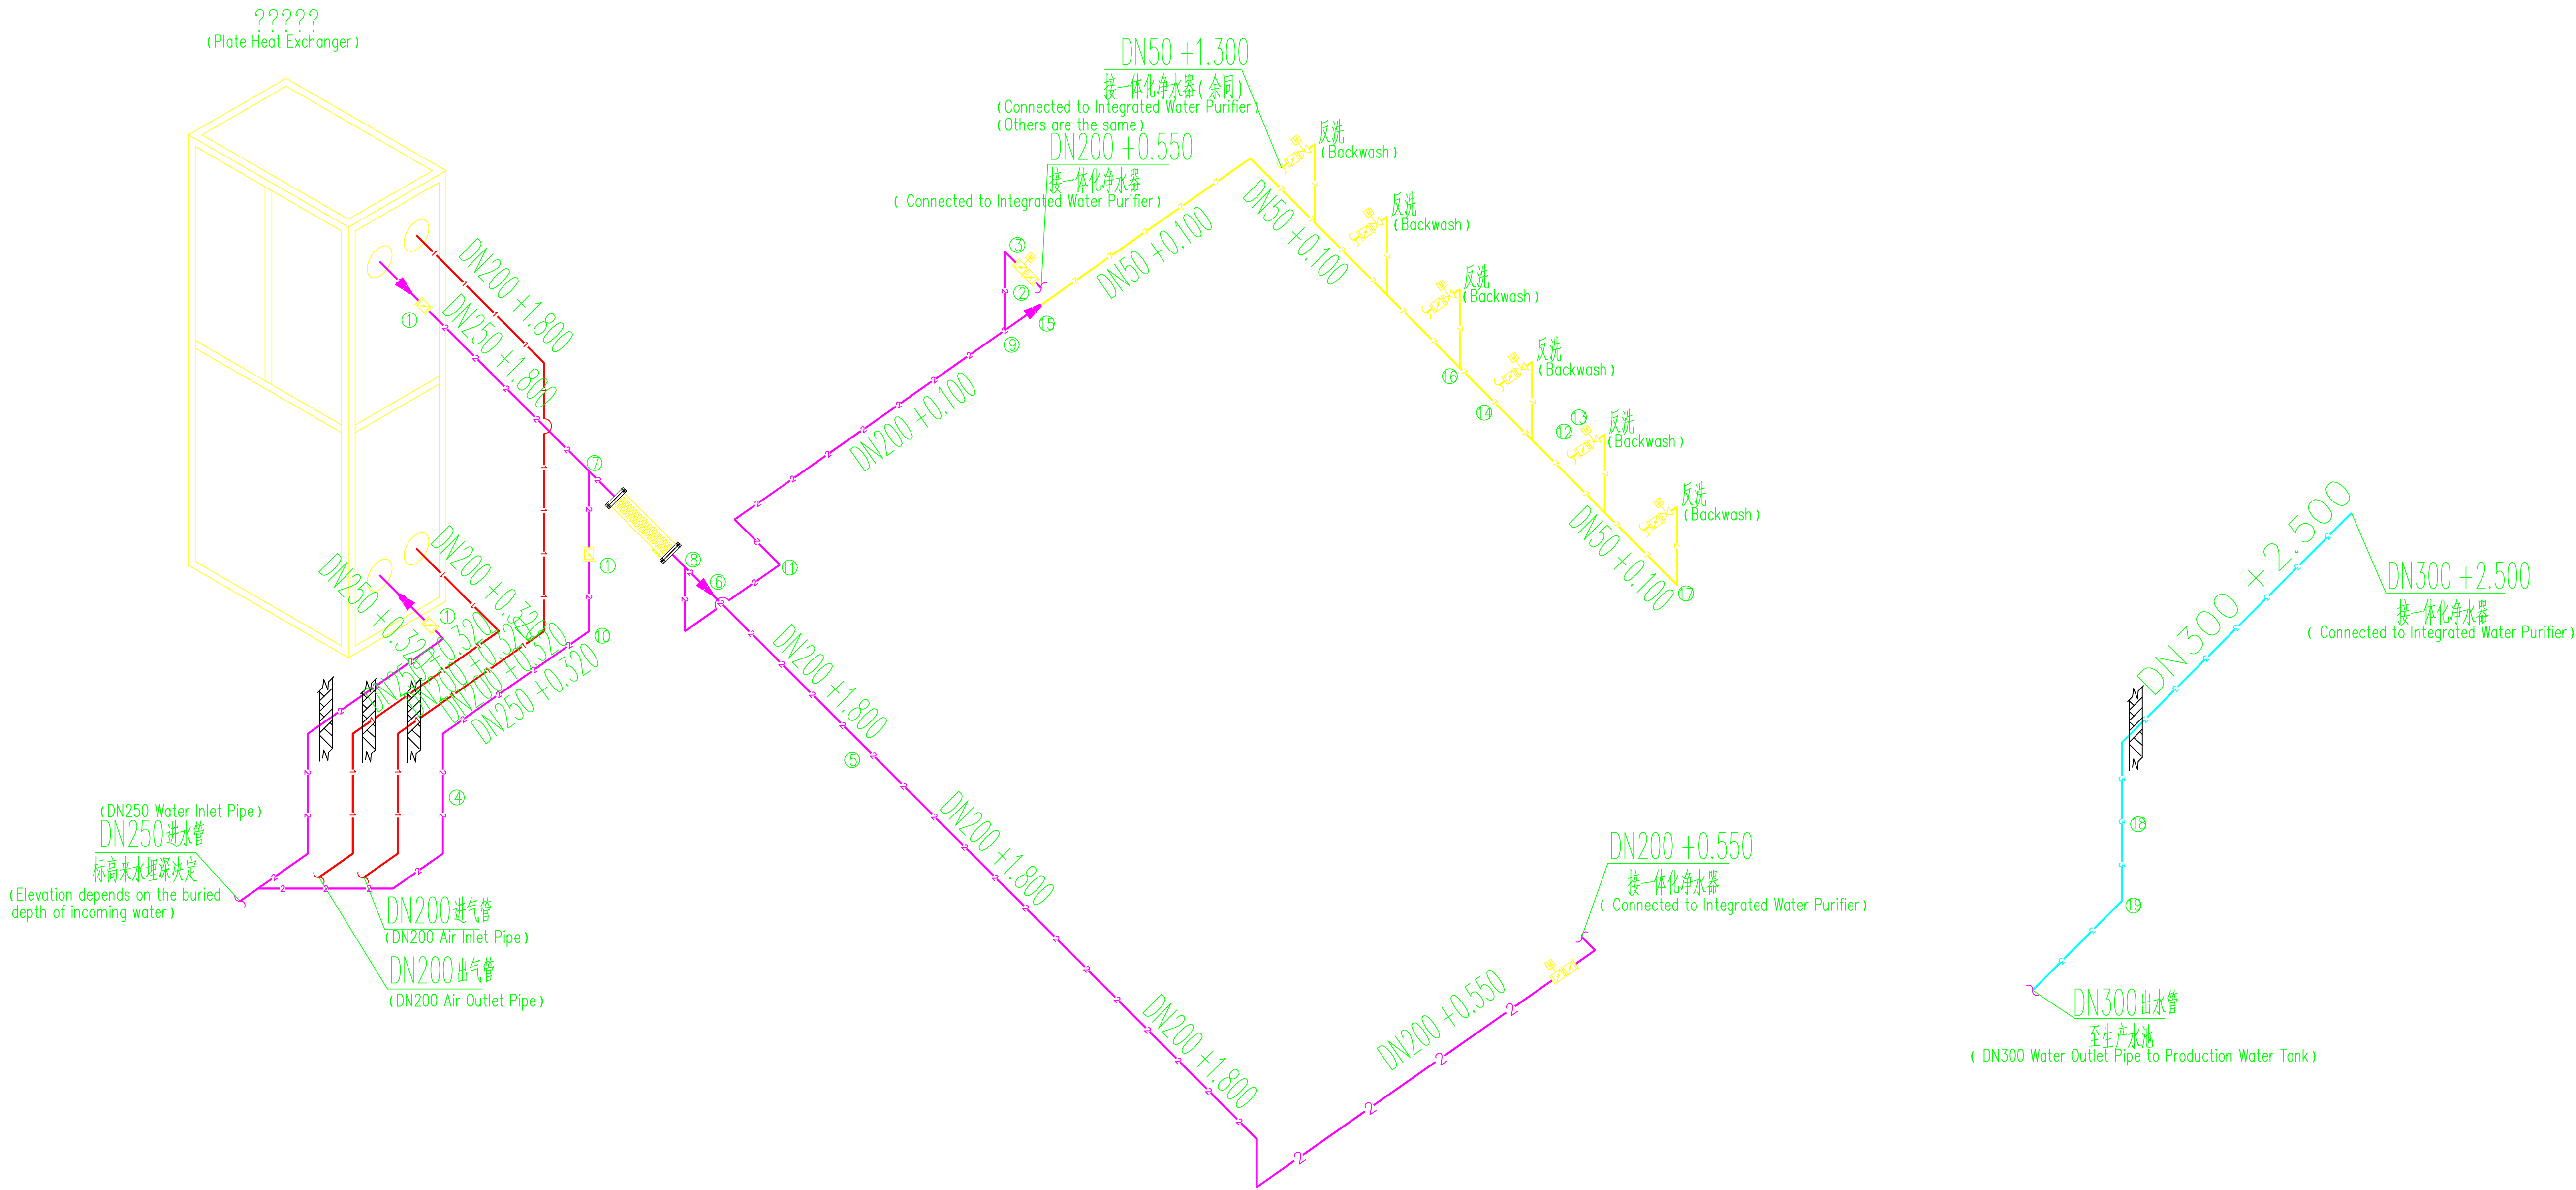

进水、进气、反洗系统图
(Water Inlet, Air Inlet and Backwash System Diagram)

出水系统图
(Water Outlet System Diagram)

四川盛玖源环境工程有限公司 Sichuan shengjiuyuan Environmental Engineering Co.,				工程名称 PROJECT		乌兹别克斯坦年产50万吨硫磺制酸项目 Uzbekistan 500,000 Tons/Year Sulfur-Based Sulfuric Acid Plant Project	
				子项名称 Sub-item Name		净水站设备项目 Project Water Purification Station Equipment	
审 定 APPROVED	张洪林	工程编号 PROJECT NO.	SJY202602	系统图1 System Diagram 1			
审 核 EXAMINED	张洪林	设计阶段 DESIGNSTAGE	施工图 CONSTRUCTION DRAWING				
校 核 CHECKED	胡欣雨	比 例 Ratio	1:100				
设 计 DESIGNED	胡欣雨	出图日期 DATE	2026. 02	图纸编号 DRAWING NO.	SJY-GY-11	专 业 Professional	工 艺 Process

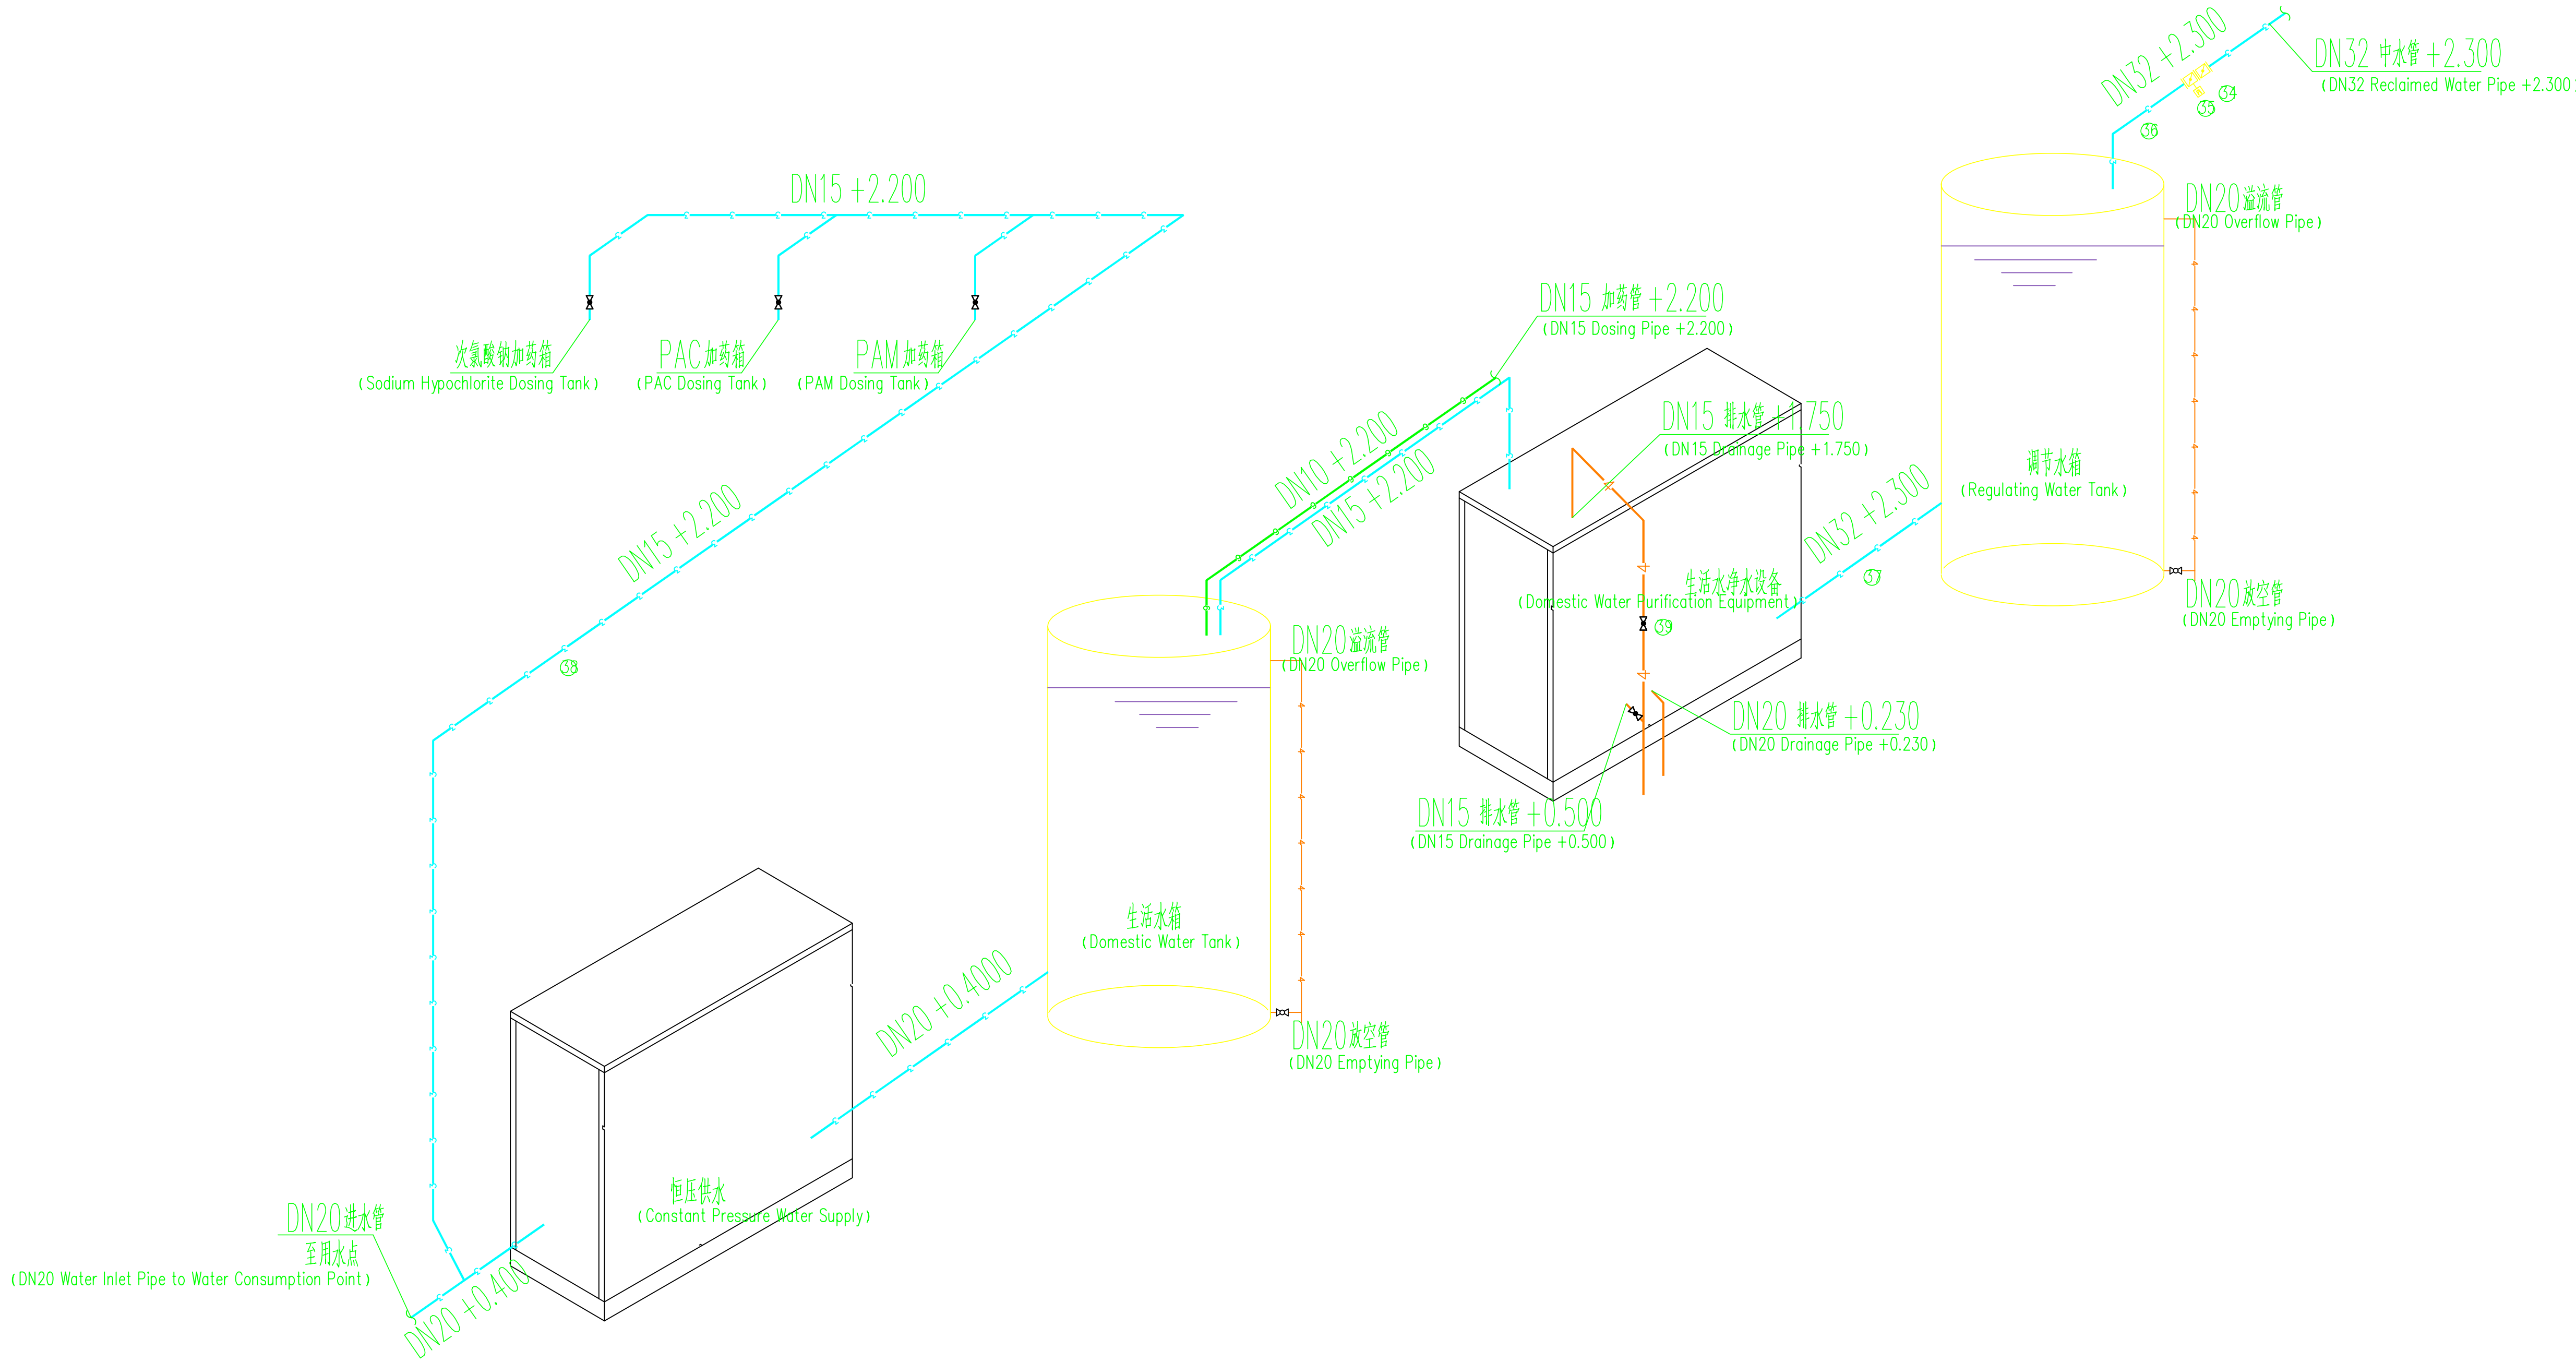


生活水系统图
(Domestic Water System Diagram)

四川盛玖源环境工程有限公司 Sichuan shengjiuyuan Environmental Engineering Co.,				工程名称 PROJECT	乌兹别克斯坦年产50万吨硫磺制酸项目 Uzbekistan 500,000 Tons/Year Sulfur-Based Sulfuric Acid Plant Project		
				子项名称 Sub-item Name	净水站设备项目 Project Water Purification Station Equipment		
审 定 APPROVED	张洪林	工程编号 PROJECT NO.	SJY202602		系统图3 System Diagram 3		
审 核 EXAMINED	张公征	设计阶段 DESIGNSTAGE	施工图 CONSTRUCTION DRAWING				
校 核 CHECKED	胡欣雨	比 例 Ratio	1:100				
设 计 DESIGNED	刘冲	出图日期 DATE	2026. 02				
				图 纸 编 号 DRAWING NO.			

???

- 溢流管 (Overflow Pipe)
- 原水管 (Raw Water Pipe)
- 产水管 (Product Water Pipe)
- 污泥管 (Sludge Pipe)
- 蒸汽管 (Steam Pipe)
- 药剂管 (Chemical Pipe)
- 反洗管 (Backwash Pipe)

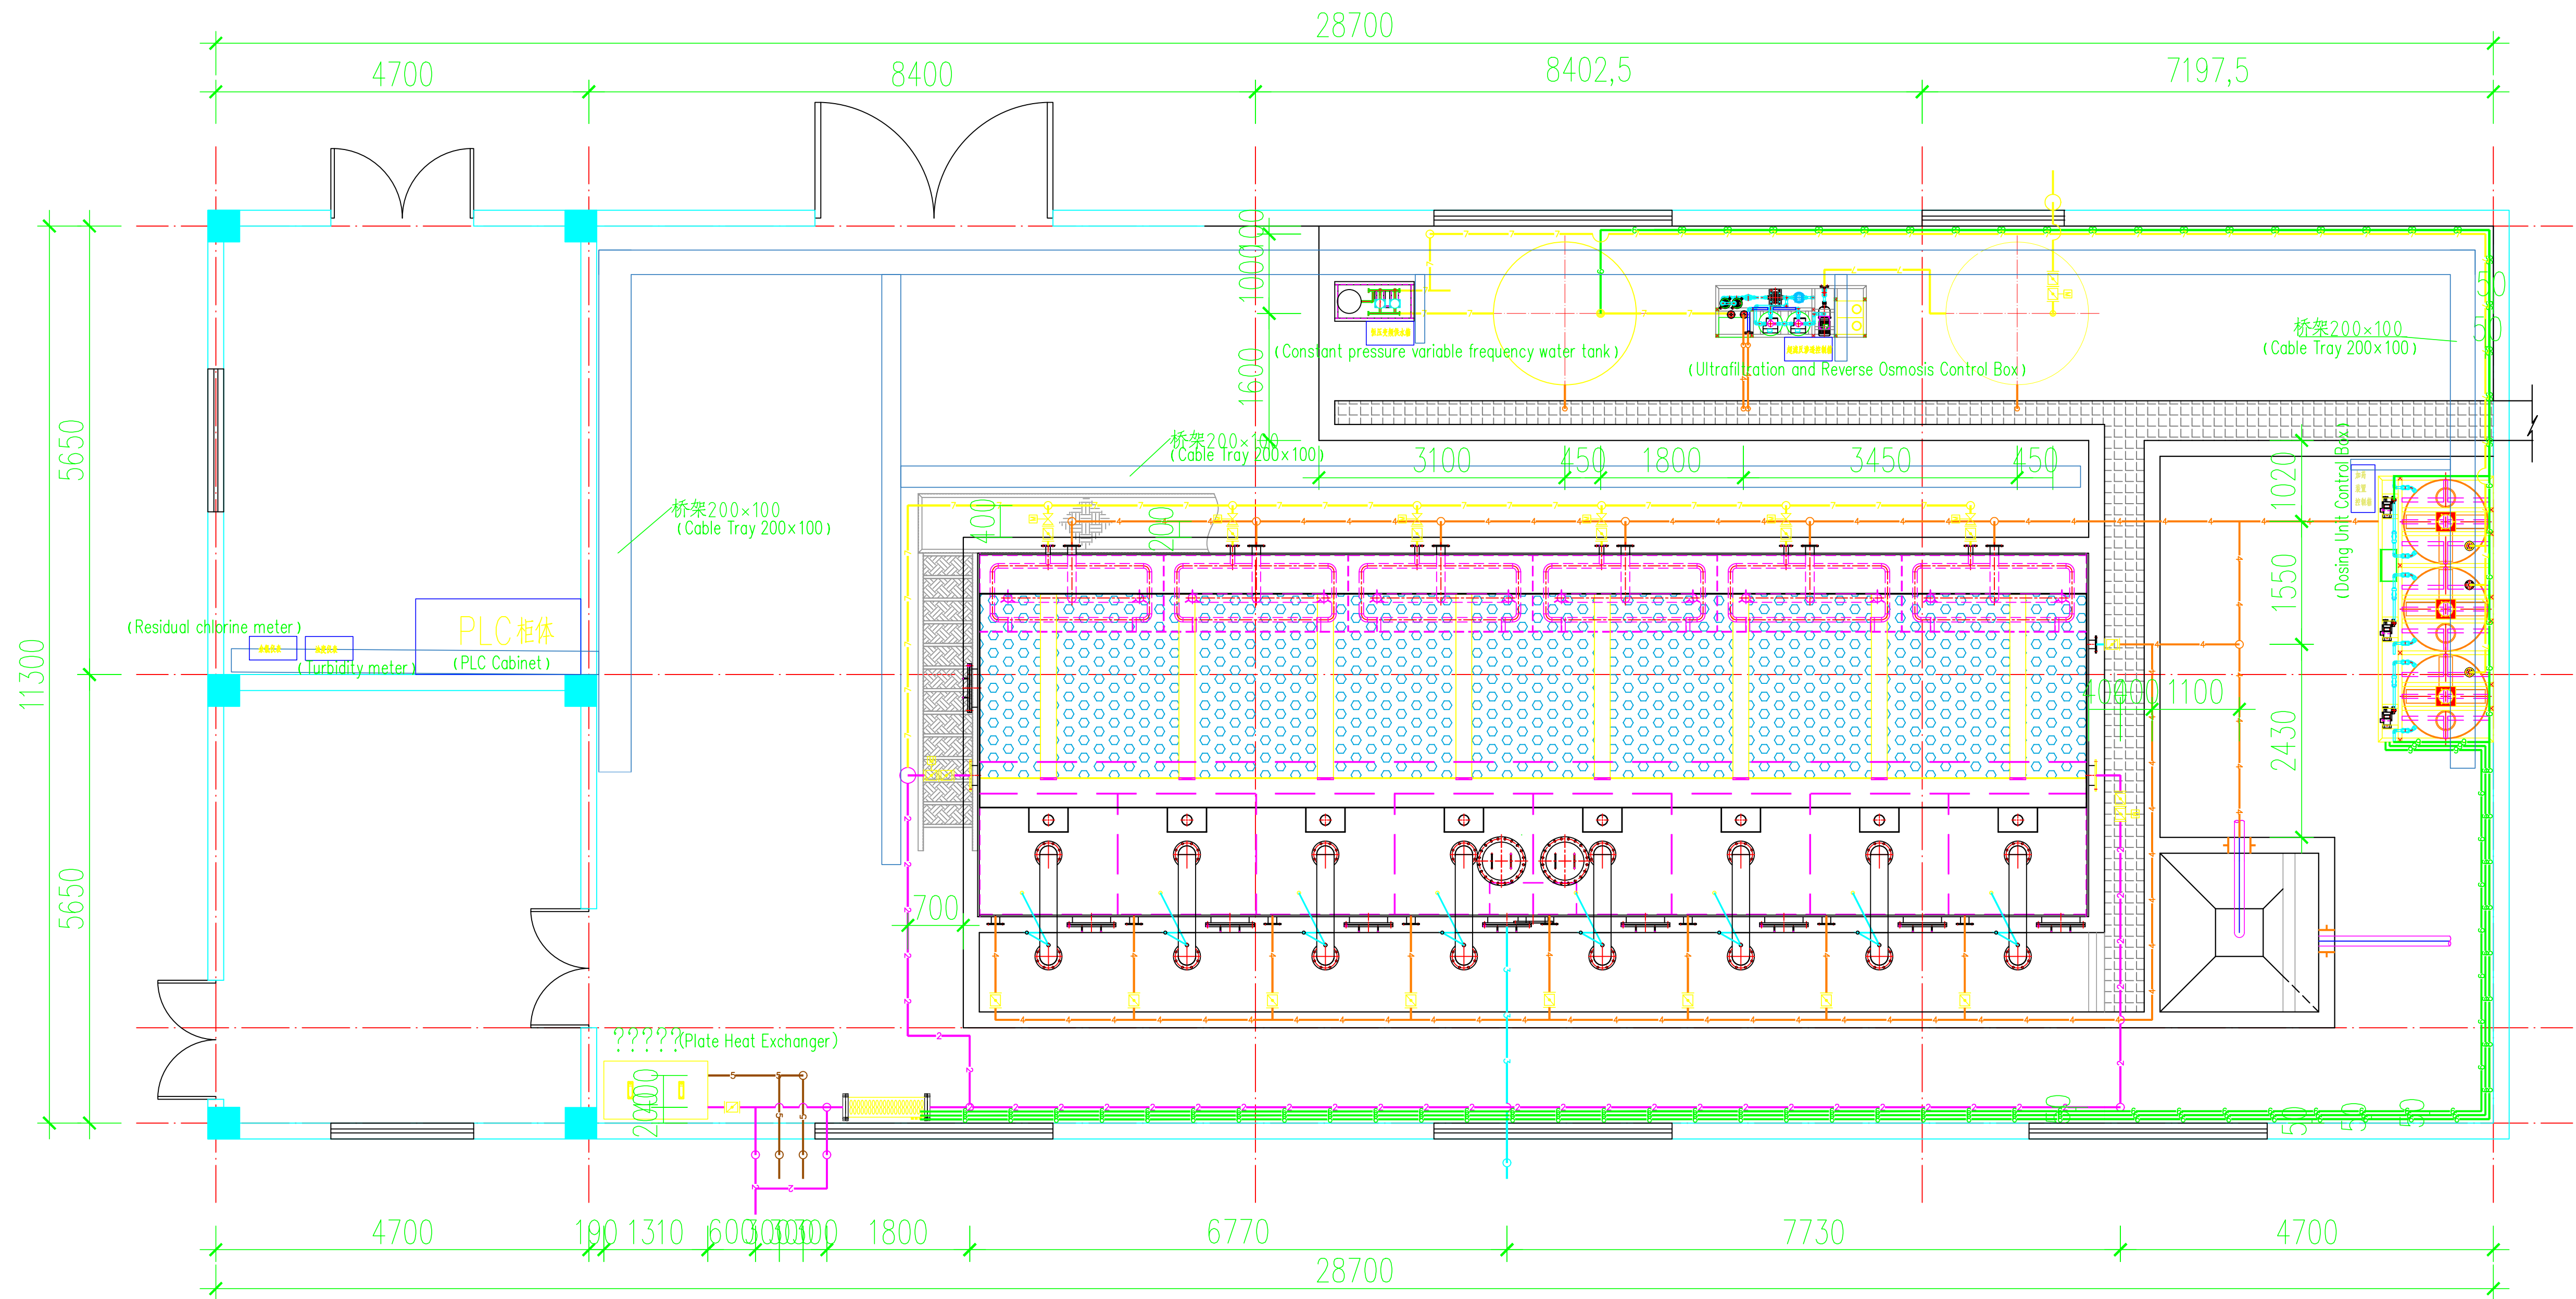

????????????

(Cable Tray & Cabinet Layout Plan of Water Purification Station)

四川盛玖源环境工程有限公司
Sichuan shengjiuyuan Environmental Engineering Co.,

工程名称
PROJECT
乌兹别克斯坦年产50万吨硫磺制酸项目
Uzbekistan 500,000 Tons/Year Sulfur-Based Sulfuric Acid Plant Project

子项名称
Sub-item Name
净水站设备项目
Project Water Purification Station Equipment

审 定
APPROVED
审 核
EXAMINED
校 核
CHECKED
设 计
DESIGNED

工程编号
PROJECT NO.
设计阶段
DESIGNSTAGE
比 例
Ratio
出图日期
DATE

SJY202602
施工图
CONSTRUCTION DRAWING
1:100
2026.02

净水站桥架柜体定位平面布置
Cable Tray & Cabinet Layout Plan of Water Purification Station

图纸编号
DRAWING NO.
SJY-GY-14

专 业
Professional
工 艺
Process