



会签	姓名	签名
工艺		
设备		
起运		
自控		
给排水		
电		
暖通		
建筑		
结构		
总图		
设计		
经理		

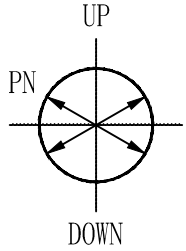


序号	管件输出	材质	公称直径	数量	单位
1	不锈钢无缝管 Φ219x6.0 GB/T 14976-2025	S30403	200	2.14	米
2	90°弯头 90EL II DN200 T=6.0 GB/T 12459-2025	S30403(SF304L)	200	2	个
3	45°弯头 90EL II DN200 T=6.0 GB/T 12459-2025	S30403(SF304L)	200	1	个
4	等径三通 TS II DN200X200 T=6.0 GB/T 12459-2025	S30403(SF304L)	200X200	1	个
5	带颈平焊法兰 SO200(B)-16 RF HG/T 20592-2009	S30403	200	2	个
6	非金属垫片 PN16 DN200 RFHG/T 20606-2009	RPTFE	200	2	个
7	全螺纹螺柱 M20X105 HG/T 20613-2009	35CrMo		24	个
8	II型六角螺母 M20 GB/T 6175-2016	30CrMo		48	个

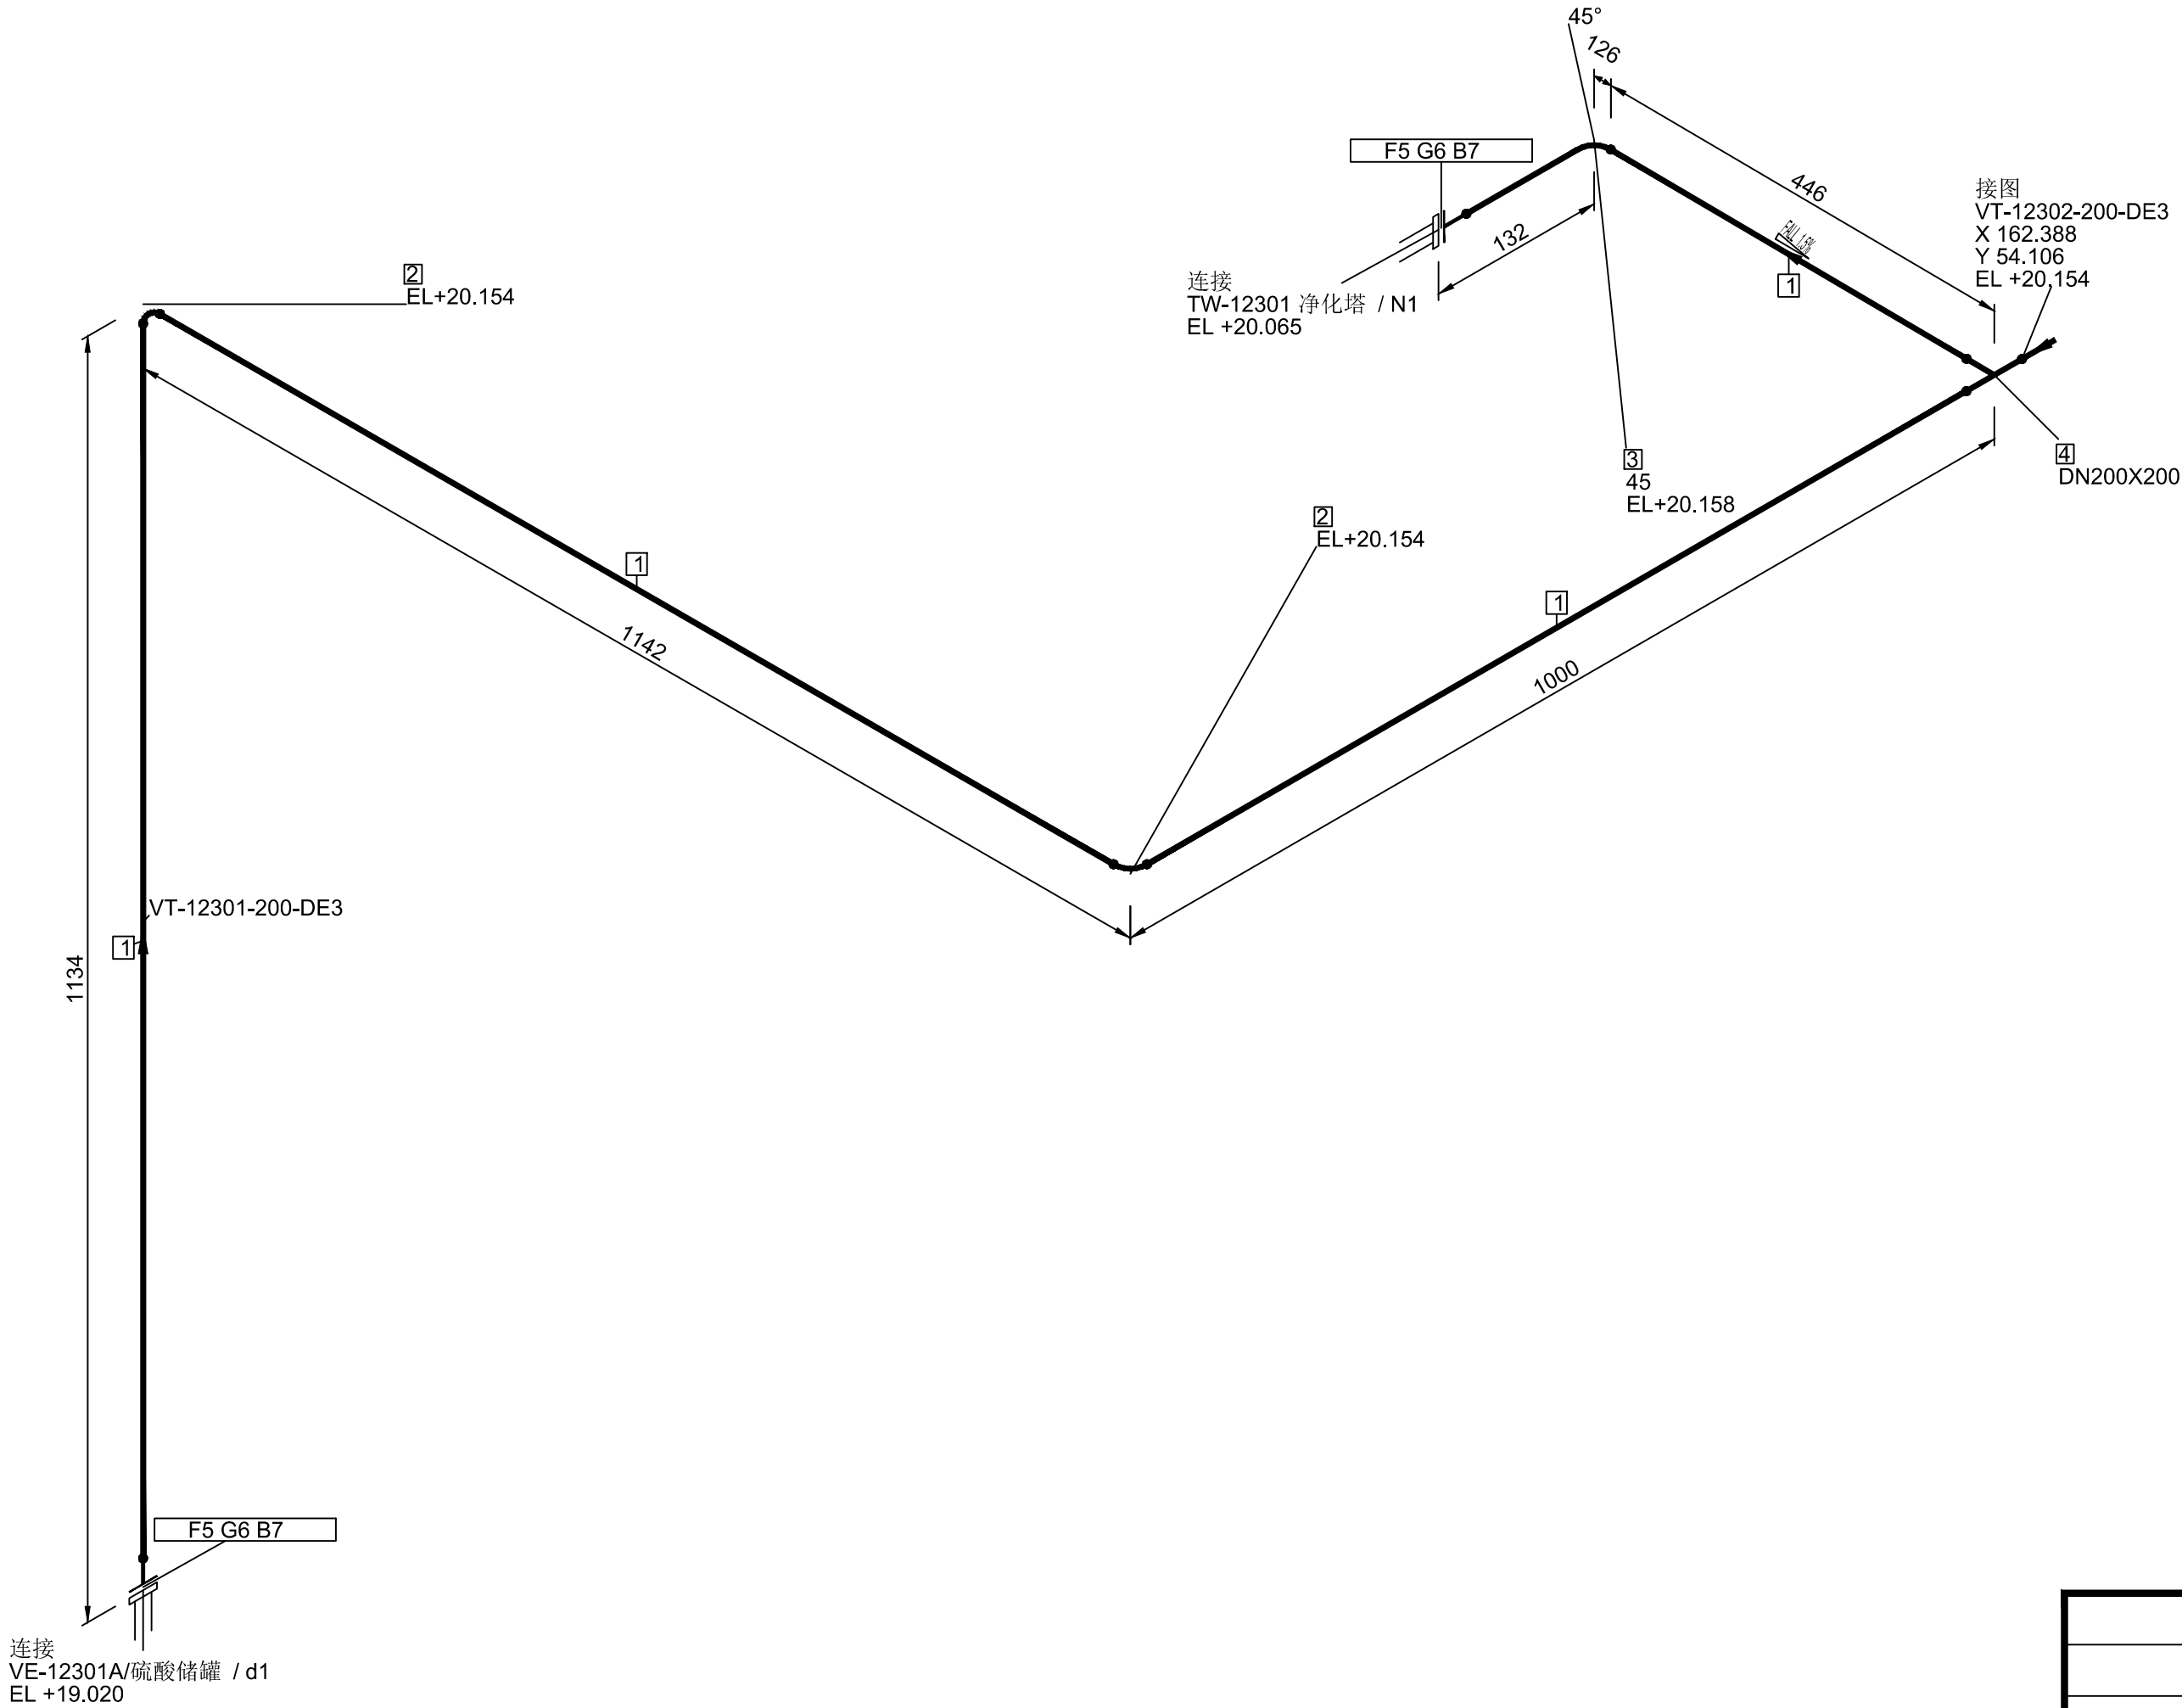


版次		说明		日期	
Версия		Примечания		Дата	
云南化工设计院有限公司		中信建设有限责任公司			
YUNNAN DESIGN INSTITUTE OF CHEMICAL ENGINEERING CO., LTD.		CITIC Construction Co., Ltd.			
工程名称		乌兹别克斯坦年产50万吨硫磺制酸项目			工程代号
НАЗВАНИЕ ПРОЕКТА		Uzbekistan UTMK Chemical LLC Проект завода по производству серной кислоты			Код объекта
3147					
姓名		签名		日期	
Фамилия и имя		Подпись		Дата	
审定		审核		管段轴测图	
Утверждение		Расм.		Аксонометрическая схема	
校核		检查		трубопровода	
Проверка		Деталь		VT-12301-200-DE3	
设计		日期		设计项目	
Проектирование		Дата		Проектируемый объект	
2026. 4. 1		2026. 4. 1		设计阶段	
版本		比例		Стадия проектирования	
1		1:1		图号	
1		1		№ чертежа	
1		1		3147-5G123-19-002	
1		1		产品硫磺制酸	
1		1		Зона резервуара для серной	
1		1		кислоты с продуктом	
1		1		Рабочий чертёж	
1		1		7 806519 924201	

VT-12301-200-DE3	VE-12301A/B硫酸储罐	TW-12201/净化塔	常压	40	常压	50	洁净水	<0.1	200	DE3			
管段号	起点	终点	压力 (MPa)	温度 (°C)	压力 (MPa)	温度 (°C)	试验介质	试验压力	公称直径	管道等级	隔热代号	隔热厚度	备注
Номер участка трубопровода	Начальная точка	Конечная точка	Давление (МПа)	Температура (°C)	Давление (МПа)	Температура (°C)	Испытательная среда	Испытательное давление	Номинальный диаметр	Класс труб	Обозначение теплоизоляции	Толщина теплоизоляции	Примечания
			操作条件	设计条件	操作条件	设计条件	试验要求	试验要求					
			Условия эксплуатации	Расчетные условия	Условия эксплуатации	Расчетные условия	Требования к испытаниям	Требования к испытаниям					

会签	姓名	签名
工艺		
设备		
起运		
自控		
给排水		
电		
暖通		
建筑		
结构		
总图		
设计		
经理		

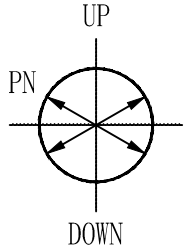

序号	管件输出	材质	规格	数量	单位
1	不锈钢无缝管 Φ219x6.0 GB/T 14976-2025	S30403	200	34.38	米
2	90°弯头 90EL II DN200 T=6.0 GB/T 12459-2025	S30403(SF304L)	200	2	个
3	带颈平焊法兰 SO200(B)-16 RF HG/T 20592-2009	S30403	200	1	个
4	非金属垫片 PN16 DN200 RFHG/T 20606-2009	RPTFE	200	1	个
5	全螺纹螺柱 M20X105 HG/T 20613-2009	35CrMo		12	个
6	II型六角螺母 M20 GB/T 6175-2016	30CrMo		24	个
7	焊接式管托 S123021,J13-200-100-300-S HG/T 21629-2021		200	2	个
8	T形架 S123021,D12-1-E-3600-419 HG/T 21629-2021			2	个

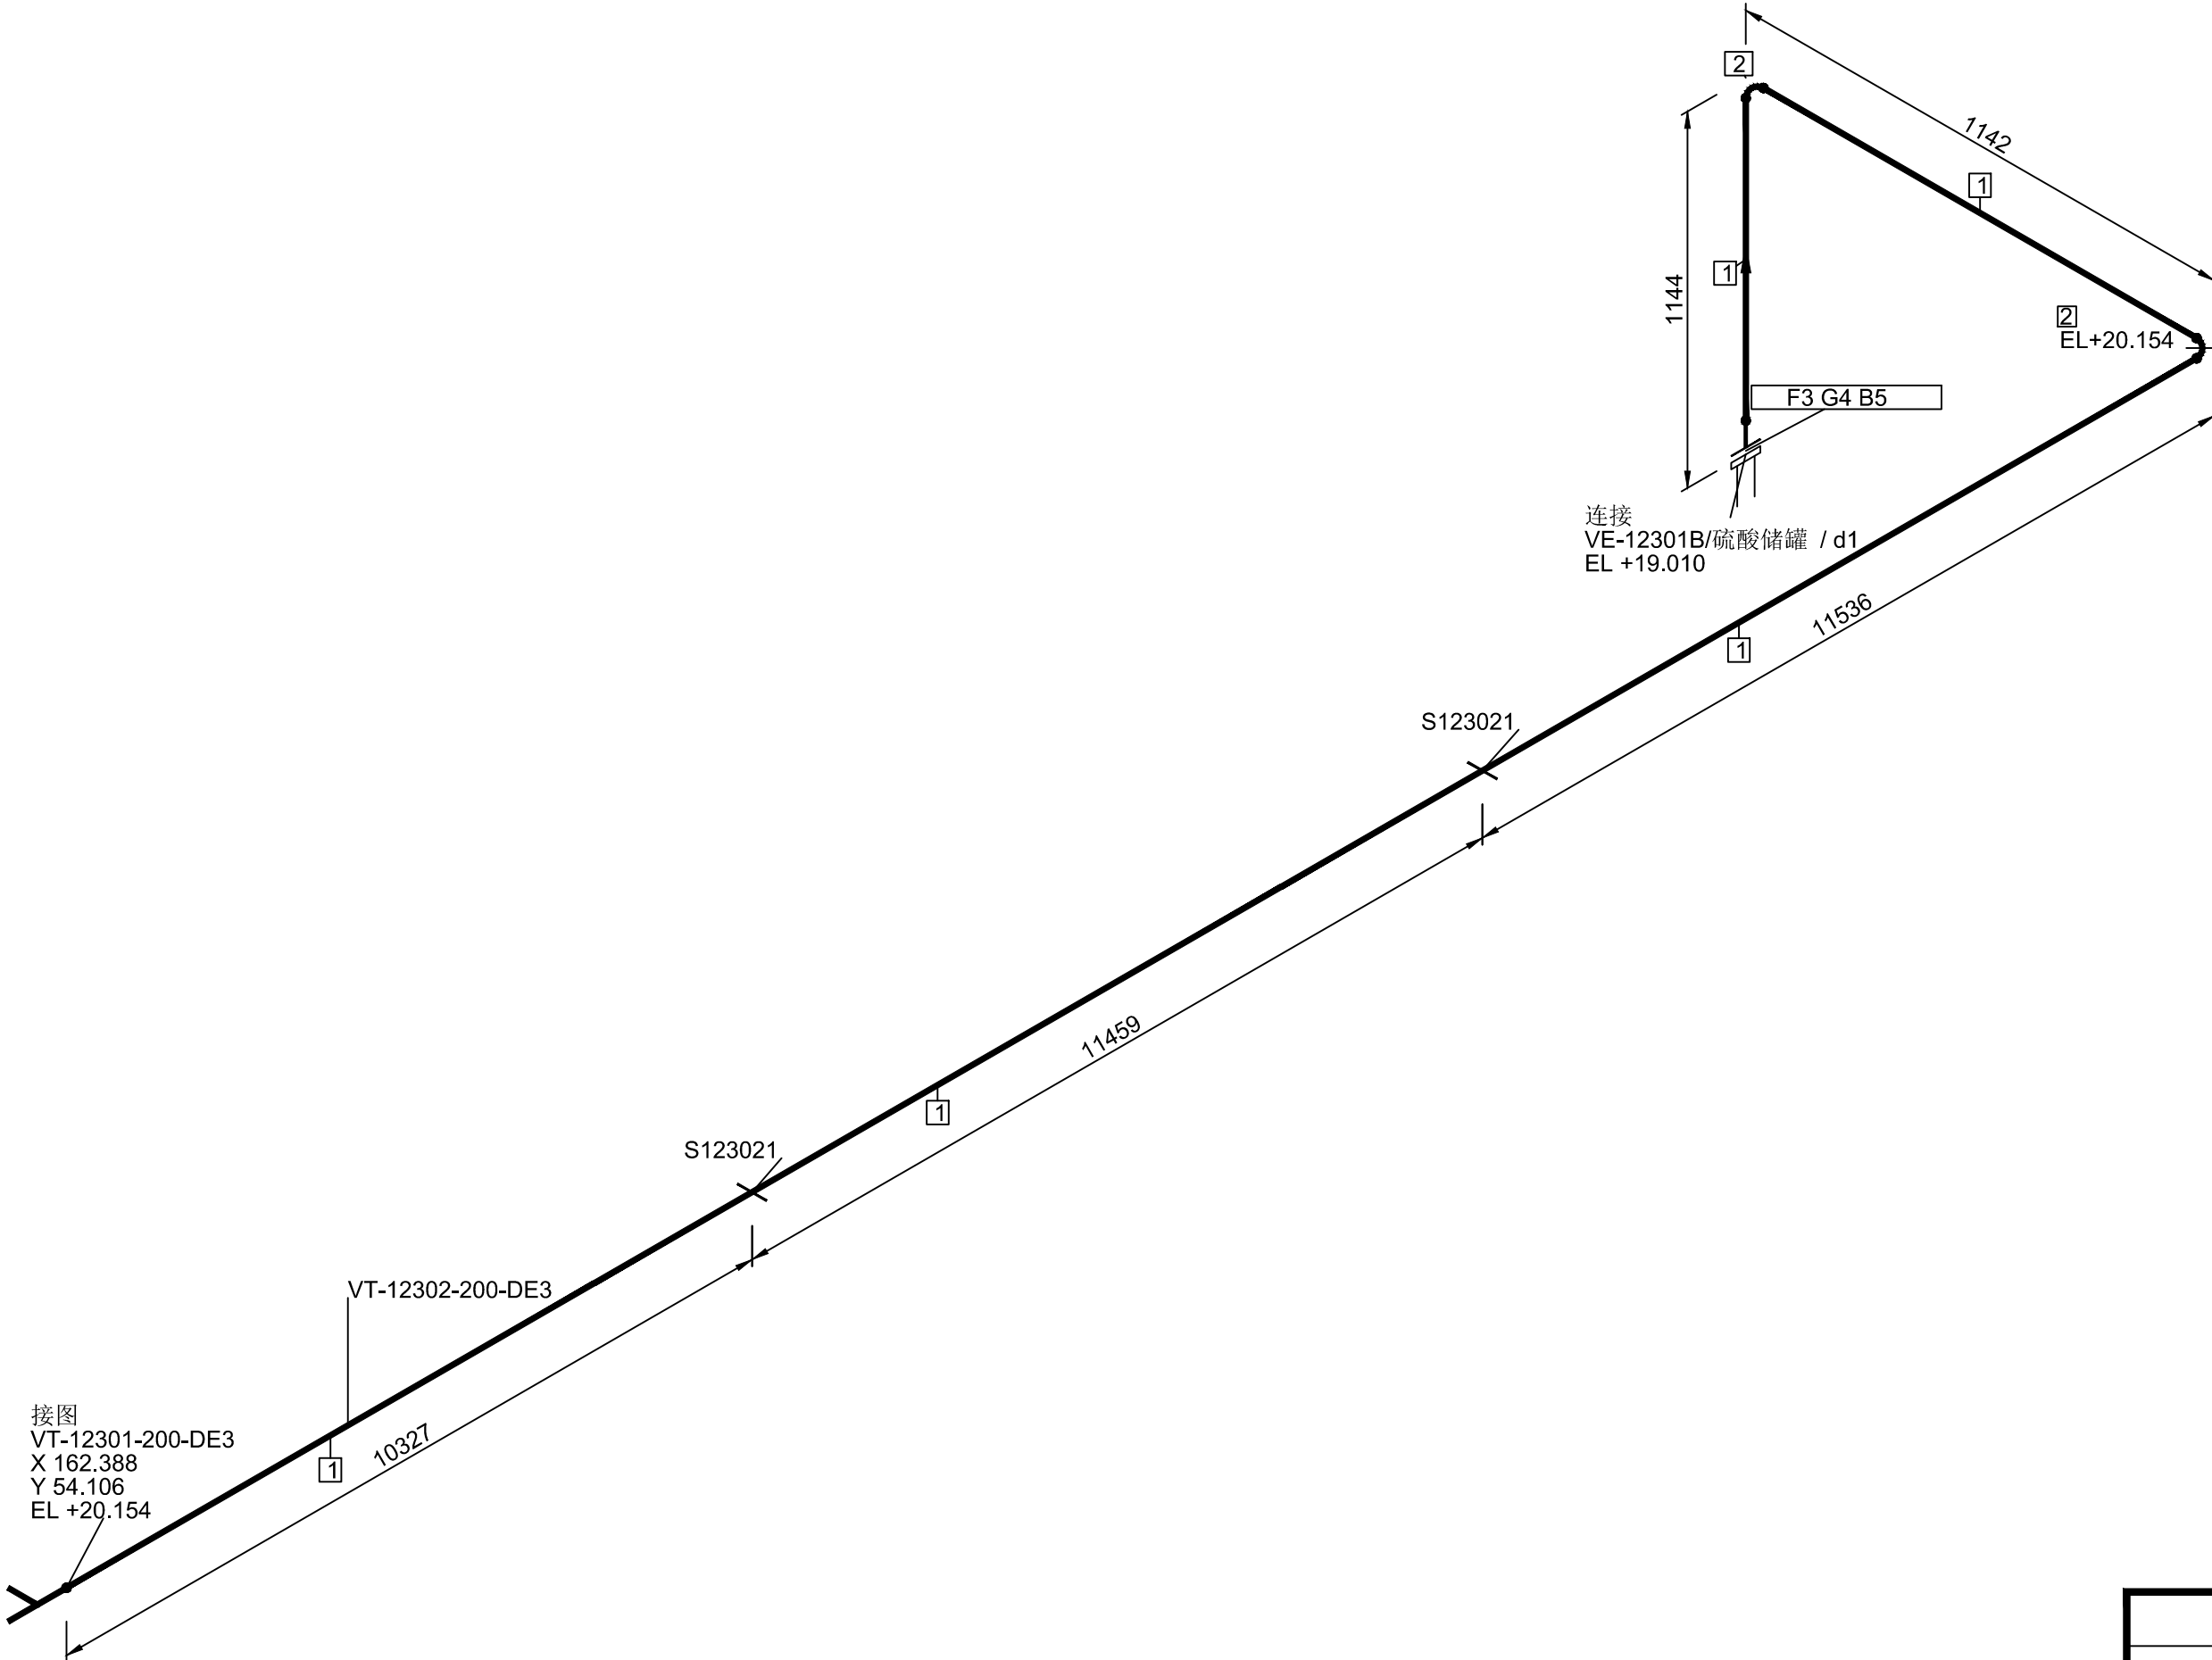

版次		说明		日期	
Версия		Примечания		Дата	
云南化工设计院有限公司		中信建设有限责任公司			
YUNNAN DESIGN INSTITUTE OF CHEMICAL ENGINEERING CO.,LTD.		CITIC Construction Co.,Ltd.			
工程名称		乌兹别克斯坦年产50万吨硫磺制酸项目			工程代号
НАЗВАНИЕ ПРОЕКТА		Uzbekistan UTMK Chemical LLC Проект завода по производству серной кислоты			Код объекта
					3147
姓名		签名	日期	管段轴侧图	
Фамилия и имя		Подпись	Дата	Аксонометрическая схема	
审定				设计项目	
Утверждение				Проектируемый объект	
审核				设计阶段	
Расом.				Стадия проектирования	
校核				图号	
Проверка				№ чертежа	
设计				第1张	
Проектирование				Лист	
				共1张	
				Листы	
				7 806519 939137	

VT-12301-200-DE3	VE-12301A/B硫酸储罐	TW-12201/净化塔	常压	40	常压	50	洁净水	<0.1	200	DE3			
管段号	起点	终点	压力(MPa)	温度(℃)	压力(MPa)	温度(℃)	介质名称	试验压力	公称直径	管道等级	隔热代号	隔热厚度	备注
Номер участка трубопровода	Начальная точка	Конечная точка	Давление (МПа)	Температура (°C)	Давление (МПа)	Температура (°C)	Испытательная среда	Испытательное давление	Номинальный диаметр	Класс труб	Обозначение теплоизоляции	Толщина теплоизоляции	Примечания
			操作条件	设计条件	操作条件	设计条件	试验要求	试验要求					
			Условия эксплуатации	Расчетные условия	Условия эксплуатации	Расчетные условия	Требования к испытаниям	Требования к испытаниям					